




ПРОЕКТ-ЭЛЕКТРИКА

2-комнатной квартиры

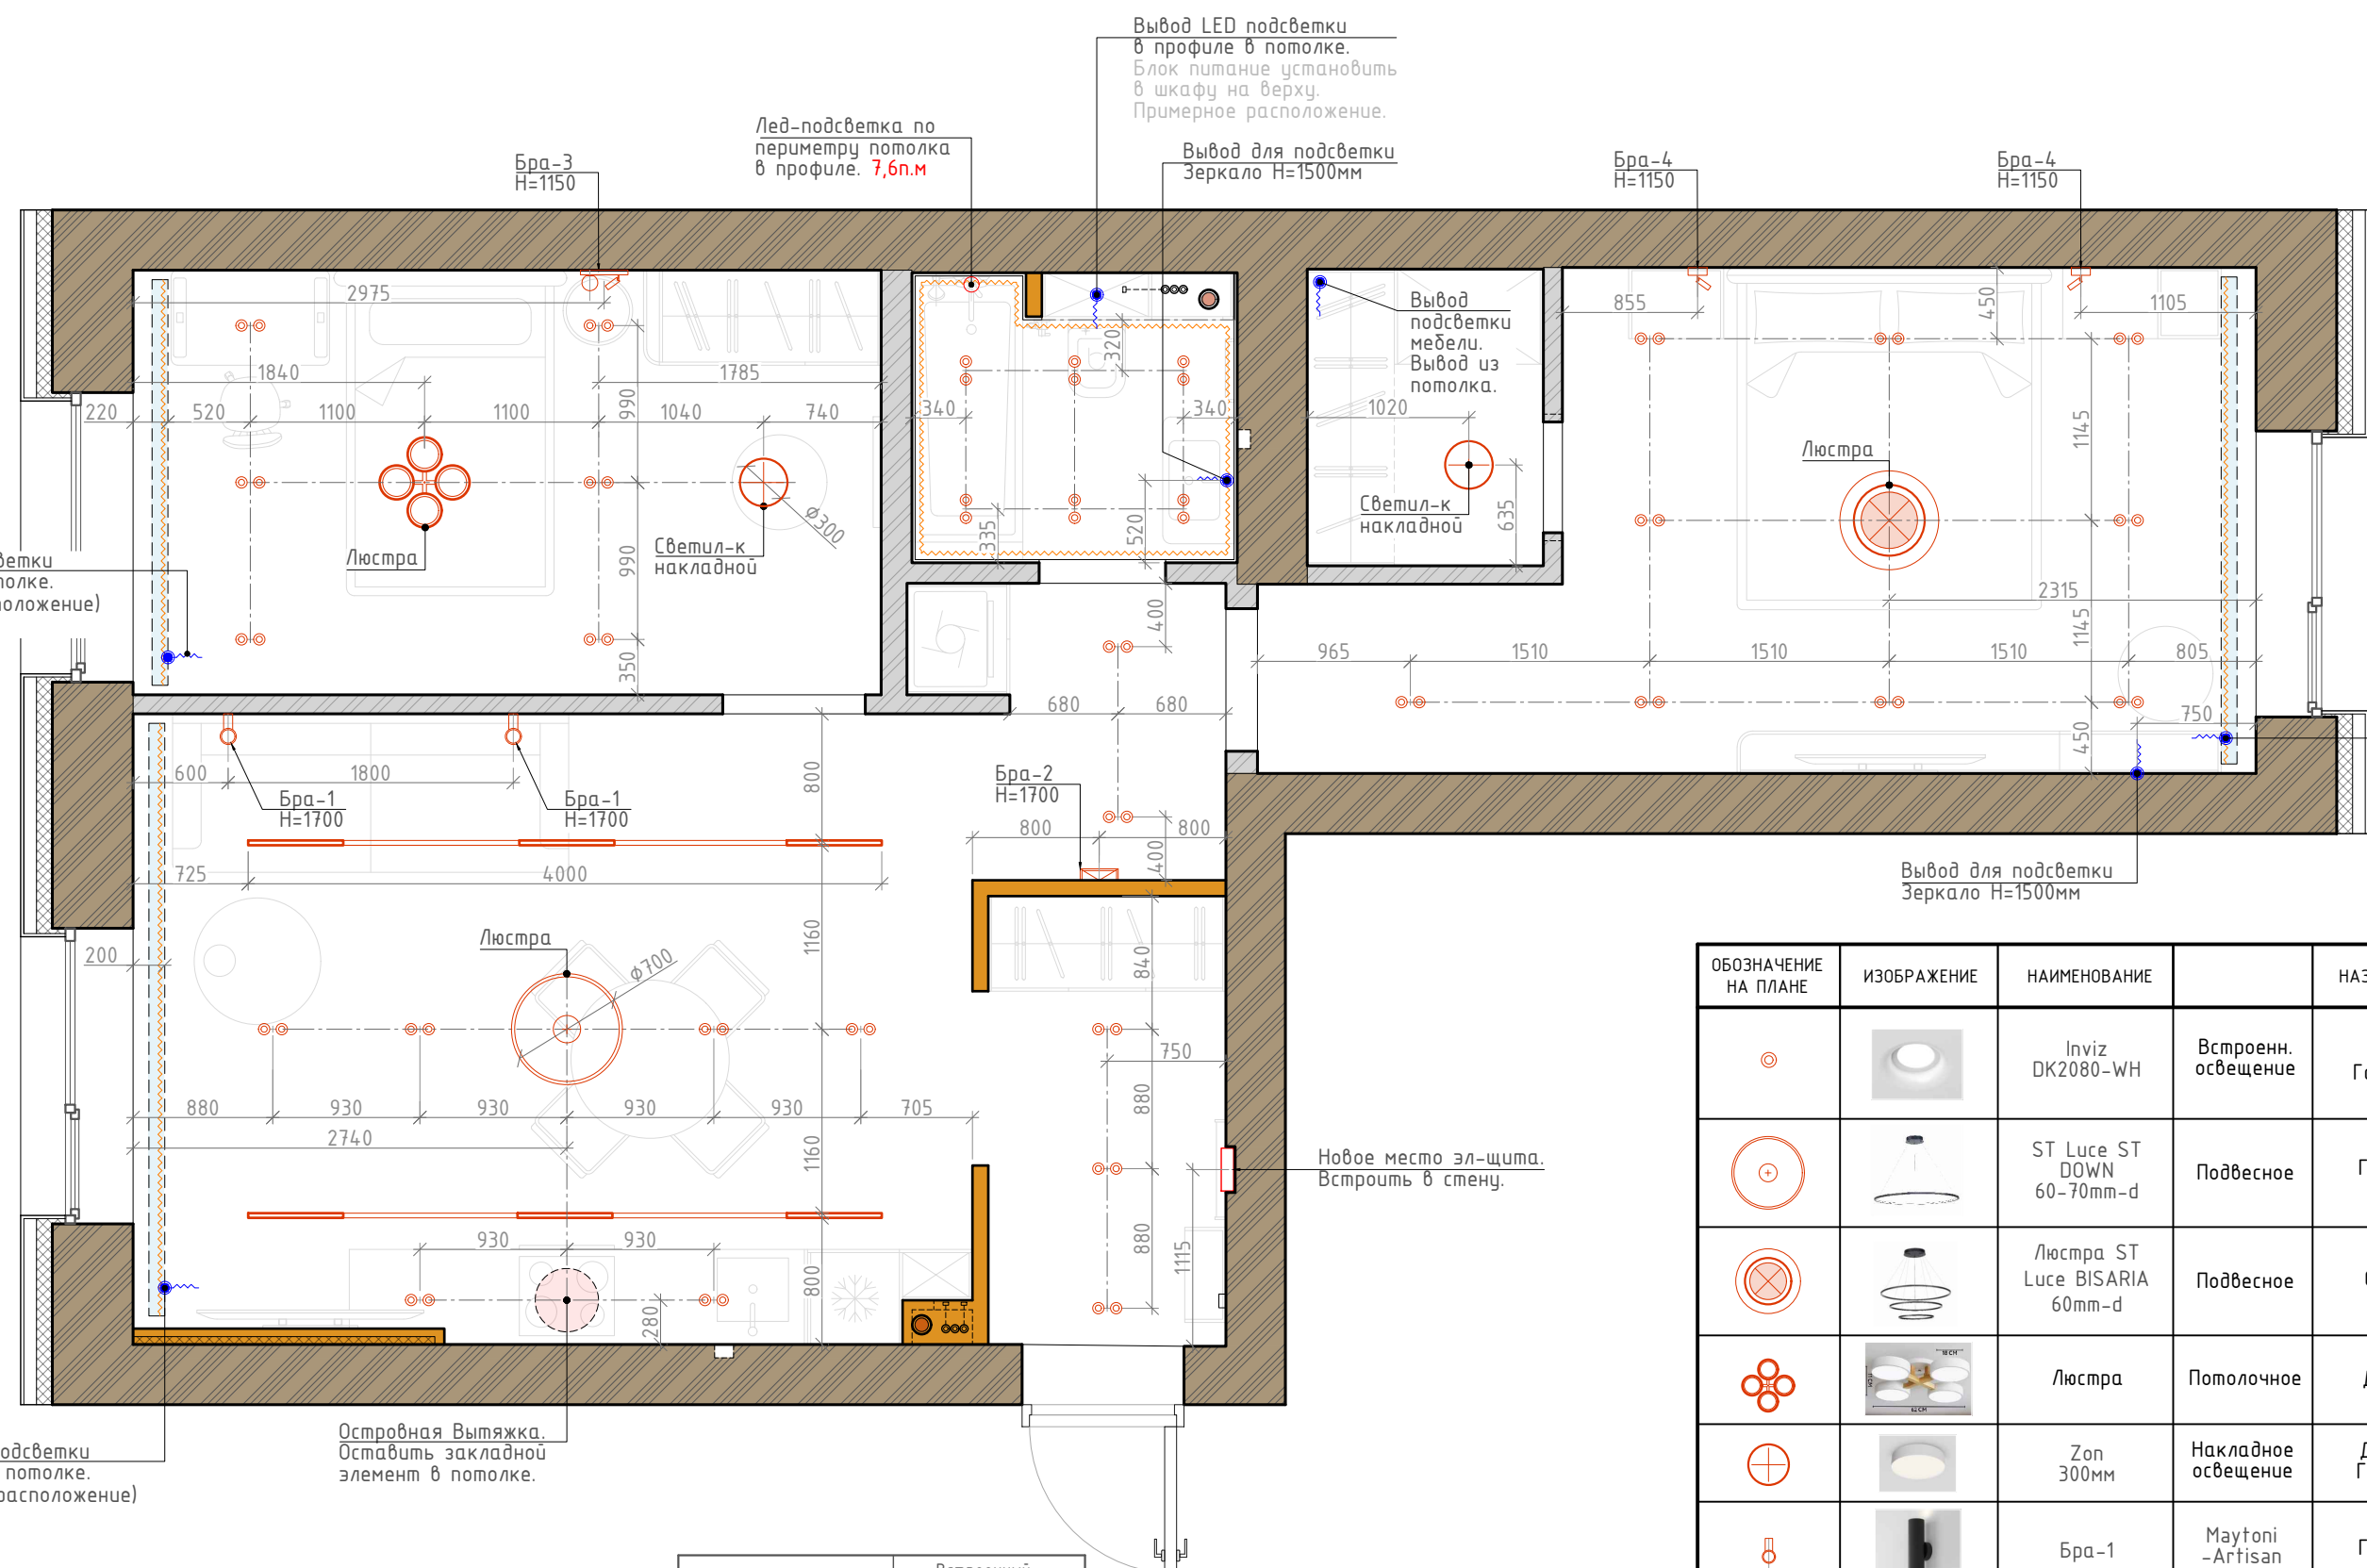

Вывод LED подсветки в карнизе в потолке. (Примерное расположение) 2.56 п/м

Лед-подсветка по периметру потолка в профиле. 7,6п.м

Вывод LED подсветки в профиле в потолке. Блок питания установить в шкафу наверху. Примерное расположение.

Вывод для подсветки Зеркало H=1500мм

Бра-4 H=1150

Бра-4 H=1150

Вывод подсветки мебели. Вывод из потолка.

Светил-к накладной

Люстра

Вывод LED в карнизе (Примерно 3.1 п/м)

Вывод для подсветки Зеркало H=1500мм

Бра-2 H=1700

Бра-1 H=1700

Бра-1 H=1700

Люстра

Новое место эл.-щита. Встроить в стену.

Вывод LED подсветки в карнизе в потолке. (Примерное расположение) 3.75 п/м

Островная Вытяжка. Оставить закладной элемент в потолке.

УСЛОВНЫЕ ОБОЗНАЧЕНИЯ:


- - Вывод электро-кабеля
- - Лед лента

ПРИМЕЧАНИЕ:
1. Все электро-кабели необходимо вывести с запасом на 50 см.

Подсветка в профиле (парящий потолок)	Встроенный карниз-профиль с подсветкой


ОБОЗНАЧЕНИЕ НА ПЛАНЕ	ИЗОБРАЖЕНИЕ	НАИМЕНОВАНИЕ		НАЗНАЧЕНИЕ	КОЛ-ВО
		Inviz DK2080-WH	Встроенн. освещение	Кроме Гардероба	62шт
		ST Luce ST DOWN 60-70mm-d	Подвесное	Гостиная	1 шт
		Люстра ST Luce BISARIA 60mm-d	Подвесное	Спальня	1 шт
		Люстра	Потолочное	Детская	1 шт
		Zon 300mm	Накладное освещение	Детская; Гардероб;	2 шт
		Бра-1	Maytoni -Artisan	Гостиная	2 шт
		Бра-2	Hiper Ricco	Гостиная	1 шт
		Бра-3	L-300mm	Детская	1 шт
		Бра-4	Mirax	Спальня;	2 шт

План освещение с размерами;	Лист	Листов
	1	--

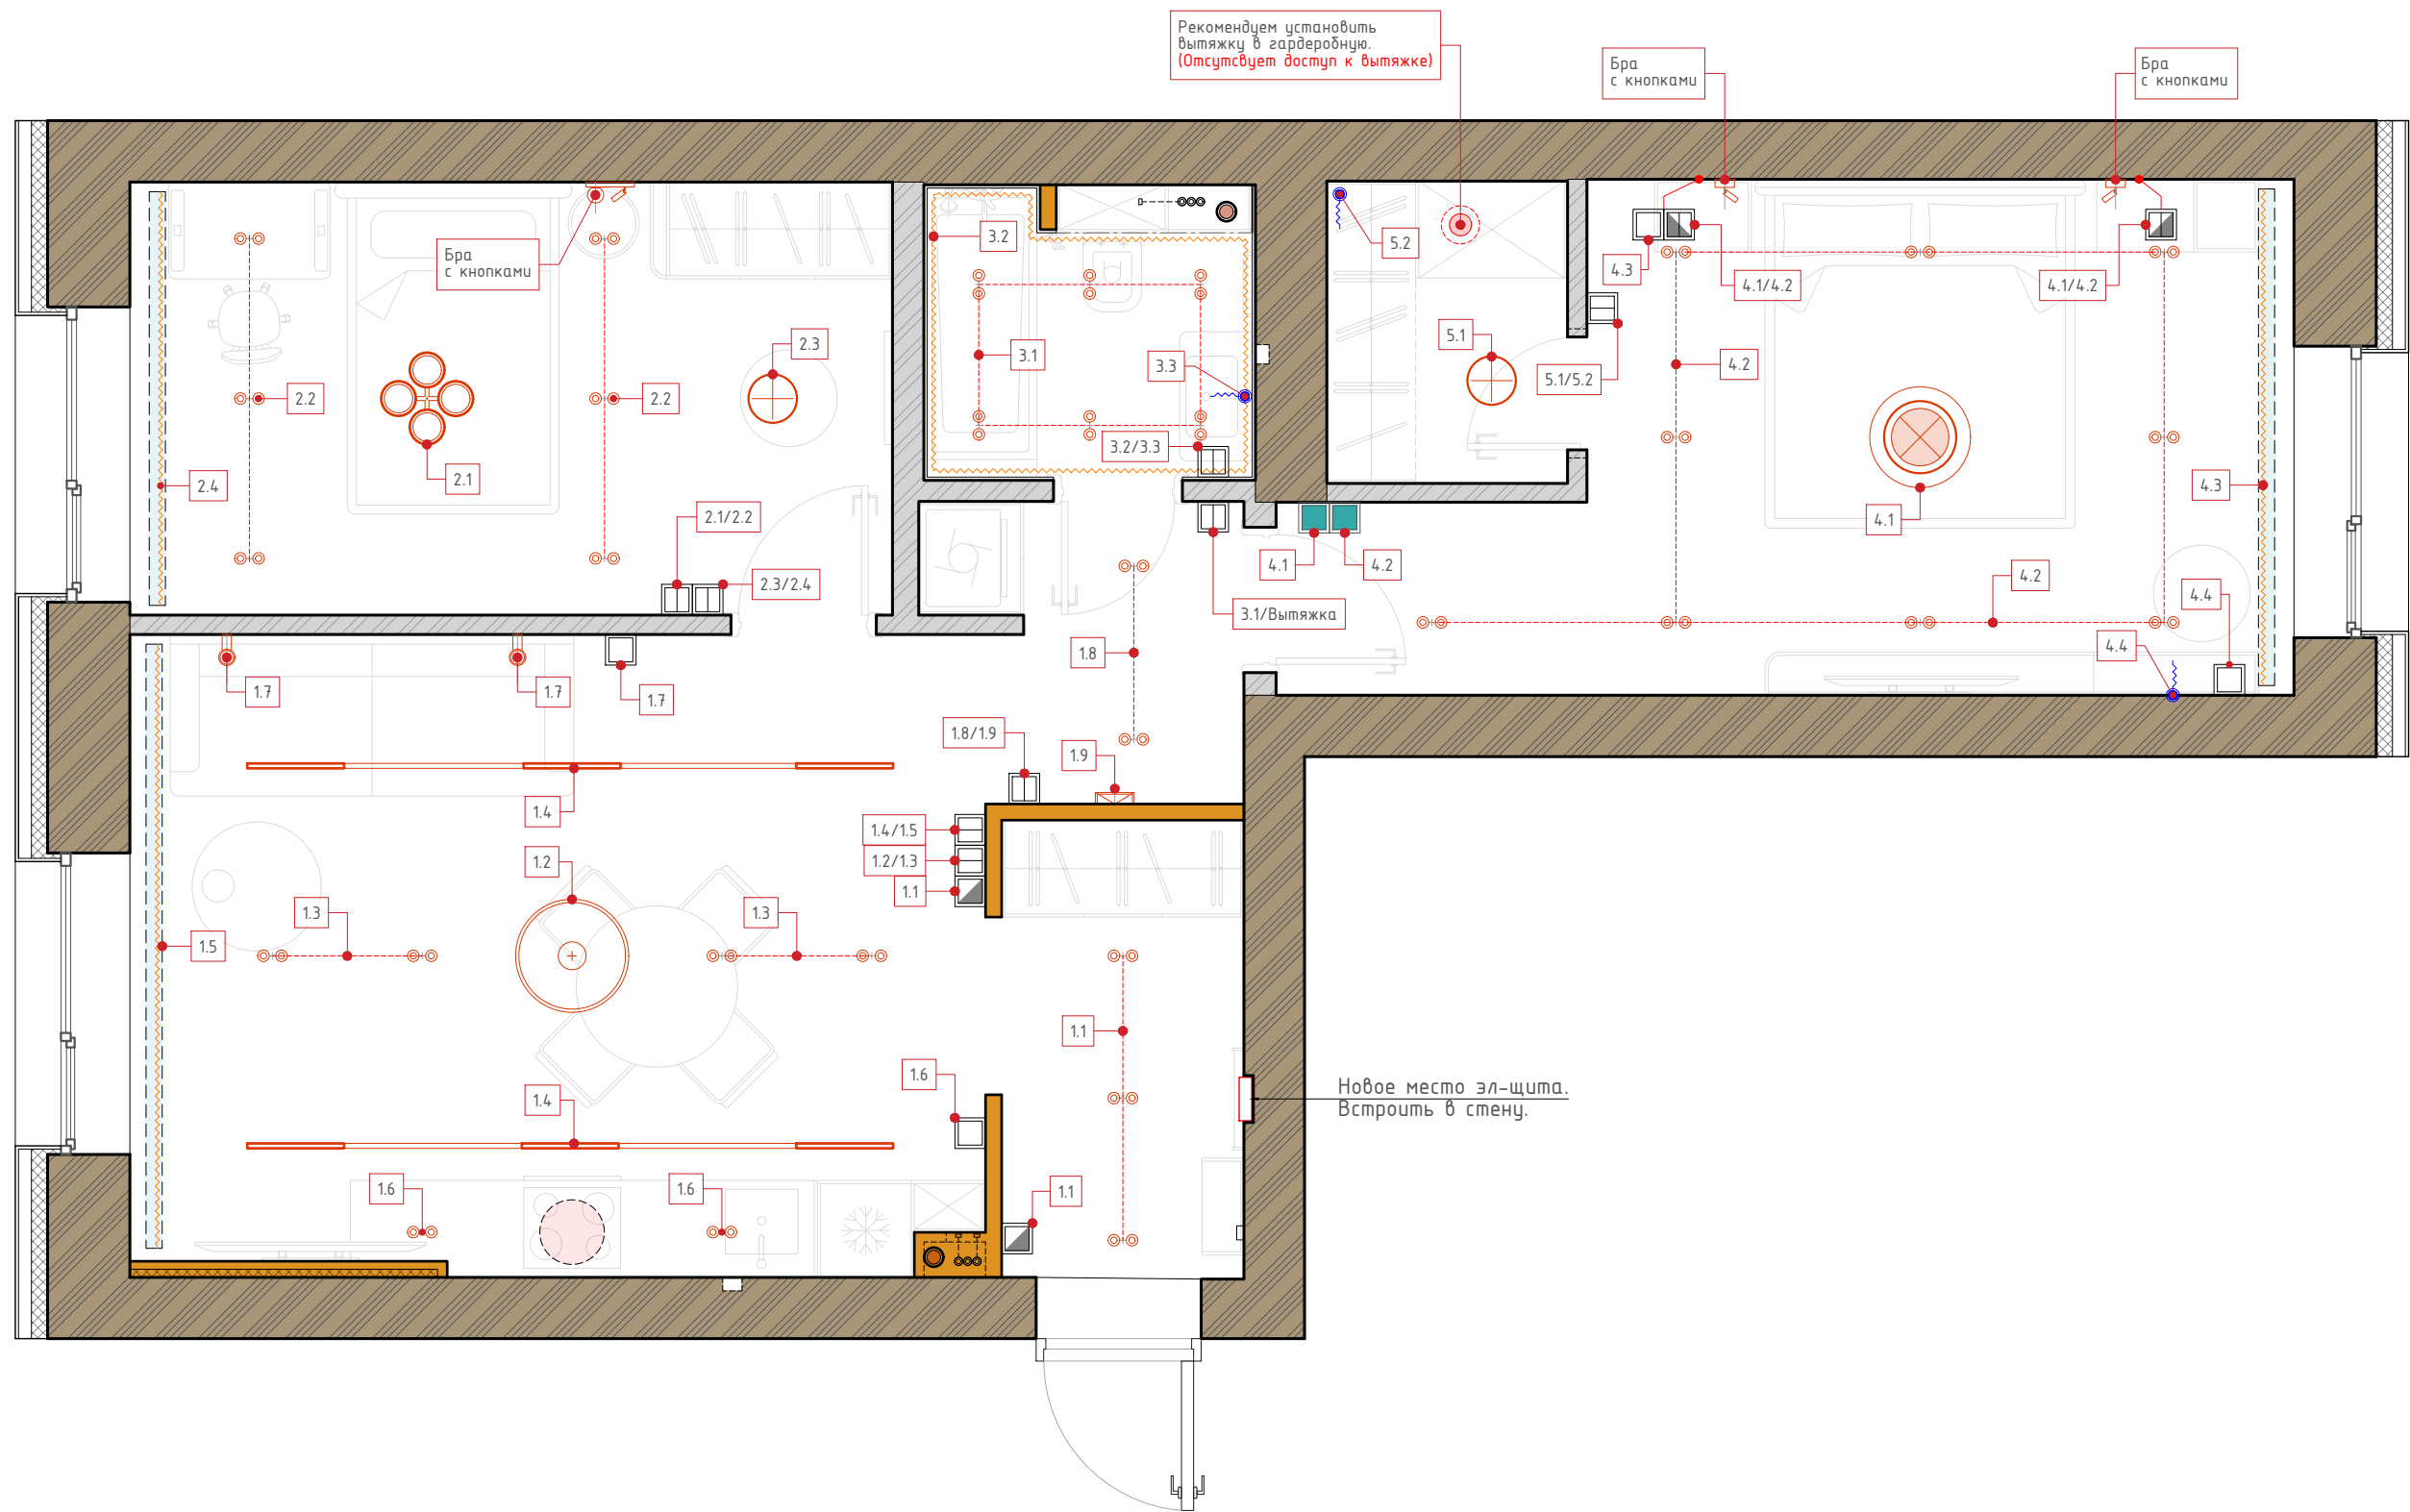

-  -Прходной двухклавишный выкл.
-  -Одноклавишный выкл.
-  -Двухклавишный выкл.
-  -Мастер выкл.
-  -Обозначение номера группы выкл-теля. (связь светильников с выключателями)

	Лист	Листов
	2	--
План Сценарий освещения;		

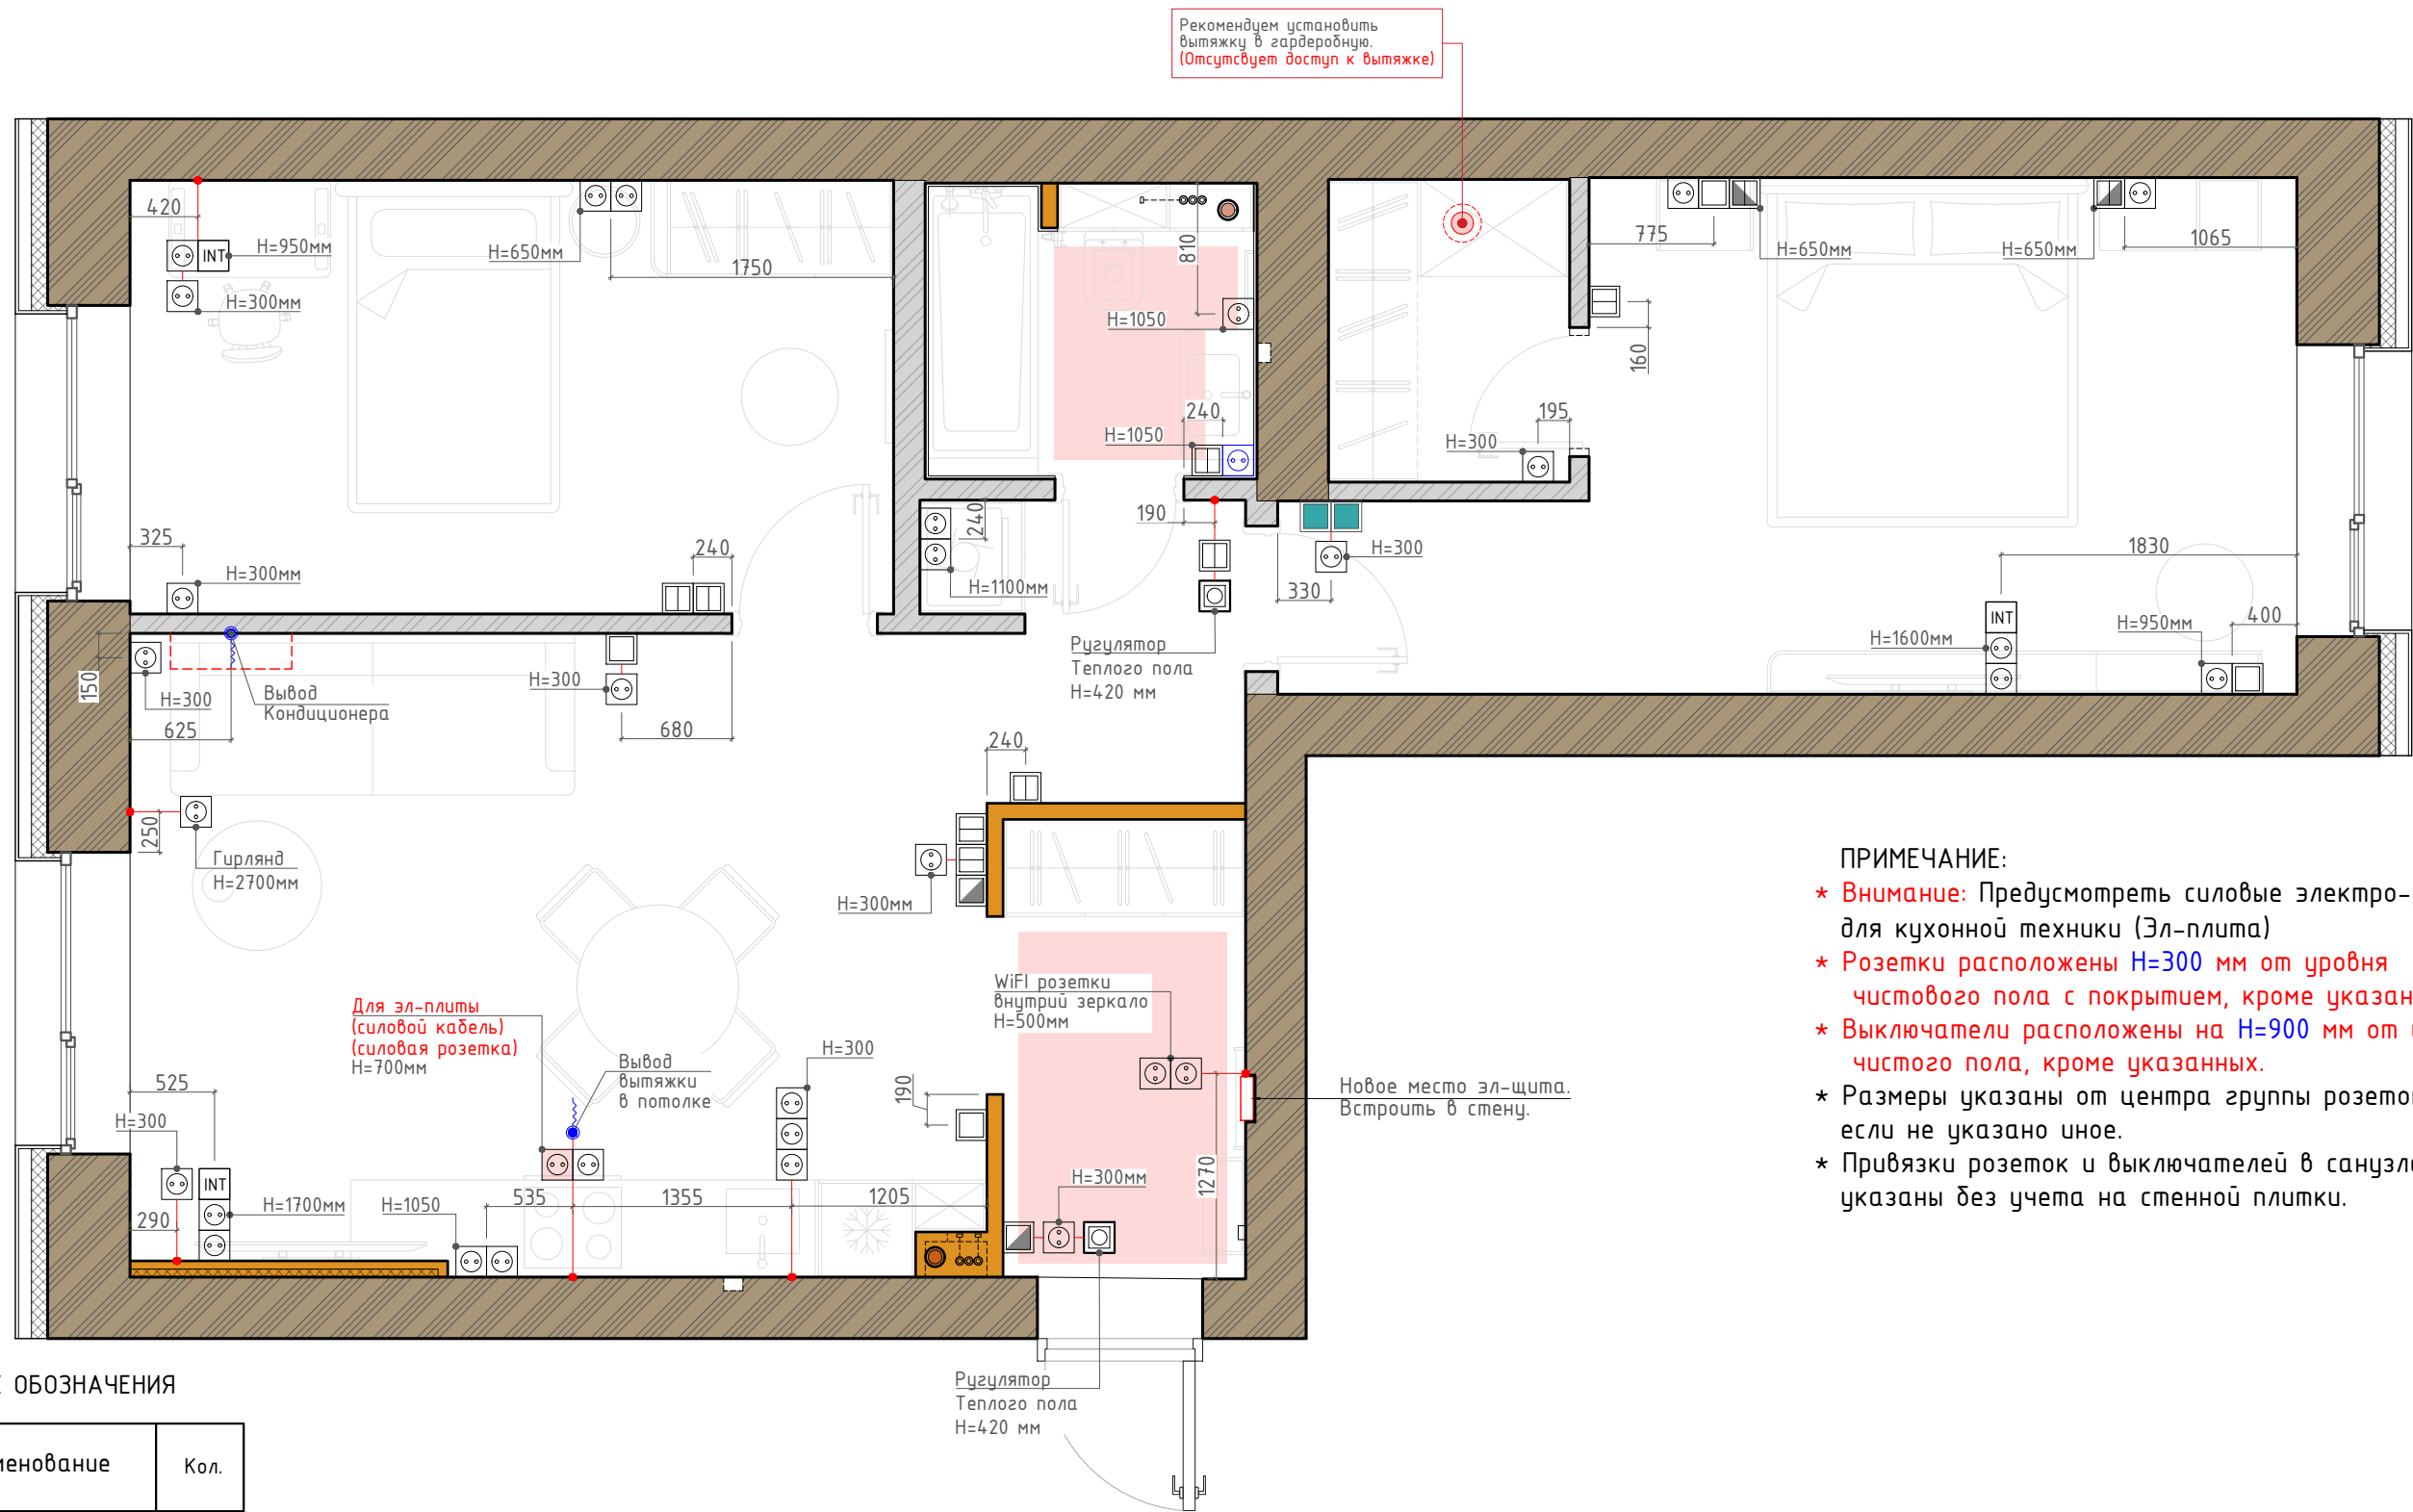

- ПРИМЕЧАНИЕ:
- * **Внимание:** Предусмотреть силовые электро-розетки для кухонной техники (Эл-плита)
 - * Розетки расположены H=300 мм от уровня чистового пола с покрытием, кроме указанных.
 - * Выключатели расположены на H=900 мм от уровня чистого пола, кроме указанных.
 - * Размеры указаны от центра группы розеток, если не указано иное.
 - * Привязки розеток и выключателей в санузлах указаны без учета на стеной плитки.


УСЛОВНЫЕ ОБОЗНАЧЕНИЯ

Обозн.	Наименование	Кол.
	Одноклавишный выключатель	0
	Двухклавишный выключатель	0
	Одноклавишный проходной	0
	Перекрестный выключатель	0
	Розетка 220 в	0
	Розетка 220 в Влагозащитная	0
	Интернет-розетка	0
	Силовая розетка	0


	1-х постовая рамка	
	2-х постовая рамка	
	3-х постовая рамка	

	Лист	Листов
	3	--
План Розеток и Выключателей;		

ТВ СТЕНА-ГОСТИНАЯ

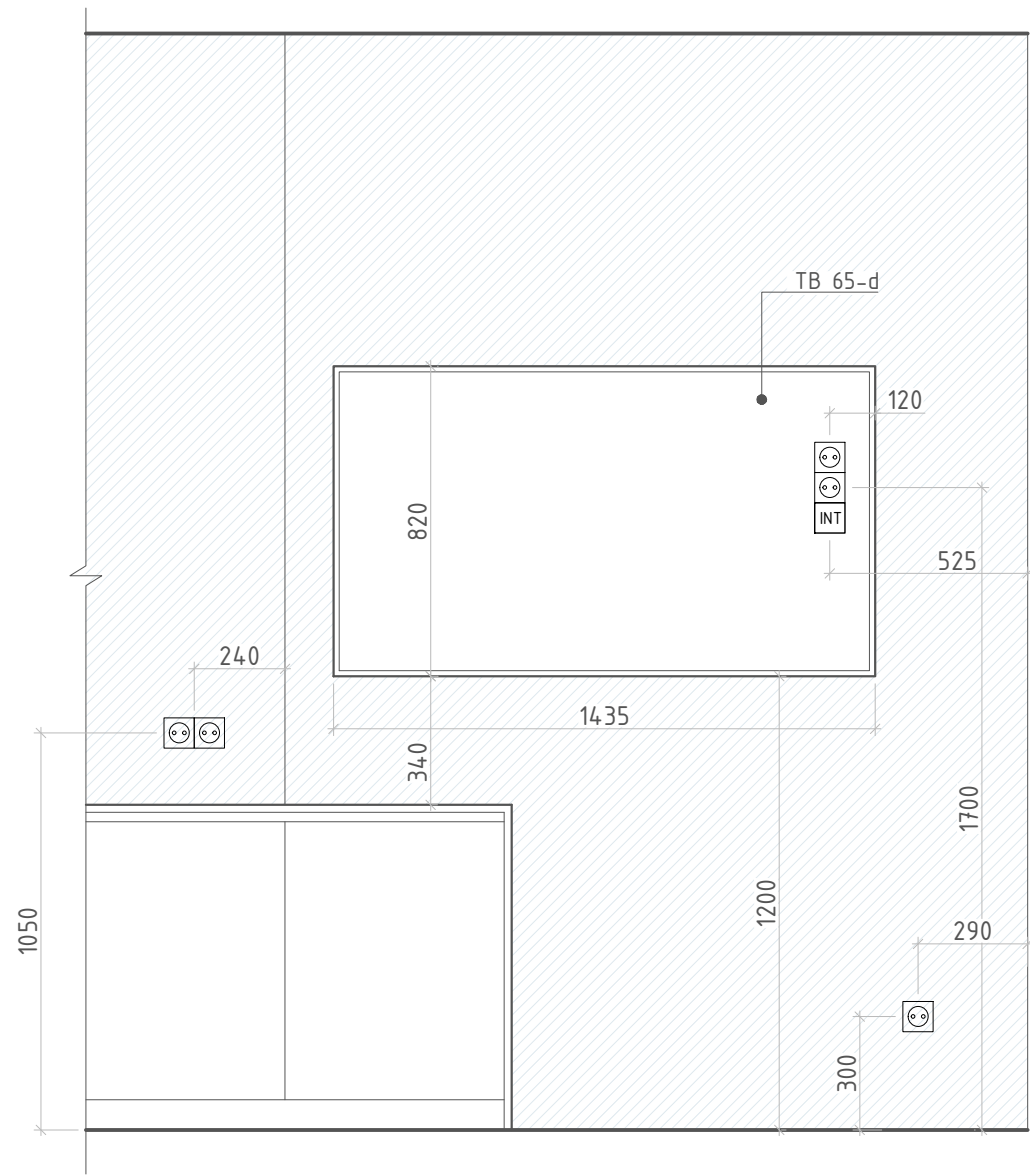

ТВ СТЕНА-СПАЛЬНЯ

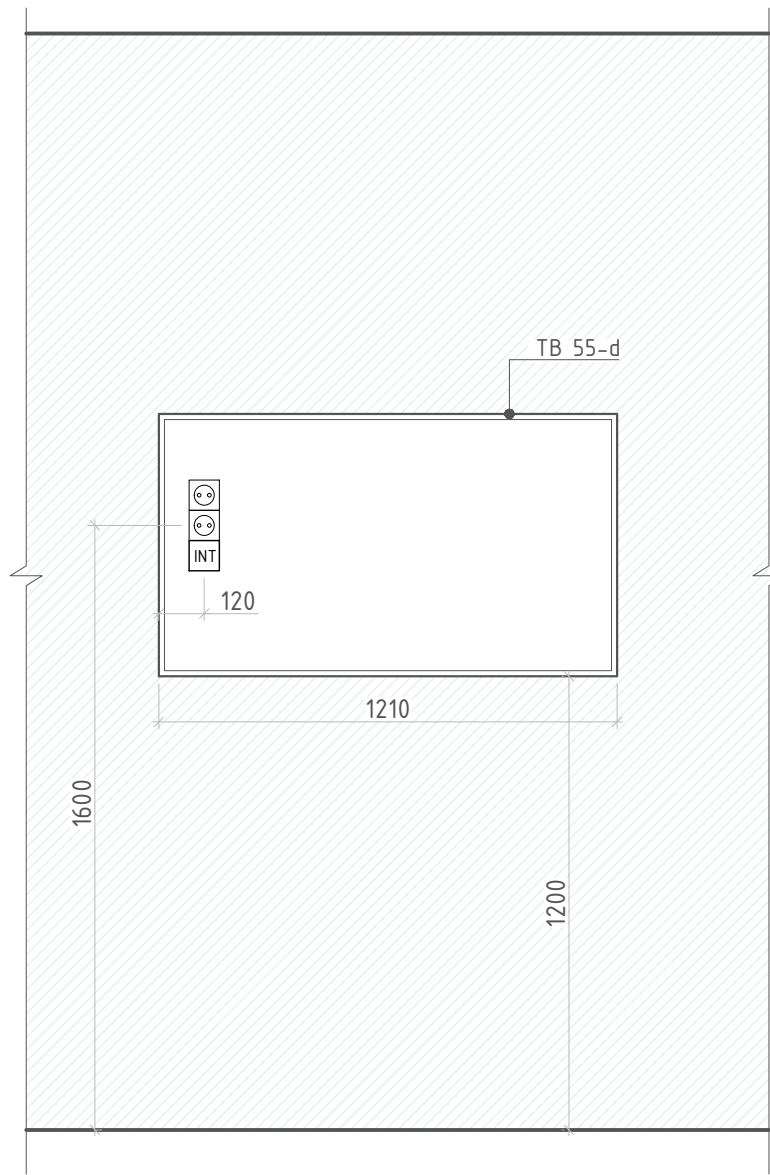

	Лист	Листов
	4	--
Фрагменты;		