



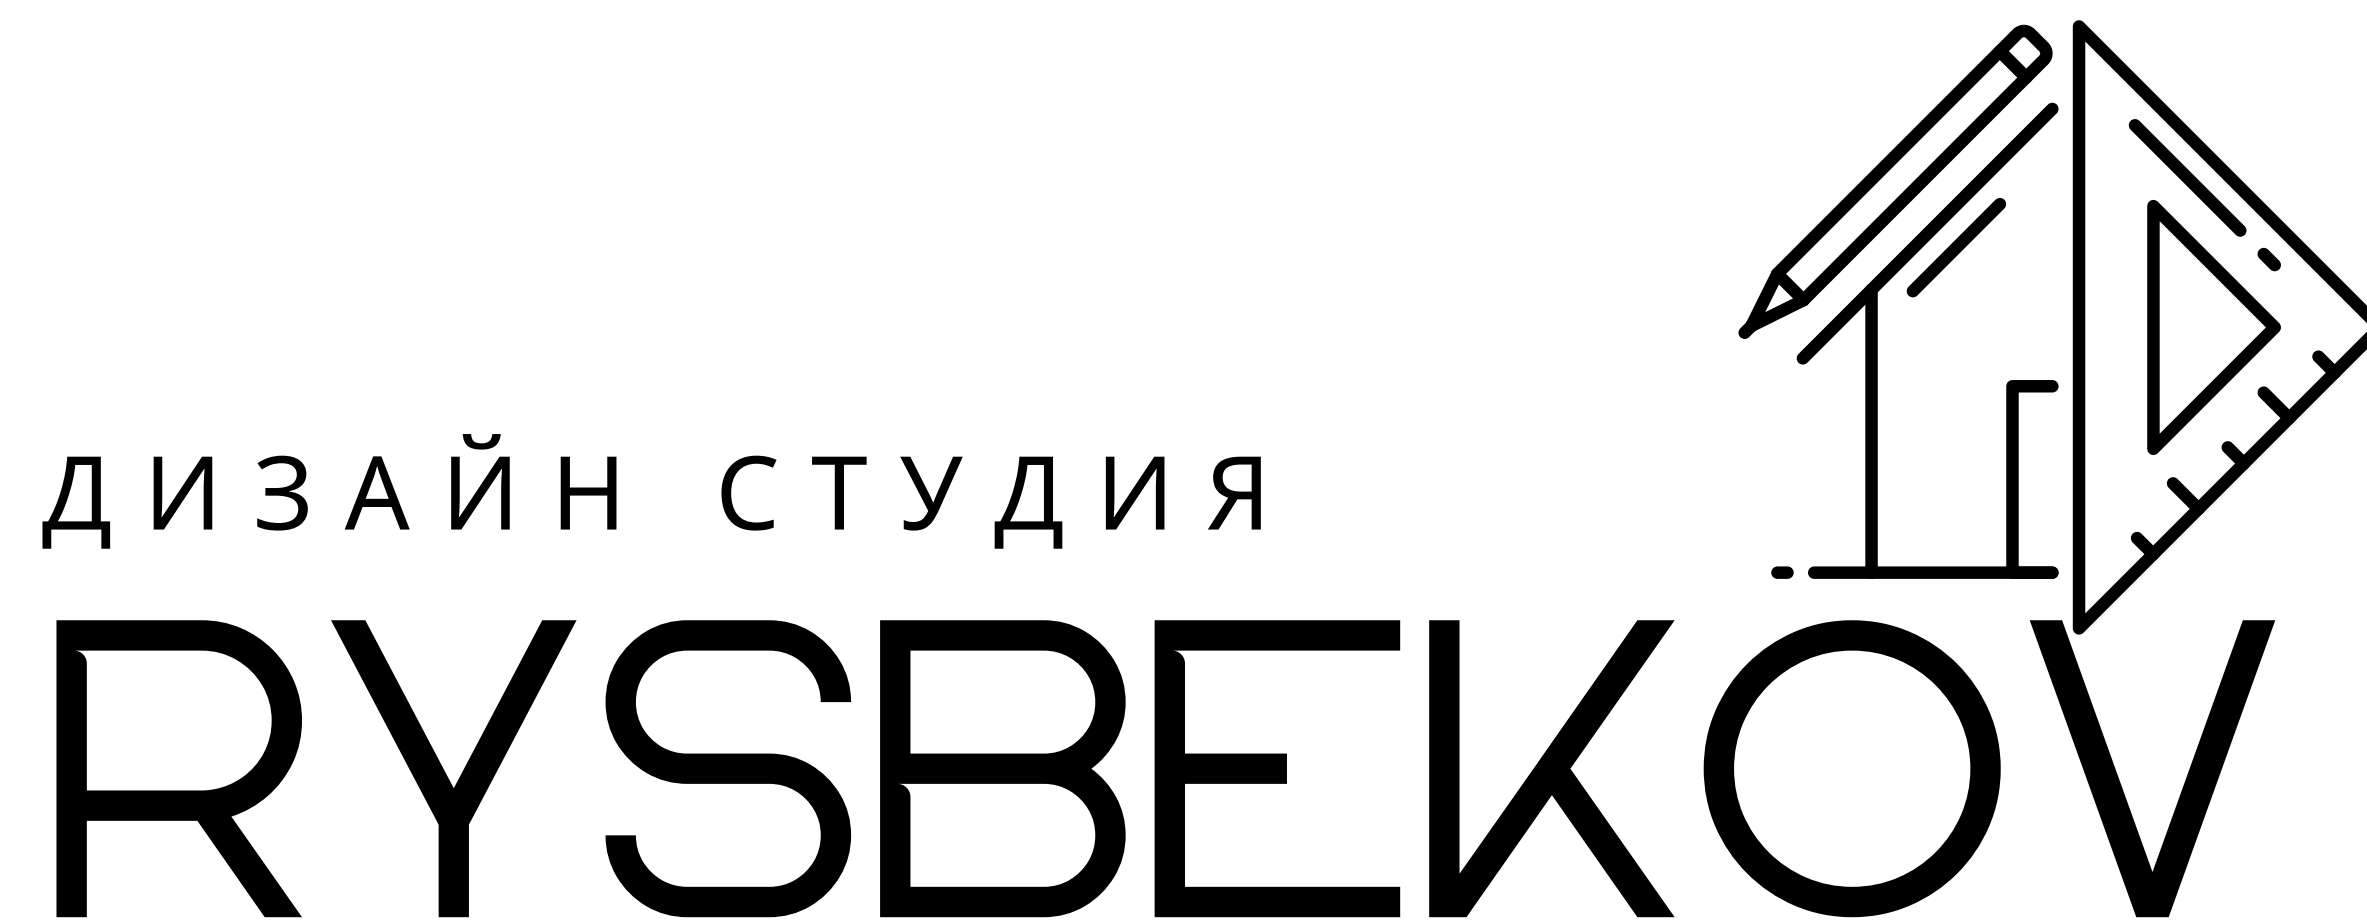

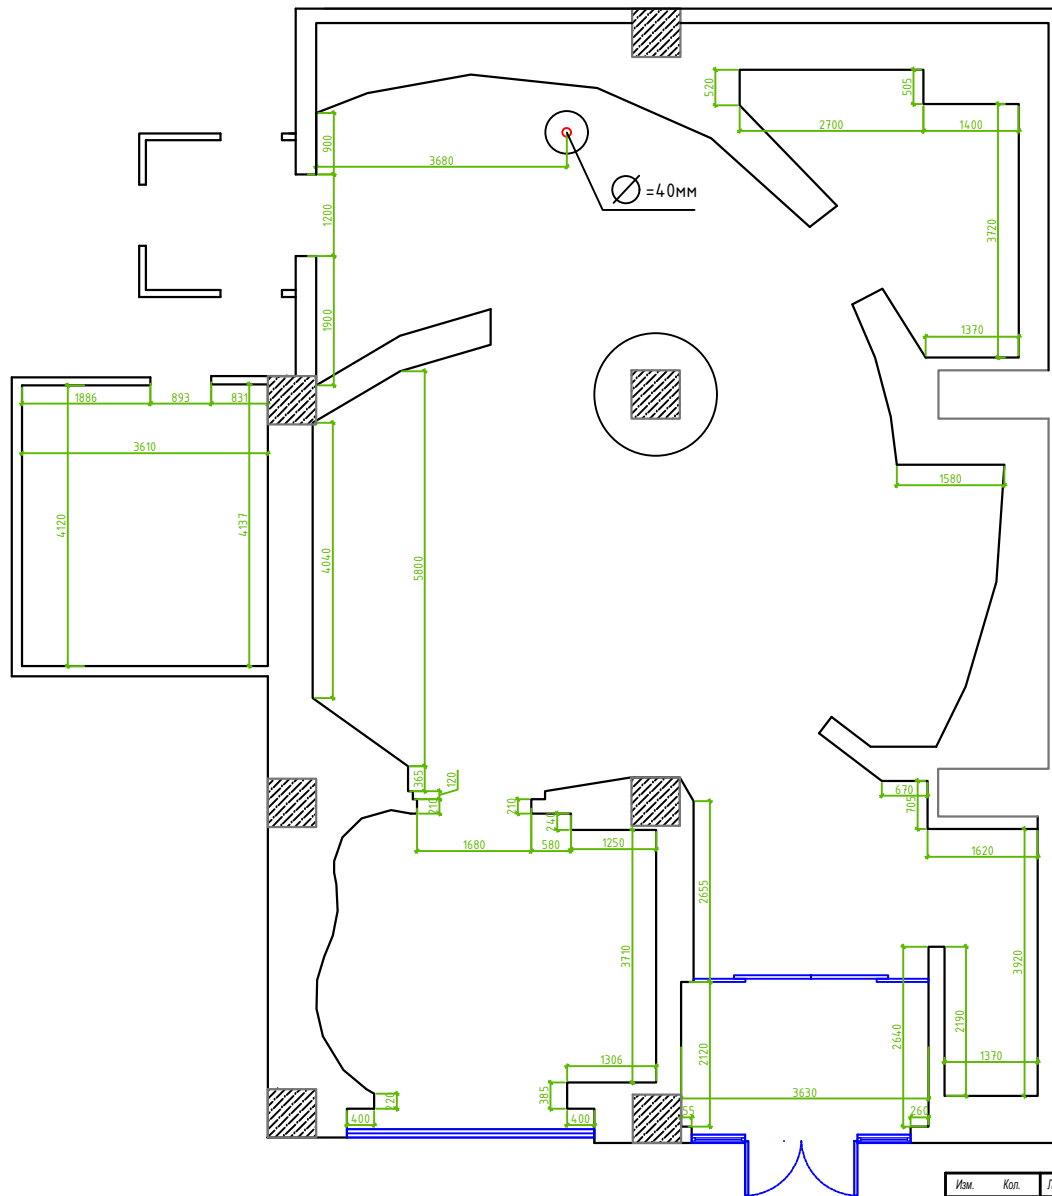

УСЛОВНЫЕ ОБОЗНАЧЕНИЯ



Колонны несущие




Базовые стены

Изм.	Кол.	Лист	Индок.	Подпись	Дата	г. Астана, Био бутик "Tell.kz"	Стадия	Лист	Листов
					03.2026		РП	2	9
Проверил						Обмерный план			
Выполнил									

монтаж перегородки конференц зала
в одну линию со стеной коридора

Ø = 40 мм
перенести на стену

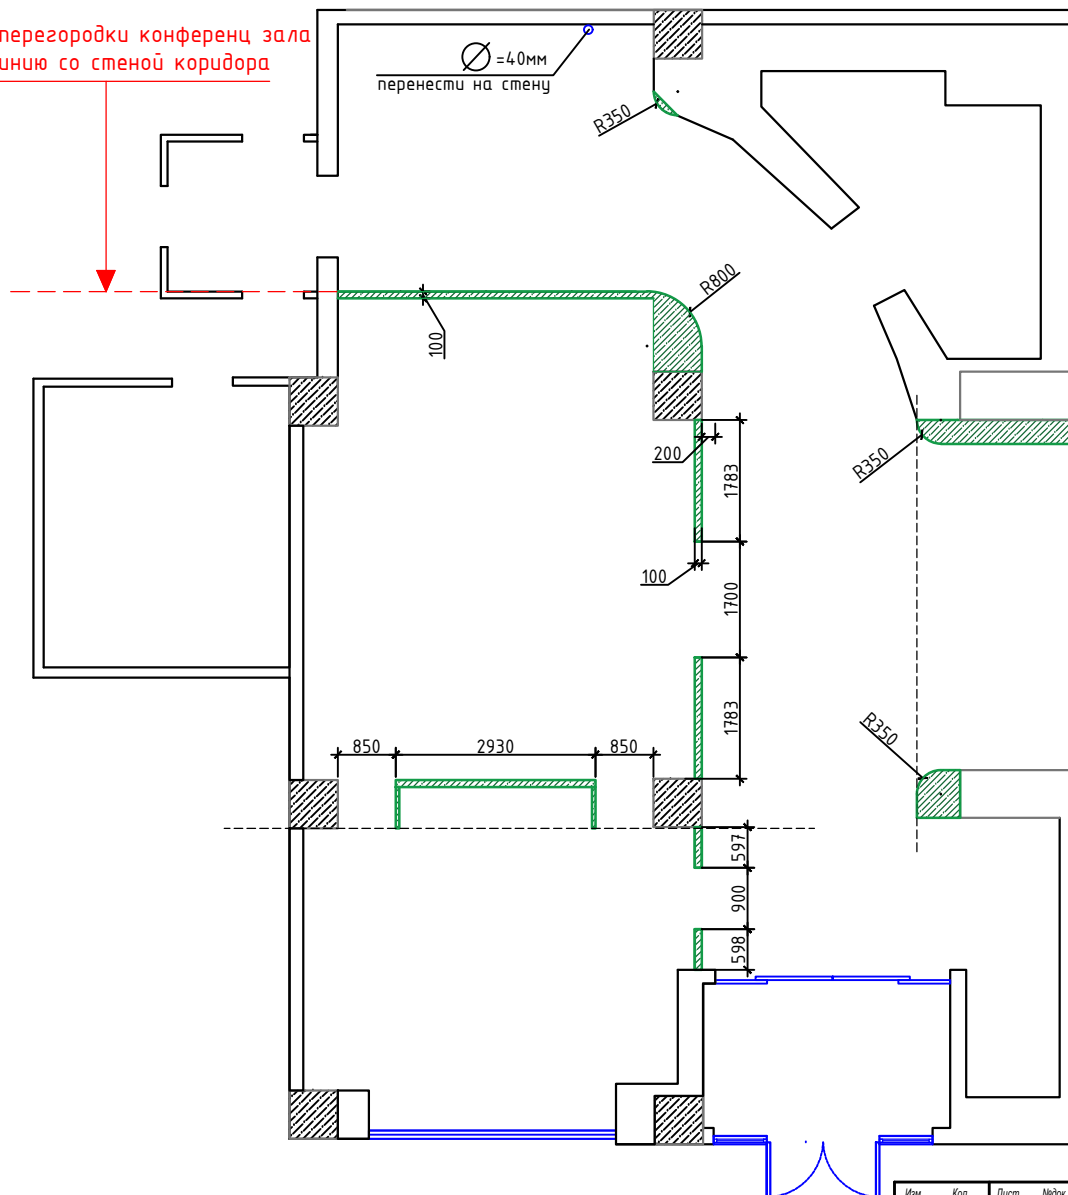

УСЛОВНЫЕ ОБОЗНАЧЕНИЯ



Колонны несущие



Базовые стены




Возводимые перегородки

Примечание:

Высота дверных проемов 2400 мм


Изм.	Кол.	Лист	Индок.	Подпись	Дата	г. Астана, Био бутик "Tell.kz"	Стадия	Лист	Листов
					03.2026		РП	4	9
Проверил						План монтажа			
Выполнил									

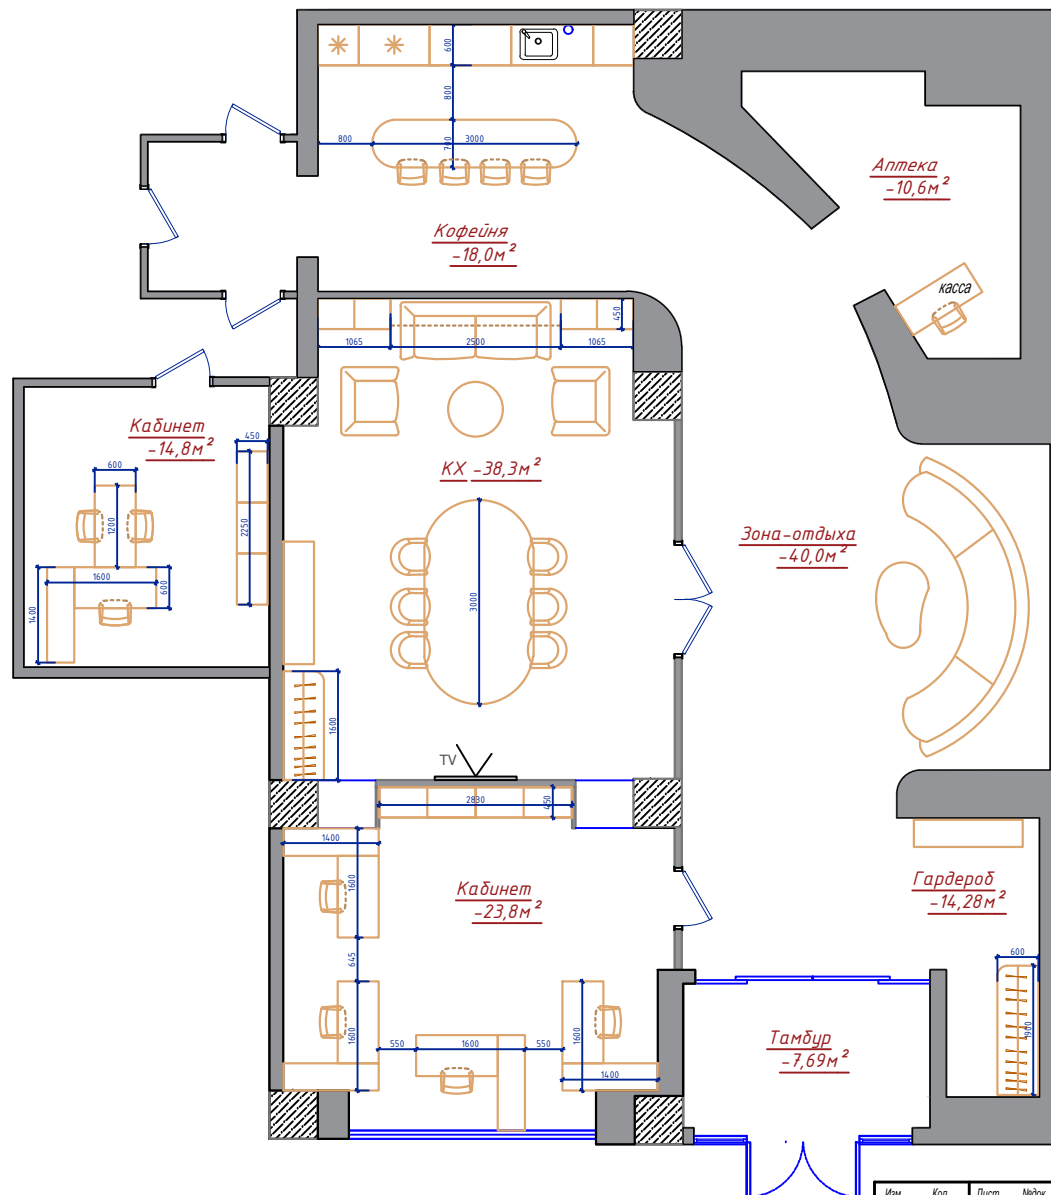

Примечание:

Общая площадь после
перепланировки - 167,47


Изм.	Кол.	Лист	Индок.	Подпись	Дата	г. Астана, Бюо бутик "Tell.kz"	Стадия	Лист	Листов
					03.2026		РП	5	9
Проверил						План расстановки мебели			
Выполнил									

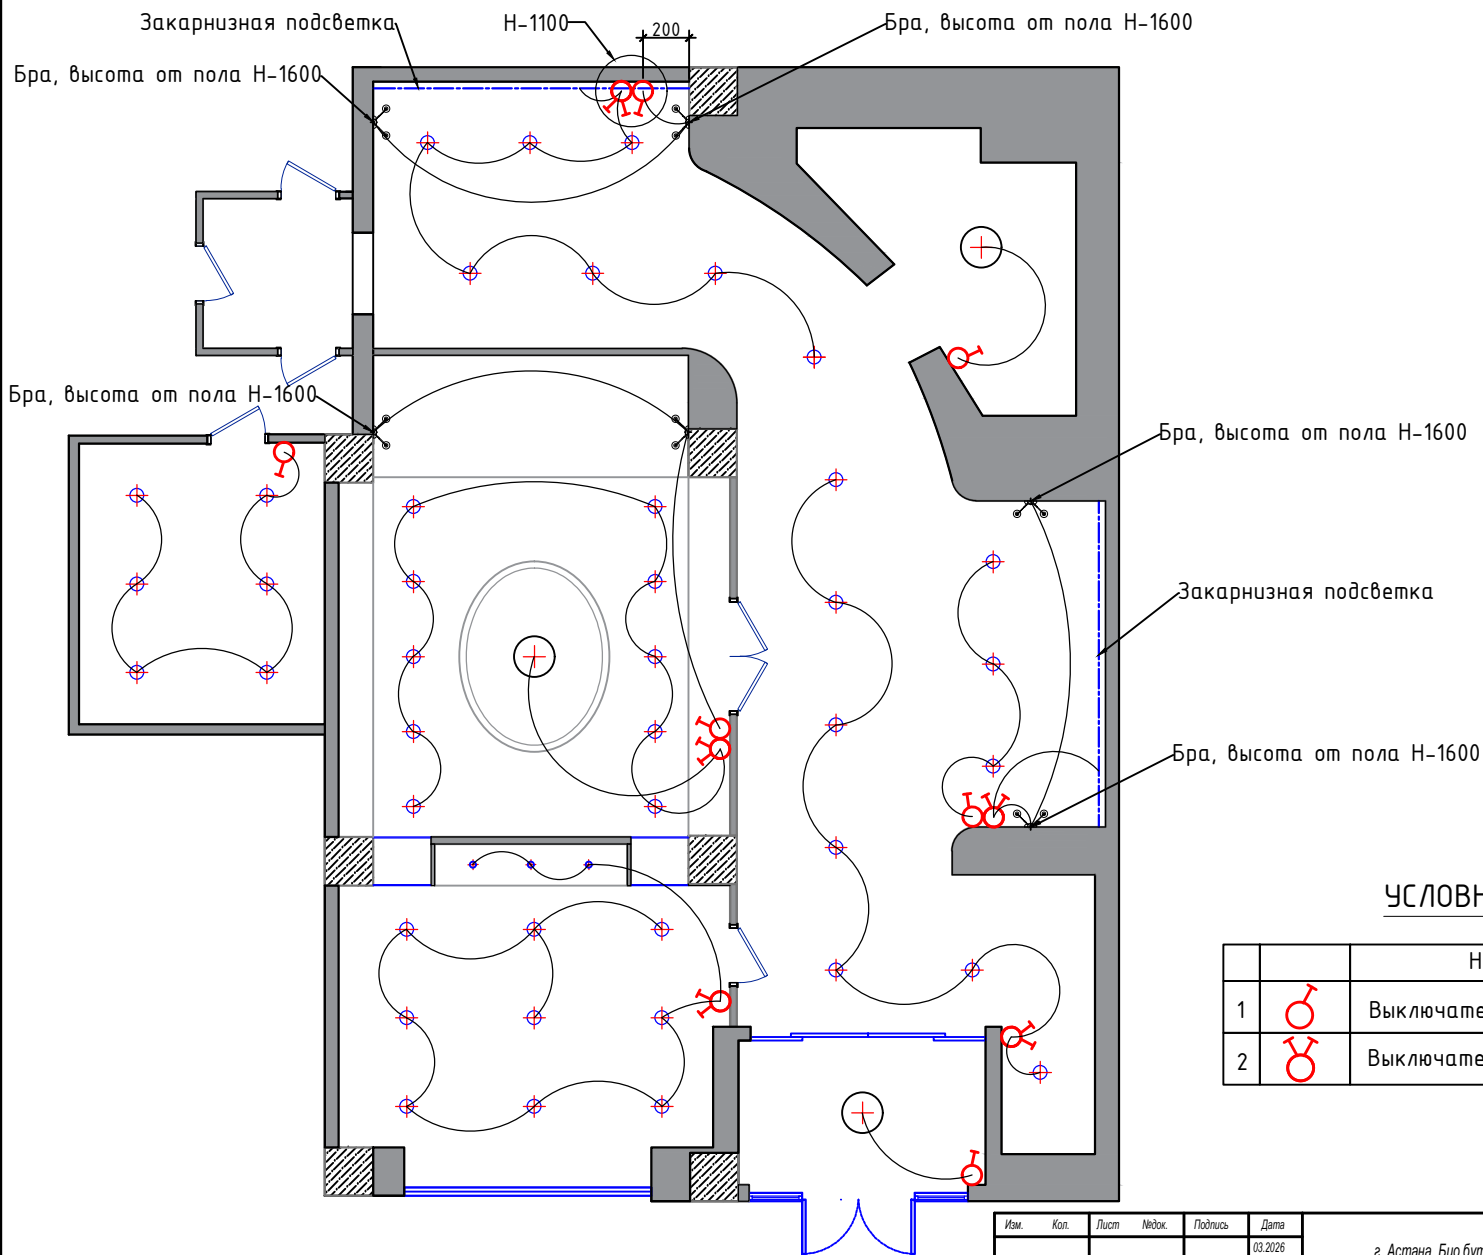

УСЛОВНЫЕ ОБОЗНАЧЕНИЯ

		Наименование	Кол-во
1	♂	Выключатель одноклавишный	6 шт.
2	♂♂	Выключатель двухклавишный	5 шт.

Изм.	Кол.	Лист	Индок.	Подпись	Дата	г. Астана, Бюо бутик "Tell.kz"	Стадия	Лист	Листов
					03.2026		РП	7	9
Проверил						План выключателей			
Выполнил									

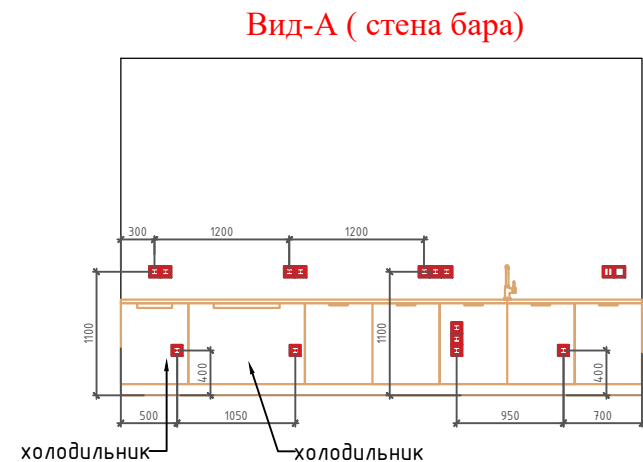


УСЛОВНЫЕ ОБОЗНАЧЕНИЯ

		Наименование	Кол-во
1		Розетка одинарная	15 шт.
2		Розетка двойная	7 шт.
3		Розетка тройная	4 шт.
4		Розетка UTP (интернет)	7 шт.
5		Вывод 220W (существующие)	3 шт.
6		Напольные розетки (касса аптека)	2 шт.

—Оставить существующий вывод для тепловой завесы
питанием = 5x6

Изм.	Коп.	Лист	Медок.	Подпись	Дата	г. Астана, Био бутик "Telli.kz"	Статья	Лист	Листов
					03.2026		Р/П	8	9
Проверил						План расстановки розеток			
Выполнил									

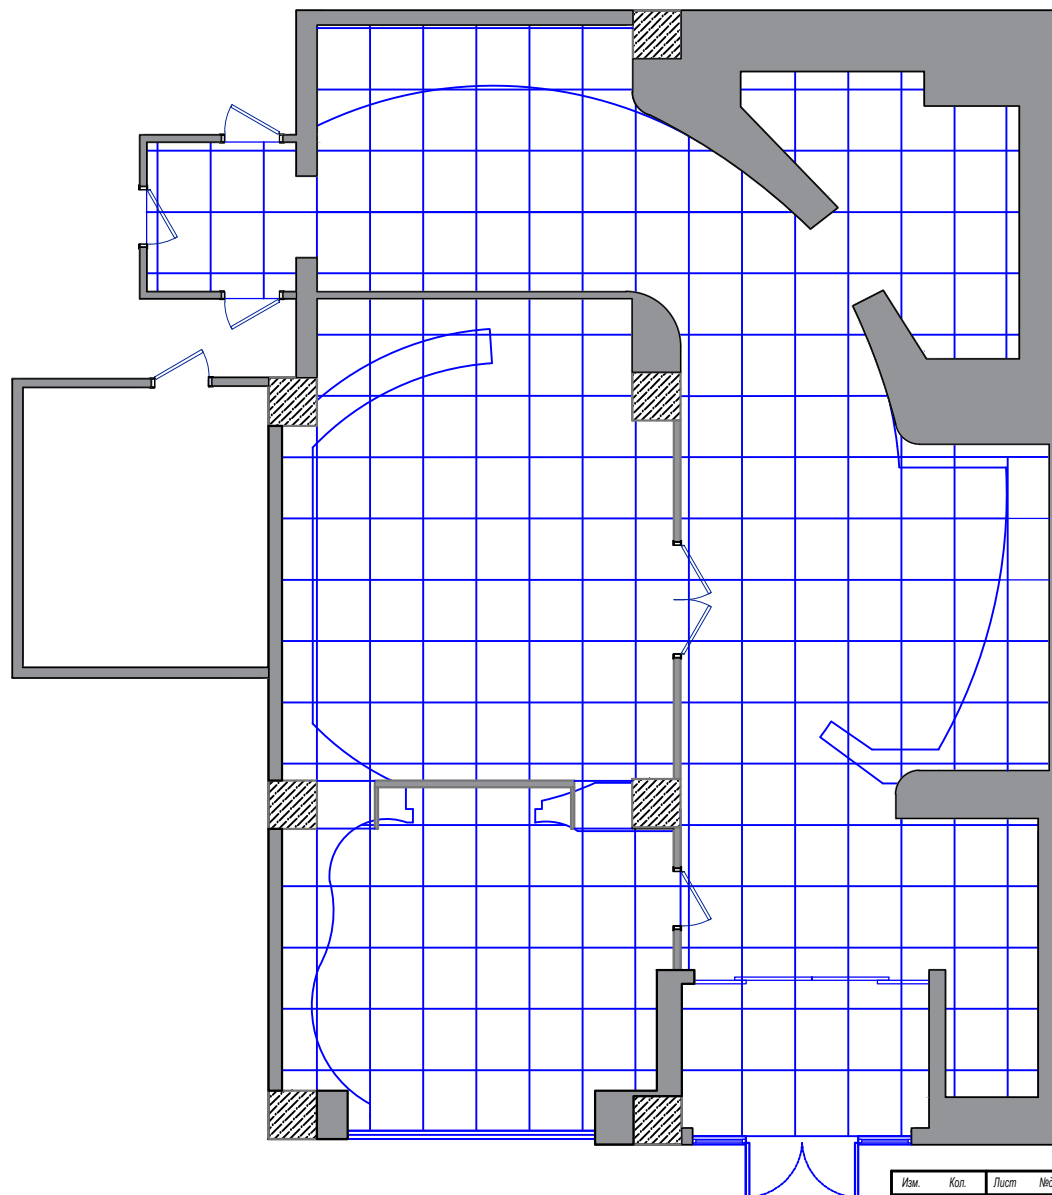

УСЛОВНЫЕ ОБОЗНАЧЕНИЯ

 Существующий мрамор

Примечание:

В местах где производился демонтаж перегородок, подобрать похожий мрамор

Изм.	Кол.	Лист	Индок.	Подпись	Дата	г. Астана, Био бутик "Tell.kz"	Стадия	Лист	Листов
					03.2026		РП	9	9
Проверил						План пола			
Выполнил									