



Условные обозначения


- теплый пол Тn1 S = 1,95м2
- теплый пол Тn2 S = 0,86 м2
- теплый пол Тn3 S = 0,89 м2
- теплый пол Тn4 S = 1,10 м2
- теплый пол Тn5 S = 1,43 м2
- терморегулятор Н=1600мм

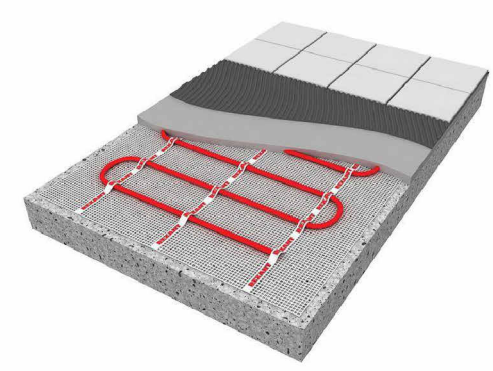

ДИЗАЙН - ПРОЕКТ КВАРТИРЫ

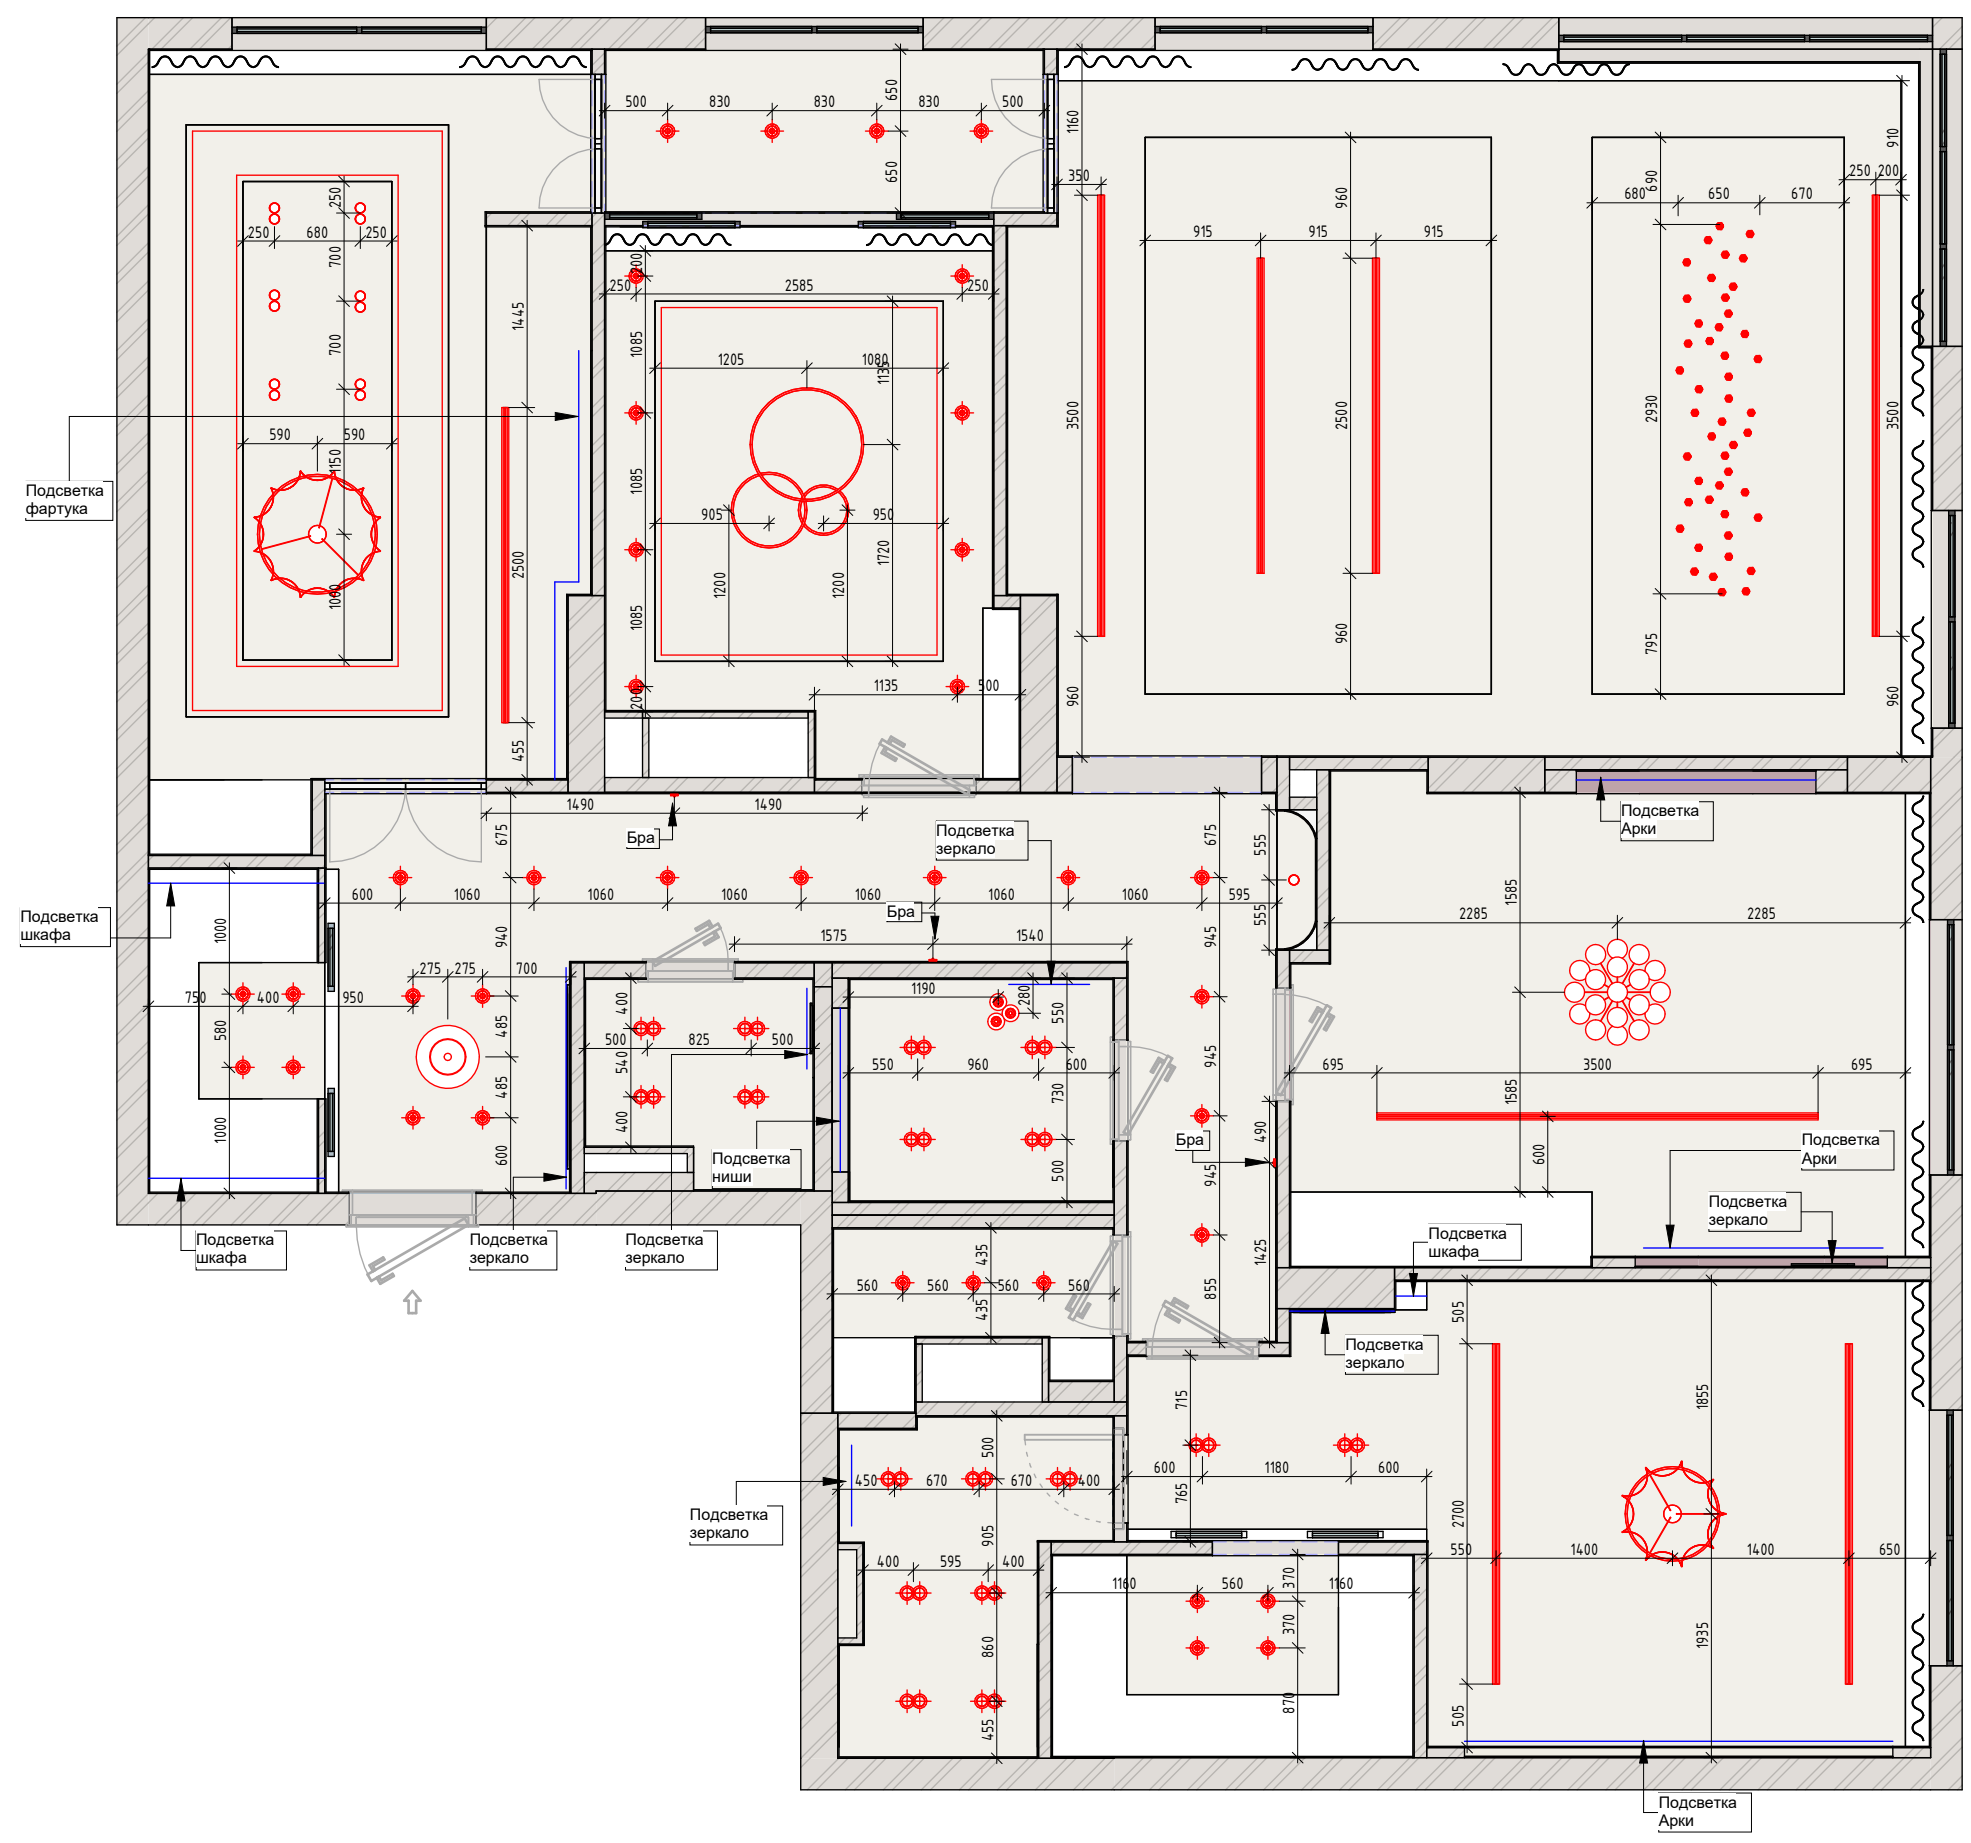

- Условные обозначения
- Двойные споты
 - Споты
 - Подвесной светильник
 - Люстра
 - Подсветка потолка
 - Подсветка

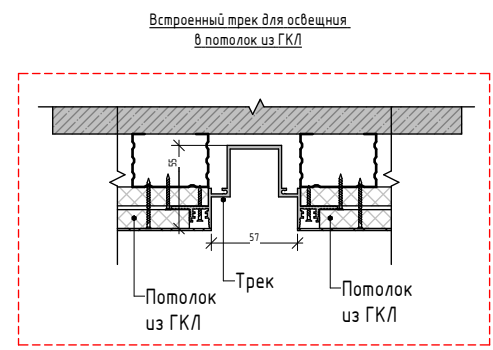

Дополнительные примечания

1. Разметить места расположения точечных светильников и согласовать с заказчиком.

Примечание:

1. Комплект рабочих чертежей разработан на основе обмеров.

2. Все размеры указаны в миллиметрах.


3. Перед началом работ все размеры проверить по месту.


ДИЗАЙН - ПРОЕКТ КВАРТИРЫ

*Спецификация силовых электроприборов – ВЫКЛЮЧАТЕЛИ по...		
Условное обозначение 2	Описание	Число
	Выключатель одноклавишный	5
	Выключатель двухклавишный	12
	Выключатель одноклавишный (мастер)	1
	Переключатель одноклавишный	2
	Переключатель двухклавишный	2
	Перекрестный переключатель двухклавишный	9

ДИЗАЙН – ПРОЕКТ КВАРТИРЫ

Схема освещения

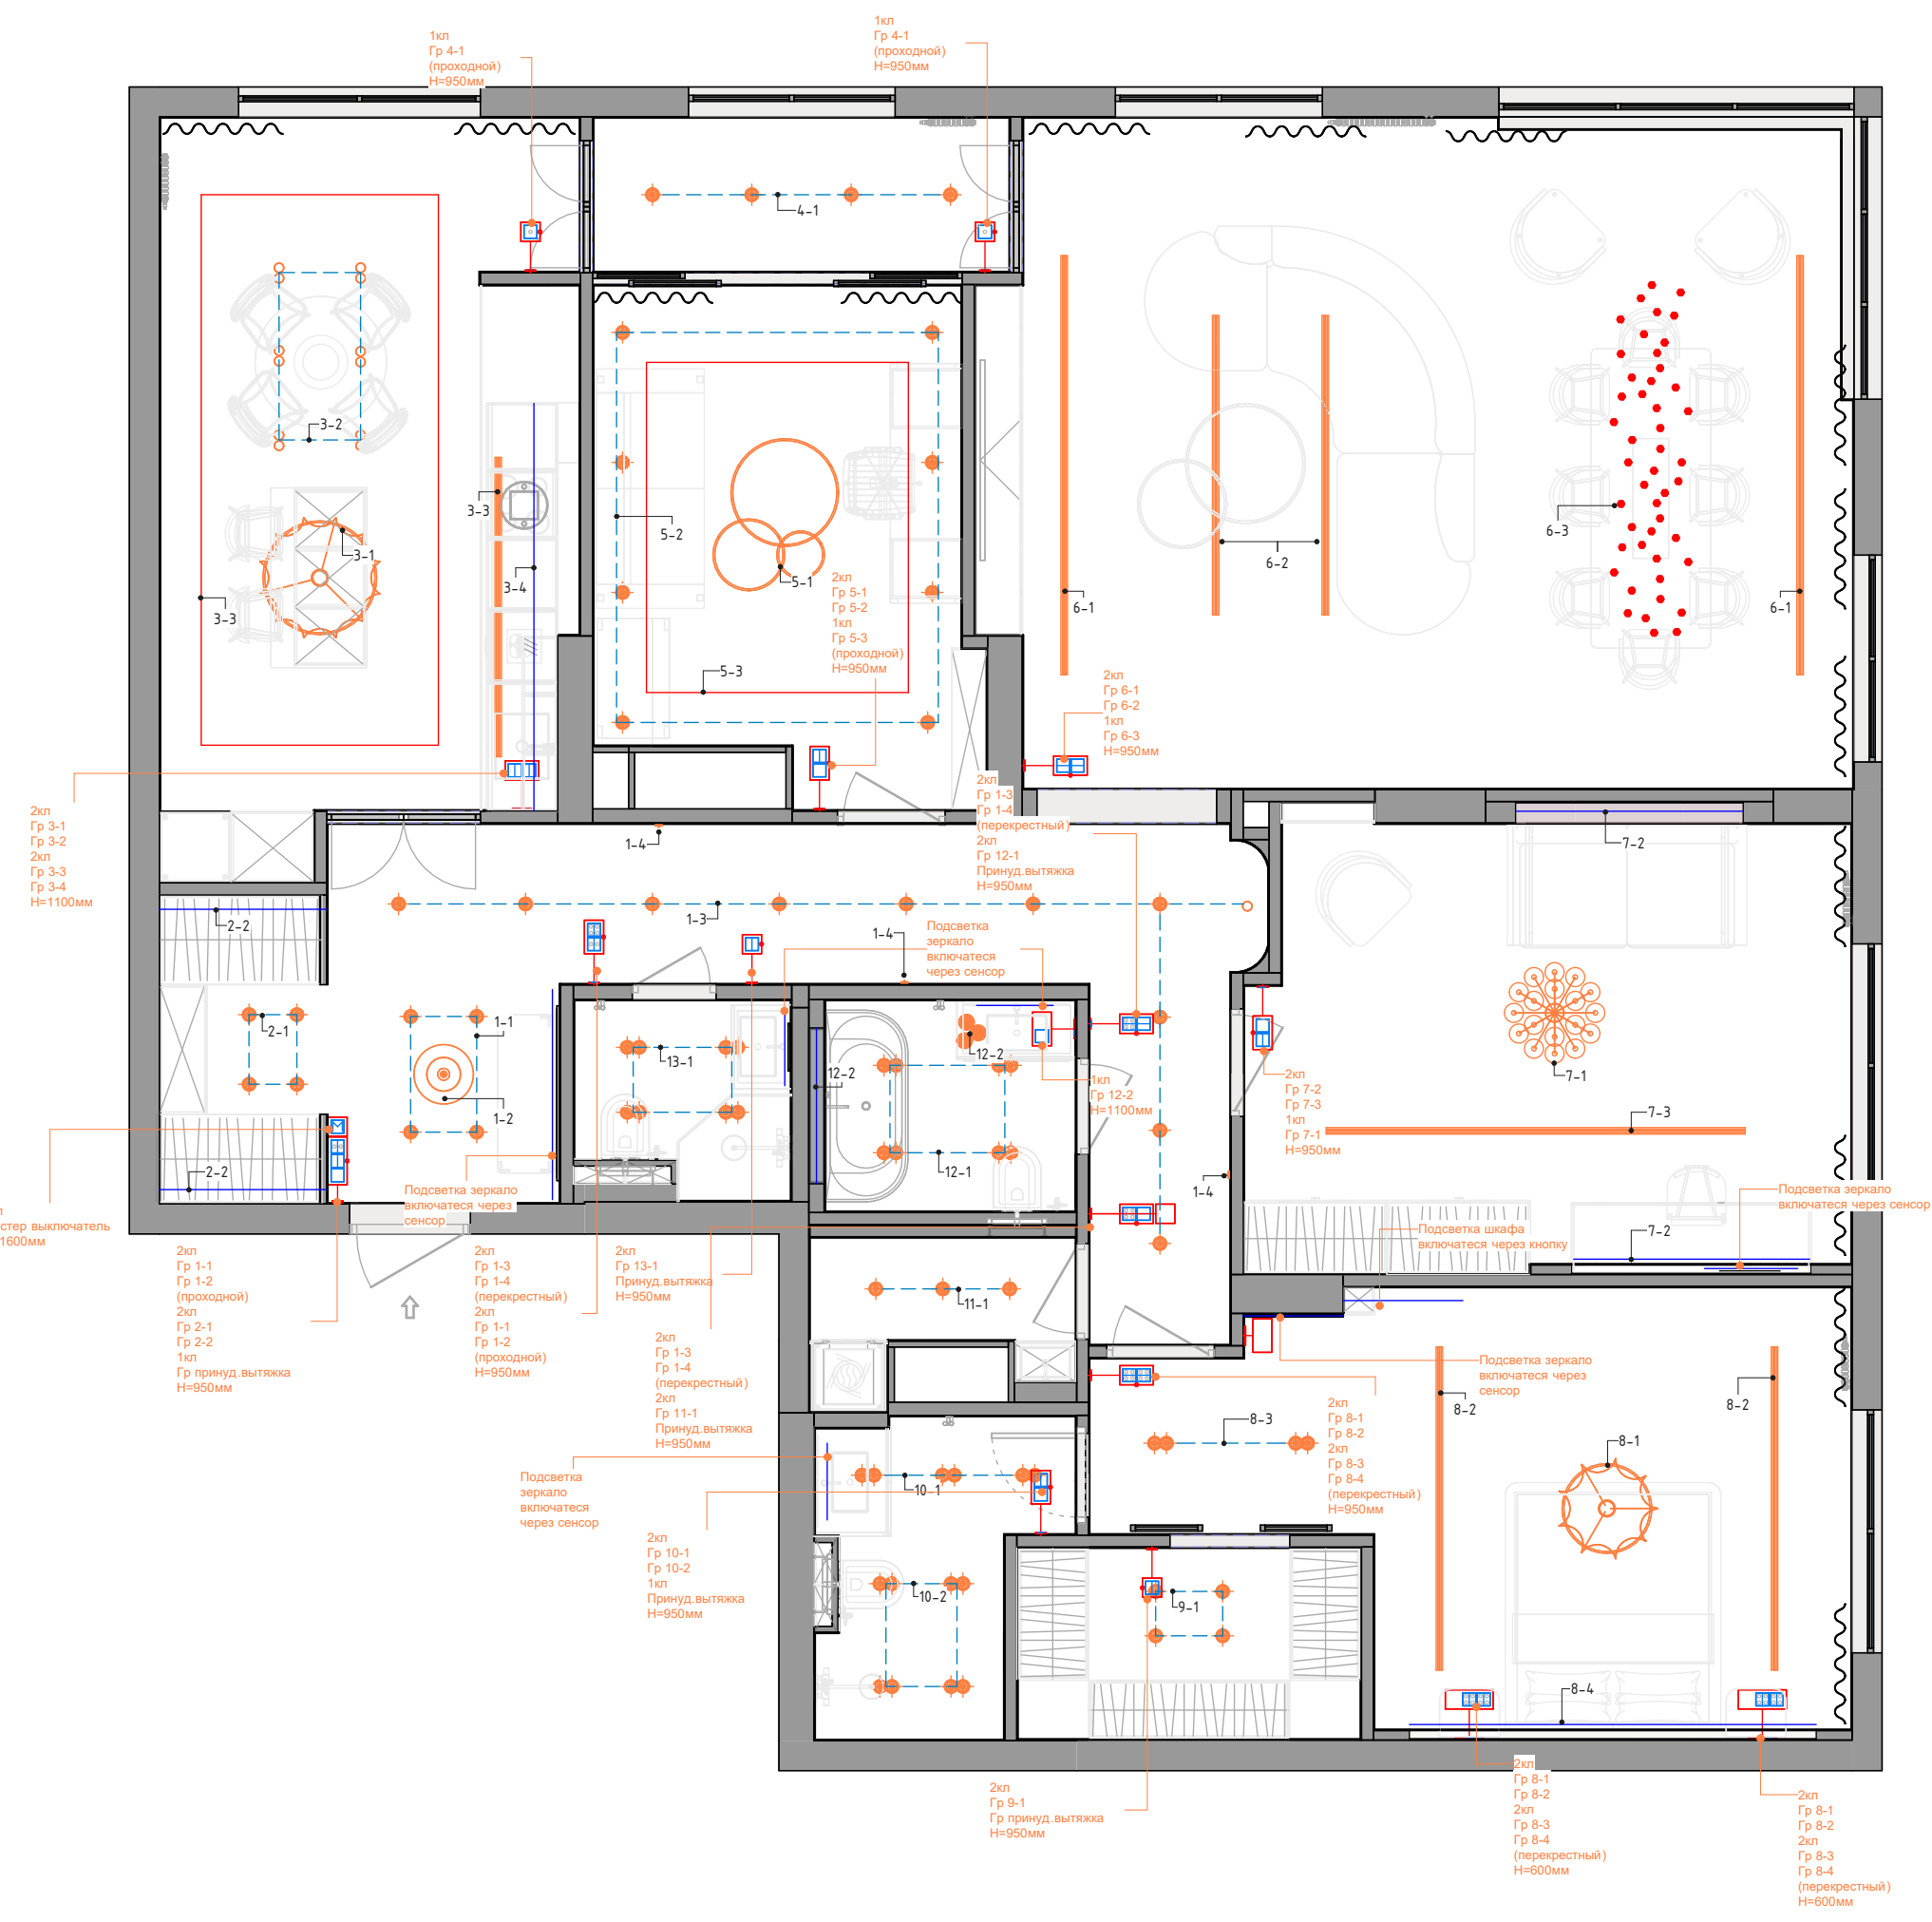

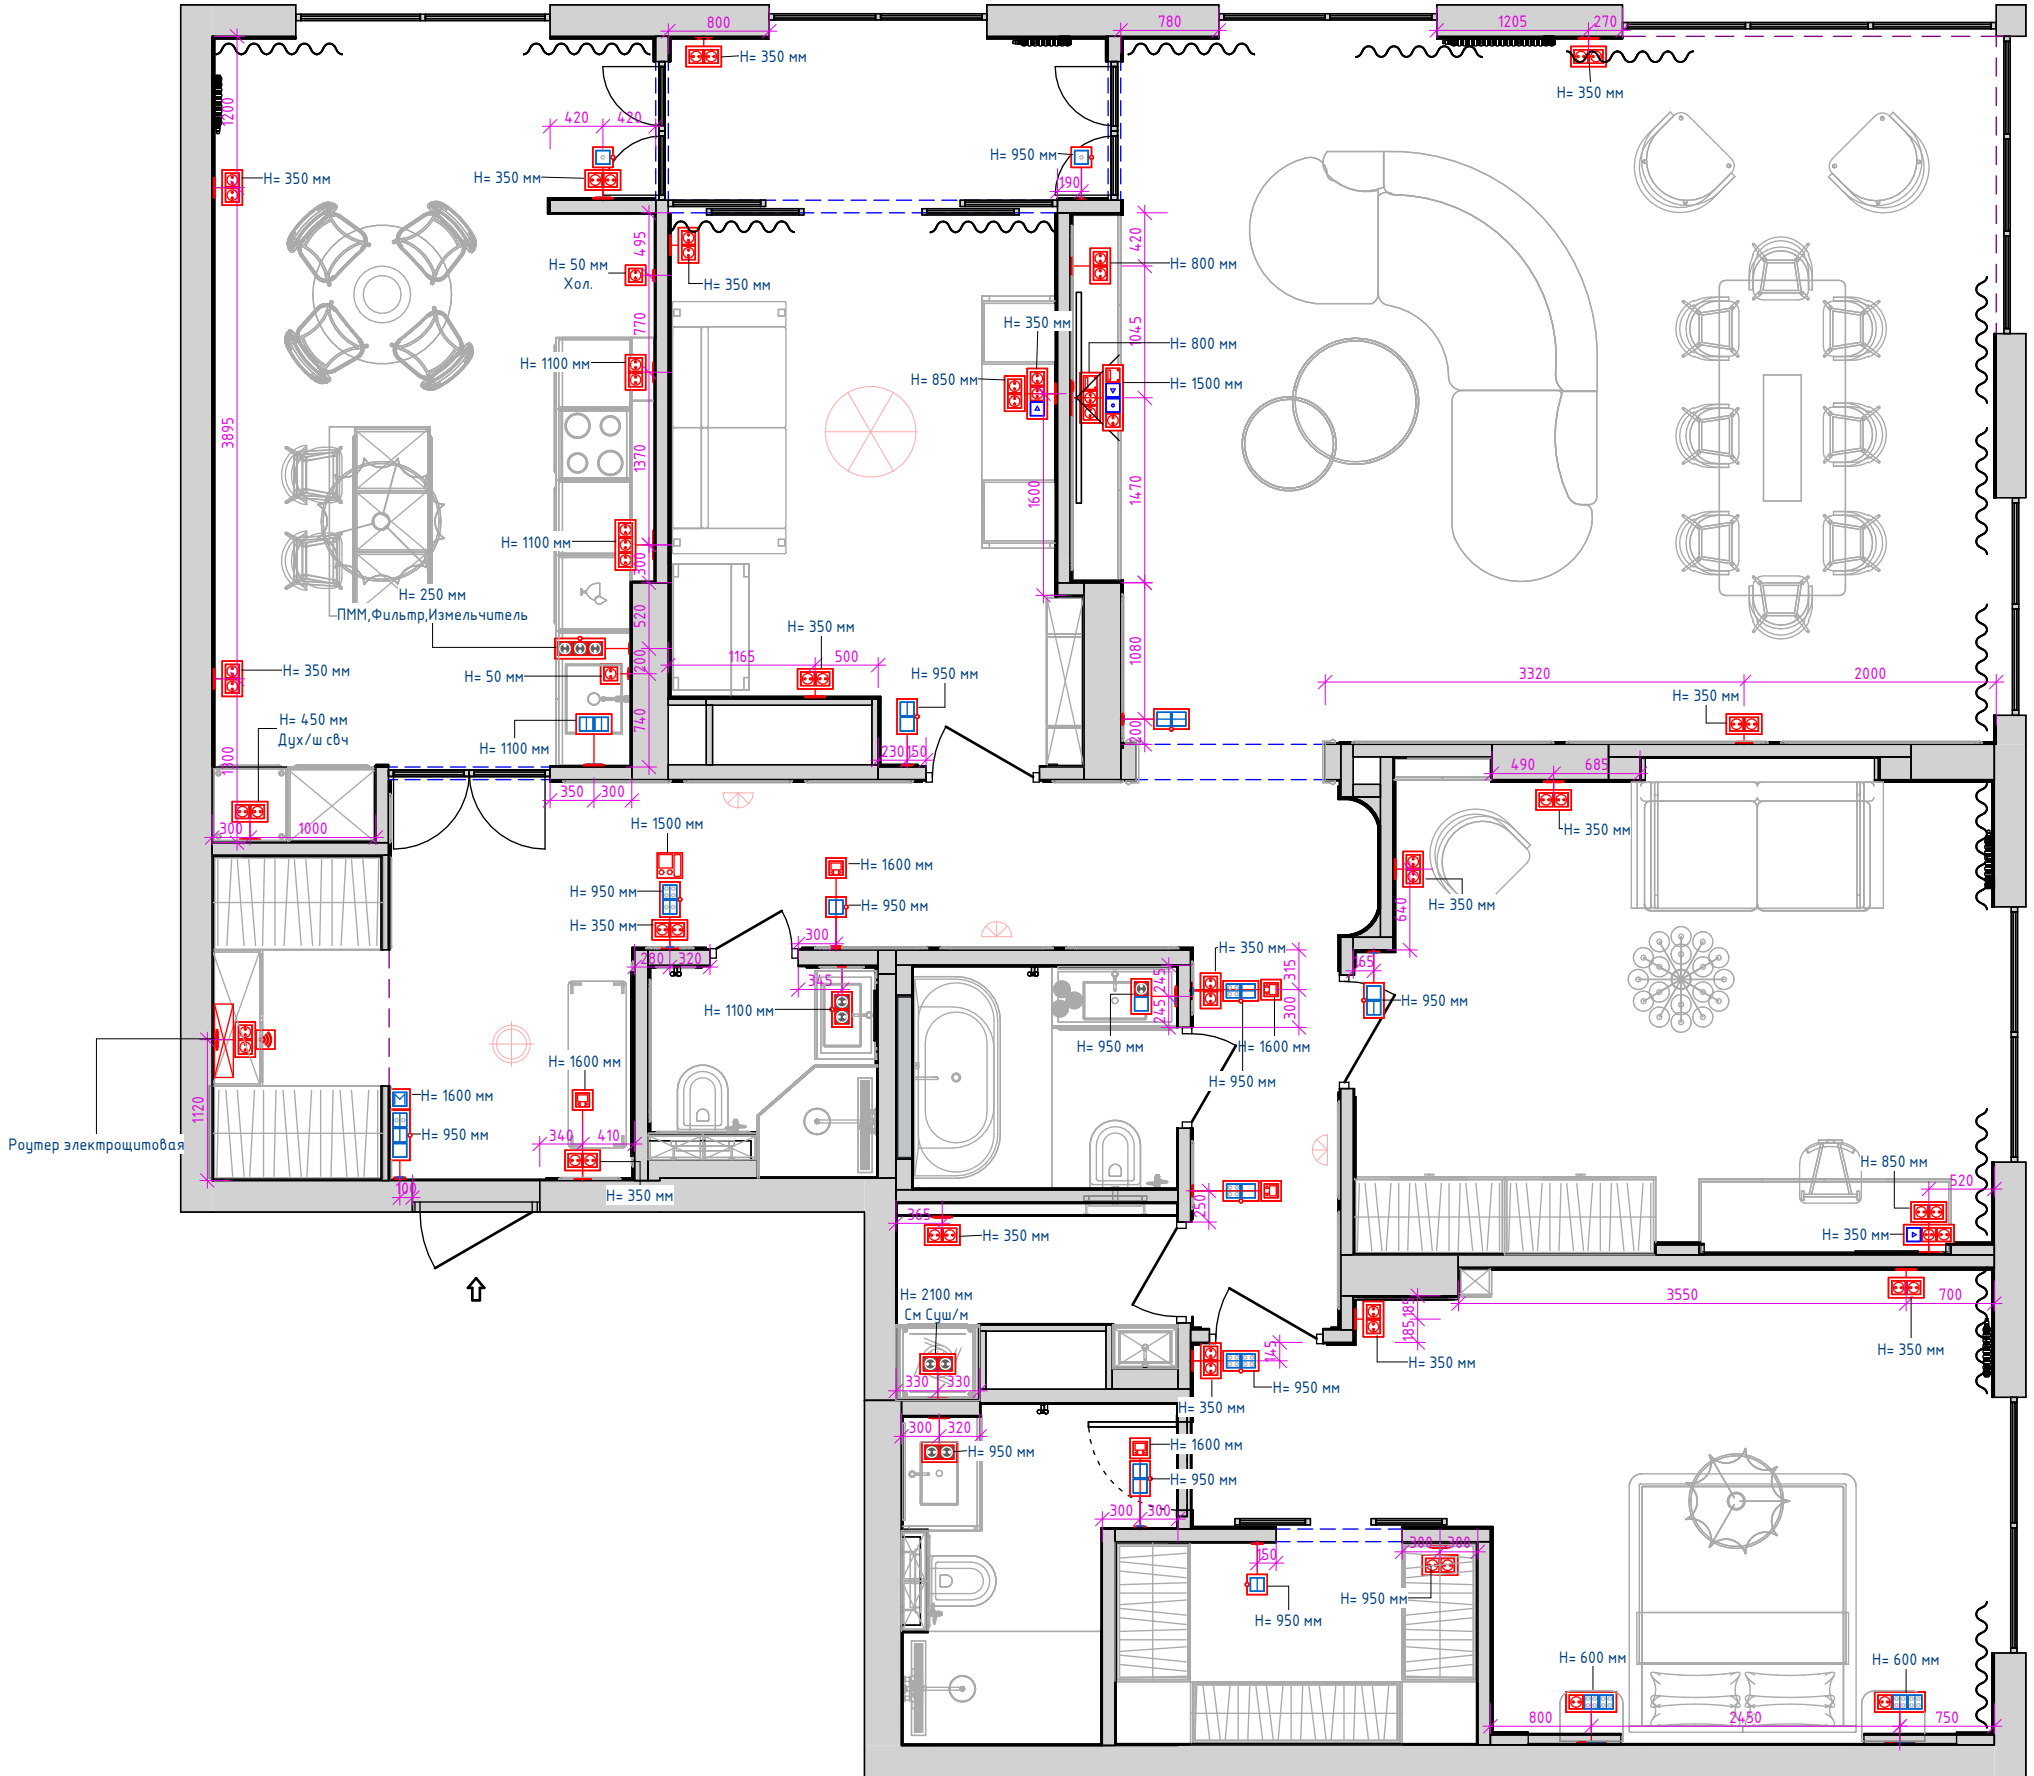


Примечание:
1. Комплект рабочих чертежей разработан на основе обмеров.
2. Все размеры указаны в миллиметрах
3. Перед началом работ все размеры проверить по месту

* Спецификация силовых электроприборов – ИТОГО РАМКИ		
Тип	Число	Описание
1х	12	Рамка на 1 пост
2х	37	Рамка на 2 поста
3х	8	Рамка на 3 поста
4х	1	Рамка на 4 поста

*Спецификация силовых электроприборов – ВЫКЛЮЧАТЕЛИ по...		
Условное обозначение 2	Описание	Число
	Выключатель одноклавишный	5
	Выключатель двухклавишный	12
	Выключатель одноклавишный (мастер)	1
	Переключатель одноклавишный	2
	Переключатель двухклавишный	2
	Перекрестный переключатель двухклавишный	9

*Спецификация силовых электроприборов – РОЗЕТКИ по...		
Условное обозначение 2	Описание	Число
	Терморегулятор теплого пола электронный	5
	Розетка 220V	62
	Розетка 220V IP44 влагозащищенная	10
	Интернет розетка RJ45 1х	3
	TV розетка 1х	1
	WiFi роутер	1
	Аудиодомофон	1
	Заглушка кабель-канала	2

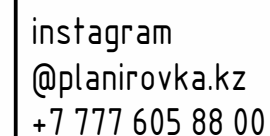

Условное обозначение 2	Число	Описание
 220V	35	Вывод кабеля 220V

План выводов