



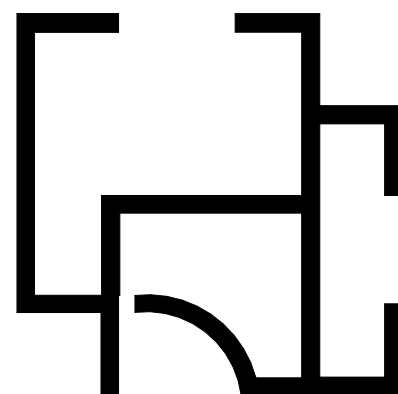

Ahmetova_design14

ТЕХНИЧЕСКИЙ ПРОЕКТ


Астана 2026 г.
Inst. ahmetova_design14
тел. 7 747 613 18 32

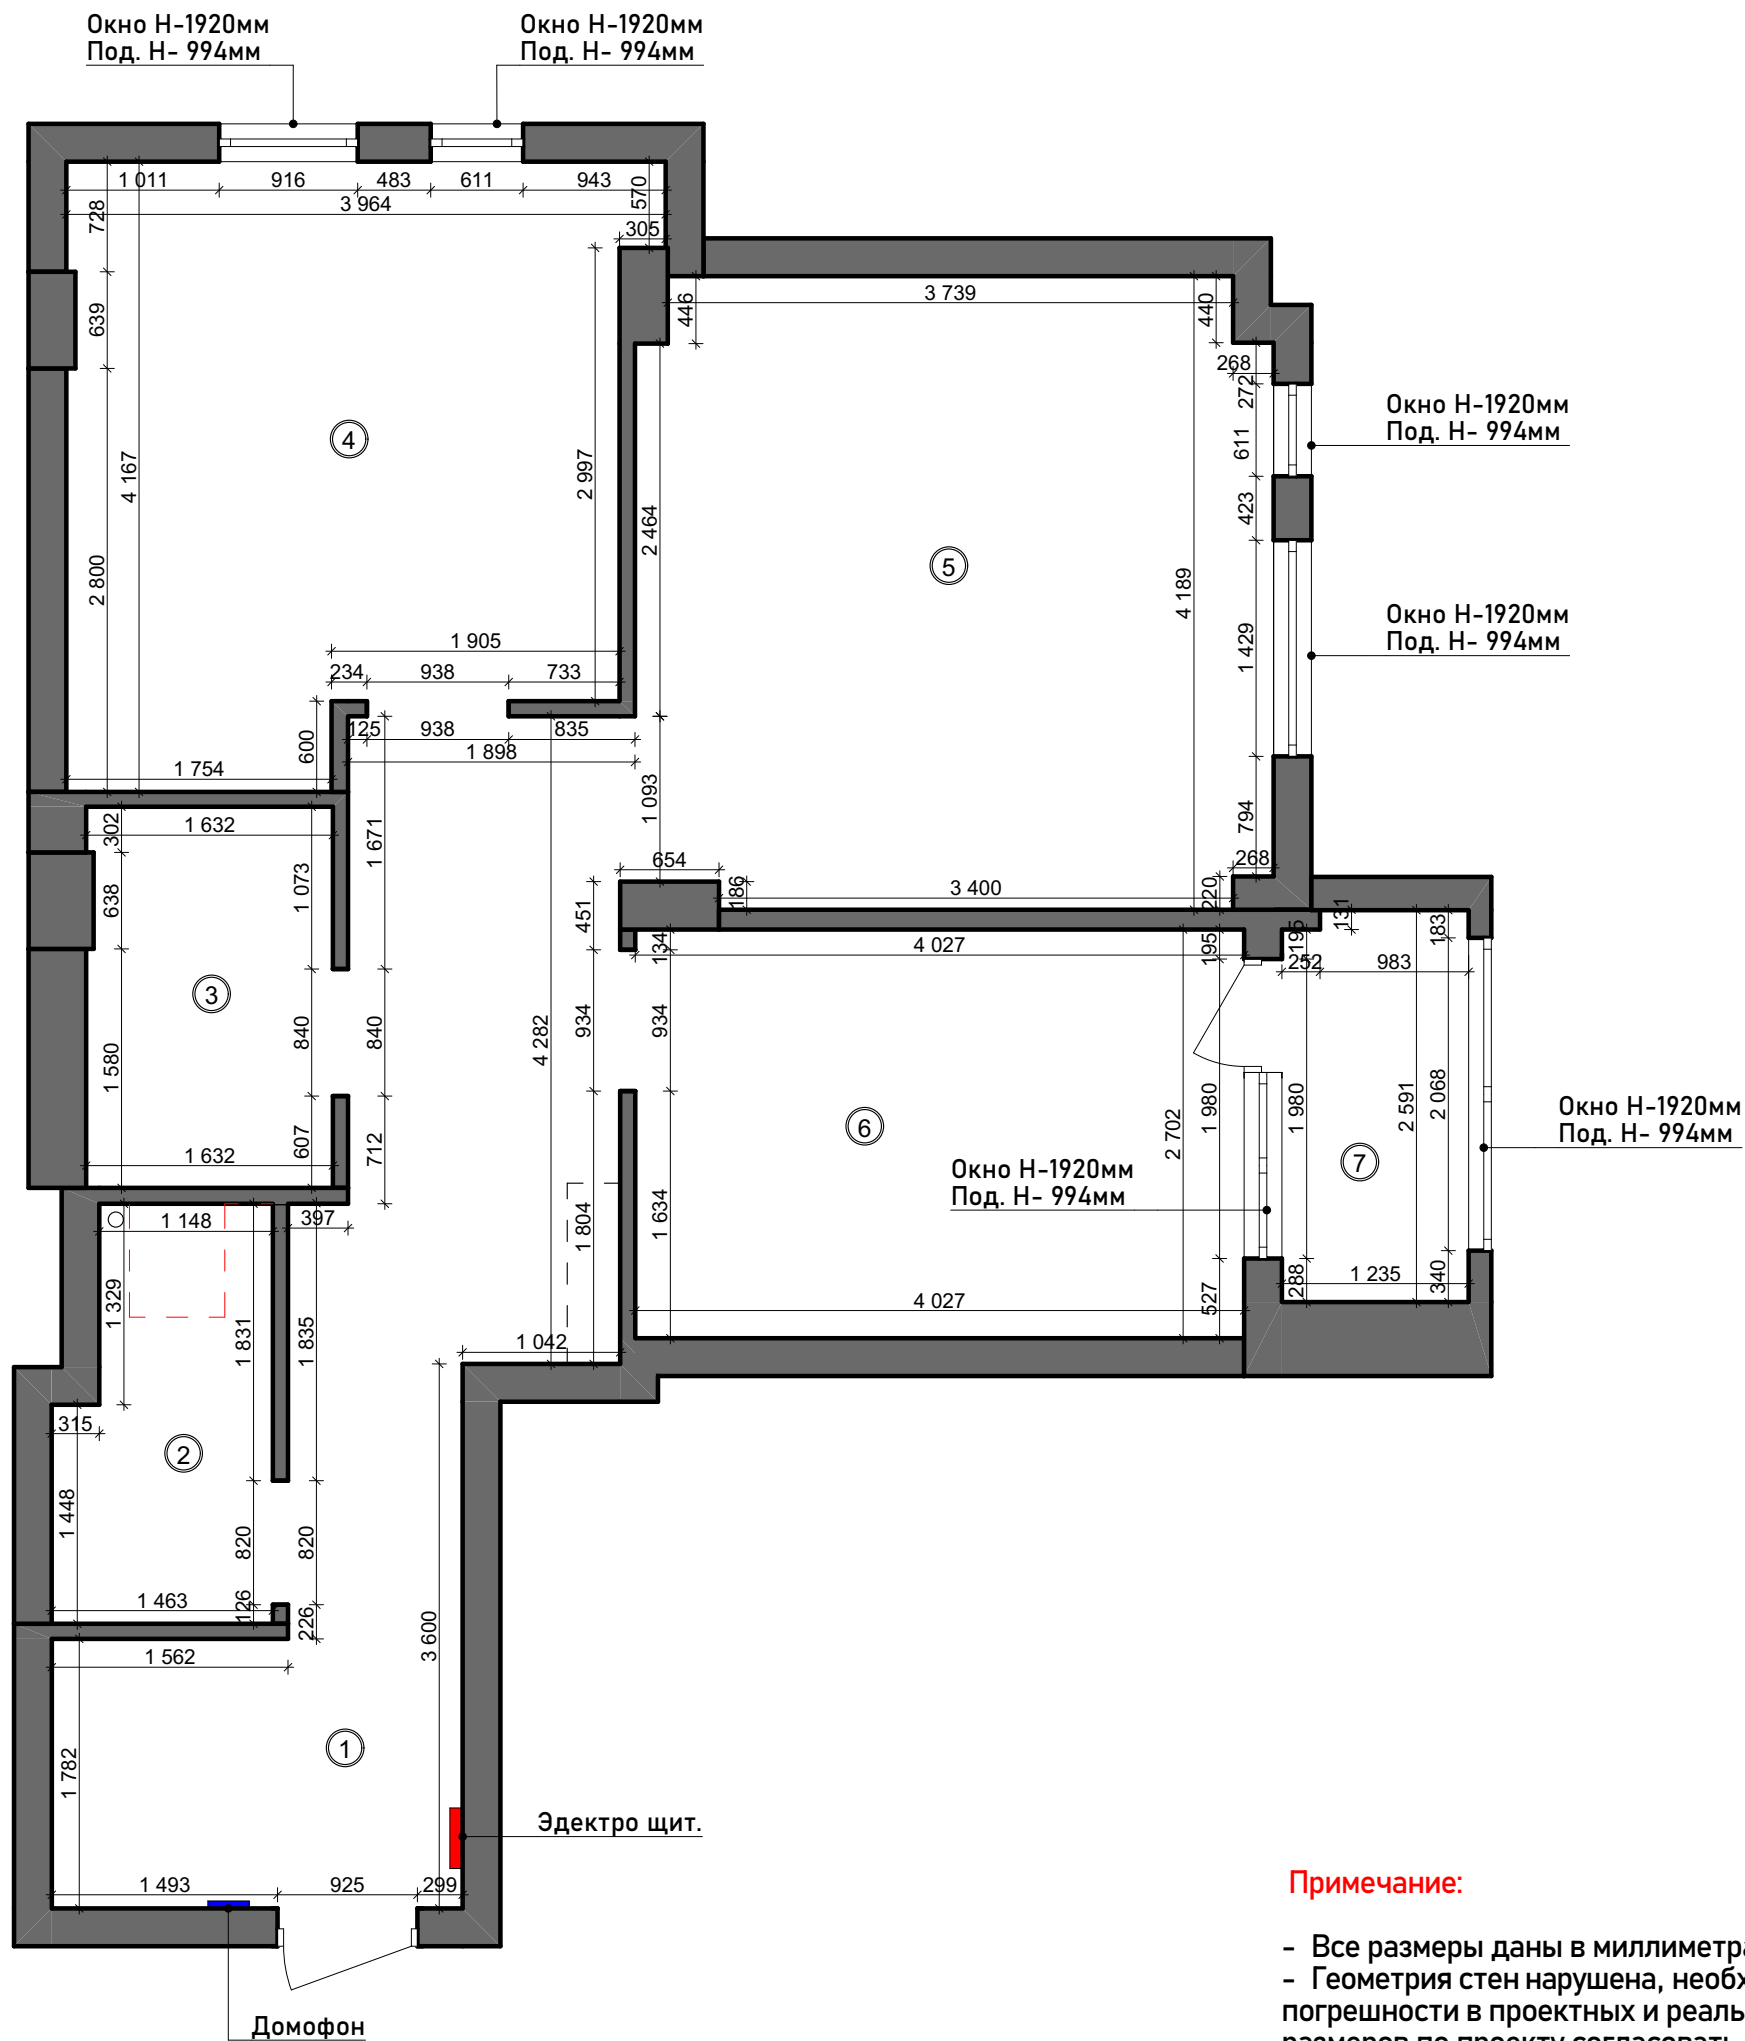

Примечание:

- Все размеры даны в миллиметрах.
- Геометрия стен нарушена, необходимо учитывать возможные погрешности в проектных и реальных размерах, (несоответствия размеров по проекту согласовать с дизайнером).
- Размеры даны без учета выравнивания стен, пола, потолка.

Экспликация помещения				
№	Примечание	Площадь м ²		
1	Холл	15,07		
2	Санузел	3,73		
3	Санузел	4,17		
4	Спальня	14,33		
5	Гостиная	17,4		
6	Кухня	10,9		
7	Балкон	3,17		
Общая площадь		68,0		
Условные обозначения:				
	Существующие стены			
	Вент шахта			
				
Н	Высота потолка			
Н _п	Высота подоконника			
Н _{ок}	Высота окна			
Н _{д.пр}	Высота дверного проема			
Дизайн - проект квартиры расположенной по адресу г.Астана А32 д13/1 кв-33		Стадия РП	Лист 2	Листов
План схема - обмерный план				

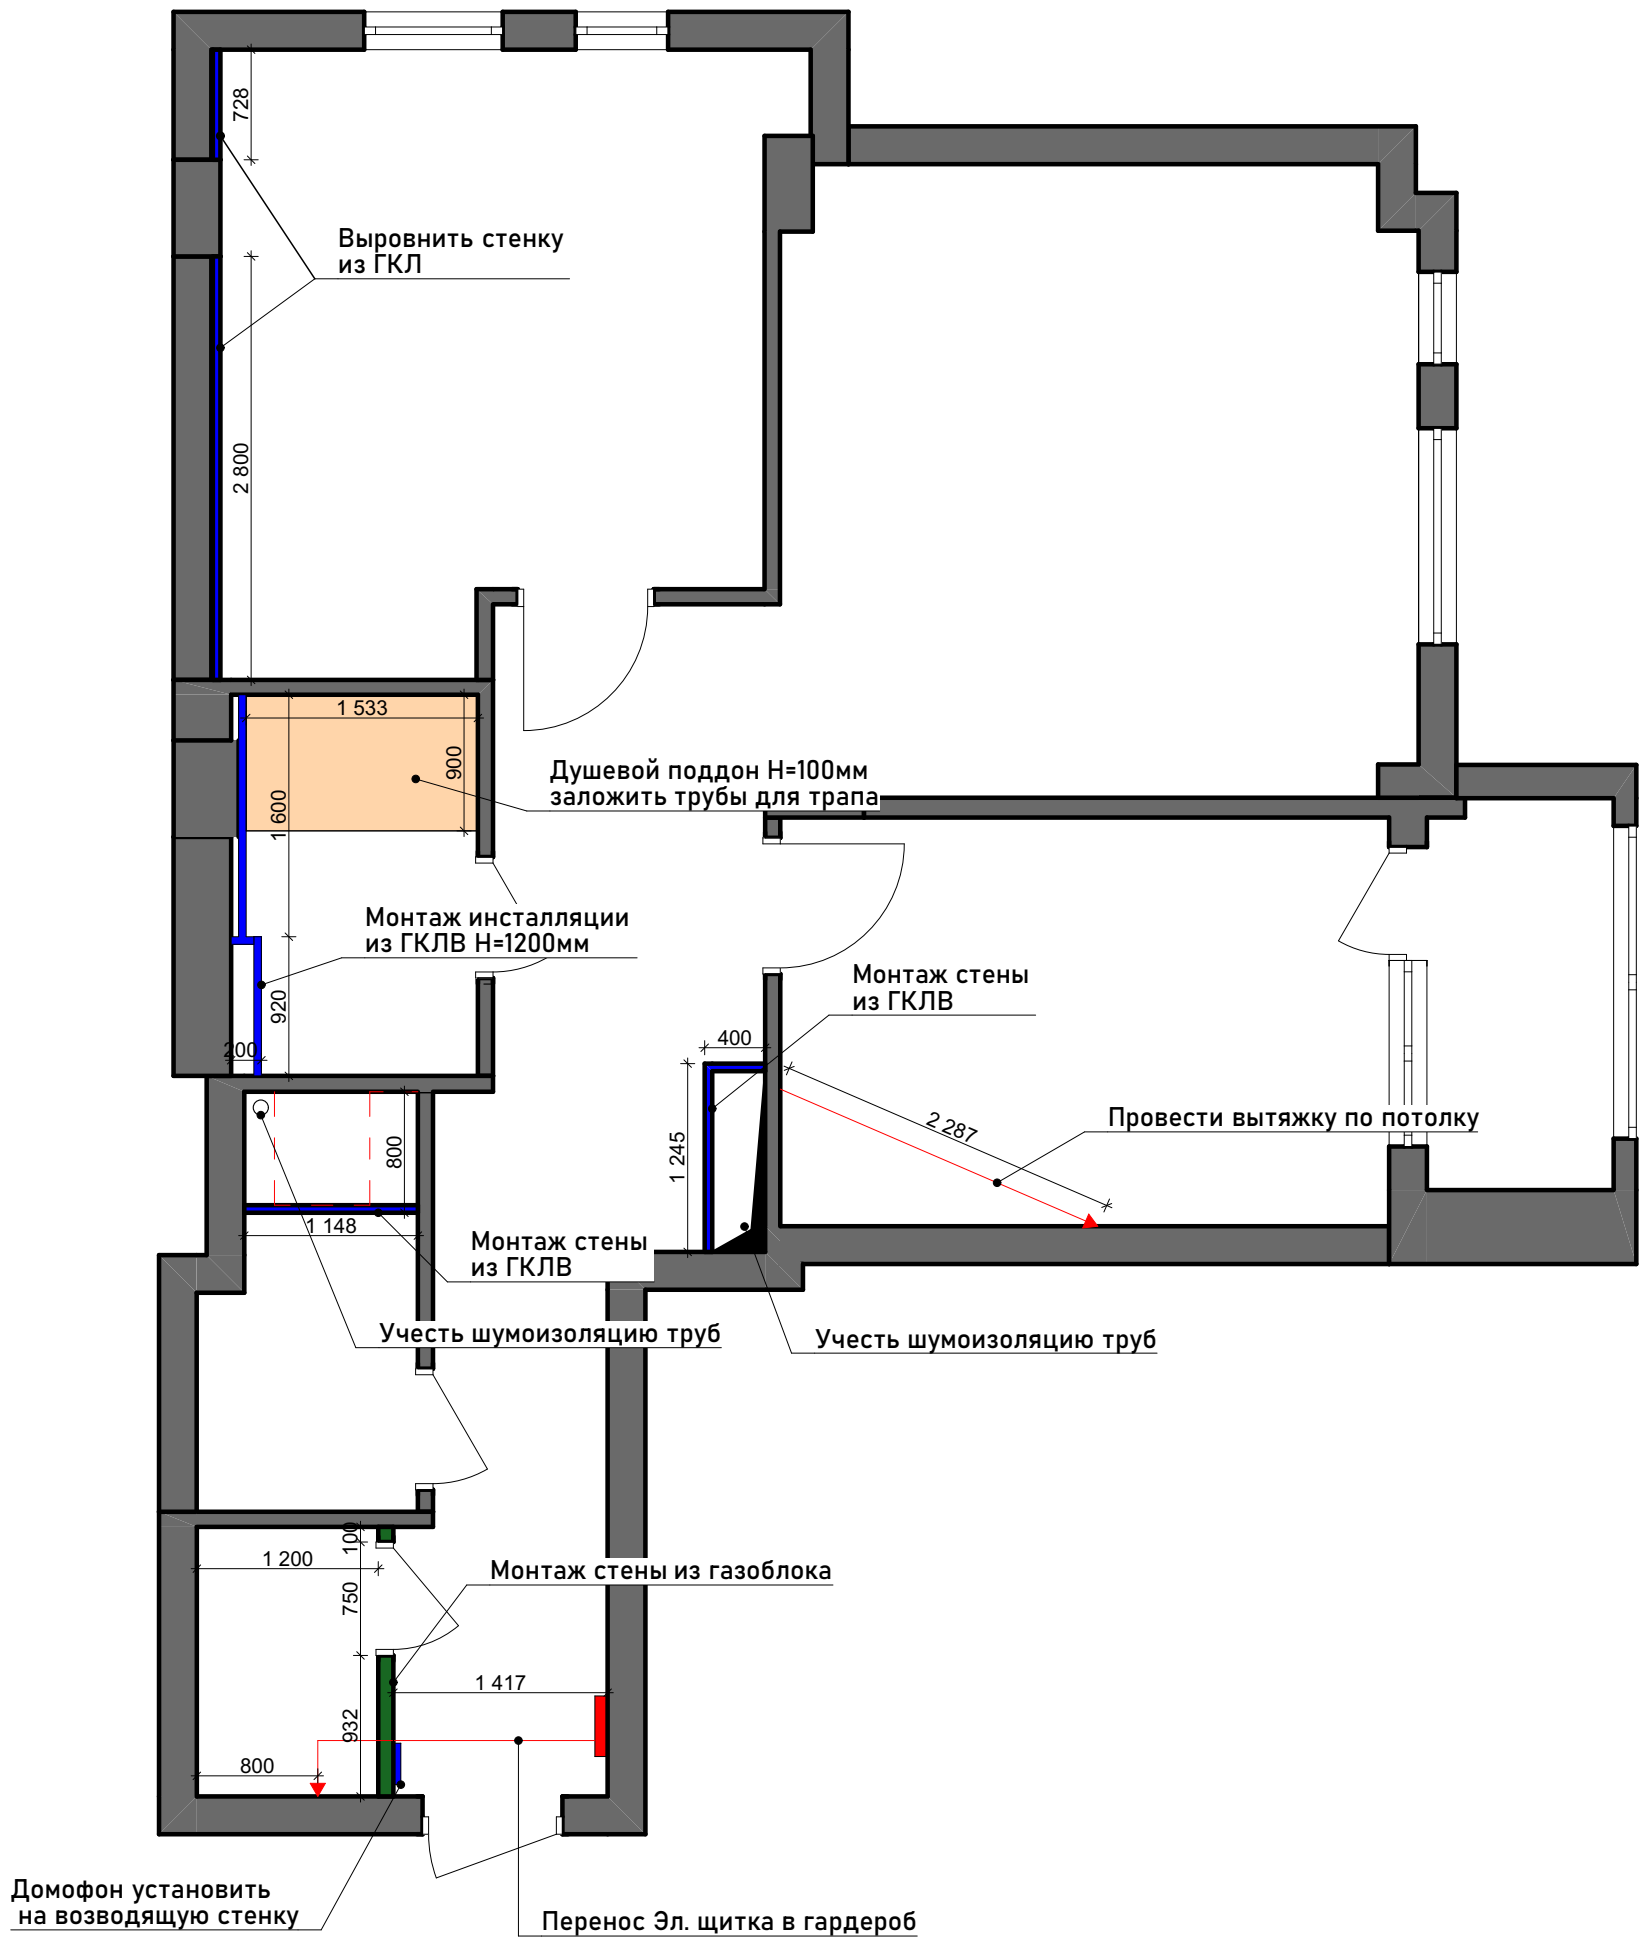

Ведомость монтажа			
	Монтаж стены из ГКЛ		
	Монтаж стены из ГКЛВ		
	Монтаж стены из газоблока		
Примечание: * Вывернить полы по всей квартирев один уровень. Материал уточнить по месту. * Утепления лоджии. * Предусмотреть ДИФФУЗОР для вентиляции в санузле, Расположение уточнить по месту , согласовать с клиентом! * Все размеры даны в миллиметрах. Геометрия стен нарушена, необходимо учитывать возможные погрешности в проектных и реальных размерах, (несоответствия размеров по проекту согласовать с дизайнером).			
Дизайн - проект квартиры расположенной по адресу г.Астана А32 д13/1 кв-33	Стадия	Лист	Листов
	РП	3	
План схема - монтаж стен			

Прикроватная тумба

Стеллаж с полками

Туалетный столик


Прикроватная тумба

Подвесная ТВ тумба


Марозильная камера

Зеркало

Подвесная тумба

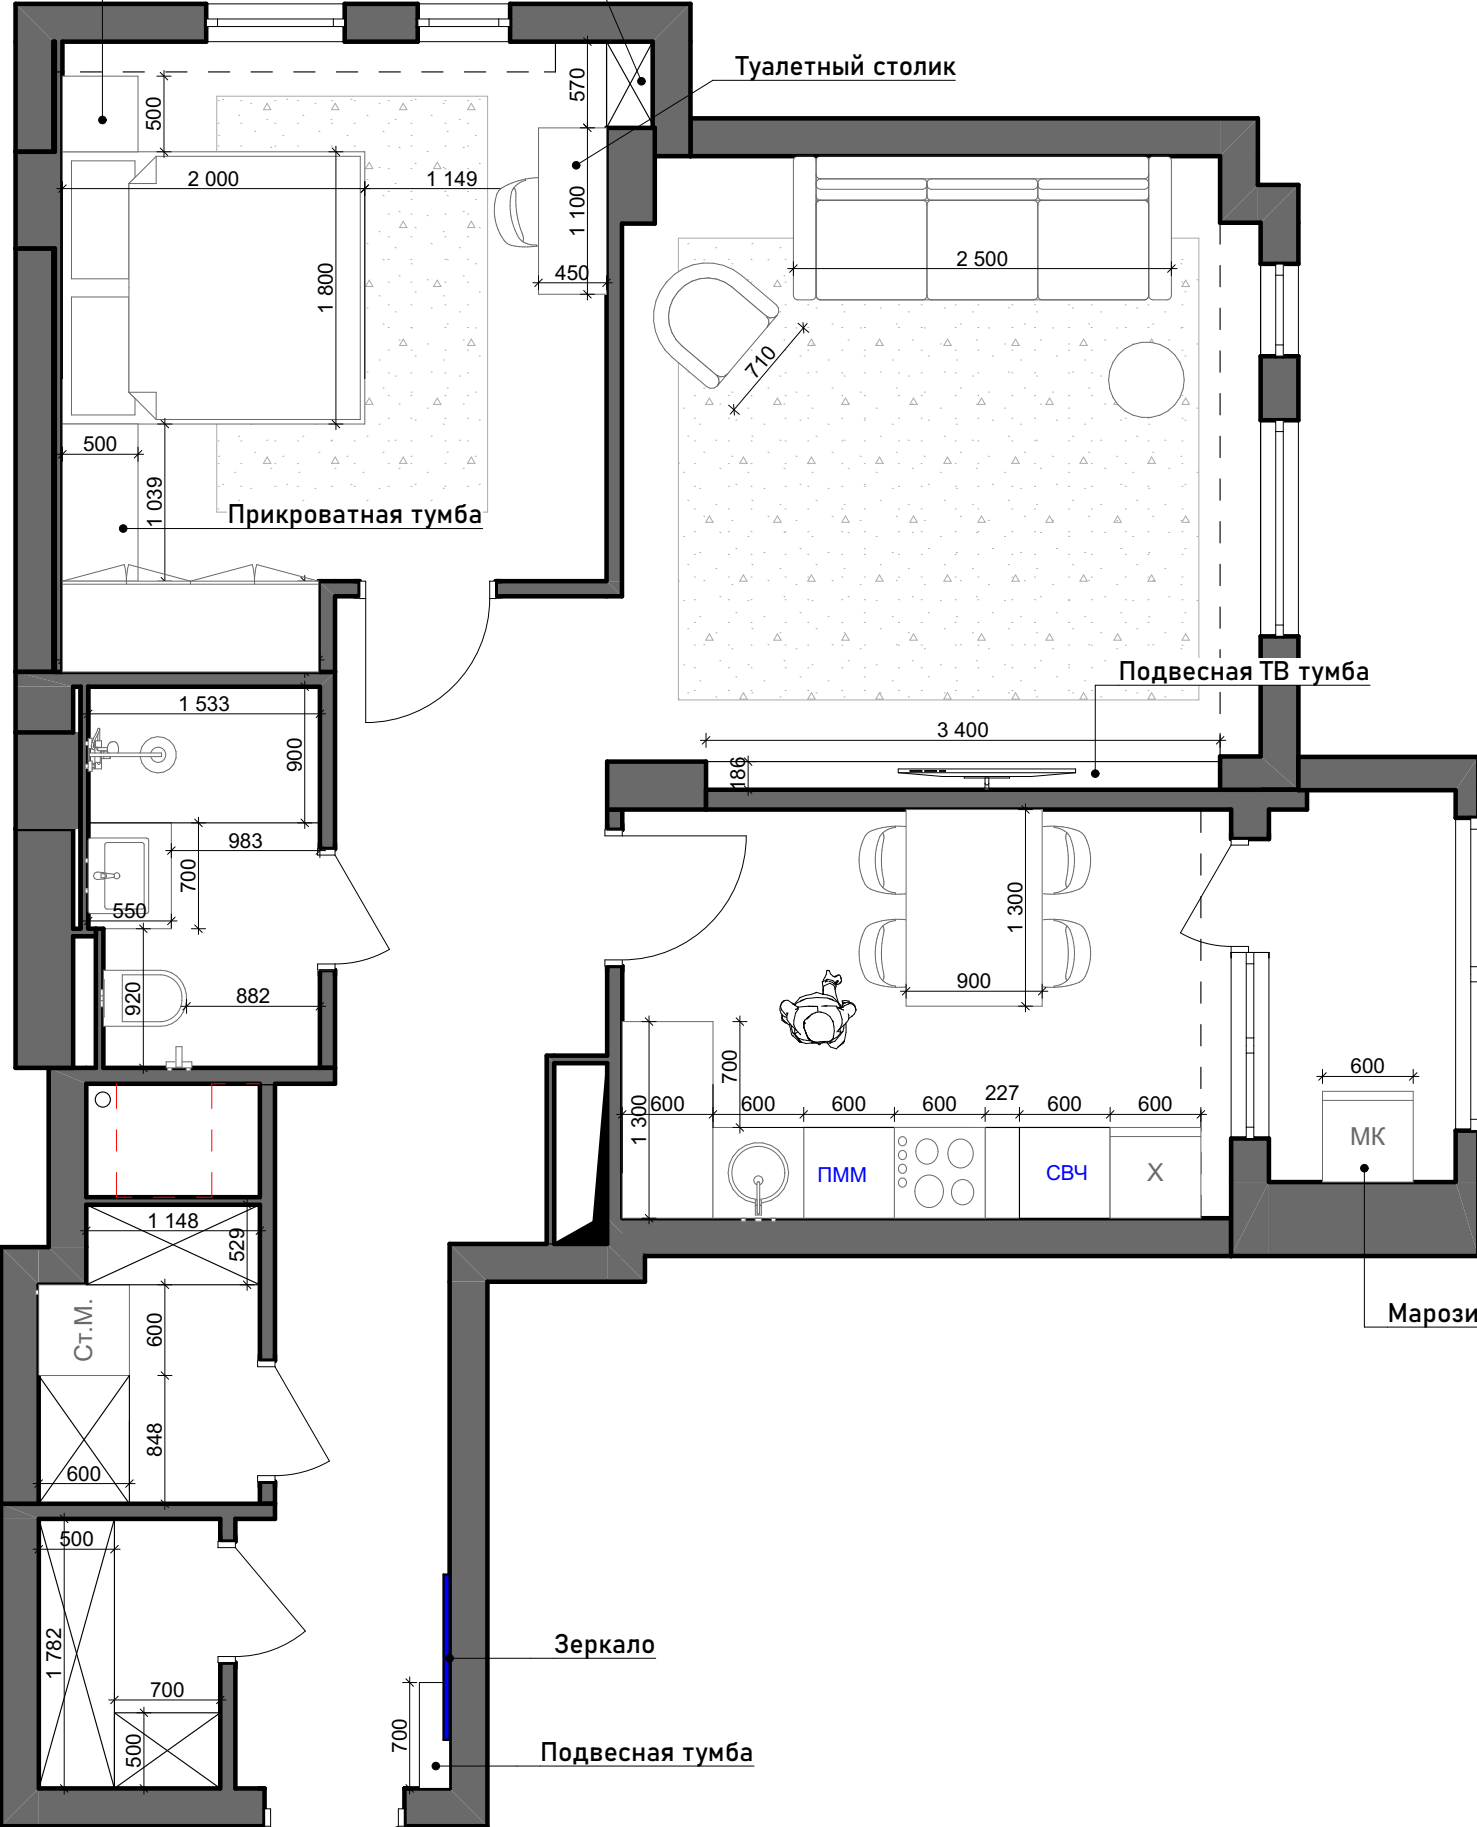

Дизайн - проект квартиры расположенной по адресу г. Астана А32 д13/1 кв-33	Стадия	Лист	Листов
	РП	4	

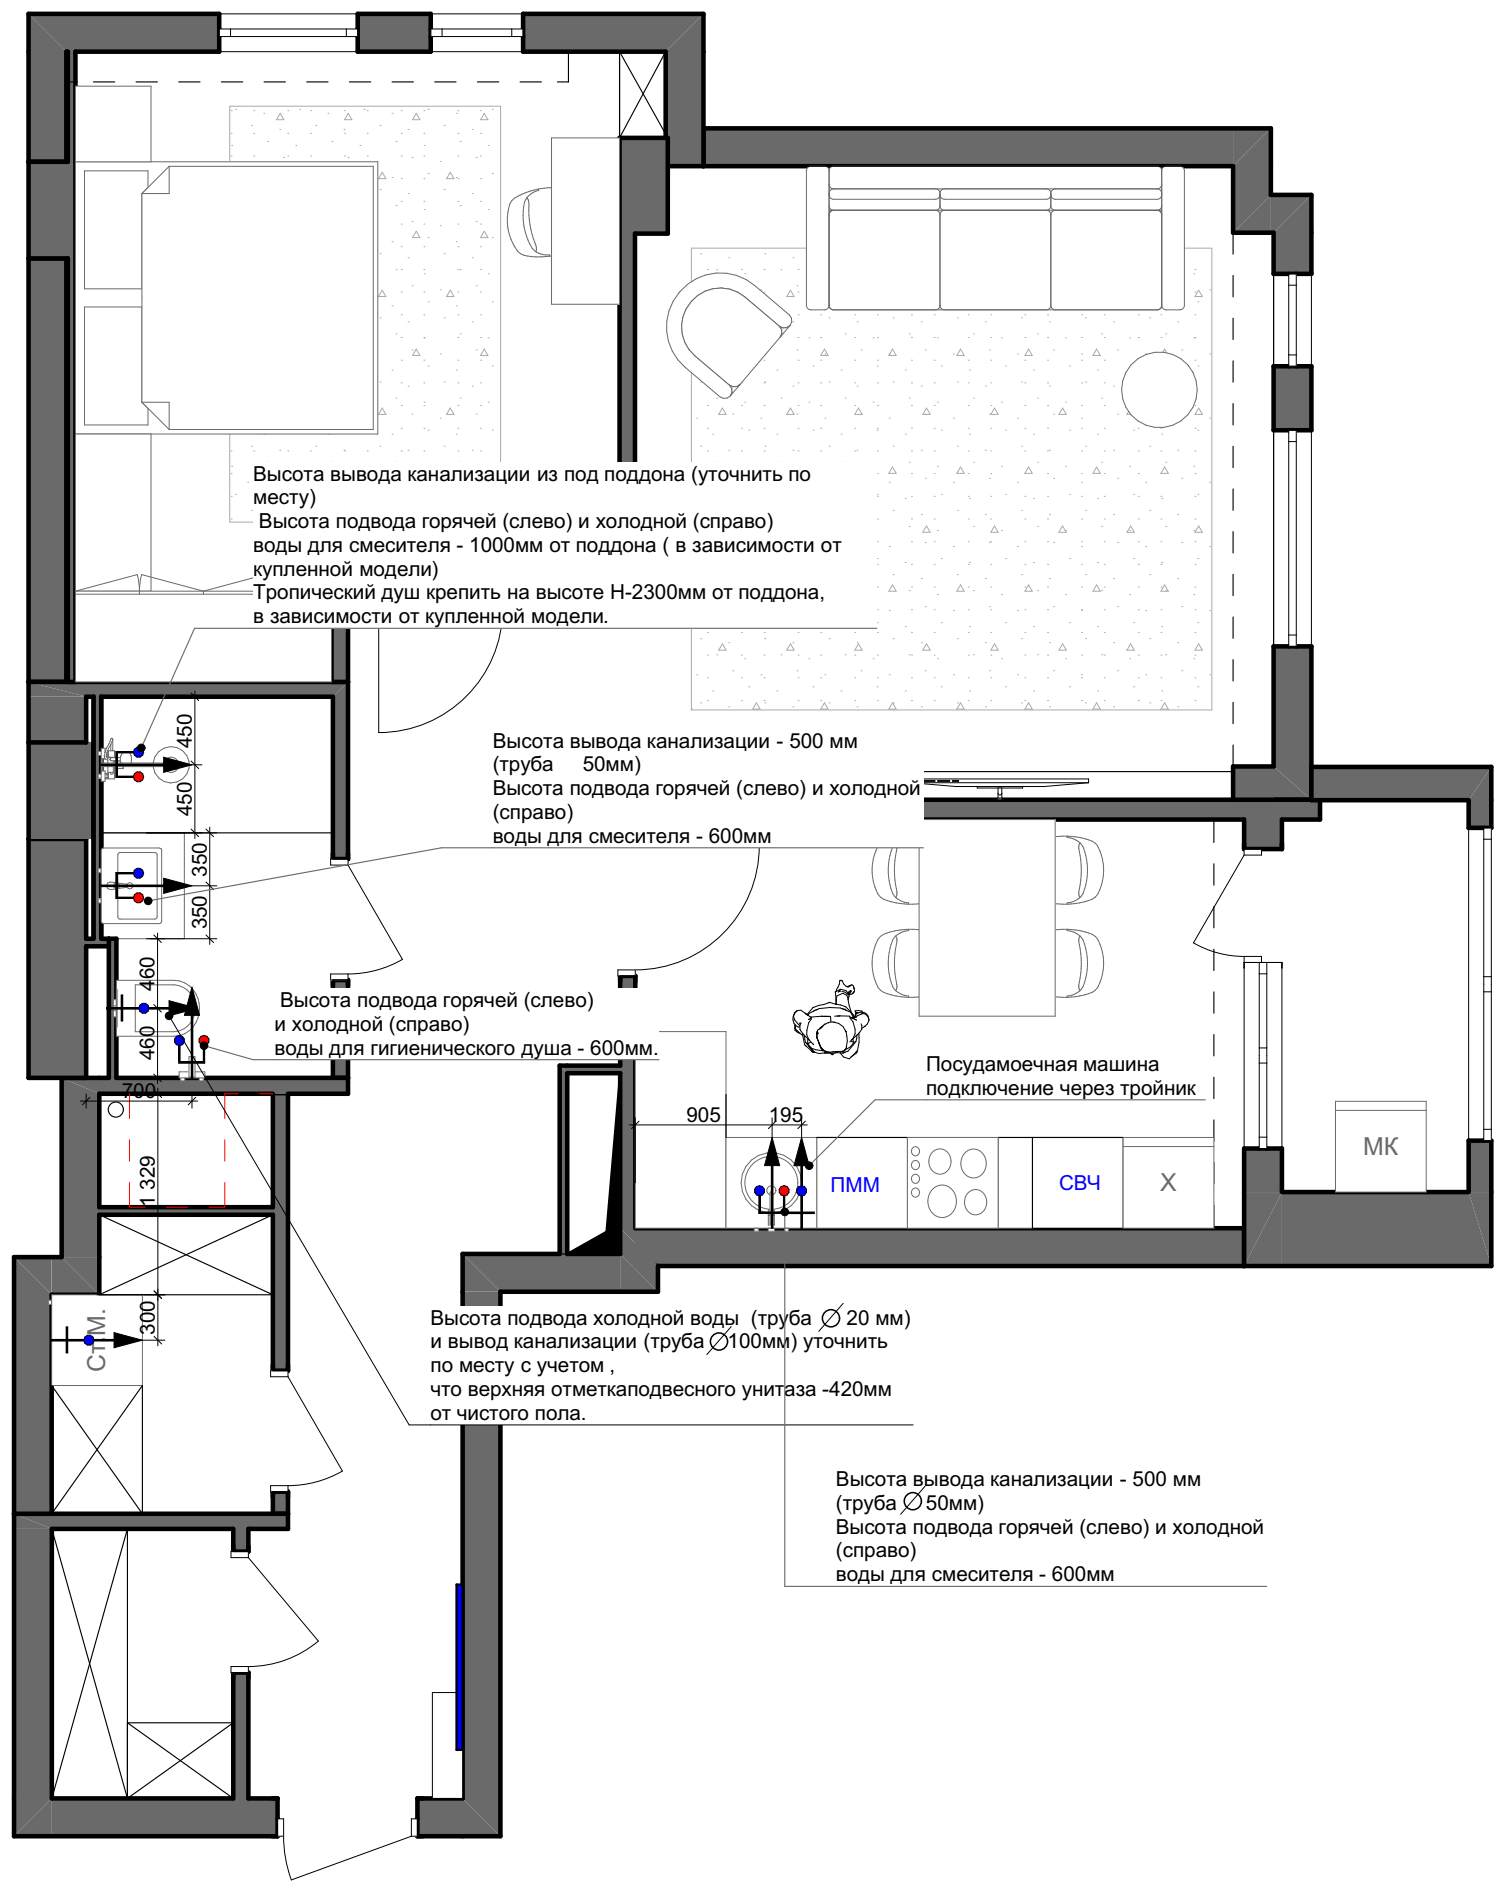

ПРИМЕЧАНИЕ :


- * Предусмотреть установку люков в зависимости от расположения счетчиков
- * Предусмотреть люк для ванны
- * Размеры планировочного решения могут измениться после возведения перегородок.
- * В связи с этим уточнить размеры для всей встраиваемой мебели.
- * Все высоты даны от чистого пола до оси трубы .
- * Высоту выводов воды для унитаза смотреть в технических характеристиках производителя инсталляции для подвесного унитаза.
- * Высоты и привязки указаны от чистой штукатурки;
- * Произвести монтаж всех труб в стене;

Условные обозначения:

- Вывод холодной воды под сантех. приборы
- Вывод холодной и горячей воды под сантех. приборы
- Выпуск канализации под сантех. приборы ($\varnothing$ = 50мм, $\varnothing$ 110мм. для унитаза)

Дизайн - проект квартиры расположенной по адресу г. Астана А32 д13/1 кв-33	Стадия	Лист	Листов
	РП	5	

План схема - сантехнических
приборов

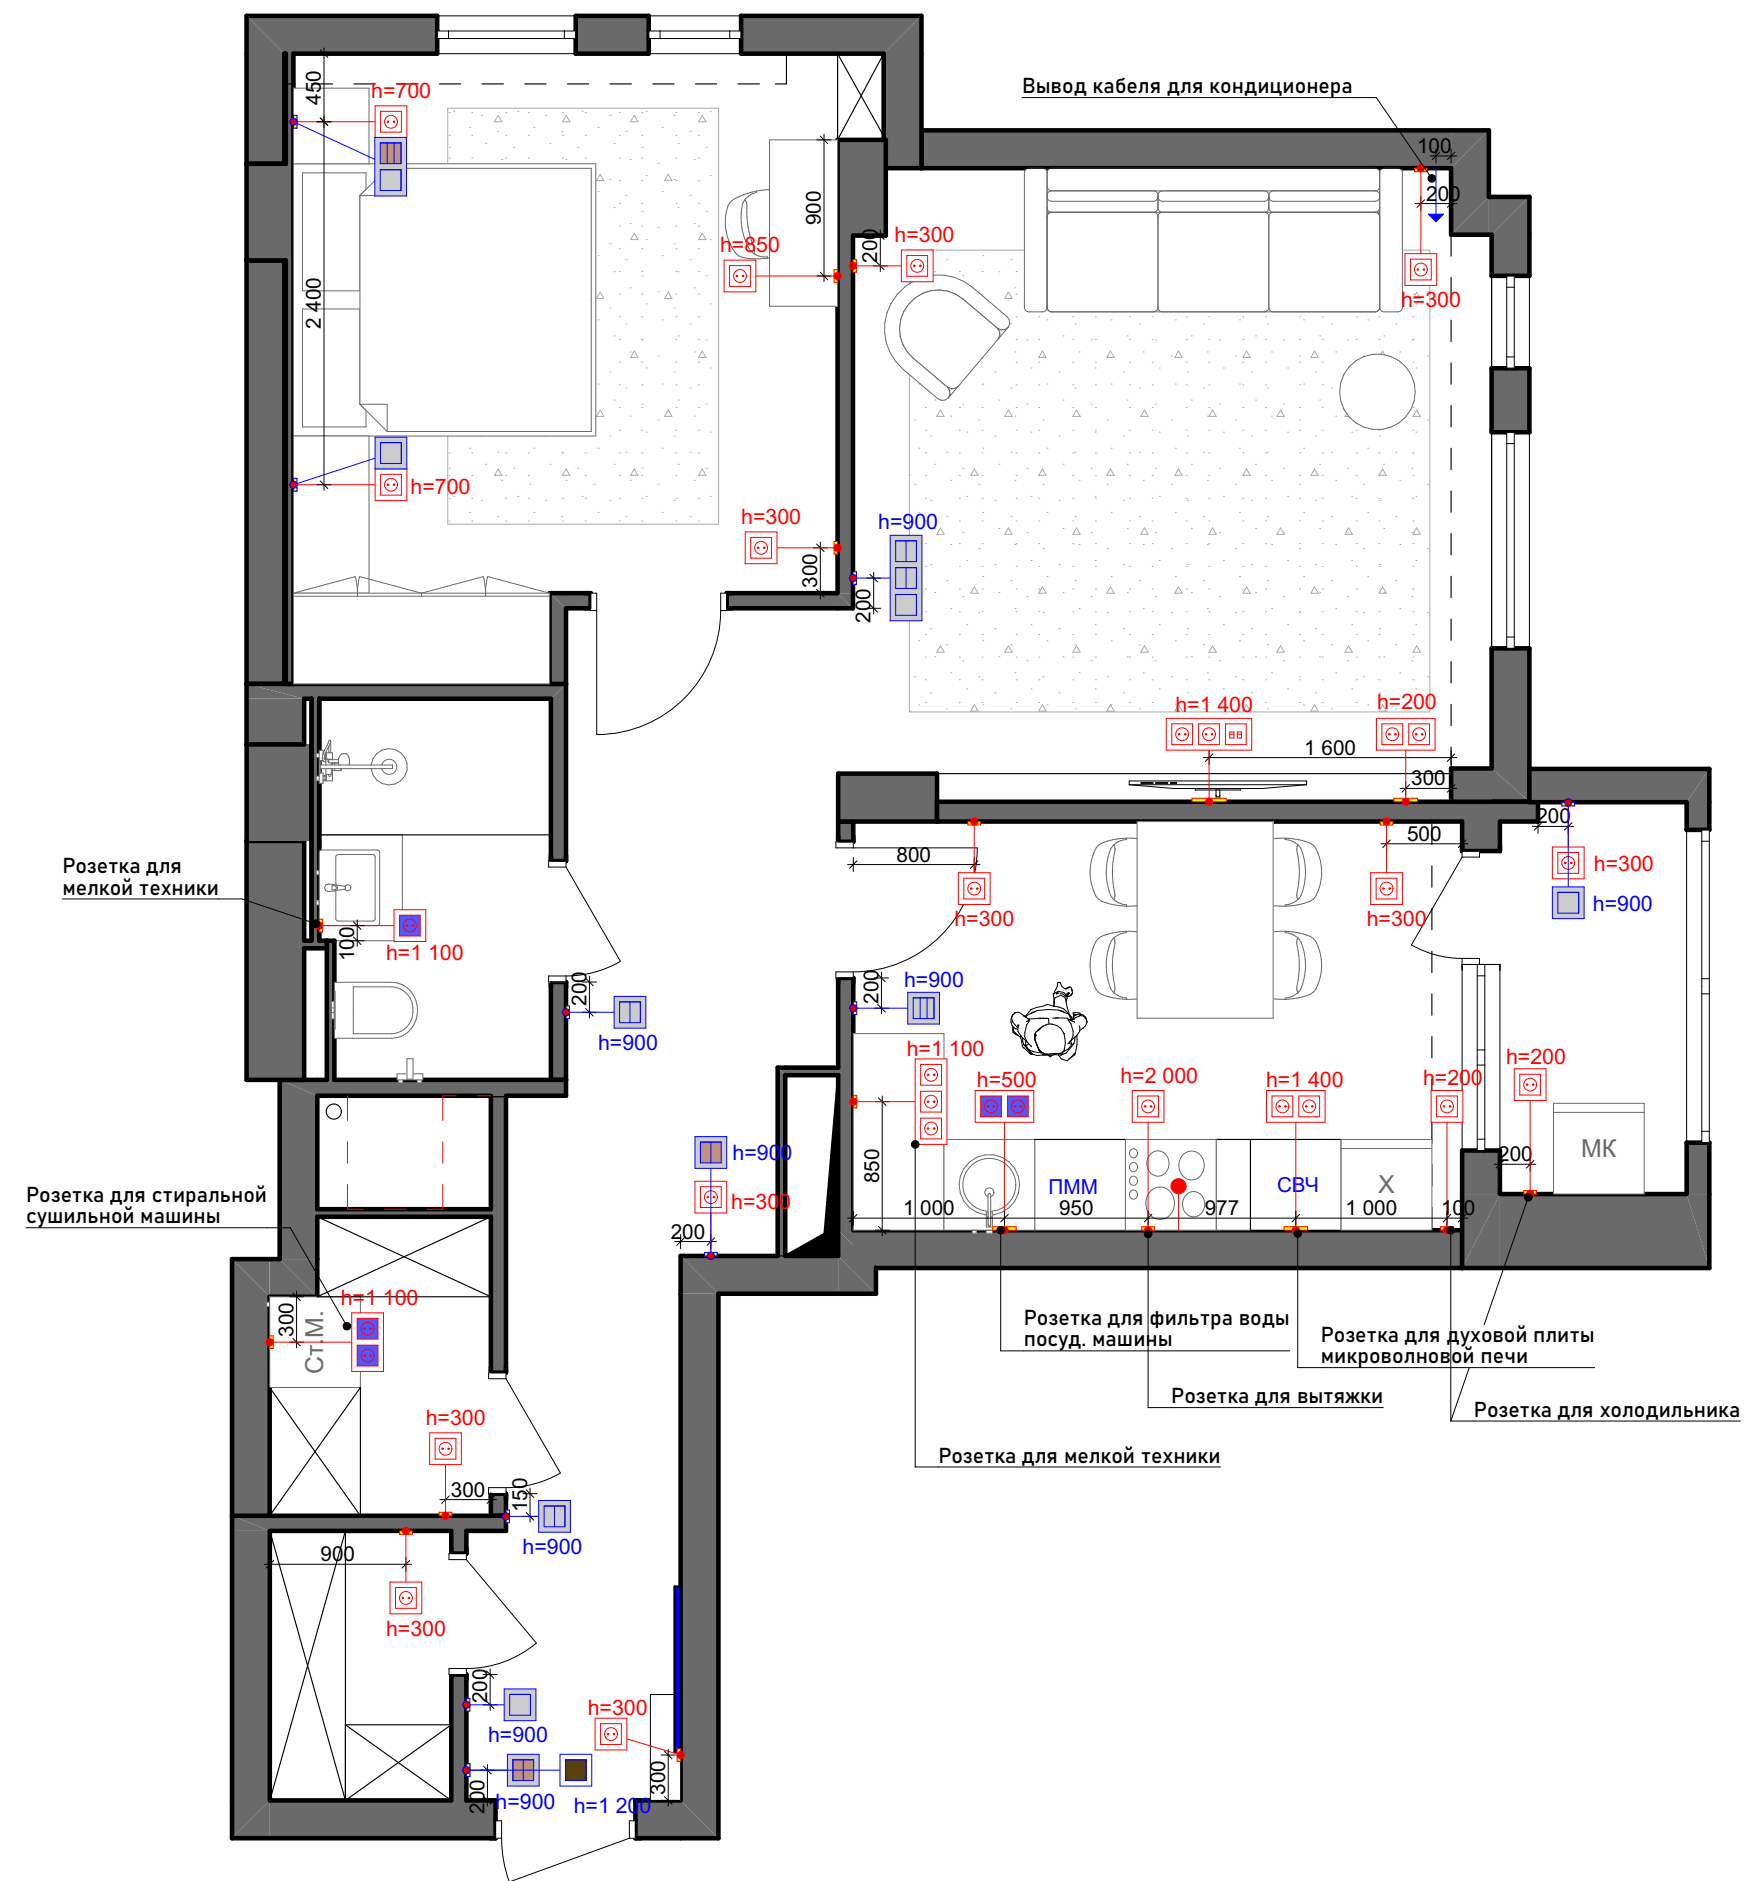



Условные обозначения розеток			
1	Рамка для розеток 1 постовой	23	
2	Рамка для розеток 2 постовой	4	
3	Рамка для розеток 3 постовой	4	

ПРИМЕЧАНИЕ :

- * Читать совместно с планами осветительных приборов, расстановки выключателей и схемой подключения, электрических розеток и выключателей.
- * Место расположения WI-FI роутера и усилителя уточнить по месту .
- * Все слаботочные провода скоммуницировать в слаботочном щите.
- * Расположение электро и сантех выводов кухни уточнить по тех. картам поставщика оборудования.
- * Для стиральной машины, холодильника, кондиционера, духовки выводить отдельные кабеля
- * **Высота розеток указана от пола и до середины розетки.**


Условные обозначения розеток		
Вид	Позиция 1	Кол-во
	Розетки 220V	25 шт
	Интернет розетка 220 V	1 шт
	Влагостойкая розетка IP 44	5 шт
	Питание для кондиционера	

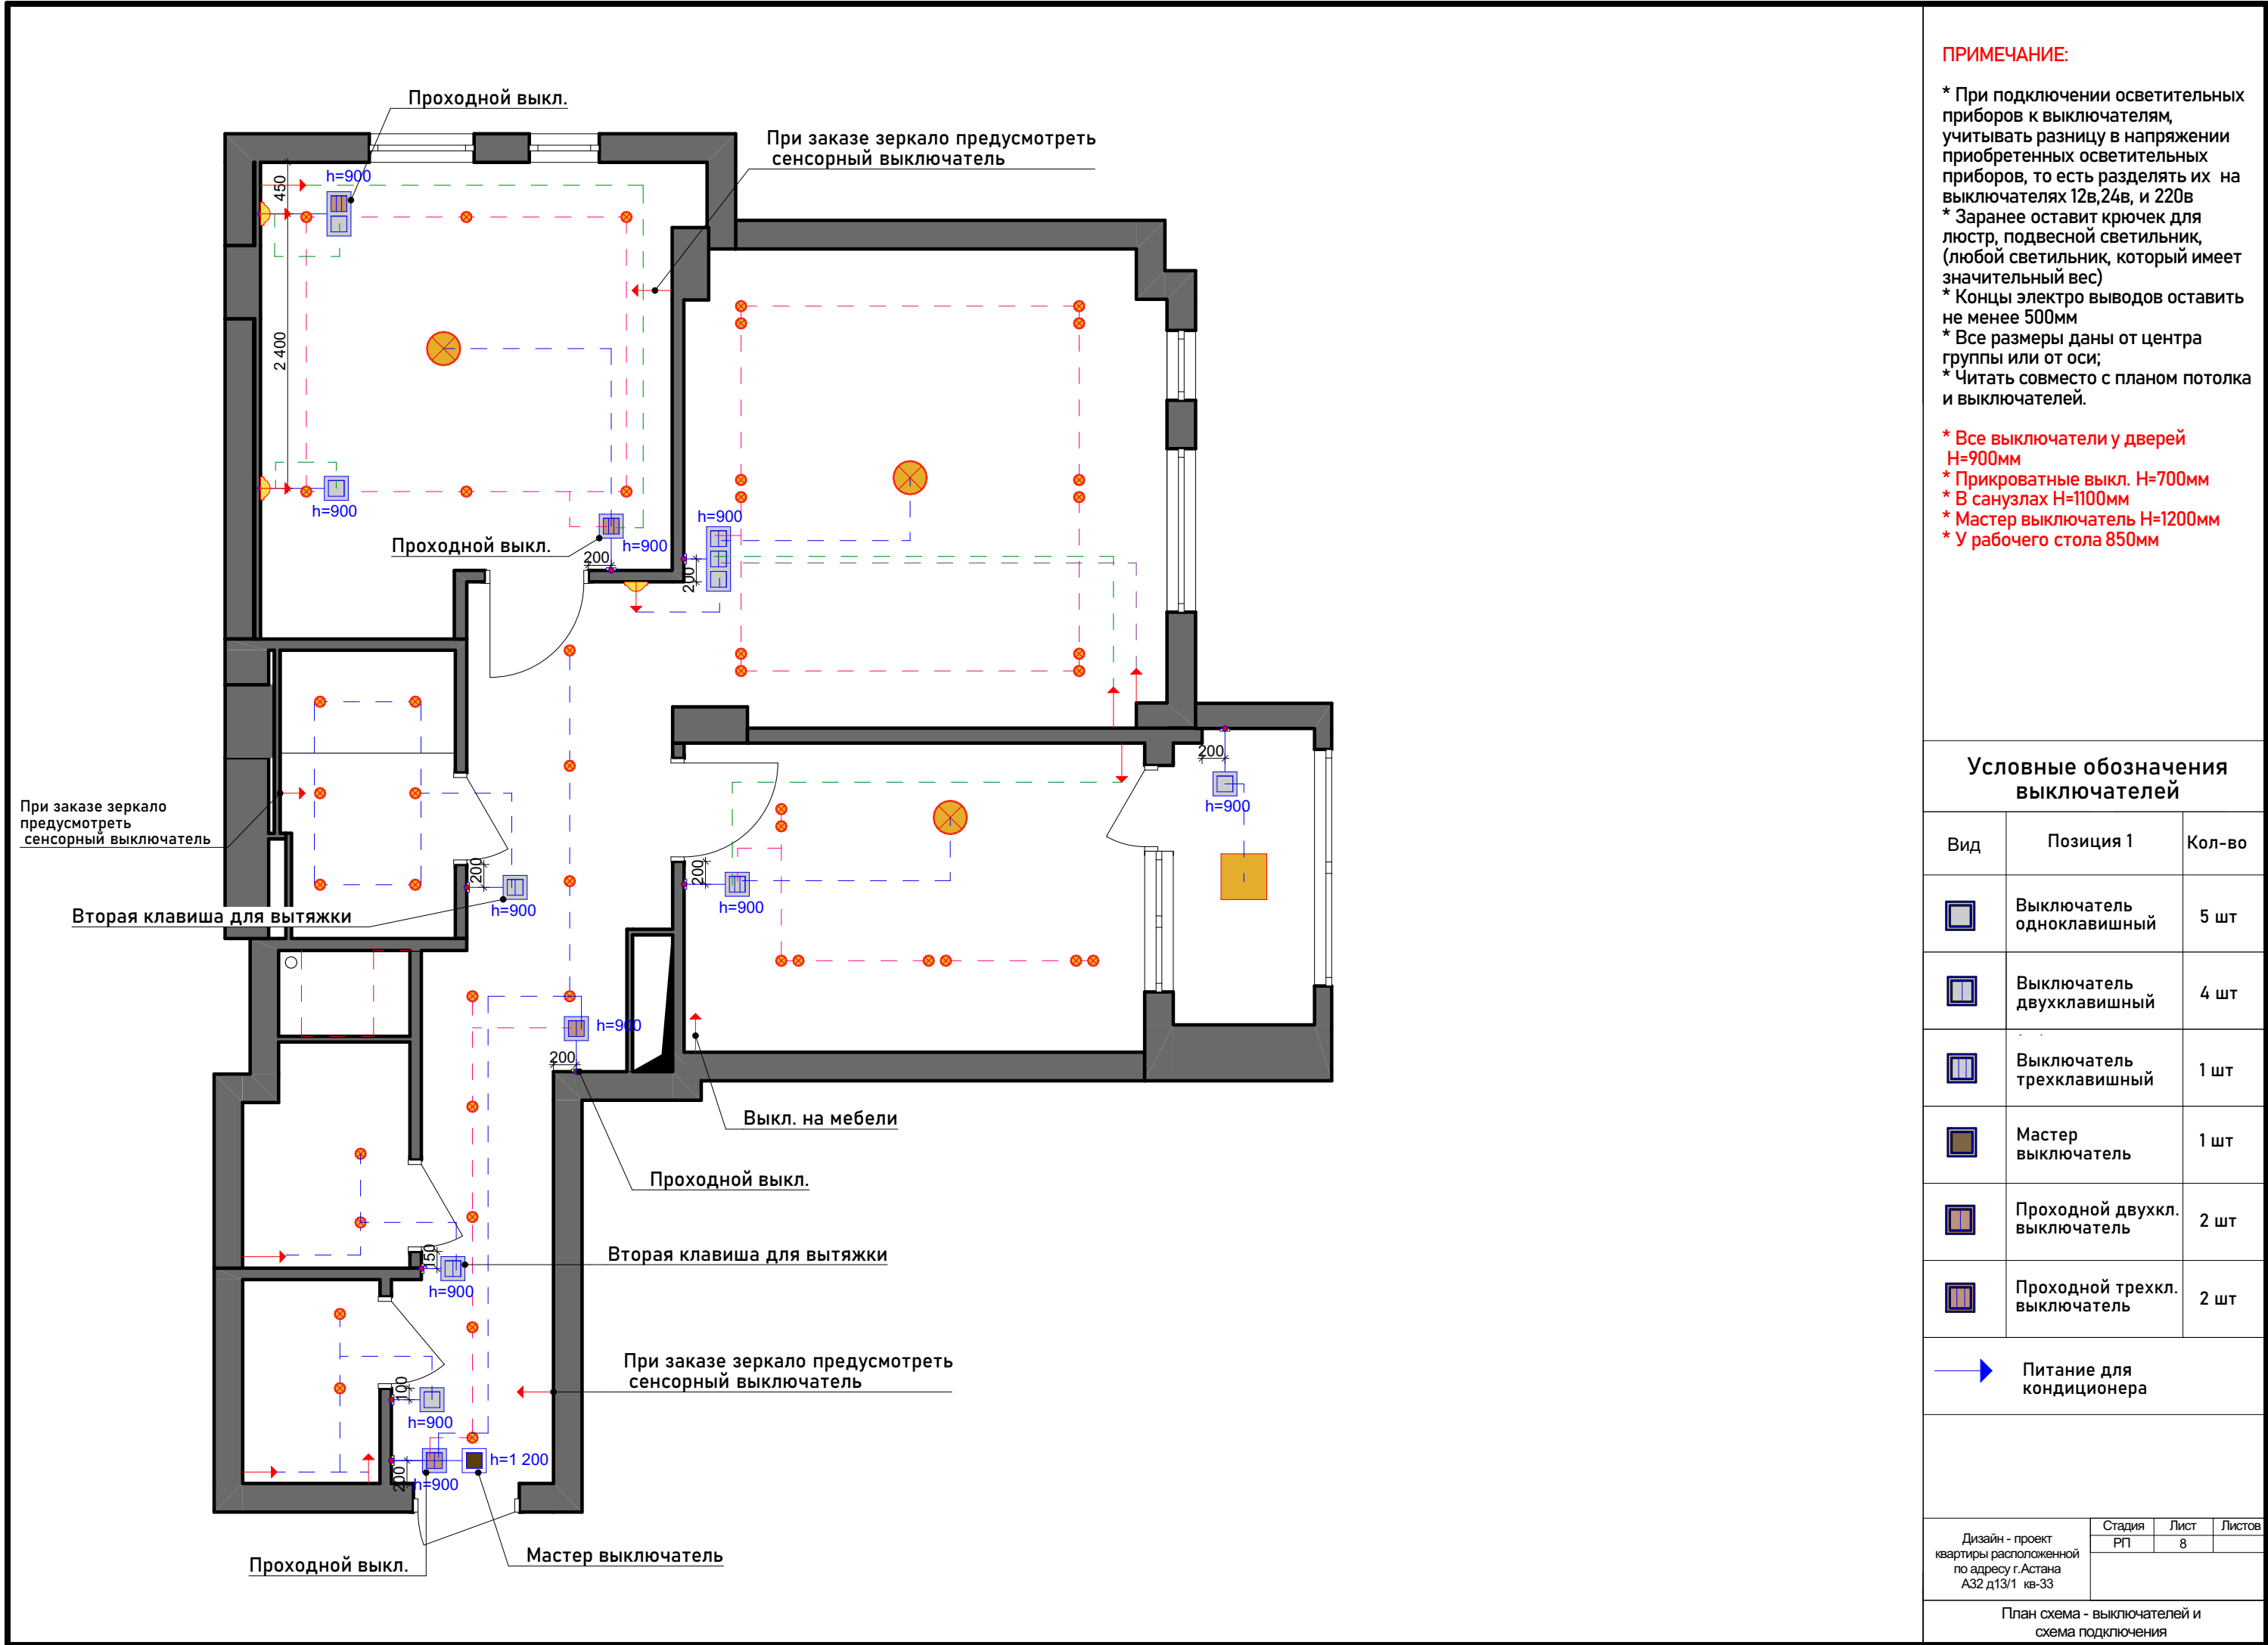

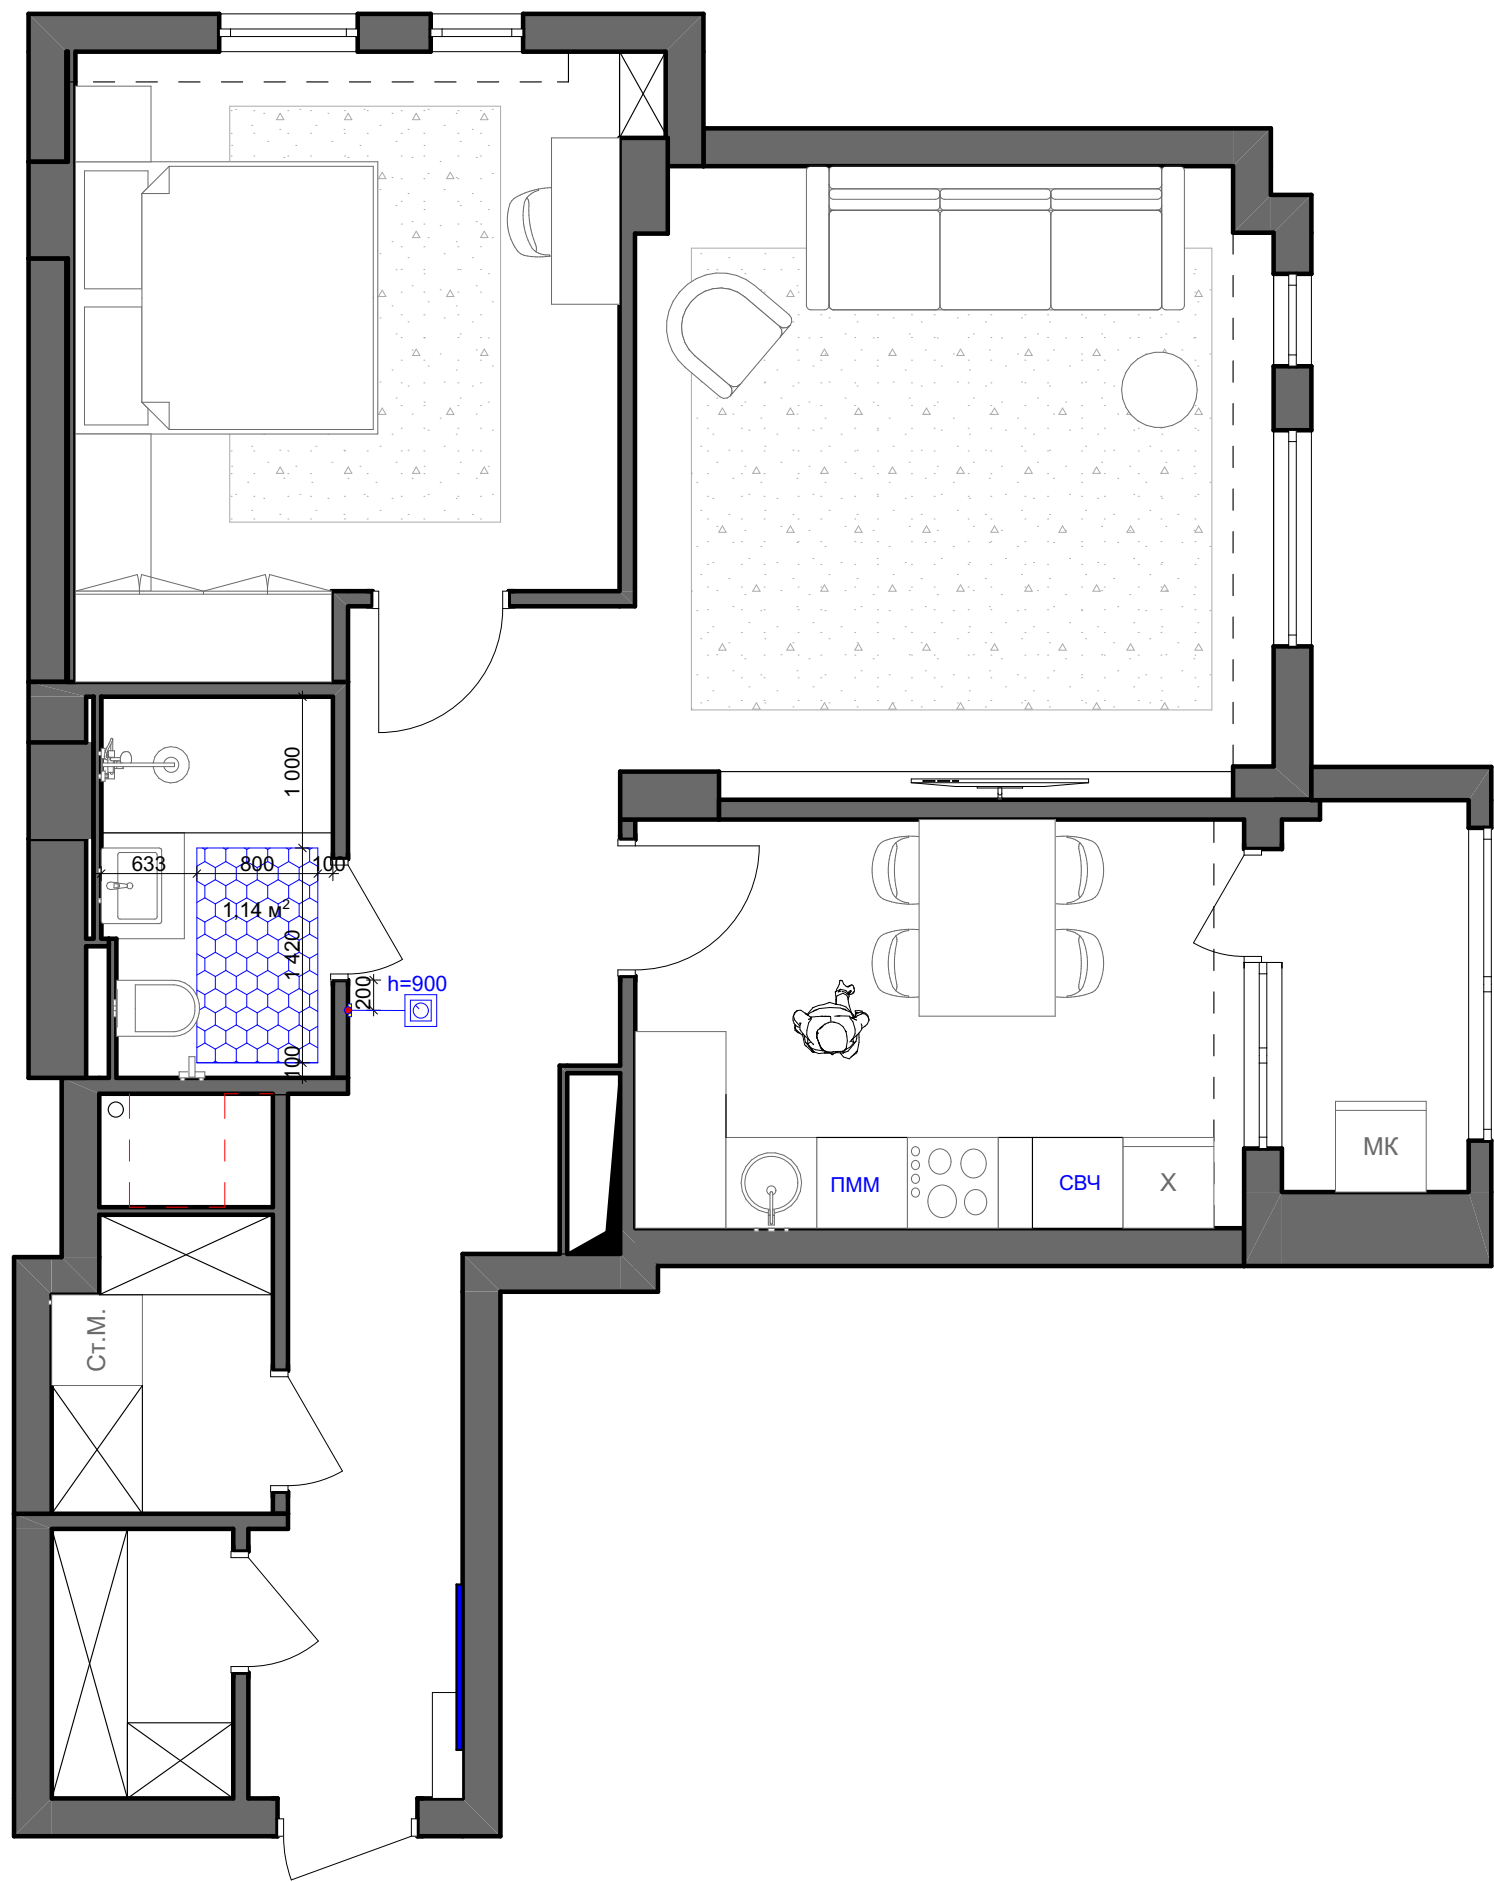

ПРИМЕЧАНИЕ:

- * Размещение Теплого пола отступ 100мм от мебели и стен.
- * Высота терморегулятора Н=300мм от уровня чистого пола.
- Согласовать с клиентом!

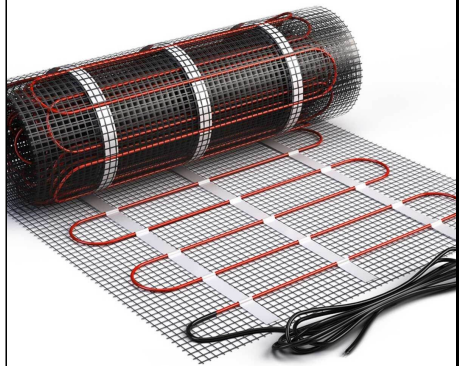

Ведомость монтажа

1	Теплый пол - санузлы, холл	1,14 м²	
2	Терморегулятор	1 шт	

Дизайн - проект квартиры расположенной по адресу г. Астана А32 д13/1 кв-33	Стадия	Лист	Листов
	РП	9	



ПРИМЕЧАНИЕ:

*Уровень потолков даны от
чернового пола


* Погонный метр профиля для
парящего потолка и теневого даны
без учета запаса!

Вытяжка потолочная



Ведомость монтажа


	Натяжной матовый потолок - уровень потолка - 0,100мм	59,0 м²
	Левкас уровень потолка -0,000	7,52 м²
	Галтели 10см	86,0 п.м

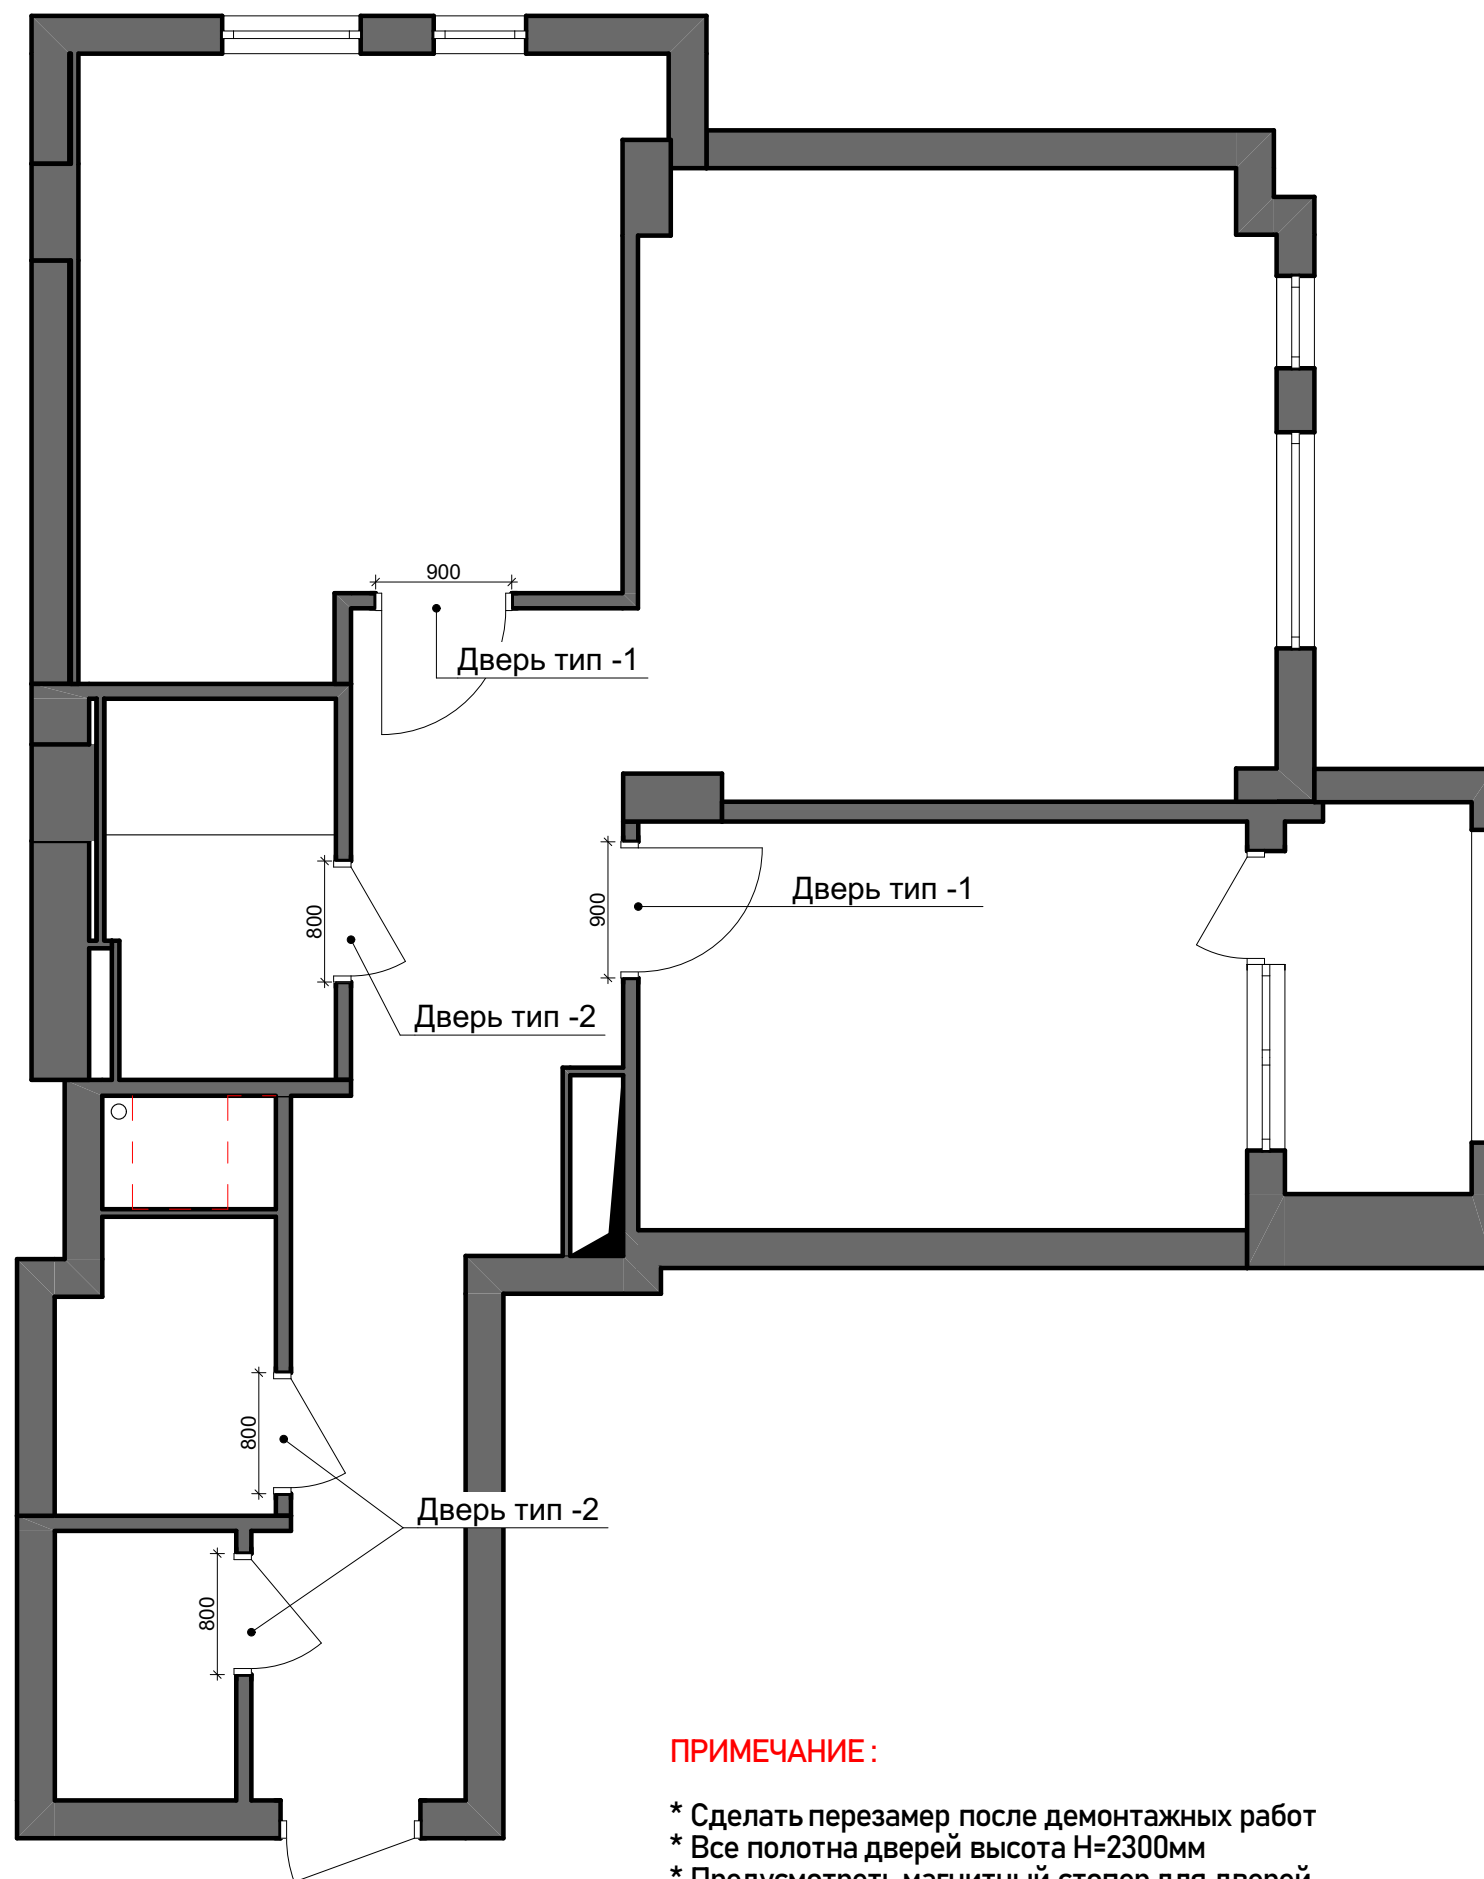






ПРИМЕЧАНИЕ :

- * Сделать переизмер после демонтажных работ
- * Все полотна дверей высота Н=2300мм
- * Предусмотреть магнитный стопер для дверей
- * Точное количество доборов и наличников и их размеры определяется замерщиком от магазина - продавца дверей:

Спецификация дверных проемов				
№ п/п	Размер проема	Размер полотна	Примечание	Кол-во
ДП-1	900-2400	800-2300	Толщина стены = 120мм	2
ДП-2	800-2400	700-2300	Толщина стены = 120мм	3

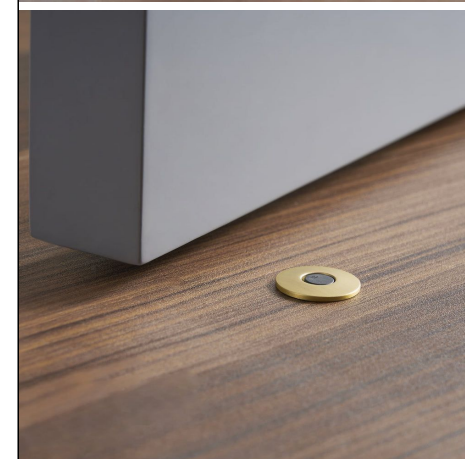

Дизайн - проект квартиры расположенной по адресу г.Астана А32 д13/1 кв-33	Стадия	Лист	Листов
	РП	12	

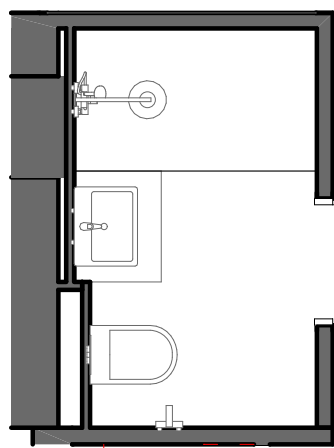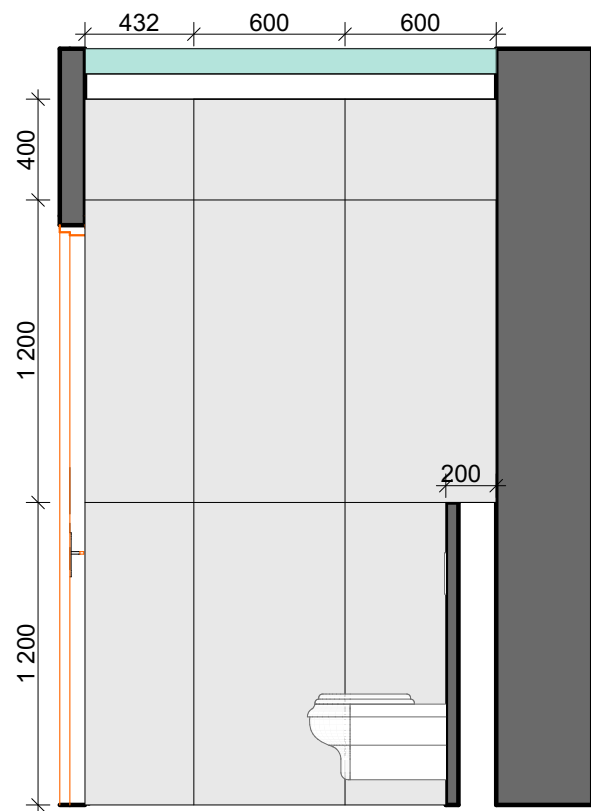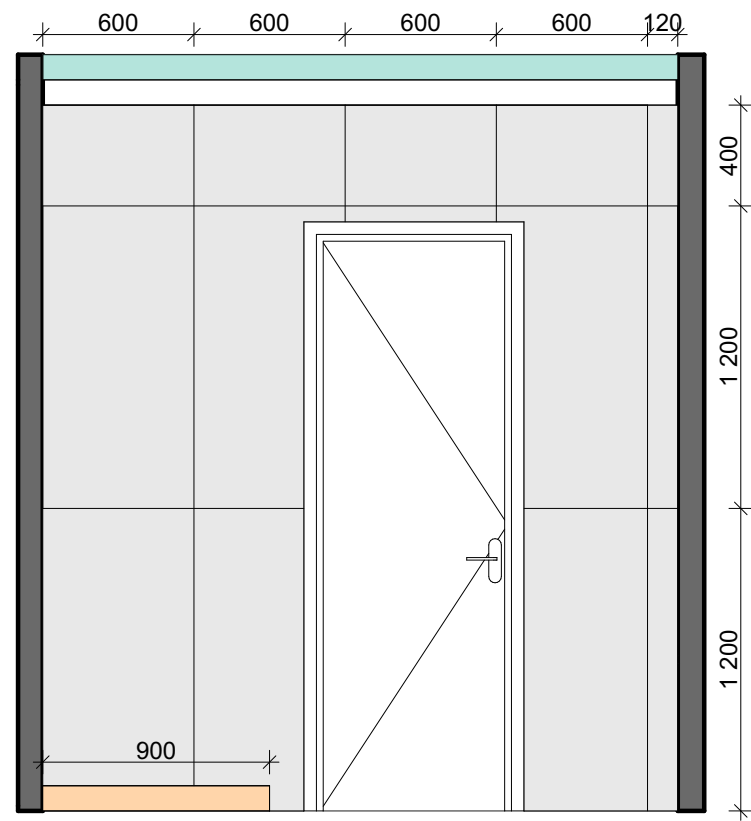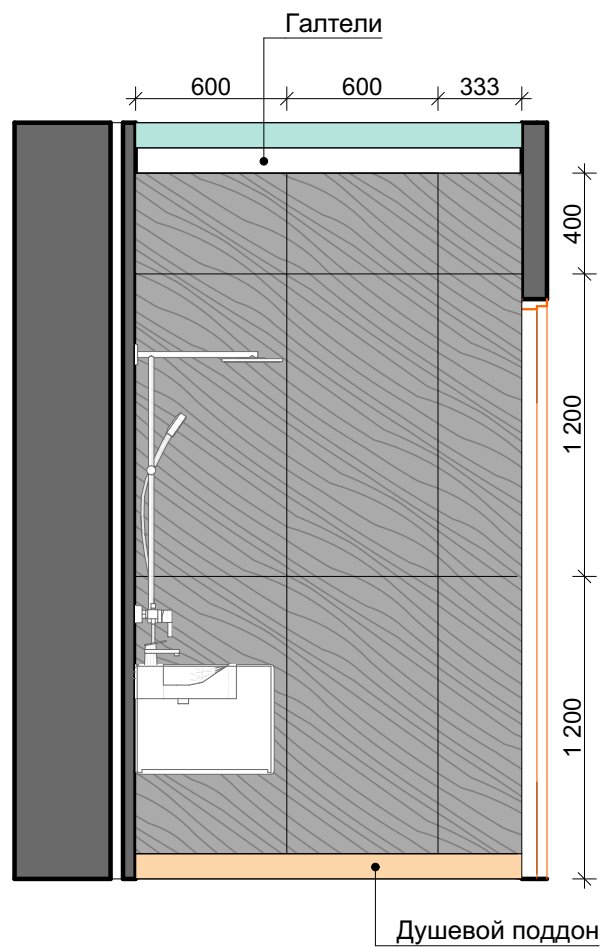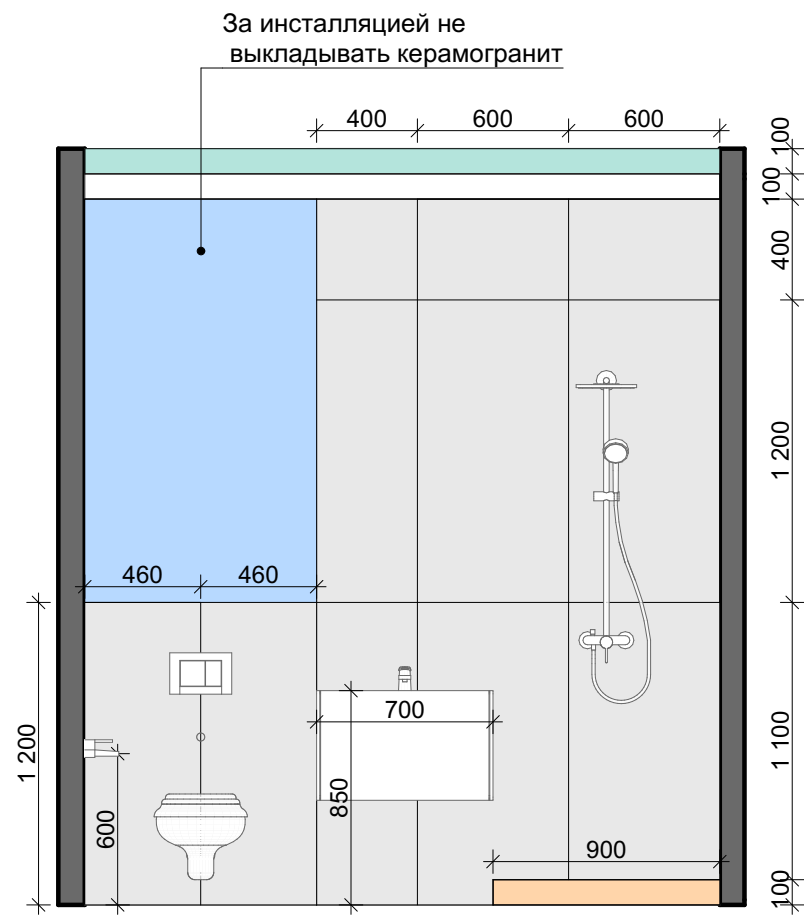



Условные обозначения
отделочных материалов

	Керамогранит 120 x 60	15,0 м²
	Керамогранит 120 x 60 акцентная	4,14 м²

Отделочные материалы
посчитаны без учета
запаса!


Дизайн - проект квартиры расположенной по адресу г. Астана А32 д13/1 кв-33	Стадия	Лист	Листов
	РП	13	

Развертка стен санузла

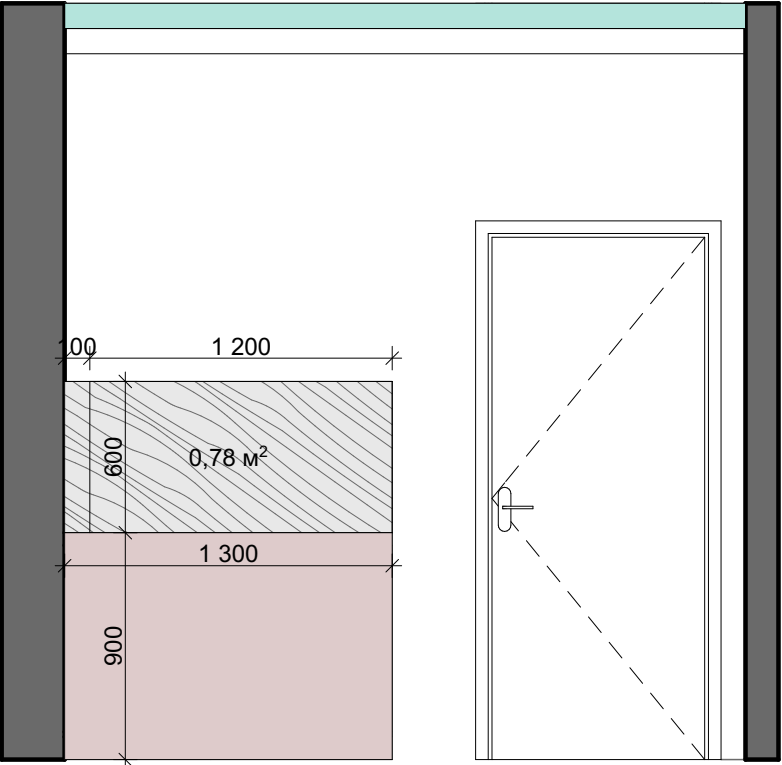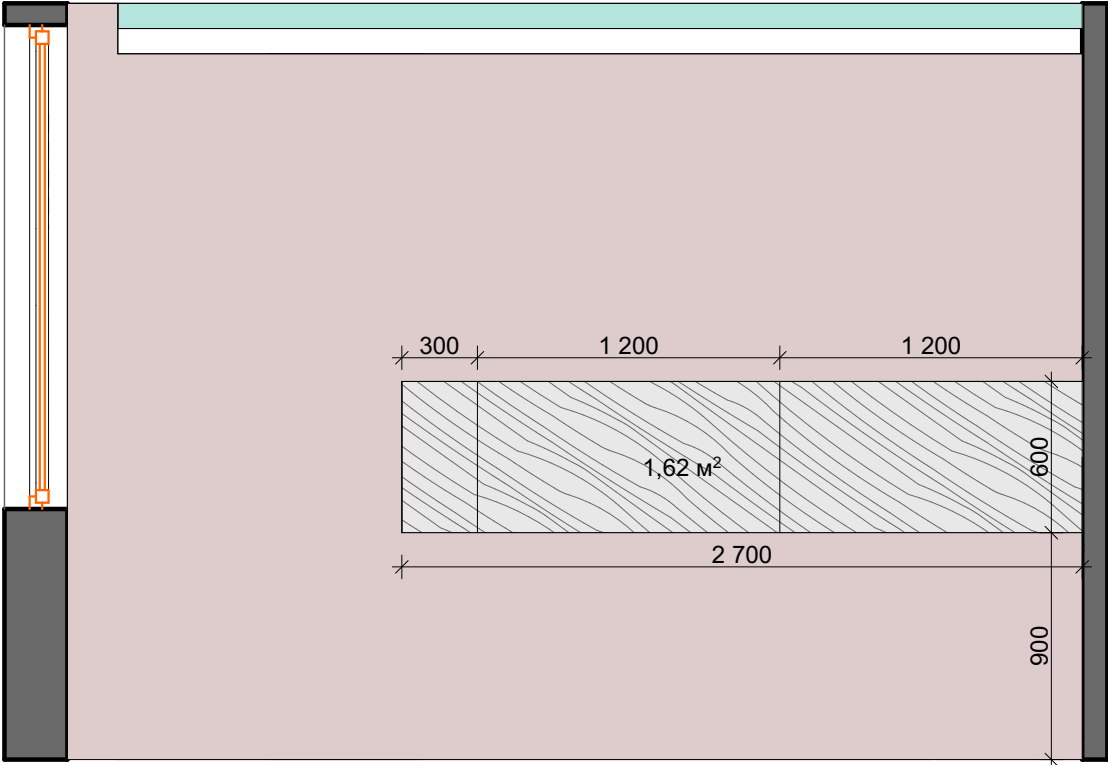

Условные обозначения отделочных материалов		
	Краска за гарнитуром не дорогая	10,87 м²
	Фартук	2,4 м²

Отделочные материалы посчитаны без учета запаса!




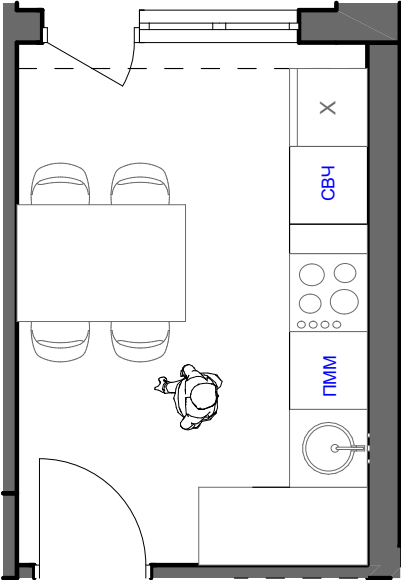


Дизайн - проект квартиры расположенной по адресу г. Астана А32 д13/1 кв-33	Стадия	Лист	Листов
	РП	14	

Развертка стен кухни

Спецификация рамок			
1	Рамка для розеток 1 постовой	23	
2	Рамка для розеток 2 постовой	4	
3	Рамка для розеток 3 постовой	4	

Спецификация осветительных приборов			
1	Вывод кабеля		
2	LED лента	уточнить по месту	
Спецификация осветительных приборов			
1	Люстра	4 шт	
2	Сафиты	45 шт	
3	Настенная бра	3 шт	

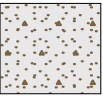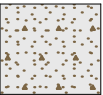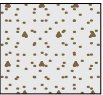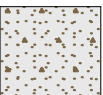
Спецификация напольных покрытий			
1	Пол тип - 1. Ламинат укладка елочка	55,0 м²	
2	Пол тп - 2. Керамогранит 1200*60	2,53 м²	
3	Пол тп - 3. Керамогранит 60*60	3,17 м²	
4	Пол тп - 4. Керамогранит 1200*60	3,83 м²	
5	Пол тп - 5. Керамогранит 60*60	2,79 м²	
6	Пол тп - 6. накладной плинтус 10см	54,0 п.м	

Спецификация розеток		
Вид	Позиция 1	Кол-во
	Розетки 220V	25 шт
	Интернет розетка 220 V	1 шт
	Влагостойкая розетка IP 44	5 шт
	Питание для кондиционера	

Спецификация потолочных материалов		
	Натяжной матовый потолок - уровень потолка - 0,100мм	59,0 м²
	Левкас уровень потолка -0,000	7,52 м²
	Галтели 10см	86,0 п.м

Спецификация дверных проемов				
N п/п	Размер проема	Размер полотна	Примечание	Кол-во
ДП-1	900-2400	800-2300	Толщина стены = 120мм	2
ДП-2	800-2400	700-2300	Толщина стены = 120мм	3

Спецификация выключателей		
Вид	Позиция 1	Кол-во
	Выключатель одноклавишный	5 шт
	Выключатель двухклавишный	4 шт
	Выключатель трехклавишный	1 шт
	Мастер выключатель	1 шт
	Проходной двухкл. выключатель	2 шт
	Проходной трехкл. выключатель	2 шт
	Питание для кондиционера	

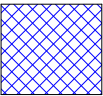Спецификация терморегулятора			
1	Теплый пол - санузлы, холл	1,14 м²	
2	Терморегулятор	1 шт	

Спецификация отделки сстен			
1	Обои	185,5 м²	