



План теплых полов

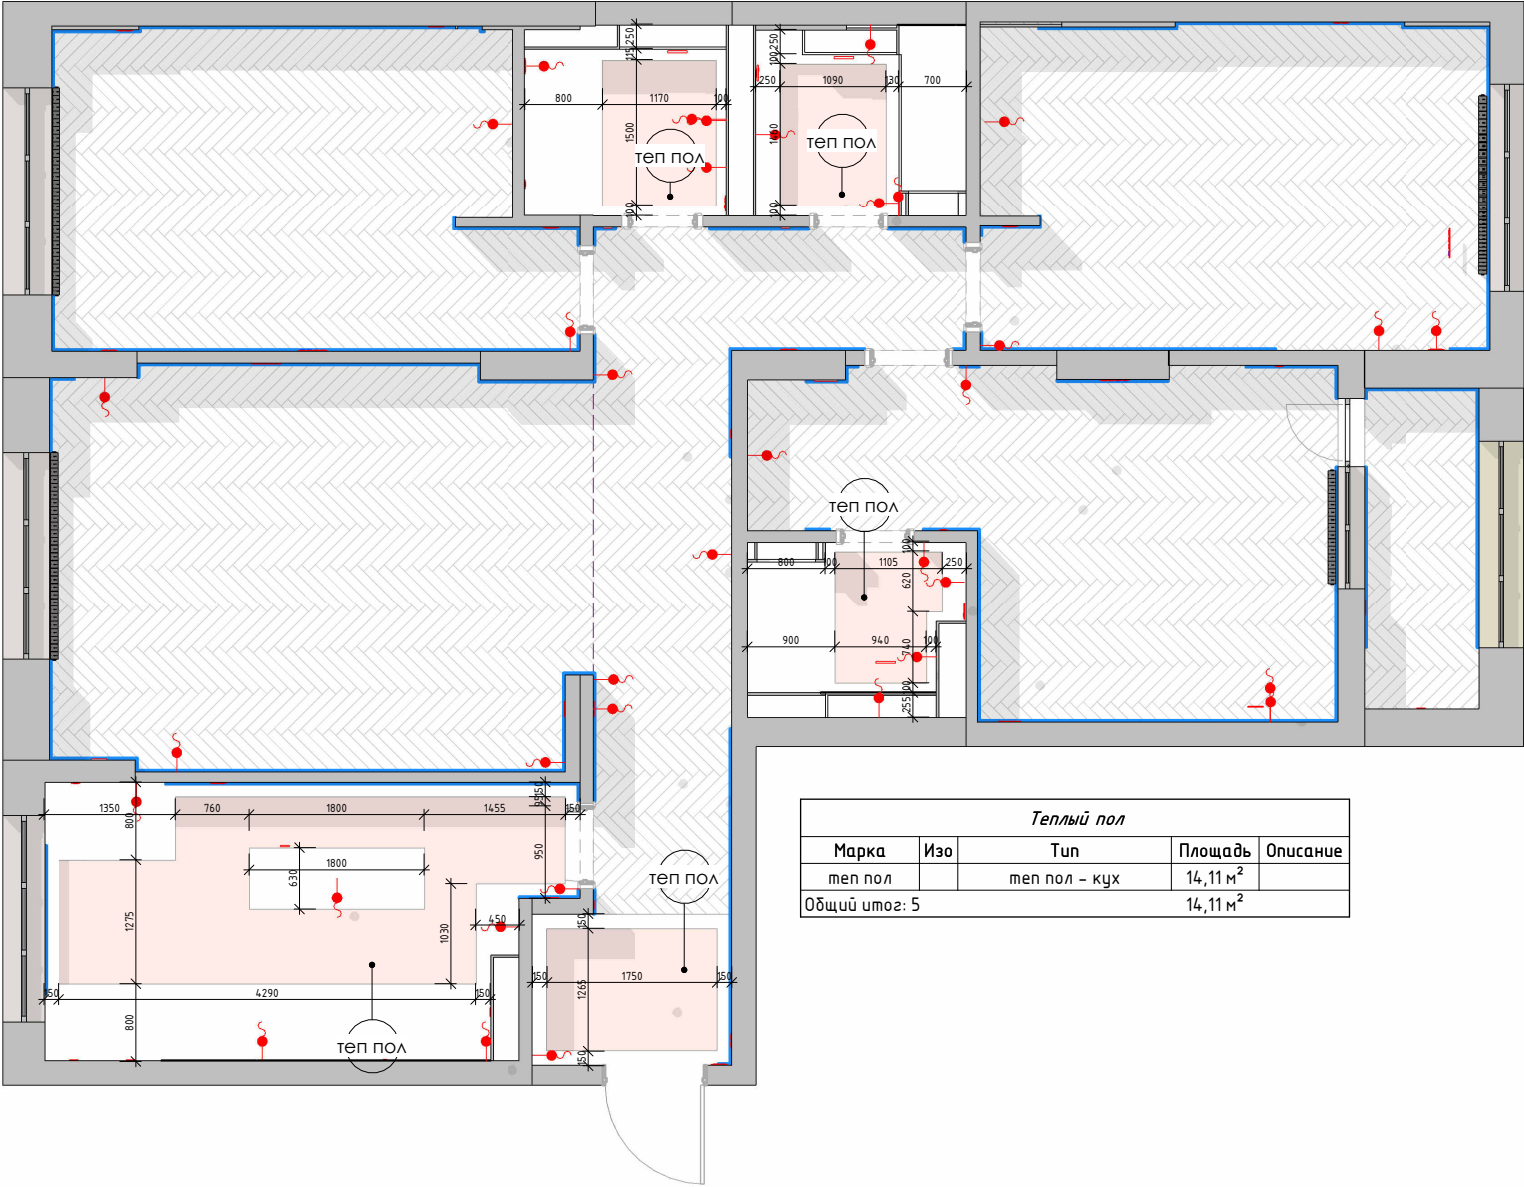

Теплый пол				
Марка	Изо	Тип	Площадь	Описание
теп пол		теп пол - кух	14,11 м ²	
Общий итог: 5			14,11 м ²	

План осветительного оборудования

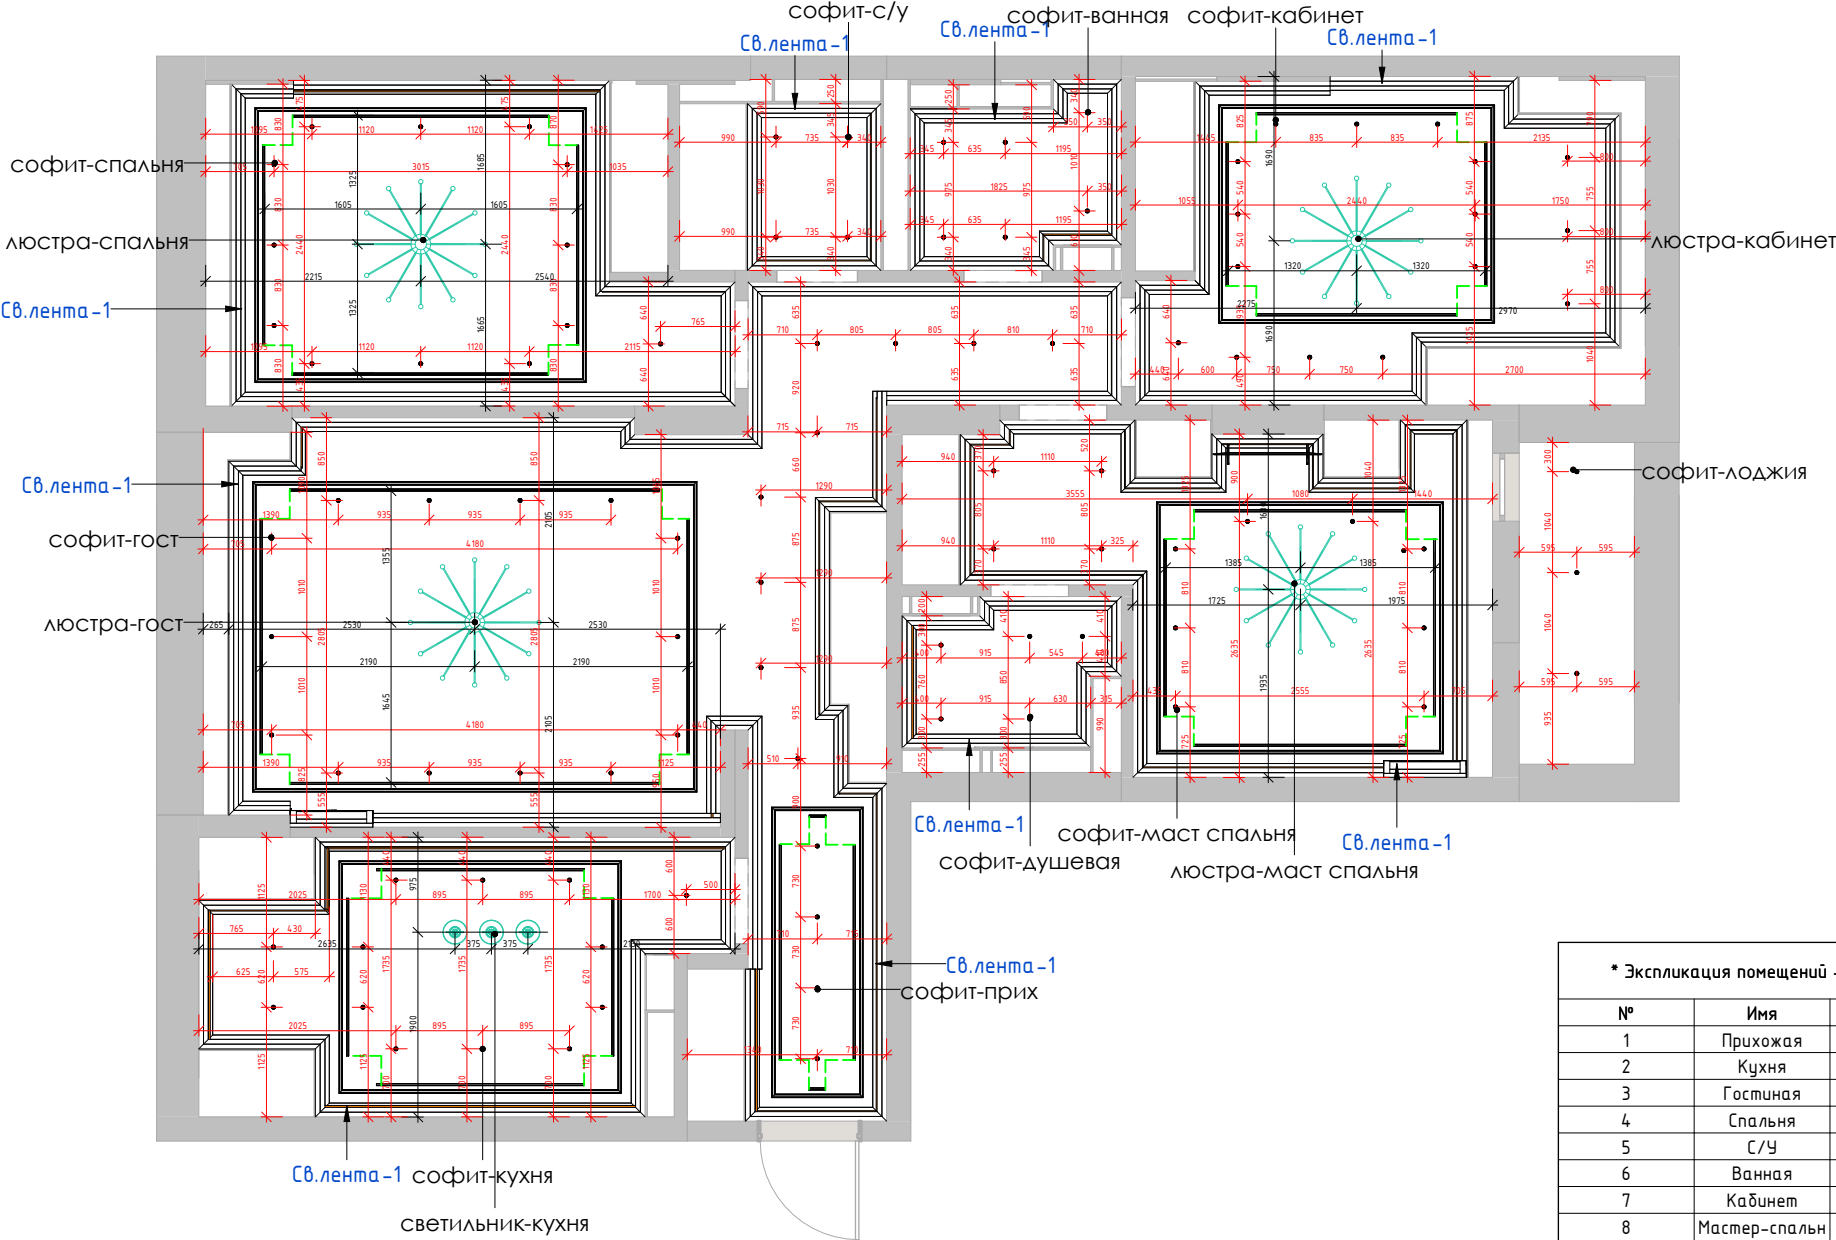


Дополнительные примечания:
1. Разметить места расположения точечных светильников и согласовать с заказчиком.


Примечание:
1. Комплект рабочих чертежей разработан на основе обмеров.
2. Все размеры указаны в миллиметрах
3. Перед началом работ все размеры проверить по месту

* Экспликация помещений - Отделка		
№	Имя	Площадь
1	Прихожая	16,32 м²
2	Кухня	14,48 м²
3	Гостиная	22,88 м²
4	Спальня	16,70 м²
5	С/У	3,52 м²
6	Ванная	3,76 м²
7	Кабинет	17,54 м²
8	Мастер-спальня	17,37 м²
9	Лоджия	3,92 м²
10	Мастер-с/у	3,10 м²
Общий итог: 10		119,58 м²

Схема управления освещением.

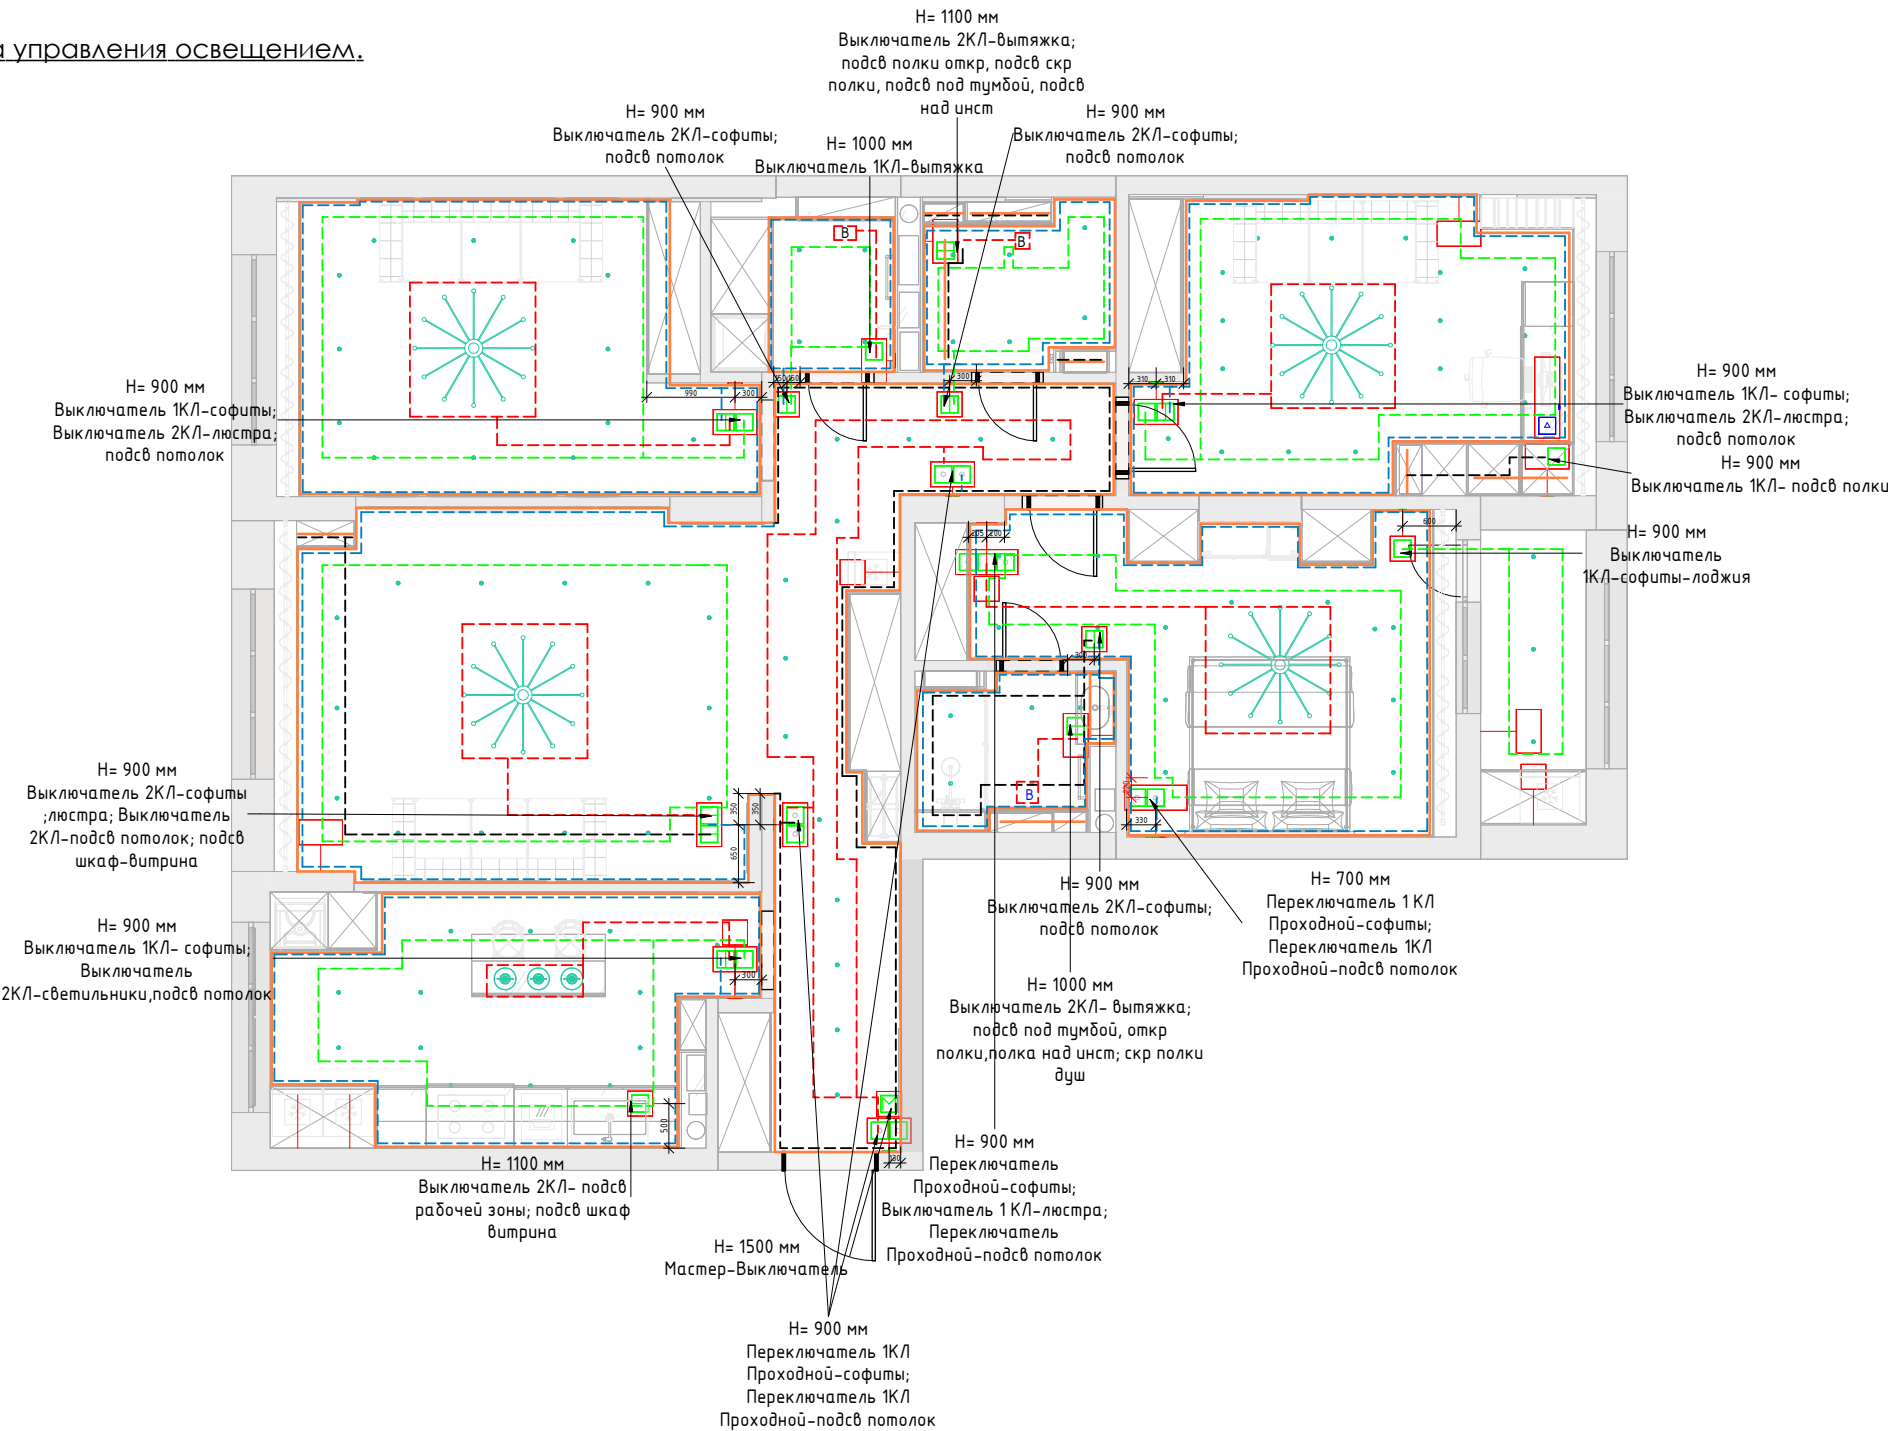

План сводный электроприборов

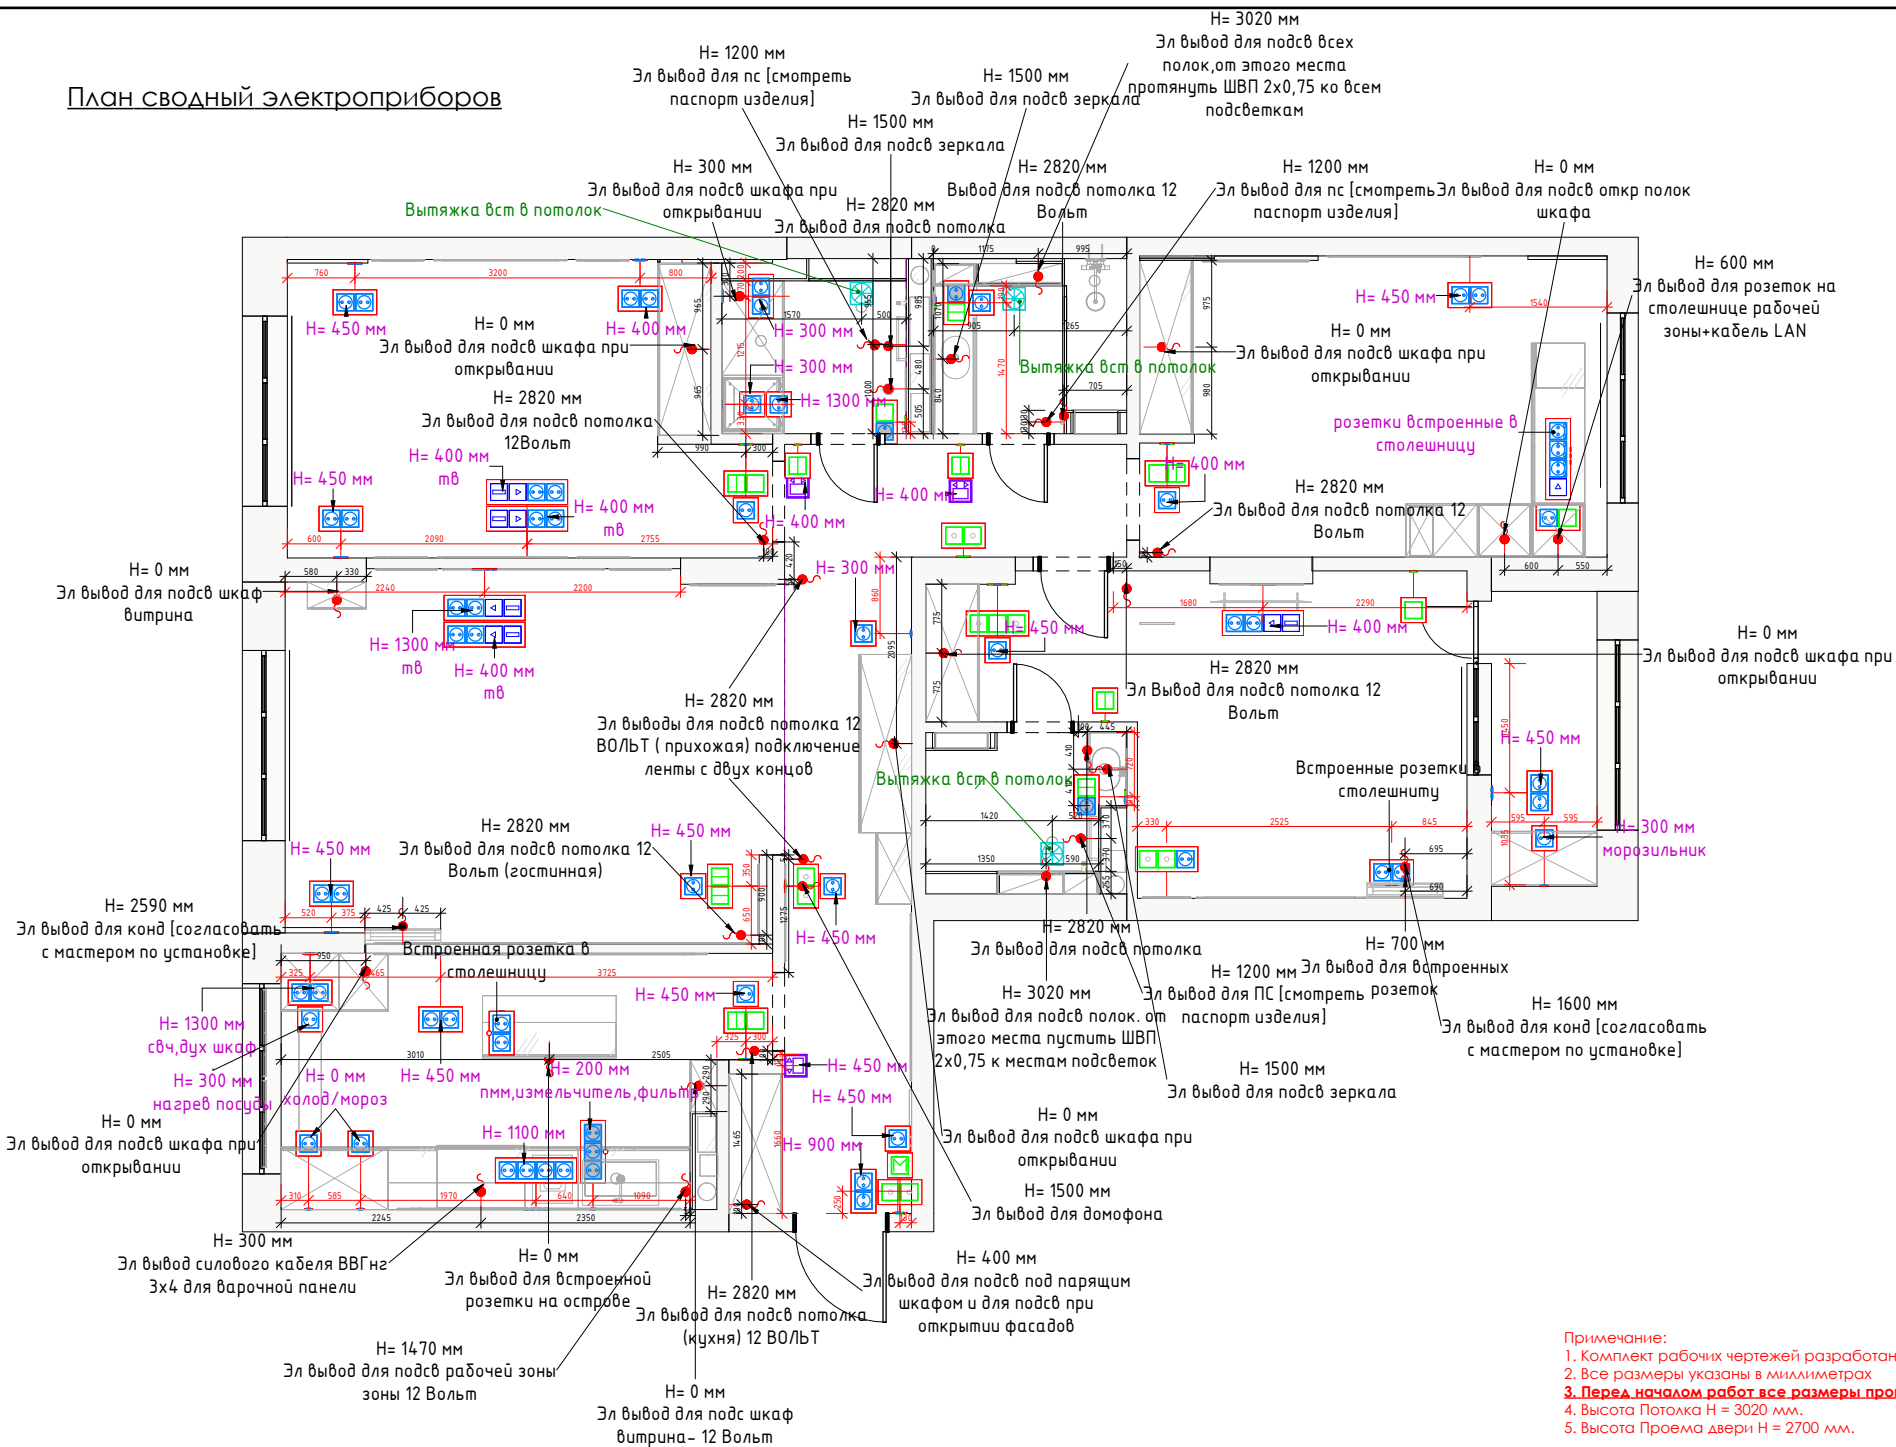

Примечание:

1. Комплект рабочих чертежей разработан на основе обмеров.
2. Все размеры указаны в миллиметрах
3. Перед началом работ все размеры проверить по месту
4. Высота Потолка Н = 3020 мм.
5. Высота Проема двери Н = 2700 мм.

*Спецификация силовых электроприборов – ВЫКЛЮЧАТЕЛИ по помещениям			
Помещение: Имя	Условное обозначени е 2	Описание	Число
Ванная			
Ванная		Выключатель двухклавишный	1
Ванная: 1			
Гостиная		Выключатель двухклавишный	2
Гостиная: 2			
Кухня			
Кухня		Выключатель одноклавишный	1
Кухня		Выключатель двухклавишный	2
Кухня: 3			
Мастер-с/у			
Мастер-с/у		Выключатель двухклавишный	1
Мастер-с/у: 1			
Мастер-спальня			
Мастер-спа льня		Выключатель одноклавишный	2
Мастер-спа льня		Выключатель двухклавишный	1
Мастер-спа льня		Переключатель одноклавишный	4
Мастер-спальня: 7			
Прихожая			
Прихожая		Выключатель двухклавишный	2
Прихожая		Выключатель одноклавишный (мастер)	1
Прихожая		Переключатель одноклавишный	6
Прихожая: 9			
С/У-1			
С/У-1		Выключатель одноклавишный	1
С/У-1: 1			
Спальня-1			
Спальня-1		Выключатель одноклавишный	1
Спальня-1		Выключатель двухклавишный	1
Спальня-1: 2			
Спальня-2			
Спальня-2		Выключатель одноклавишный	2
Спальня-2		Выключатель двухклавишный	1
Спальня-2: 3			

* Спецификация силовых электроприборов – ИТОГО			
Условное обозначение 2	Тип	Число	Описание
	1КЛ	7	Выключатель одноклавишный
	1КЛ	10	Переключатель одноклавишный
	2КЛ	11	Выключатель двухклавишный
	220 V	55	Розетка 220V
	220V	36	Вывод кабеля 220V
	HDMI 1x	5	HDMI розетка 1x
	IP20 с крышкой	6	Розетка 220V IP20 с крышкой
	RJ45 1x (Интернет)	6	Интернет розетка RJ45 1x
	USB	3	Розетка 220V + 2x USB
	Вентилятор	3	Вентилятор
	МАСТЕР	1	Выключатель одноклавишный (мастер)
	Терморегулято р теплого пола – Электронный	3	Терморегулятор теплого пола – Электронный

* Спецификация осветительных приборов		
Марка	Тип	Ко-во
	690 lm 6W 830 350 mA 18,6V 38° IP20	2
люстра-кабин ет	Люстра классическая	1
люстра-гост	люстра- гост	1
люстра-маст спальня	люстра-мас спальня	1
люстра-спаль ня	люстра-спальня2	1
светильник-к ухня	свтильник-кухня	3
софит-ванная	софит-ванная	6
софит-гост	софит-гост	14
софит-душева я	софит-душ	5
софит-кабине т	софит-кабинет	16
софит-кухня	софит-кухня	13
софит-лоджия	софит-лоджия	3
софит-маст спальня	софит-маст спальня	13
софит-с/у	софит-с/у	4
софит-спальн я	софит-спальня2	13
софит-прих	софиты-прих	13

* Спецификация силовых электроприборов – ИТОГО РАМКИ		
Тип	Число	Описание
1x	21	Рамка на 1 пост
2x	23	Рамка на 2 поста
3x	3	Рамка на 3 поста
4x	7	Рамка на 4 поста