

РАБОЧИЙ ПРОЕКТ


SARA.architects

КВАРТИРА

Расположенная по адресу:


г.Нур-Султан, ул.ца ,

ЖК "**AKDIDAR**" кв .

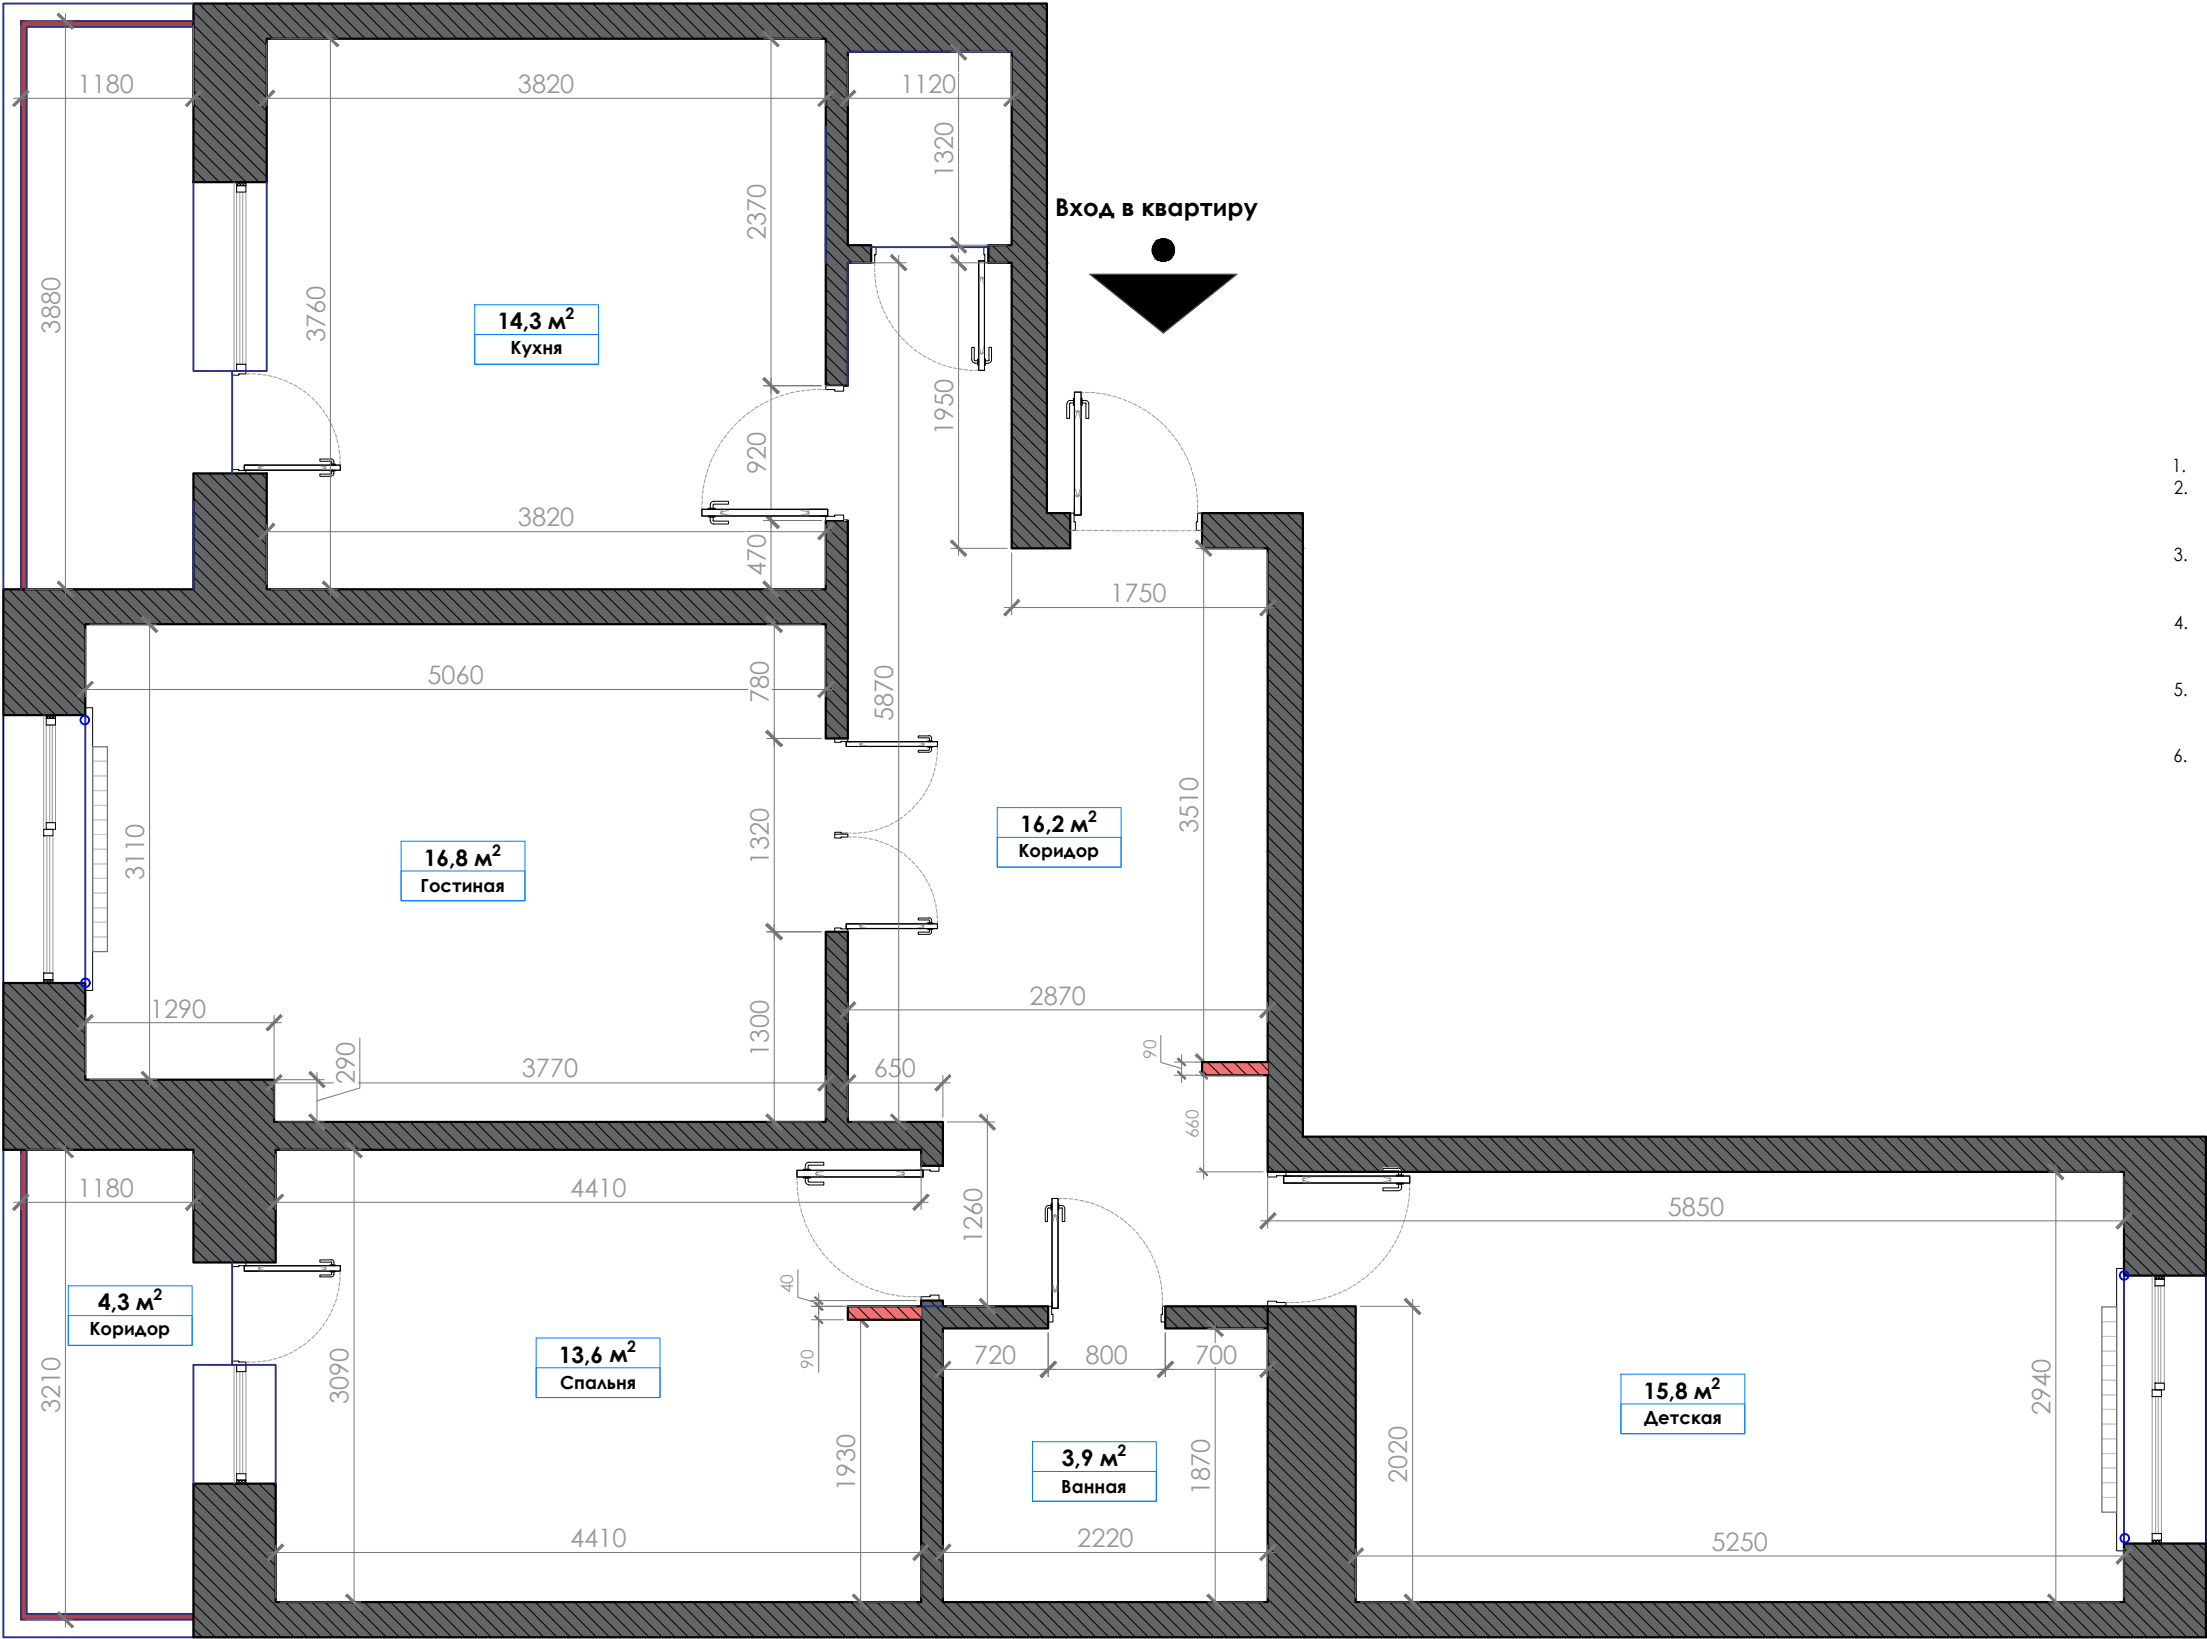

Экспликация помещений:		
№ п/п	Наименование помещения	S, м²
1	Коридор	16.2
2	Детская	15.8
3	Ванная	3.9
4	Спальня	13.6
5	Балкон	3.7
6	Гостиная	16.80
7	Санузел	1.40
8	Кухня	14.30
9	Балкон	4.30
Общая площадь (S) квартиры:		90м2
Высота потолка: 2740мм		
Высота дверных проемов: 2100мм		

1. Все размеры указаны в миллиметрах.
2. Стык покрытий, попадающий в дверной проем предусмотреть под толщиной дверного полотна.
3. Отметки верха напольного покрытия по всей квартире должны быть выполнены в одном уровне без перепадов.
4. Перед укладкой плитки/паркета- уточнить способ и начало укладки у представителя авторского надзора.
5. За встроенными и крупногабаритными шкафами, а также на местах отмеченные на плане плинтус не предусматривать
6. Отрезки плинтуса, примыкающие к встроенной мебели устанавливать после монтажа встроенной мебели

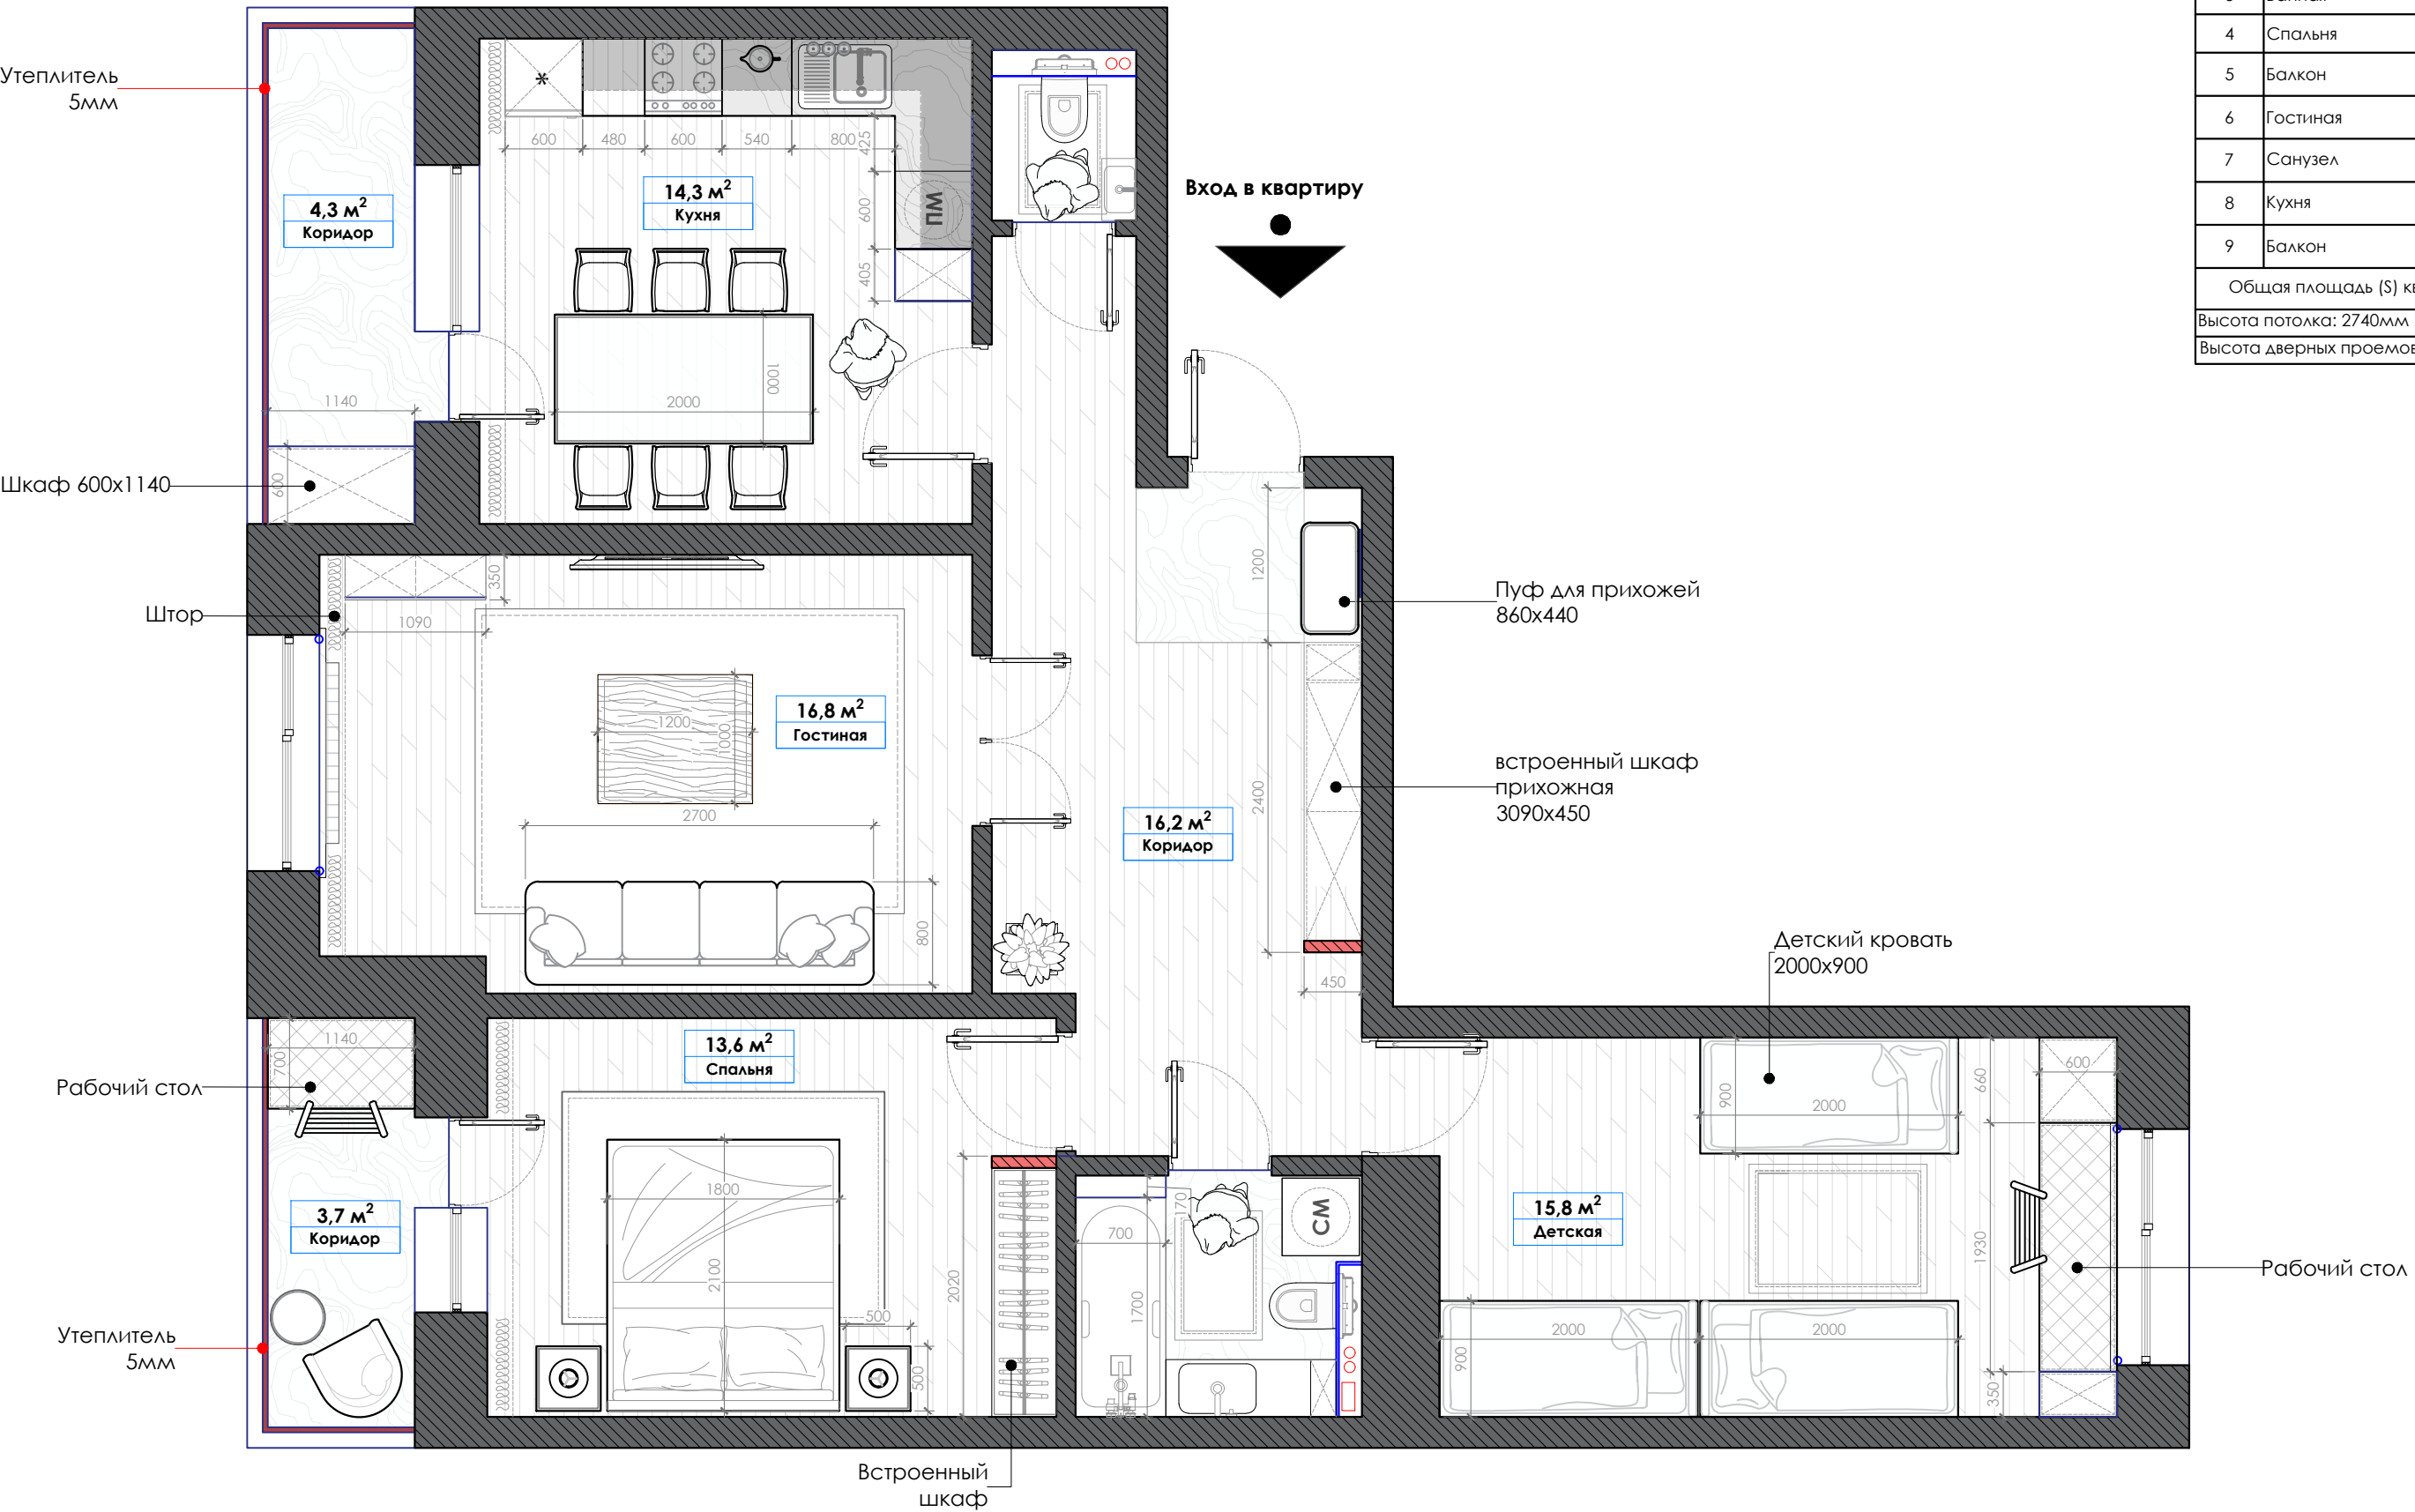


Экспликация помещений:		
№ п/п	Наименование помещения	S, м²
1	Коридор	16.2
2	Детская	15.8
3	Ванная	3.9
4	Спальня	13.6
5	Балкон	3.7
6	Гостиная	16.80
7	Санузел	1.40
8	Кухня	14.30
9	Балкон	4.30
Общая площадь (S) квартиры:		90м2
Высота потолка: 2740мм		
Высота дверных проемов: 2100мм		

ПРИМЕЧАНИЯ:

1. Все размеры указаны в миллиметрах
2. На плане указаны проектные размеры.
3. Размеры по факту могут незначительно отличаться от проектных. Регулировать на месте.

				Дизайн проект 90м2	Стадия	Лист	Листов
					АИ	2	16
Выполнил				План расстановки мебели			
Проверил							

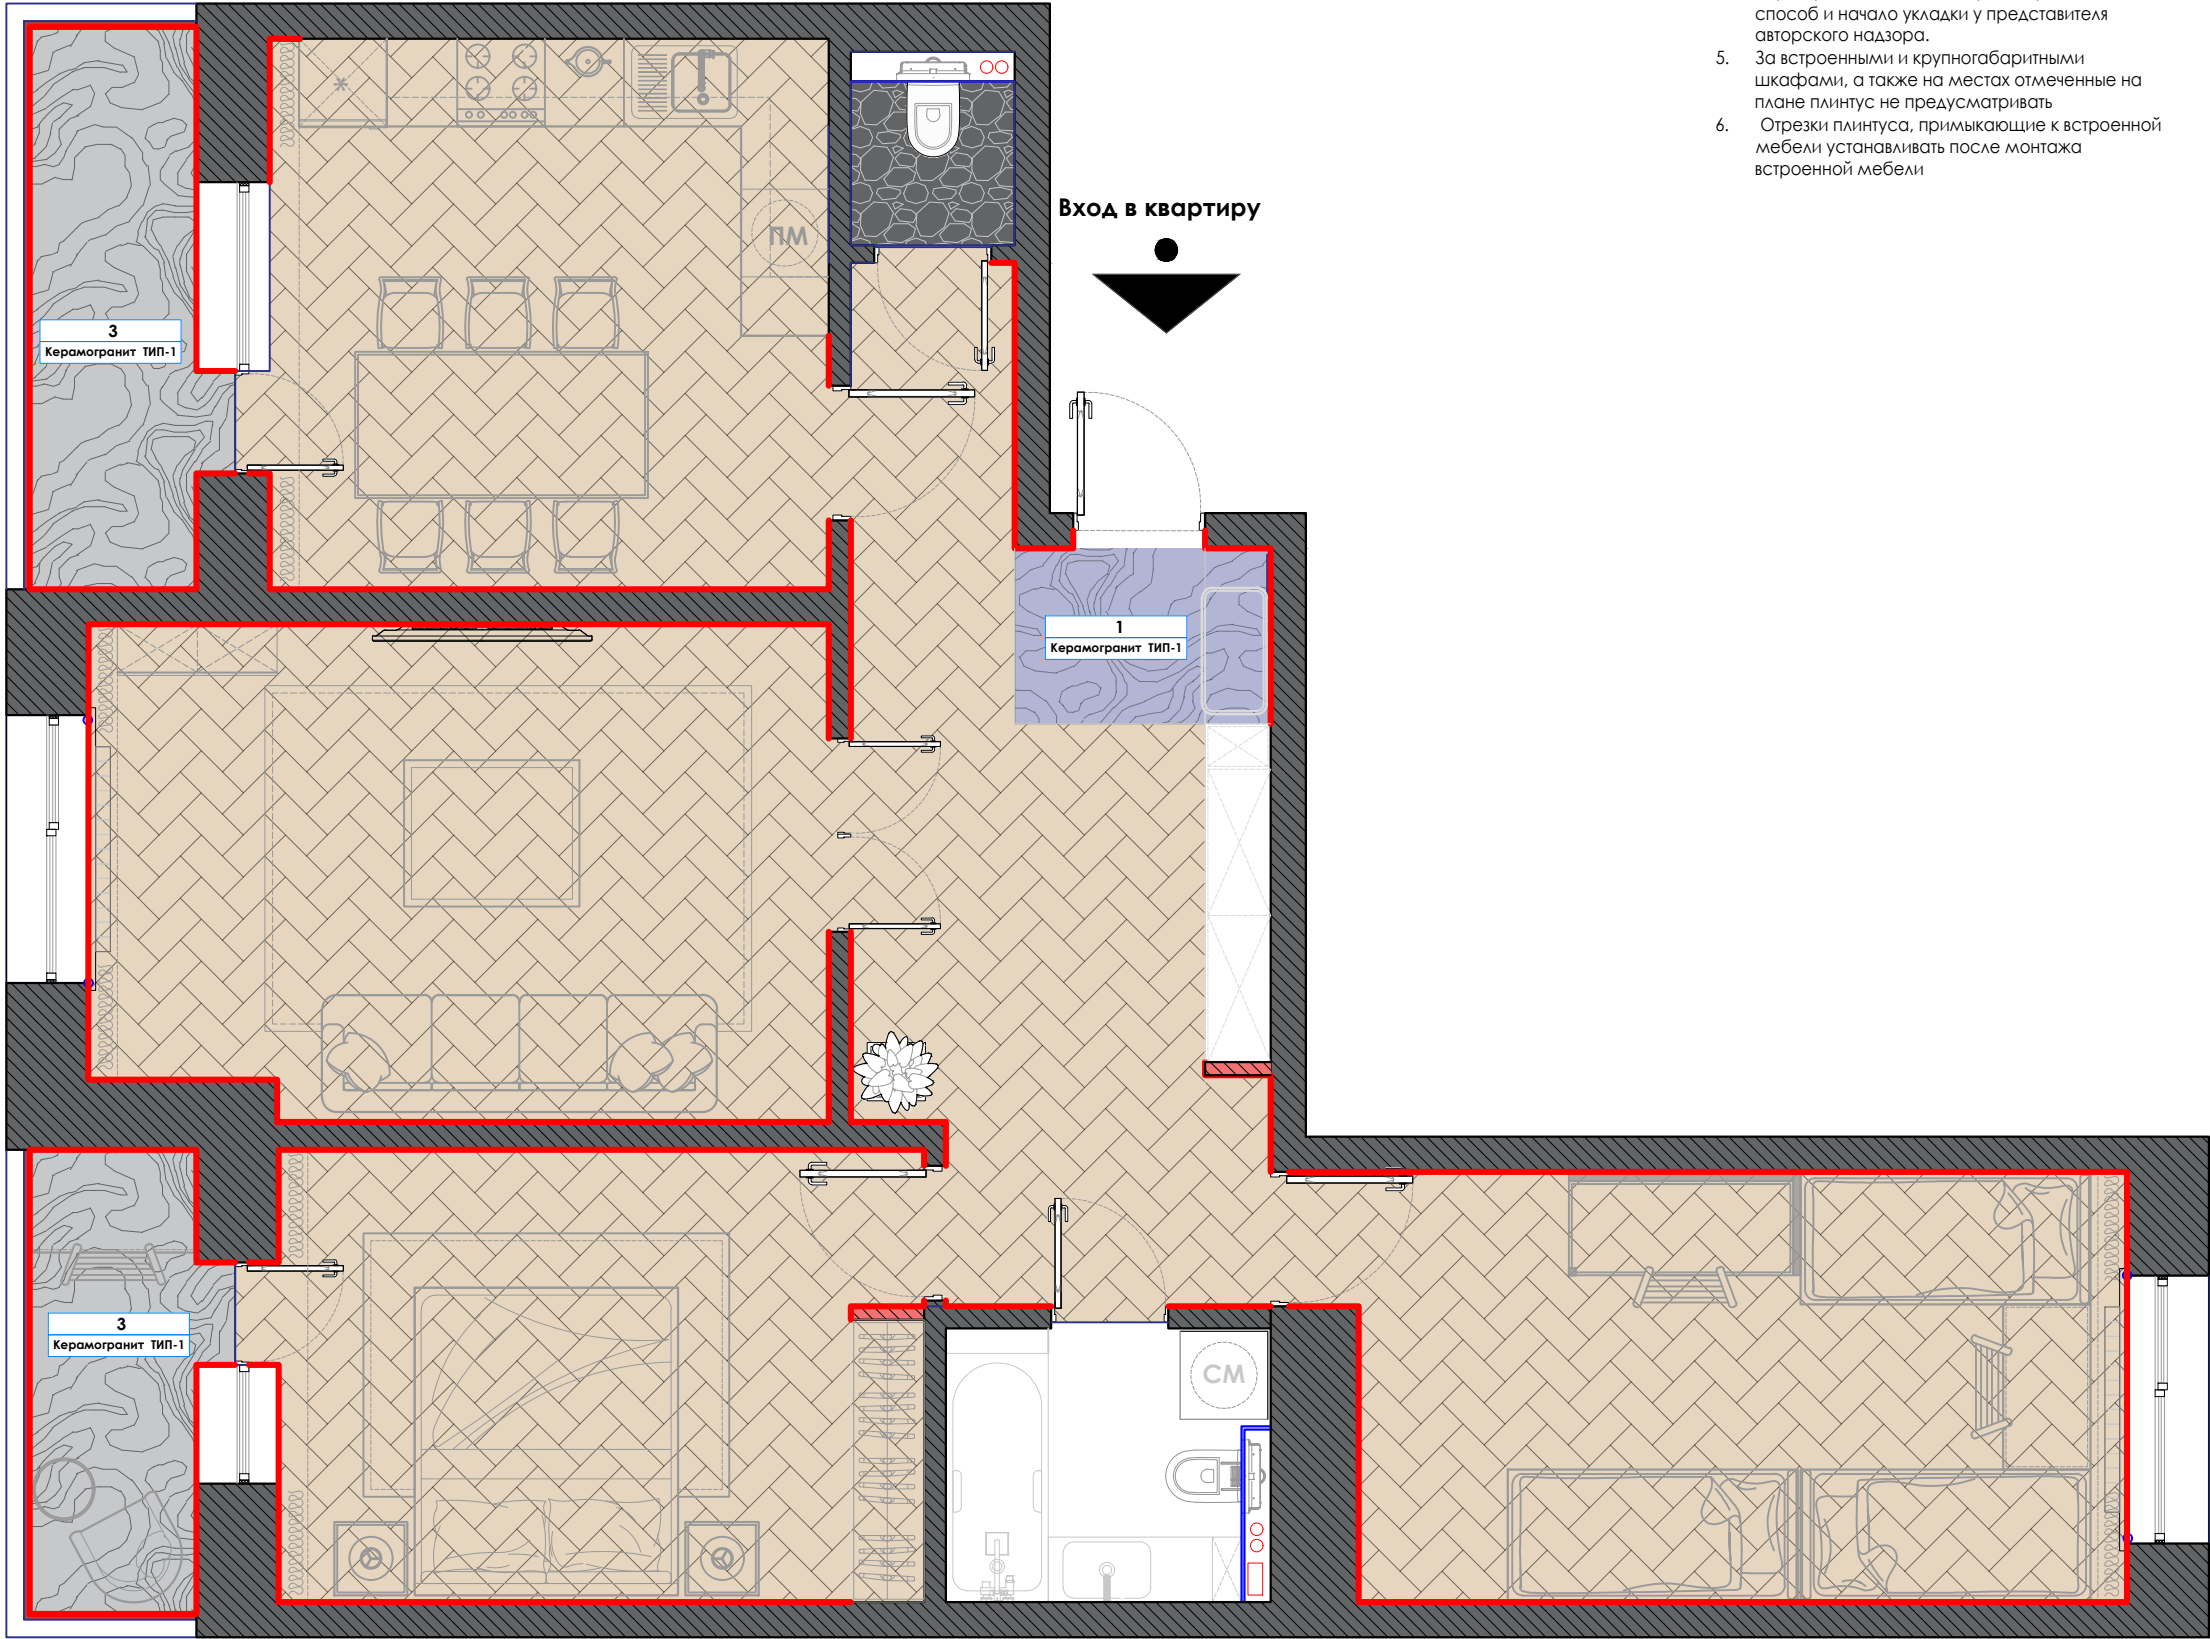

1. Все размеры указаны в миллиметрах.
2. Стык покрытий, попадающий в дверной проем предусмотреть под толщиной дверного полотна.
3. Отметки верха напольного покрытия по всей квартире должны быть выполнены в одном уровне без перепадов.
4. Перед укладкой плитки/паркета- уточнить способ и начало укладки у представителя авторского надзора.
5. За встроенными и крупногабаритными шкафами, а также на местах отмеченные на плане плинтус не предусматривать
6. Отрезки плинтуса, примыкающие к встроенной мебели устанавливать после монтажа встроенной мебели

Экспликация помещений:		
№ п/п	Наименование помещения	S, м²
1	Коридор	16,2
2	Детская	15,8
3	Ванная	3,9
4	Спальня	13,6
5	Балкон	3,7
6	Гостиная	16,80
7	Санузел	1,40
8	Кухня	14,30
9	Балкон	4,30
Общая площадь (S) квартиры:		90м2
Высота потолка: 2740мм		
Высота дверных проемов: 2100мм		

Усл. обозначения	Материал	м²
Тип1	Керамогранит (Тип 1) 600х600	2м2
Тип2	Керамогранит (Тип 2) 1200х600	2.7м2
Тип3	Керамогранит (Тип 3) 1200х600	8.2м2
Тип4	Керамогранит (Тип 4) 600х600	1.52м2
	Ламинат	74.7м2
	Плинтус Н=100	77.1 п.м

ПРИМЕЧАНИЯ:
1. Все размеры указаны в миллиметрах
2. На плане указаны проектные размеры.
3. Размеры по факту могут незначительно отличаться от проектных. Регулировать на месте.

				Дизайн проект 90м2	Стадия	Лист	Листов
					АИ	3	16
Выполнил				План пола			
Проверил							

ПРИМЕЧАНИЯ:

1. Все размеры указаны в миллиметрах.
2. Отметки высот указаны от уровня существующего потолка отм. 0.000.
3. Конструкции потолка из ГКЛ/ГКЛВ (санузлы) монтировать только после прокладки воздуховодов (вытяжная вентиляция во влажных помещениях, кондиционирование комнат, воздуховод для кухонной вытяжки) и других коммуникаций, проходящих над потолком.
4. Подвесной потолок устроить из ГК листов по каркасу из оцинкованных профилей с последующей проклейкой швов, грунтовкой, шпаклевкой, оклейкой флизелином (безфактурным) и покраской в 2 слоя.
5. Монтажные отверстия для накладных и встраиваемых светильников выполнить по факту (при наличии подобного типа светильников).
6. Конструкция потолка из ГКЛ/ГКЛВ (санузлы) монтироваться только после выбора встраиваемых софитов. Уточнить у представителя авторского надзора.

Экспликация помещений:

№ п/п	Наименование помещения	S, м²
1	Коридор	16.2
2	Детская	15.8
3	Ванная	3.9
4	Спальня	13.6
5	Балкон	3.7
6	Гостиная	16,80
7	Санузел	1,40
8	Кухня	14,30
9	Балкон	4,30
Общая площадь (S) квартиры:		90м2

Высота потолка: 2740мм

Высота дверных проемов: 2100мм

Обозн.	Материал	Кол-во	Цвет
	Натяжной потолок	76 м2	
	Натяжной потолок	5 м2	
	Покраска	4.3 м2	Ral-9016

Узел 1

Узел 1


Узел 1

Вход в квартиру

Узел 1

Устройство ниш для скрытого
потолочного карниза для штор

Узел 2

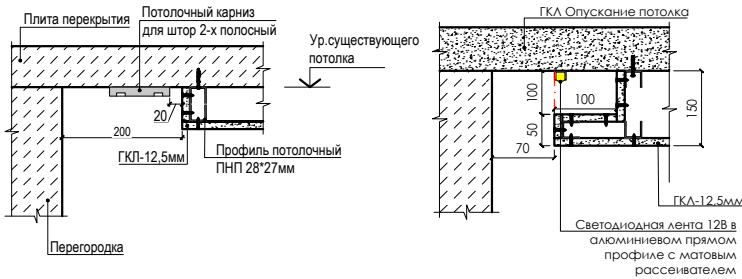


Узел 2

ПРИМЕЧАНИЯ:

1. Все размеры указаны в миллиметрах
2. На плане указаны проектные размеры.
3. Размеры по факту могут незначительно отличаться от проектных. Регулировать на месте.

				Дизайн проект 90м2	Стадия	Лист	Листов
					АИ	4	16
Выполнил				План потолка			
Проверил							

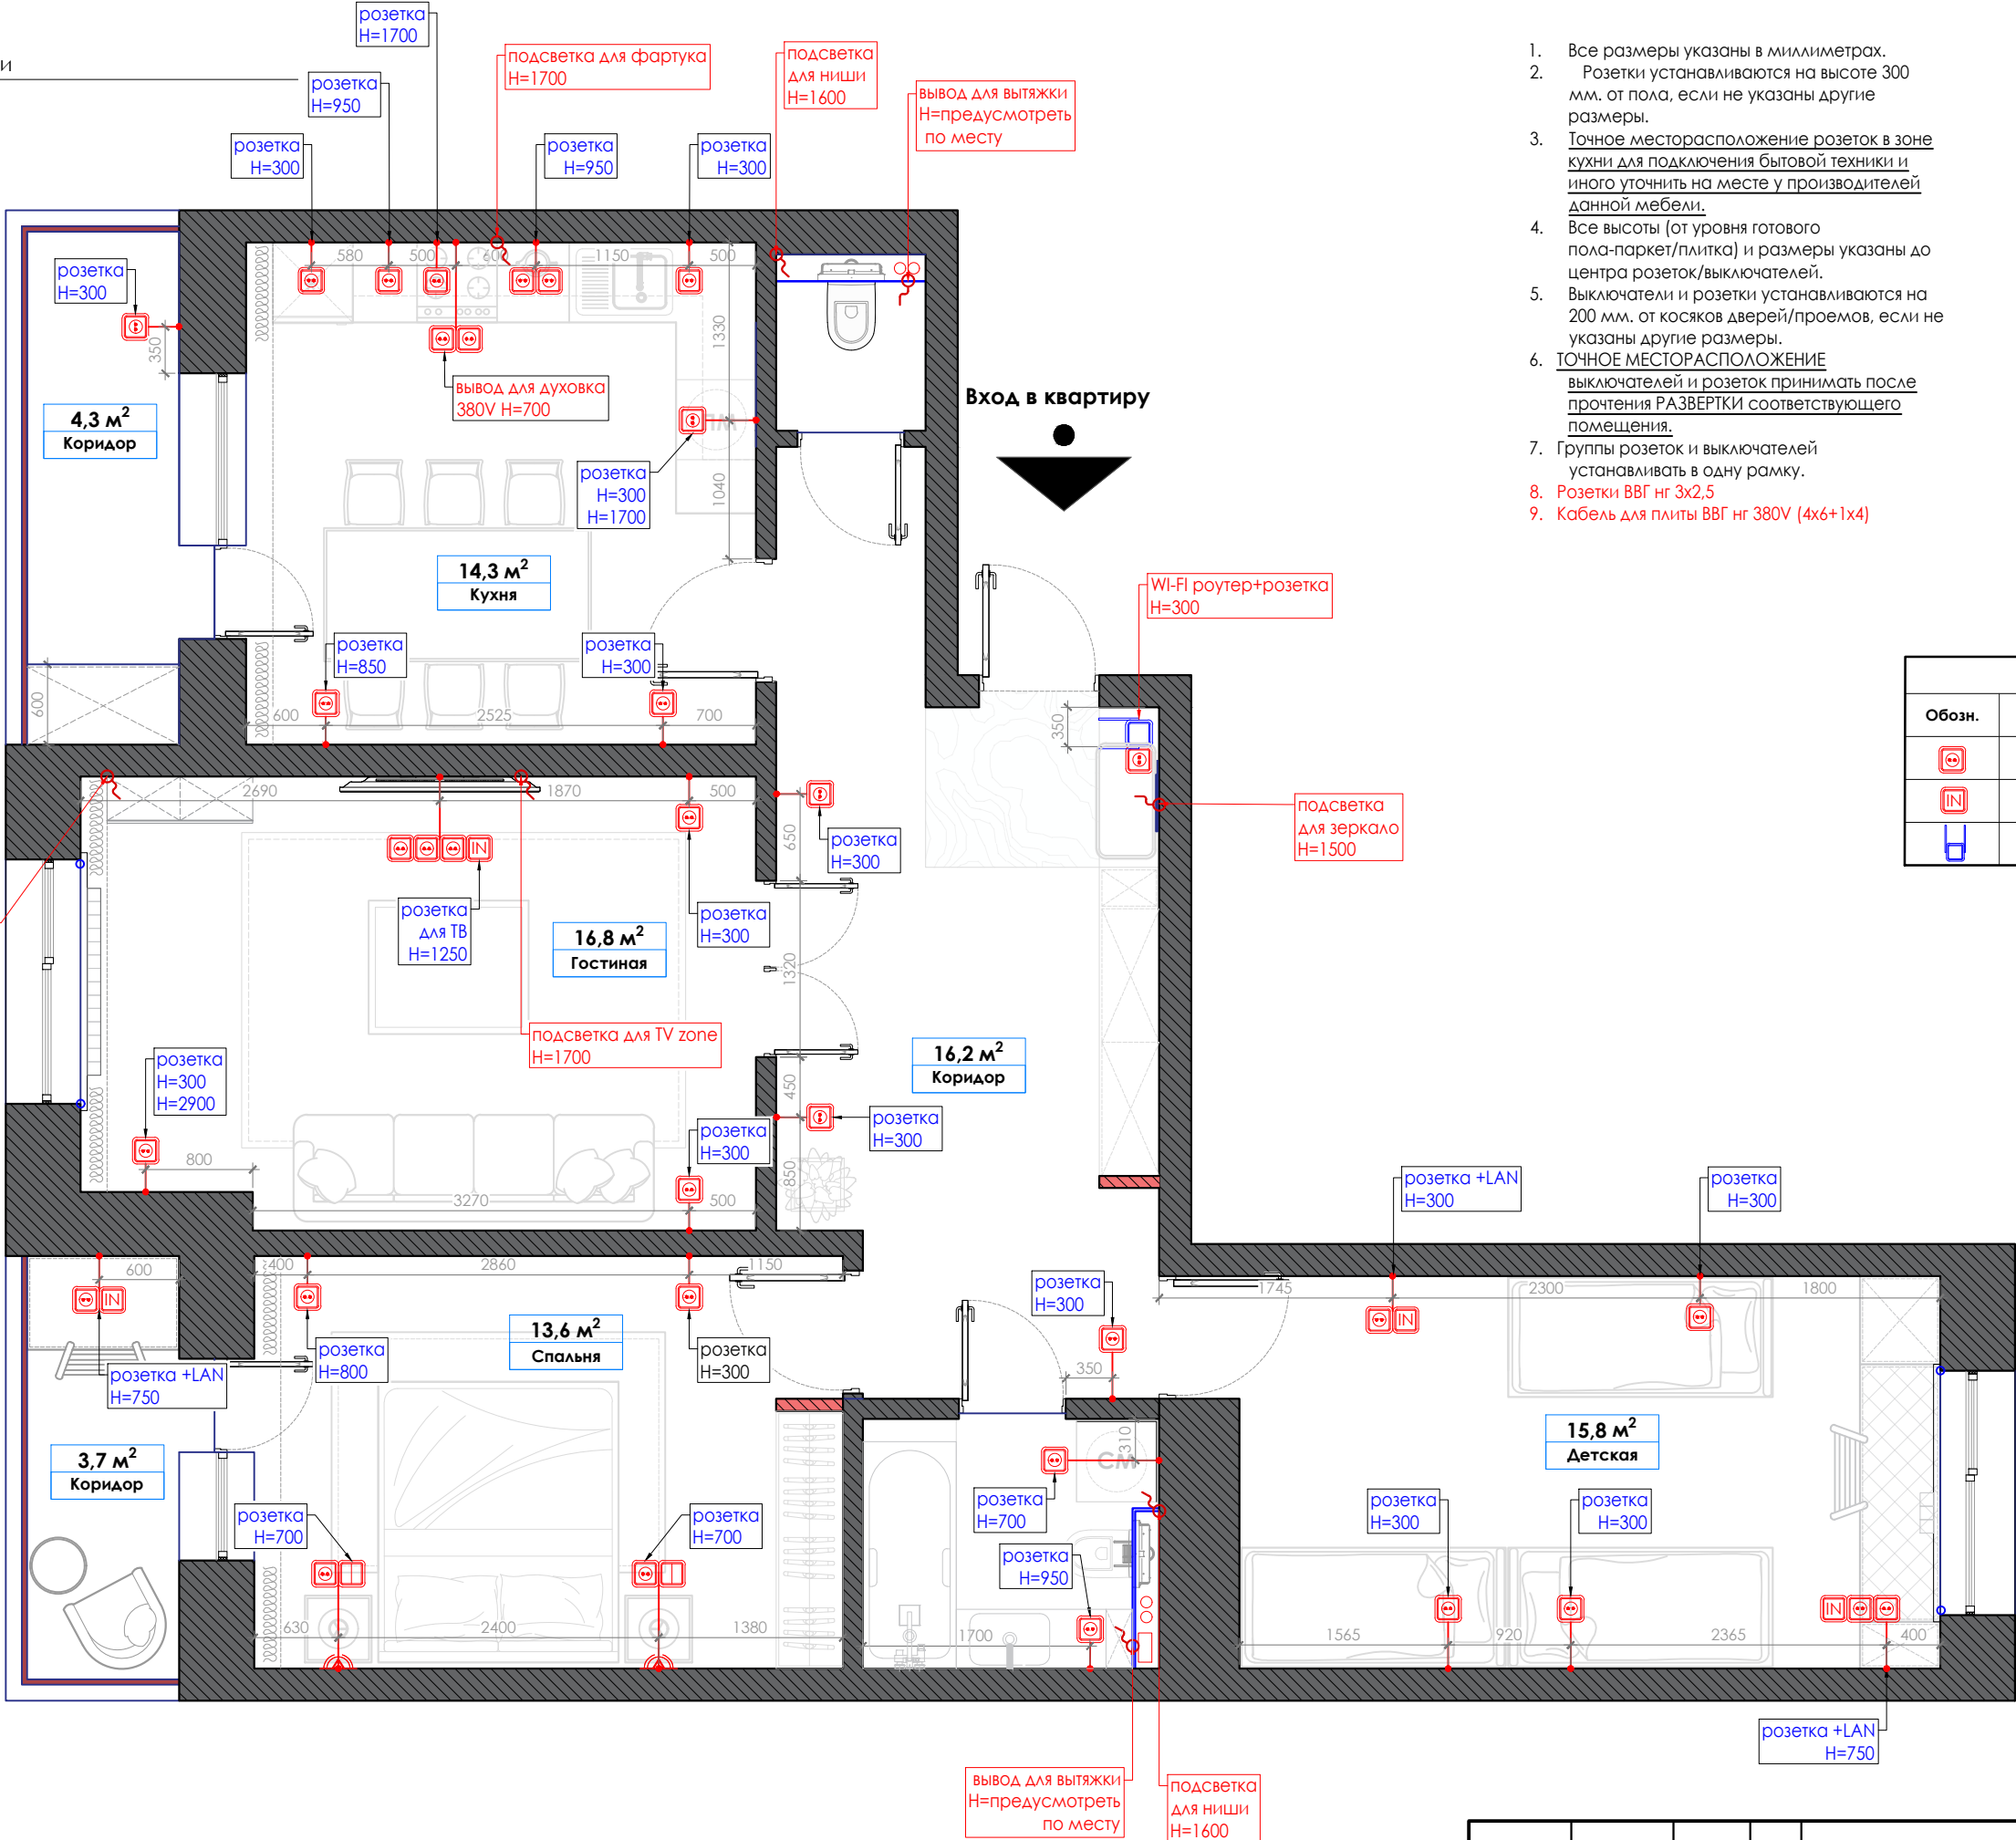


1. Все размеры указаны в миллиметрах.
2. Розетки устанавливаются на высоте 300 мм. от пола, если не указаны другие размеры.
3. Точное месторасположение розеток в зоне кухни для подключения бытовой техники и иного уточнить на месте у производителей данной мебели.
4. Все высоты (от уровня готового пола-паркет/плитка) и размеры указаны до центра розеток/выключателей.
5. Выключатели и розетки устанавливаются на 200 мм. от косяков дверей/проемов, если не указаны другие размеры.
6. ТОЧНОЕ МЕСТОРАСПОЛОЖЕНИЕ выключателей и розеток принимать после прочтения РАЗВЕРТКИ соответствующего помещения.
7. Группы розеток и выключателей устанавливать в одну рамку.
8. Розетки ВВГ нг 3х2,5
9. Кабель для плиты ВВГ нг 380V (4х6+1х4)

Экспликация помещений:		
№ п/п	Наименование помещения	S, м²
1	Коридор	16.2
2	Детская	15.8
3	Ванная	3.9
4	Спальня	13.6
5	Балкон	3.7
6	Гостиная	16.80
7	Санузел	1.40
8	Кухня	14.30
9	Балкон	4.30
Общая площадь (S) квартиры:		90м2
Высота потолка: 2740мм		
Высота дверных проемов: 2100мм		

Розеточная группа		
Обозн.	Наименование	Кол-во
	Настенная пылезащитная розетка с заземлением	36
	INTERNET	4
	Wi-Fi роутер	1

ПРИМЕЧАНИЯ:
1. Все размеры указаны в миллиметрах.
2. На плане указаны проектные размеры.
3. Размеры по факту могут незначительно отличаться от проектных. Регулировать на месте.

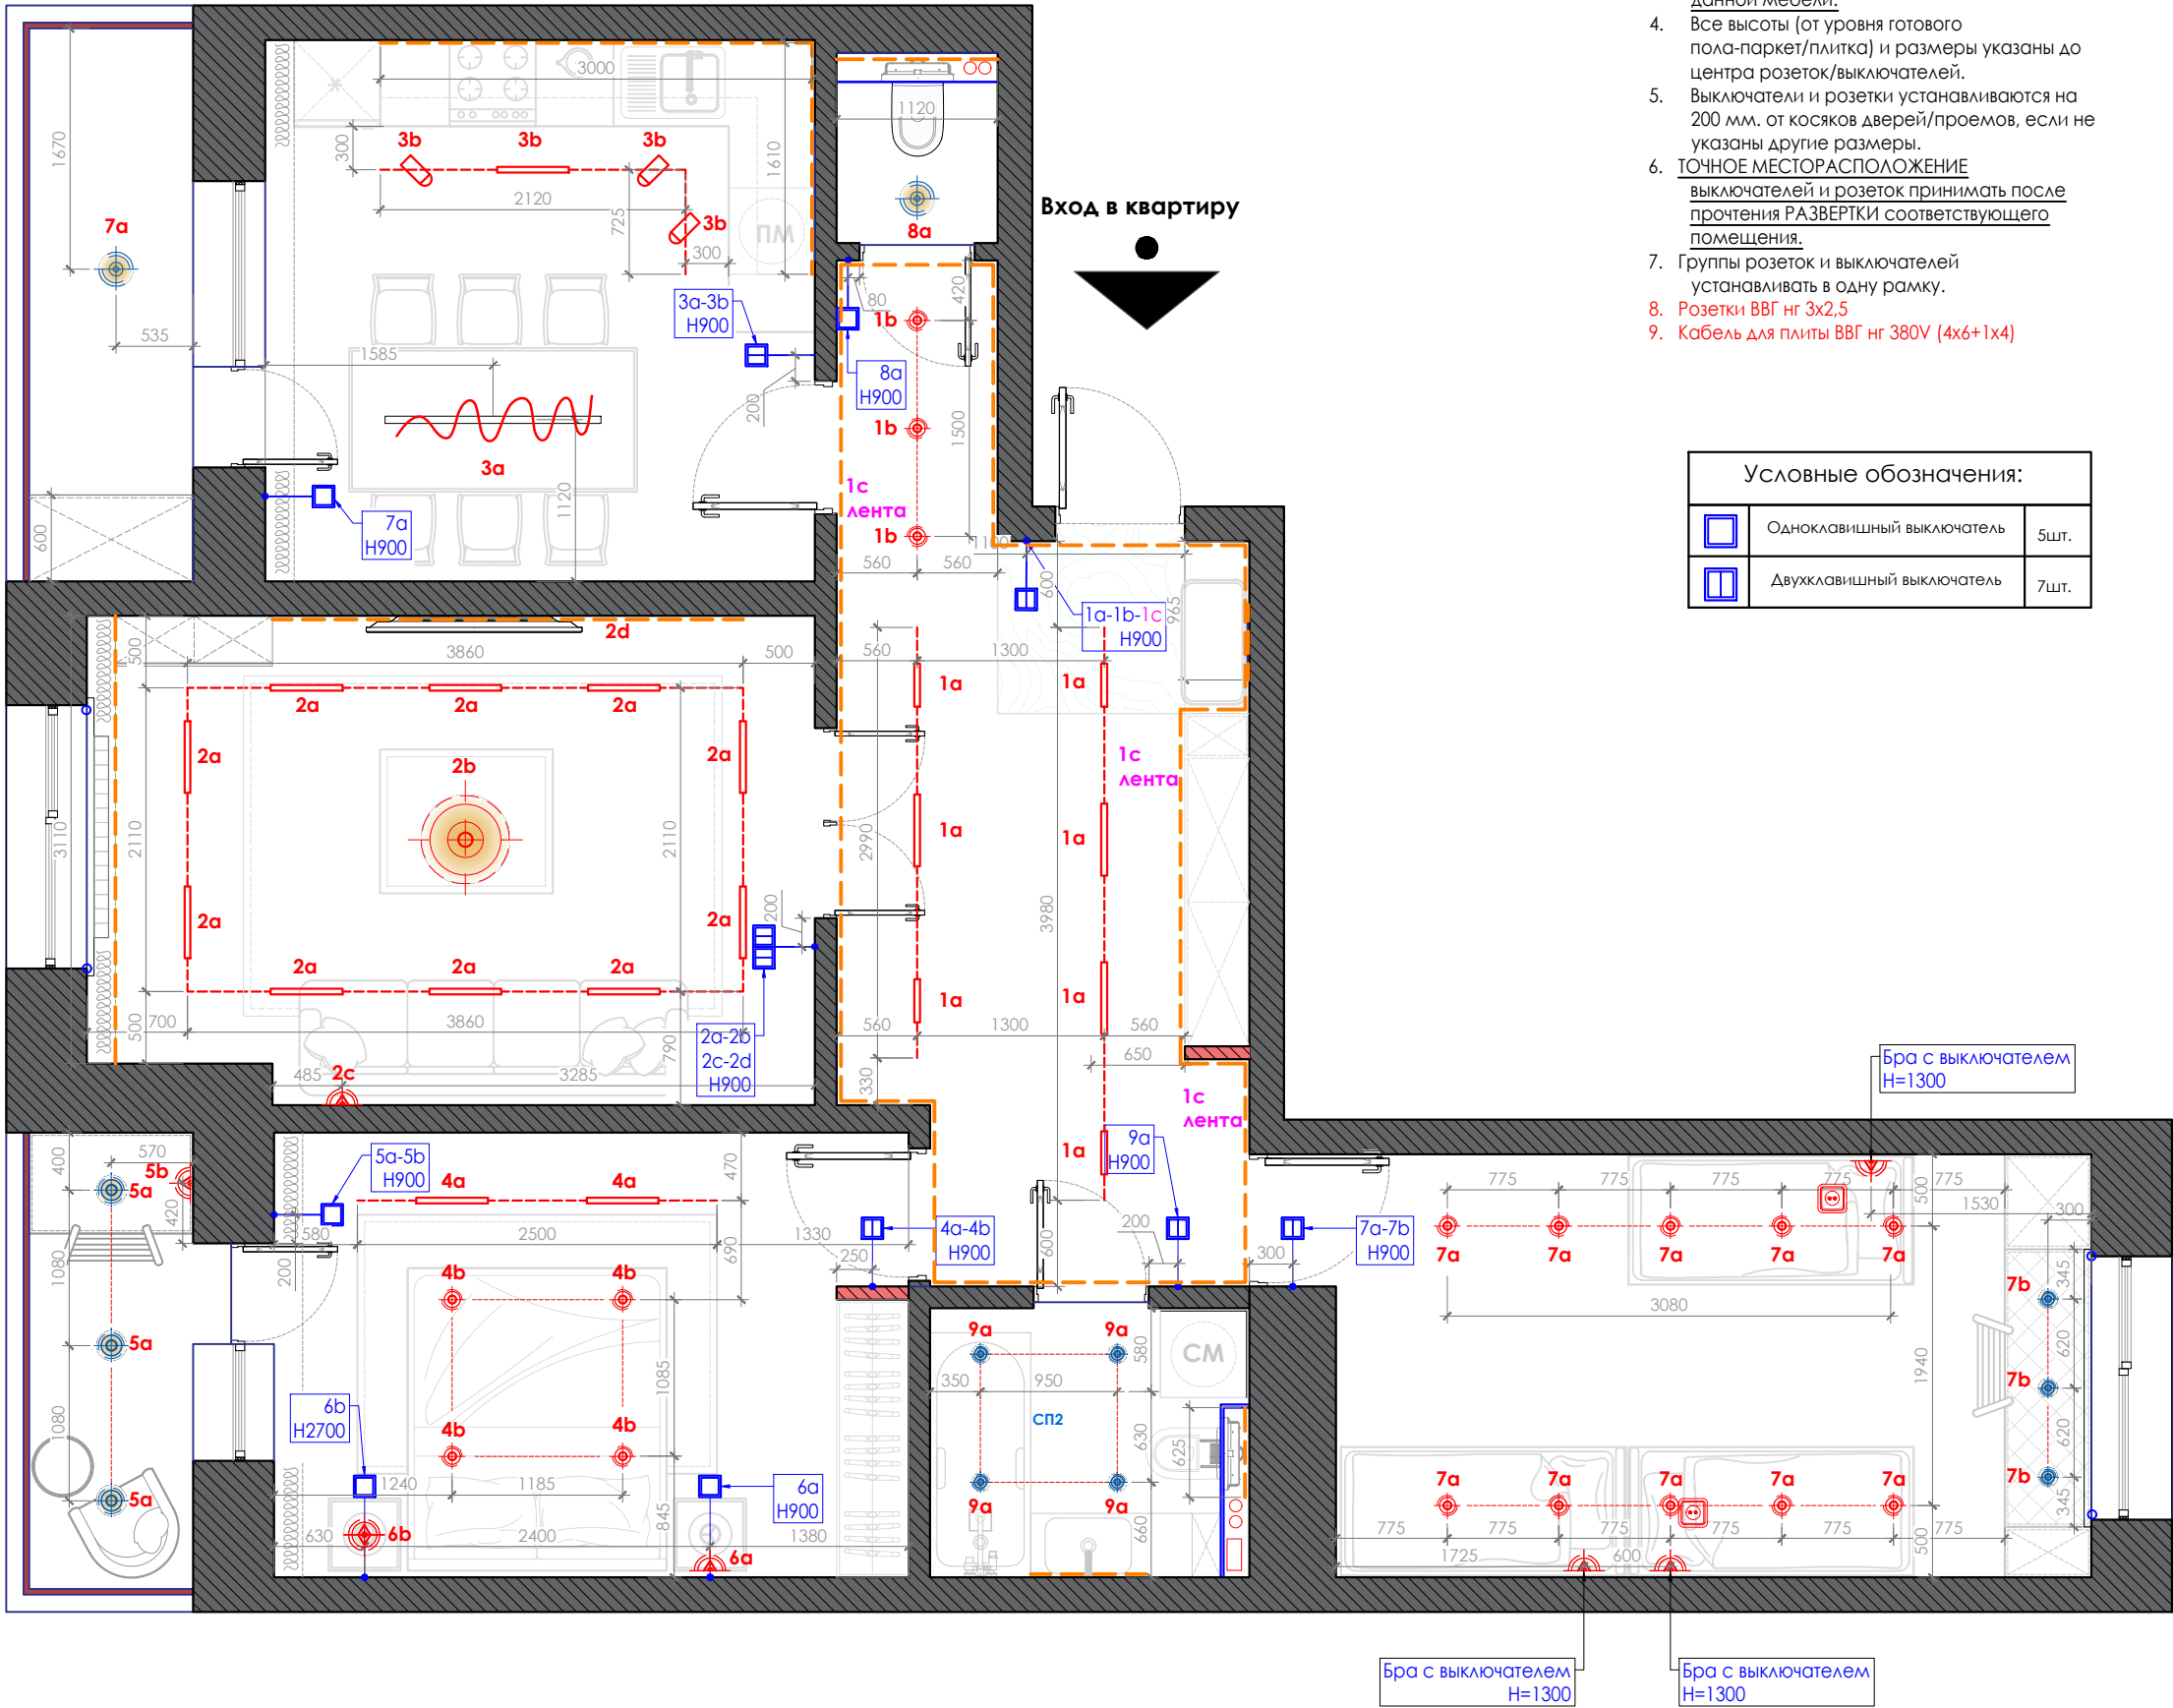

1. Все размеры указаны в миллиметрах.
2. Розетки устанавливаются на высоте 300 мм. от пола, если не указаны другие размеры.
3. Точное месторасположение розеток в зоне кухни для подключения бытовой техники и иного уточнить на месте у производителей данной мебели.
4. Все высоты (от уровня готового пола-паркет/плитка) и размеры указаны до центра розеток/выключателей.
5. Выключатели и розетки устанавливаются на 200 мм. от косяков дверей/проемов, если не указаны другие размеры.
6. Точное месторасположение выключателей и розеток принимать после прочтения РАЗВЕРТКИ соответствующего помещения.
7. Группы розеток и выключателей устанавливать в одну рамку.
8. Розетки ВВГ нг 3х2,5
9. Кабель для плиты ВВГ нг 380V (4х6+1х4)


Условные обозначения:		
	Одноклавишный выключатель	5шт.
	Двухклавишный выключатель	7шт.

Экспликация помещений:		
№ п/п	Наименование помещения	S, м²
1	Коридор	16,2
2	Детская	15,8
3	Ванная	3,9
4	Спальня	13,6
5	Балкон	3,7
6	Гостиная	16,80
7	Санузел	1,40
8	Кухня	14,30
9	Балкон	4,30
Общая площадь (S) квартиры:		90м2
Высота потолка: 2740мм		
Высота дверных проемов: 2100мм		

Обозн.	Наименование	Кол-во
СП2	Спот встроенный (влагозащитный)	4
	Спот	6
	Софиты	17
	БРА	6
	Led лента	35п.м
	Трековый светильник	3
	Трековый светильник 500мм	20
	Люстра	1
	Плафон в балконе	1
	Люстра на кухню	1
	Светильник подвесной	1

ПРИМЕЧАНИЯ:
1. Все размеры указаны в миллиметрах.
2. На плане указаны проектные размеры.
3. Размеры по факту могут незначительно отличаться от проектных. Регулировать на месте.

Дизайн проект 90м2				Стадия	Лист	Листов
План привязки осветительных приборов к выключателям				АИ	6	16
Выполнил						
Проверил						

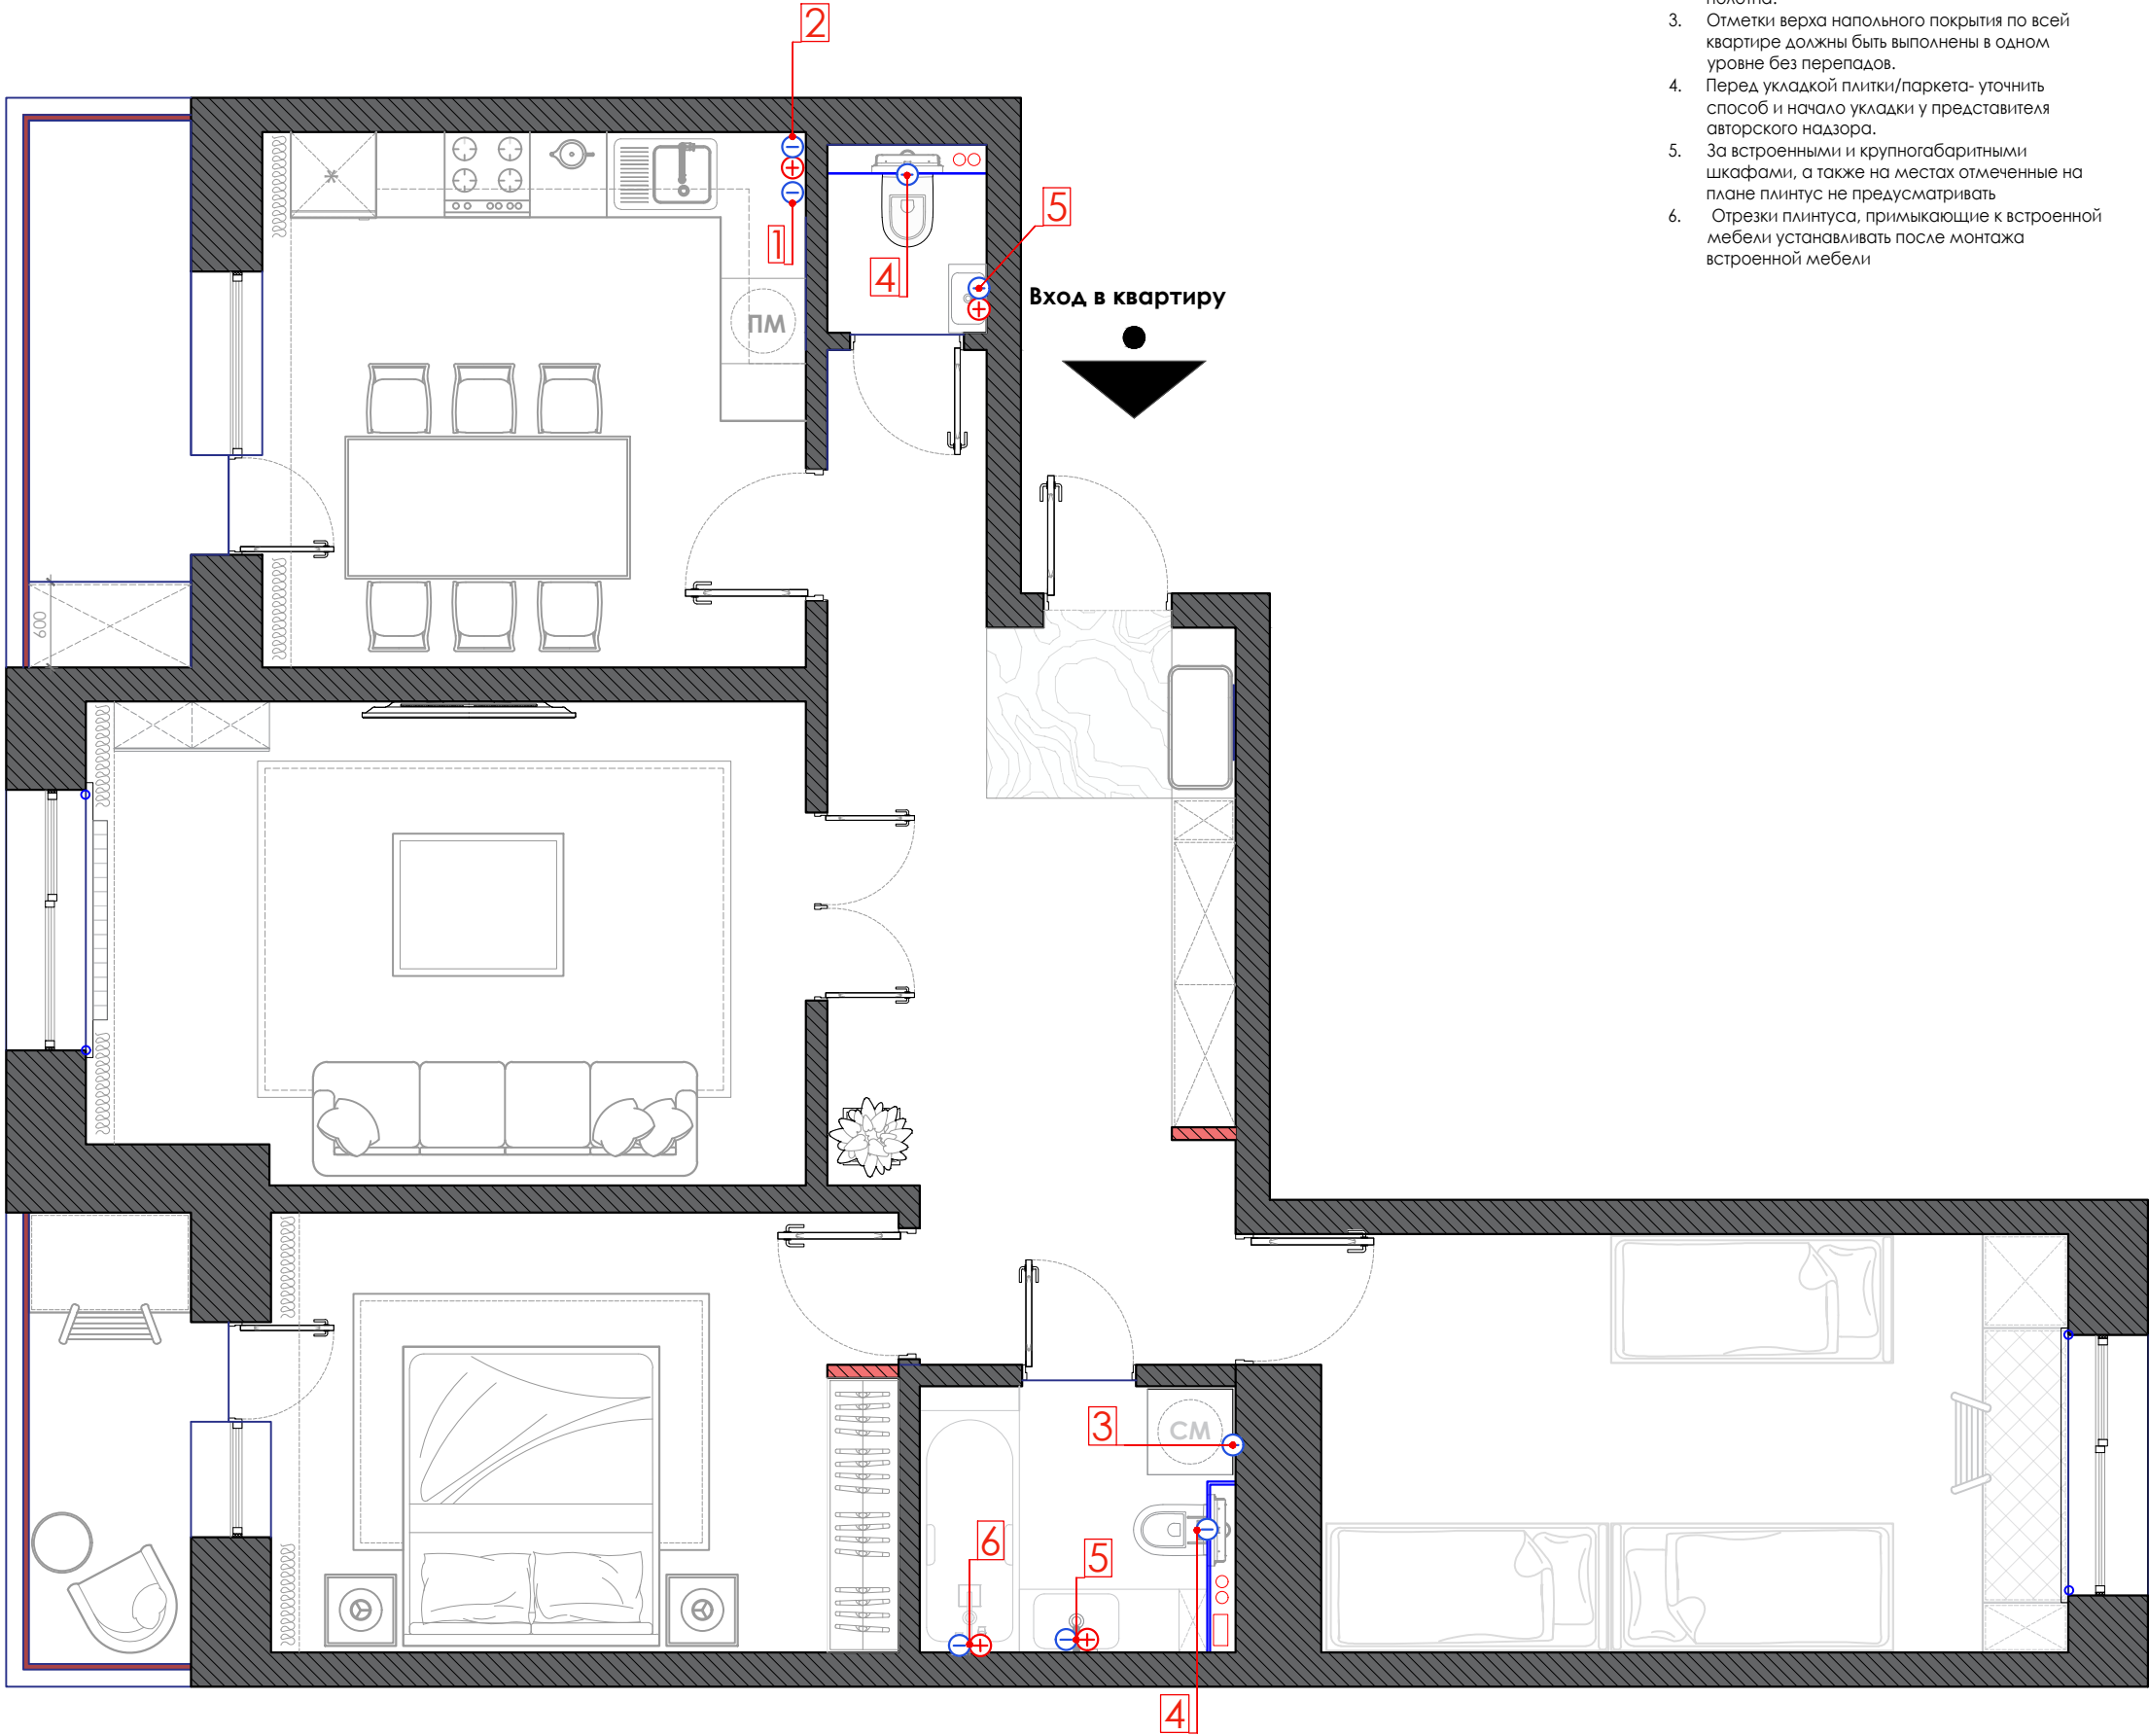


1. Все размеры указаны в миллиметрах.
2. Стык покрытий, попадающий в дверной проем предусмотреть под толщиной дверного полотна.
3. Отметки верха напольного покрытия по всей квартире должны быть выполнены в одном уровне без перепадов.
4. Перед укладкой плитки/паркета- уточнить способ и начало укладки у представителя авторского надзора.
5. За встроенными и крупногабаритными шкафами, а также на местах отмеченные на плане плинтус не предусматривать
6. Отрезки плинтуса, примыкающие к встроенной мебели устанавливать после монтажа встроенной мебели

Экспликация помещений:		
№ п/п	Наименование помещения	S, м²
1	Коридор	16,2
2	Детская	15,8
3	Ванная	3,9
4	Спальня	13,6
5	Балкон	3,7
6	Гостиная	16,80
7	Санузел	1,40
8	Кухня	14,30
9	Балкон	4,30
Общая площадь (S) квартиры:		90м2
Высота потолка: 2740мм		
Высота дверных проемов: 2100мм		

Спецификация сантехнических приборов	
2.Гостевой санузел	
1	Посудомойка Н=300
2	Мойка Н=600
3	Стиральная машина Н=300
4	Унитаз Н=220
5	Умывальник Н=220
6	Душевой гарнитур Н=1000
Условные обозначения:	
⊕	Горячая вода
⊖	Холодная вода

ПРИМЕЧАНИЯ:
1. Все размеры указаны в миллиметрах.
2. На плане указаны проектные размеры.
3. Размеры по факту могут незначительно отличаться от проектных. Регулировать на месте.

				Дизайн проект 90м2	Стадия	Лист	Листов
					АИ	7	16
Выполнил				План сантехнических приборов			
Проверил							

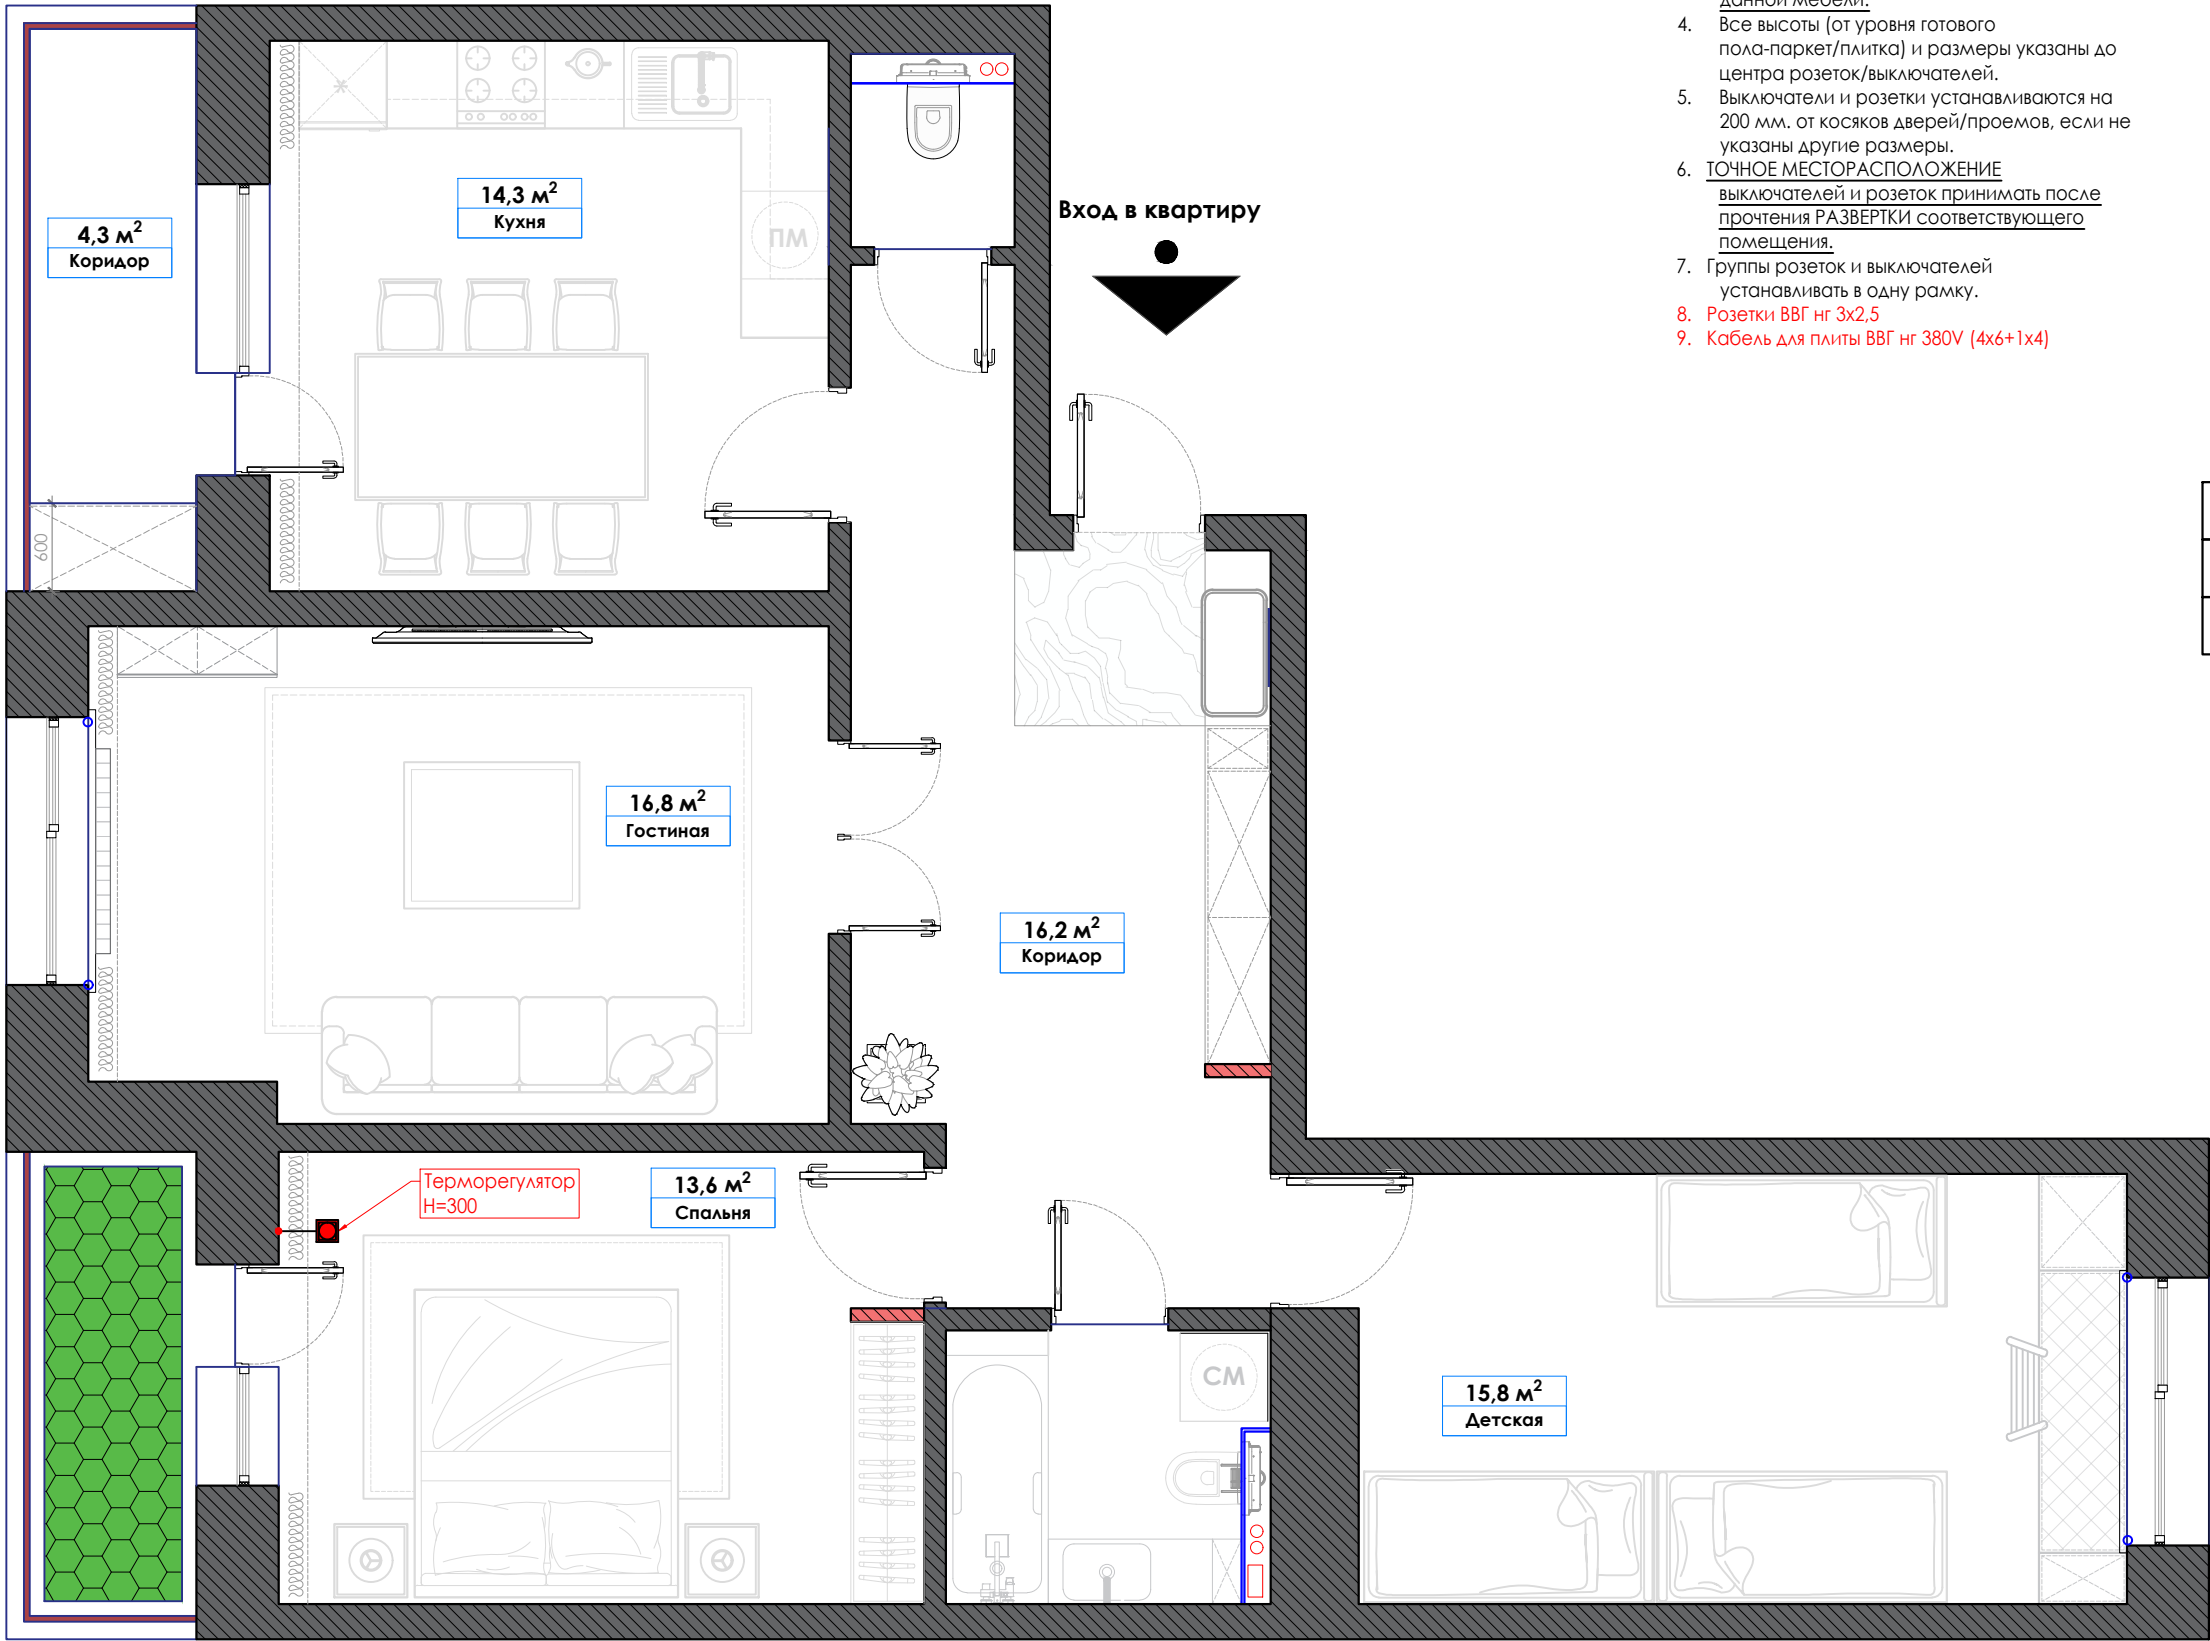

1.

Все размеры указаны в миллиметрах.
2.

Розетки устанавливаются на высоте 300 мм. от пола, если не указаны другие размеры.
3.

Точное месторасположение розеток в зоне кухни для подключения бытовой техники и иного уточнить на месте у производителей данной мебели.
4.

Все высоты (от уровня готового пола-паркет/плитка) и размеры указаны до центра розеток/выключателей.
5.

Выключатели и розетки устанавливаются на 200 мм. от косяков дверей/проемов, если не указаны другие размеры.
6.

ТОЧНОЕ МЕСТОРАСПОЛОЖЕНИЕ выключателей и розеток принимать после прочтения РАЗВЕРТКИ соответствующего помещения.
7.

Группы розеток и выключателей устанавливать в одну рамку.
8.

Розетки ВВГ нг 3х2,5
9.

Кабель для плиты ВВГ нг 380V (4х6+1х4)

Экспликация помещений:		
№ п/п	Наименование помещения	S, м²
1	Коридор	16.2
2	Детская	15.8
3	Ванная	3.9
4	Спальня	13.6
5	Балкон	3.7
6	Гостиная	16,80
7	Санузел	1,40
8	Кухня	14,30
9	Балкон	4,30
Общая площадь (S) квартиры:		90м2
Высота потолка: 2740мм		
Высота дверных проемов: 2100мм		

Спецификация материалов		
1.Балкон	теплый пол электрический	2.7 м2
	Терморегулятор	1шт.

ПРИМЕЧАНИЯ:

1.

Все размеры указаны в миллиметрах


2.

На плане указаны проектные размеры.

3.

Размеры по факту могут незначительно отличаться от проектных. Регулировать на месте.

				Дизайн проект 90м2	Стадия	Лист	Листов
					АИ	8	16
Выполнил				План теплого пола			
Проверил							

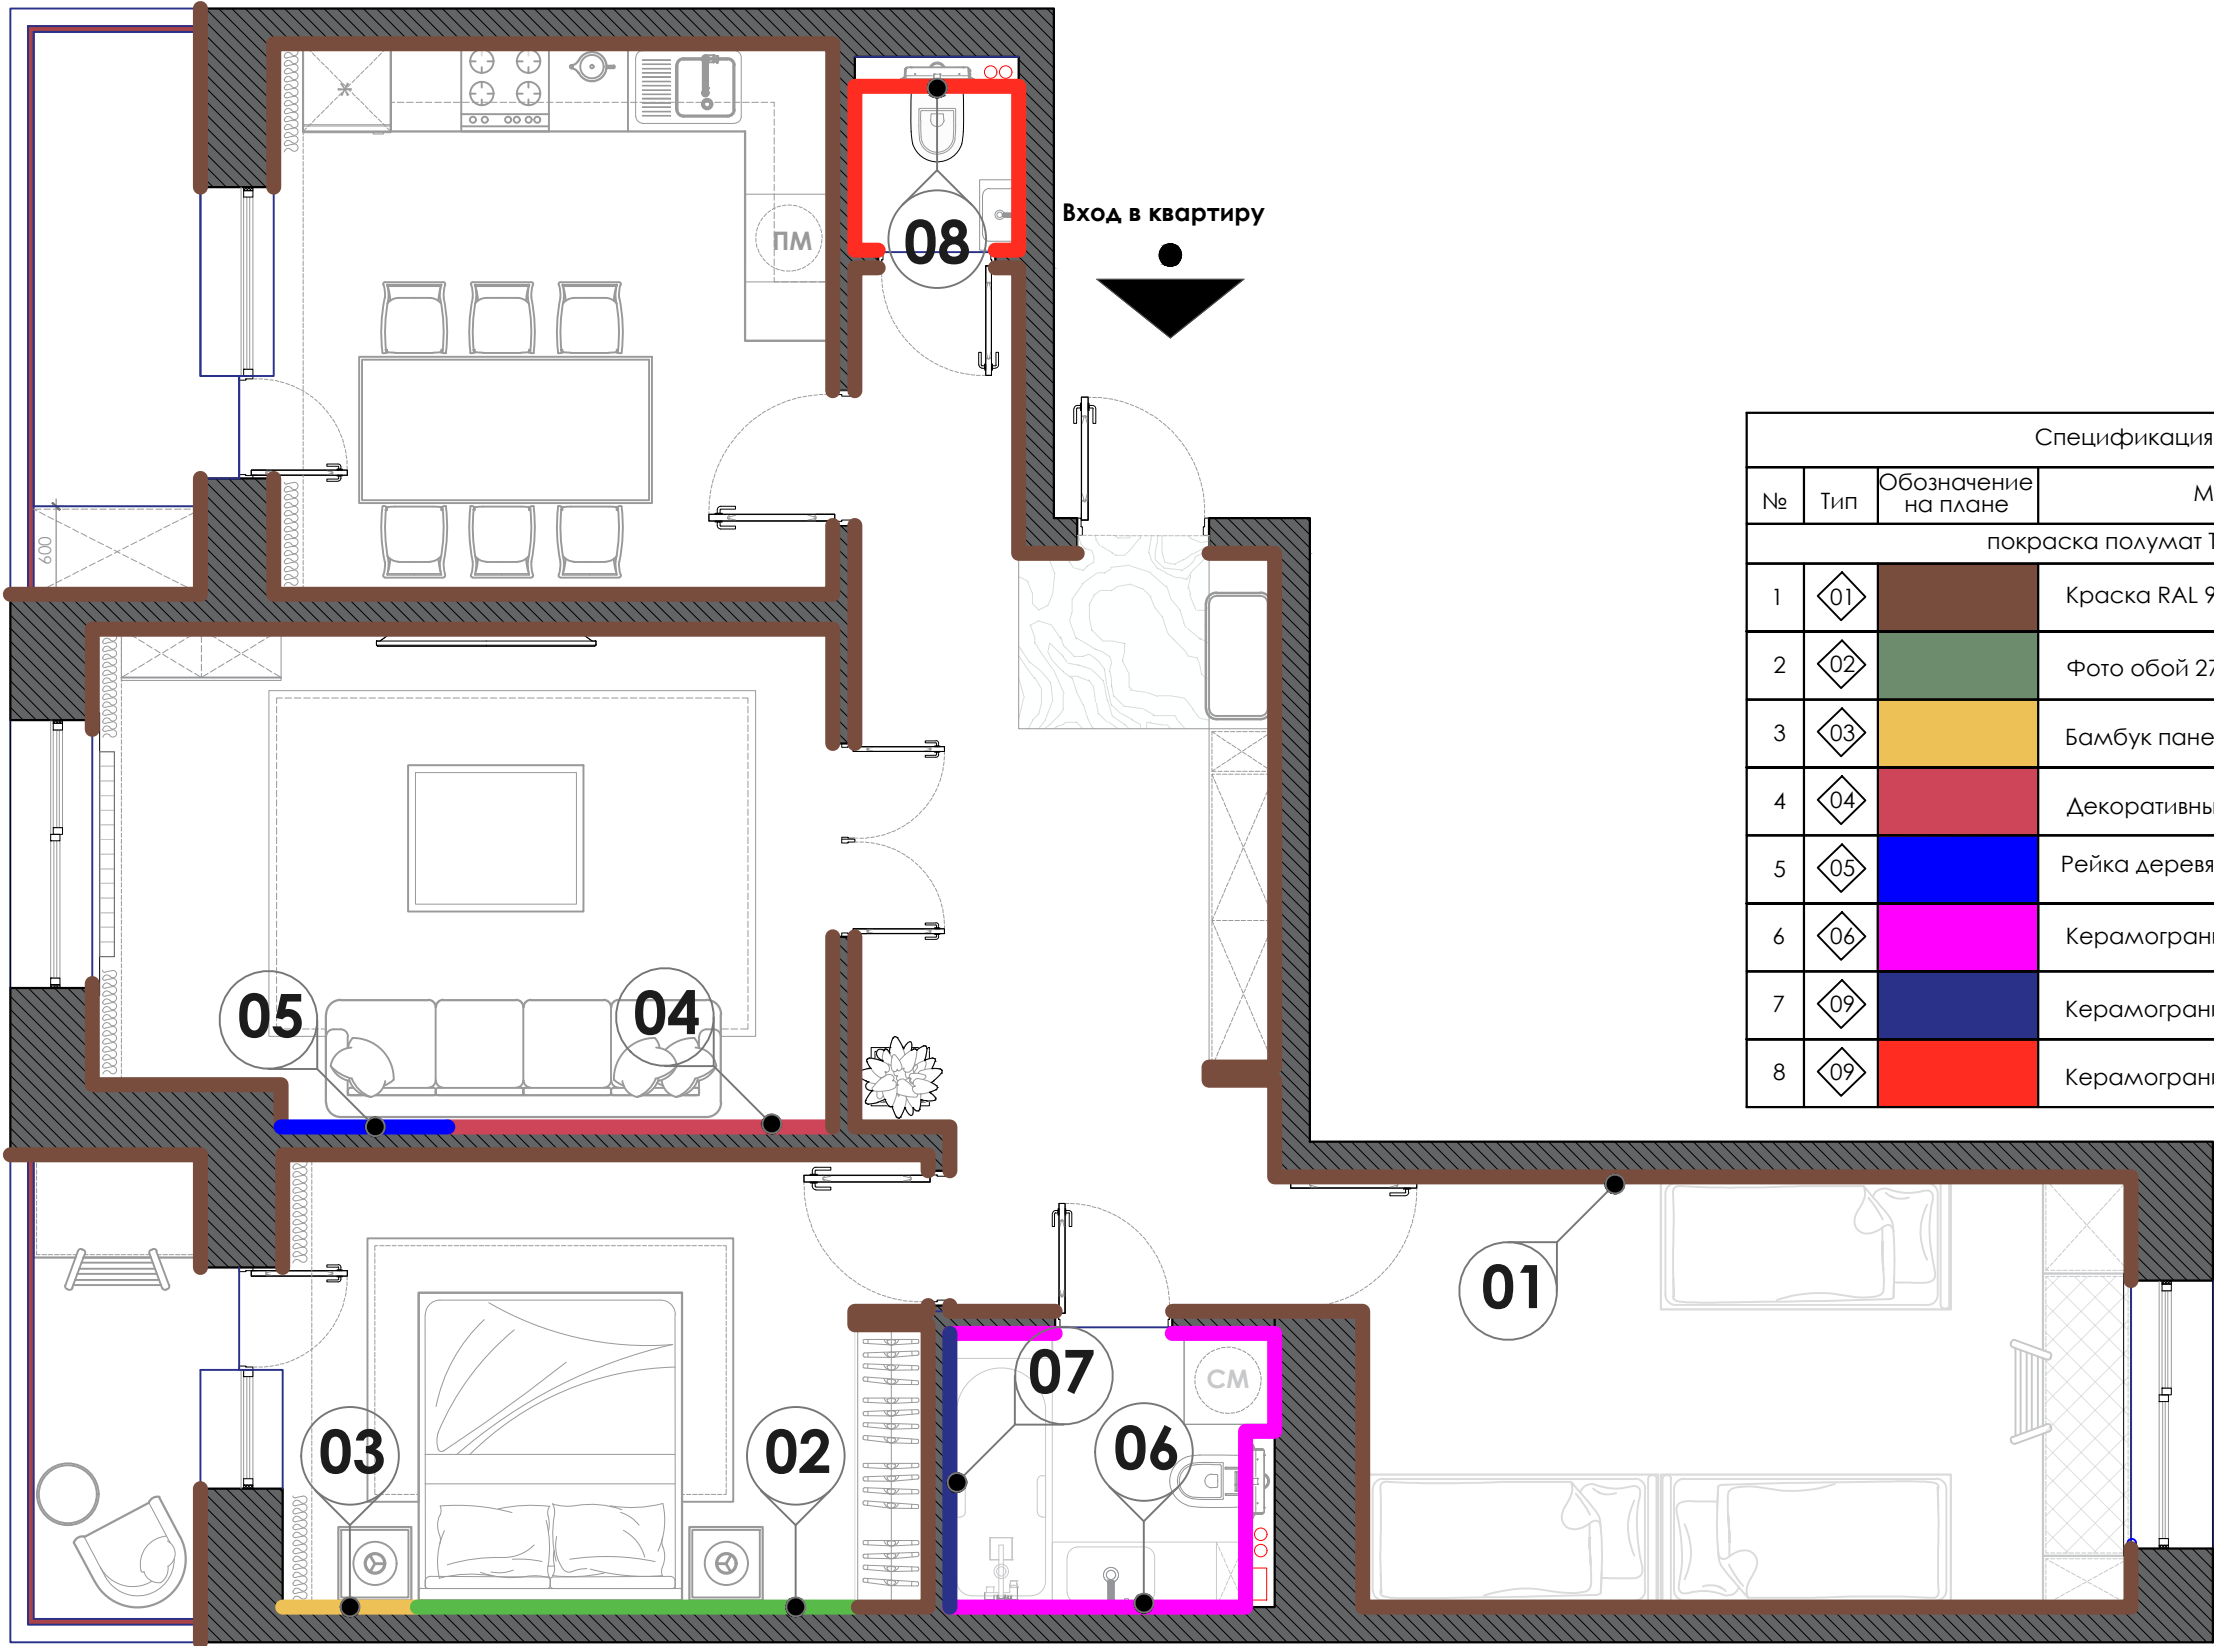


Экспликация помещений:		
№ п/п	Наименование помещения	S, м²
1	Коридор	16.2
2	Детская	15.8
3	Ванная	3.9
4	Спальня	13.6
5	Балкон	3.7
6	Гостиная	16,80
7	Санузел	1,40
8	Кухня	14,30
9	Балкон	4,30
Общая площадь (S) квартиры:		90м2
Высота потолка: 2740мм		
Высота дверных проемов: 2100мм		

Спецификация материалов					
№	Тип	Обозначение на плане	Материал	S,м²	
покраска полумат Tikkurila за 2 раза					
1	01		Краска RAL 9016	260м2	
2	02		Фото обой 2780x2650мм	7,1 м2	
3	03		Бамбук панель	2,6 м2	
4	04		Декоративный панель (крашенный)	7.1 м2	
5	05		Рейка деревянная 20x17x2650	2,4м2	
6	06		Керамогранит 1200*600	10м2	
7	09		Керамогранит 1200*600	3,5 м2	
8	09		Керамогранит 1200*600	8,2 м2	

ПРИМЕЧАНИЯ:
1. Все размеры указаны в миллиметрах
2. На плане указаны проектные размеры.
3. Размеры по факту могут незначительно отличаться от проектных. Регулировать на месте.

				Дизайн проект 90м2	Стадия	Лист	Листов
					АИ	9	16
Выполнил				Маркировка стен			
Проверил							

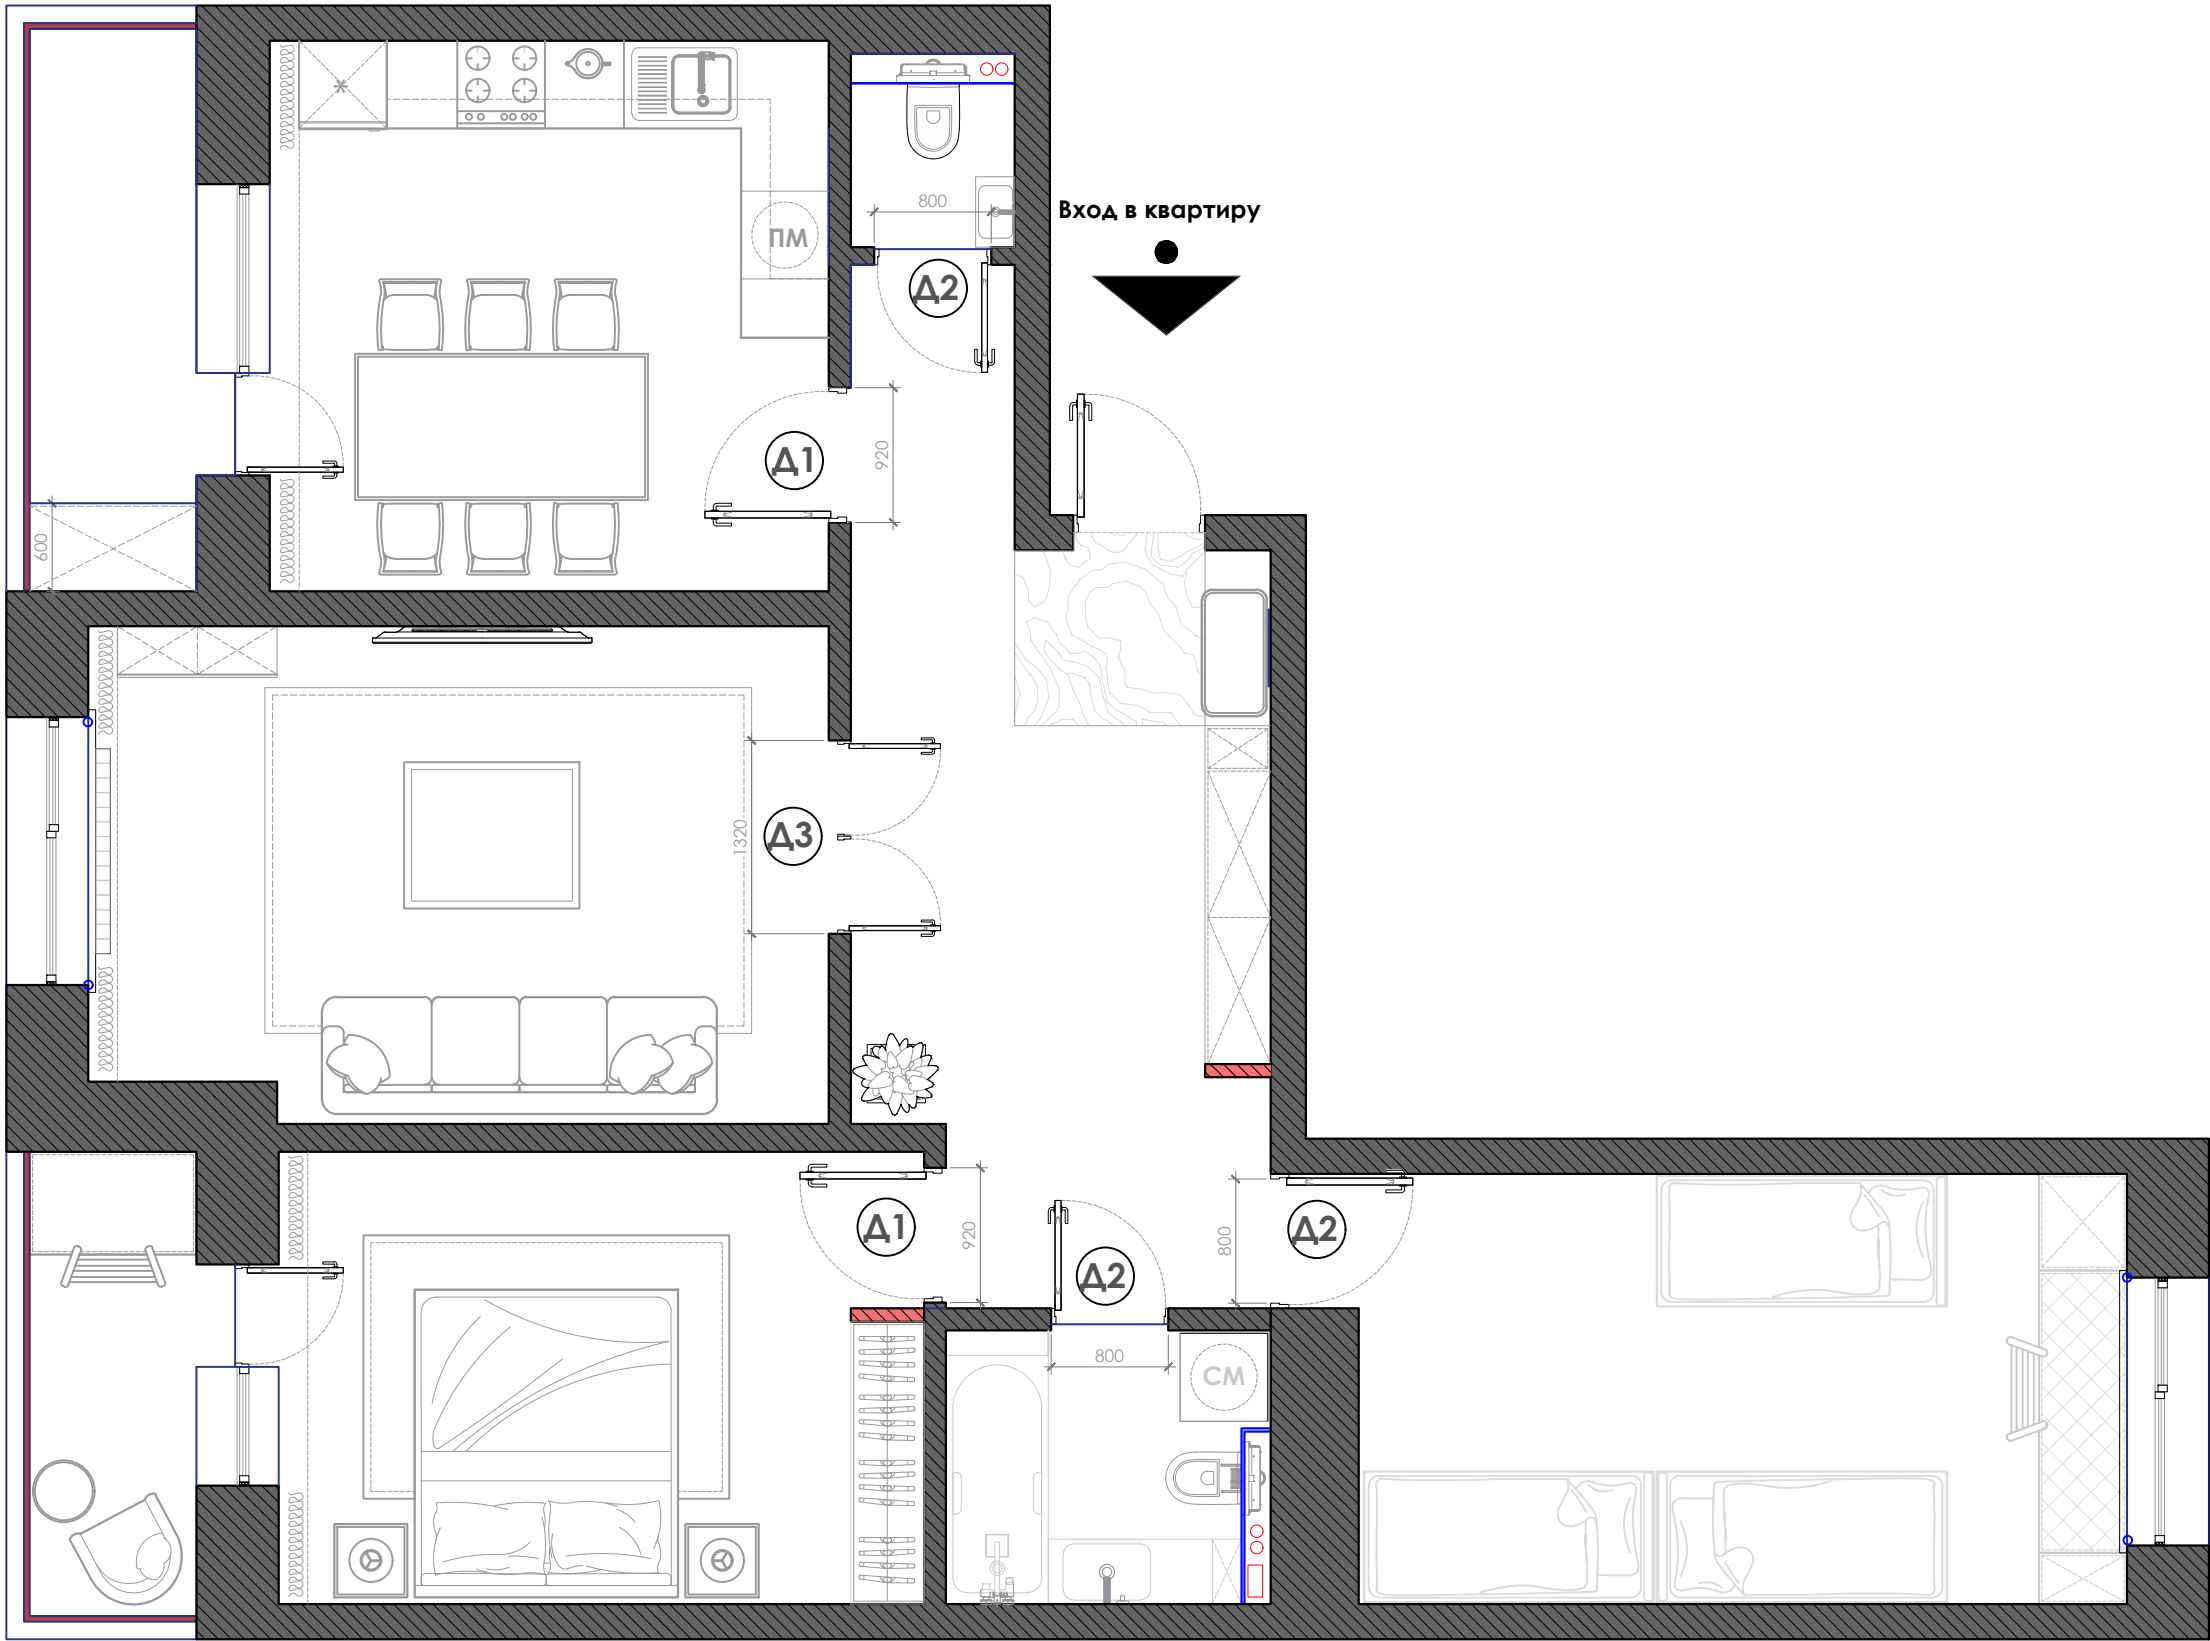


Экспликация помещений:		
№ п/п	Наименование помещения	S, м²
1	Коридор	16.2
2	Детская	15.8
3	Ванная	3.9
4	Спальня	13.6
5	Балкон	3.7
6	Гостиная	16.80
7	Санузел	1.40
8	Кухня	14.30
9	Балкон	4.30
Общая площадь (S) квартиры:		90м2
Высота потолка: 2740мм		
Высота дверных проемов: 2100мм		

Спецификация дверей		
Δ1	Полотно В2000Ш800	2шт.
Δ2	Полотно В2000Ш700	2шт.
Δ3	Полотно В2000Ш1220	1шт.

ПРИМЕЧАНИЯ:



- Все размеры указаны в миллиметрах
- На плане указаны проектные размеры.
- Размеры по факту могут незначительно отличаться от проектных. Регулировать на месте.

				Дизайн проект 90м2	Стадия	Лист	Листов
					АИ	9	16
Выполнил				Спецификация дверей			
Проверил							

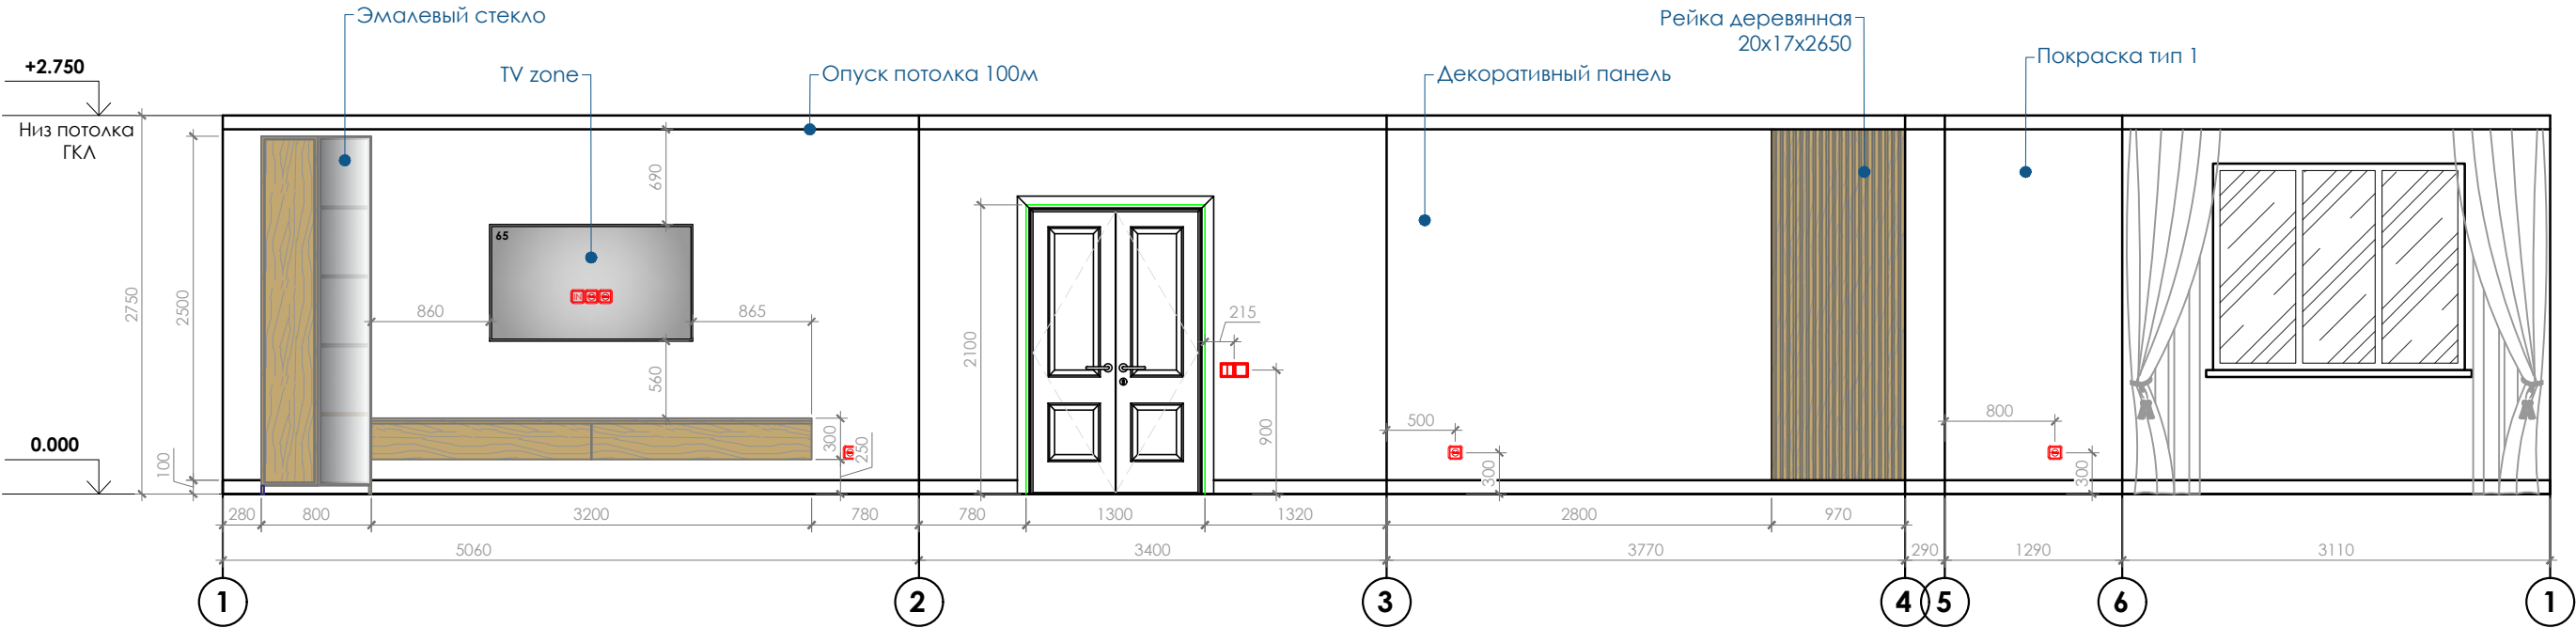


Спецификация материалов		
Обозначение	Материал	S, м²
	Покраска тип 4 NCS S 1002-B	260м2
	Декоративный панель (крашеный)	7,1м2
	Рейка деревянная 20x17x2650	2,4м2


Фрагмент плана

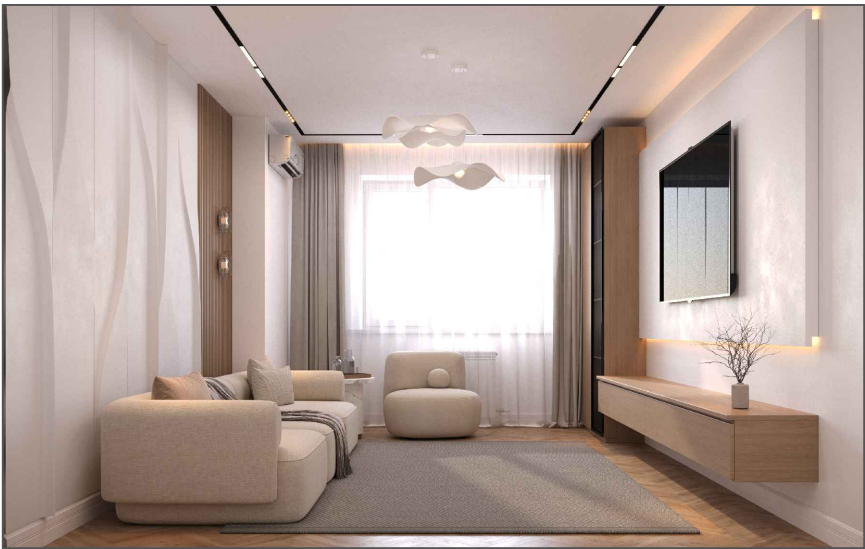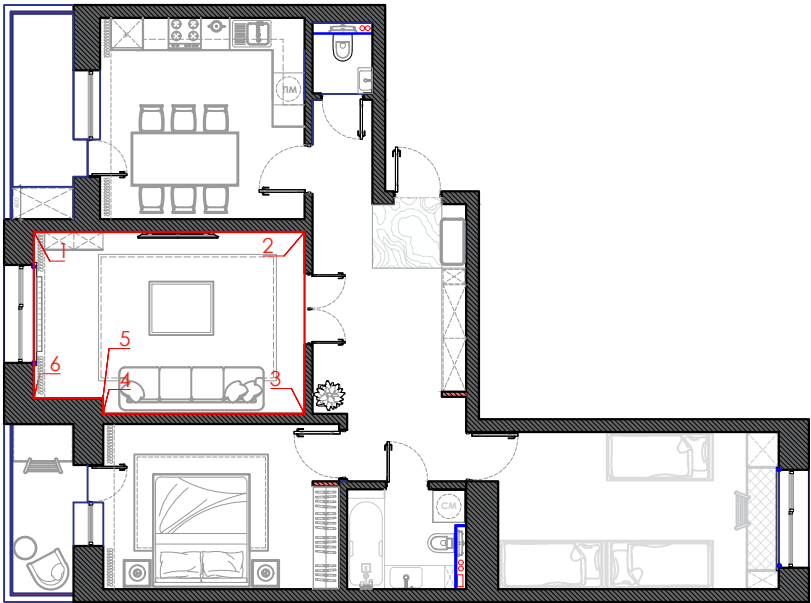


				Дизайн проект 90м2	Стадия	Лист	Листов
					АИ	11	16
Выполнил				Развертка стен гостиной			
Проверил							

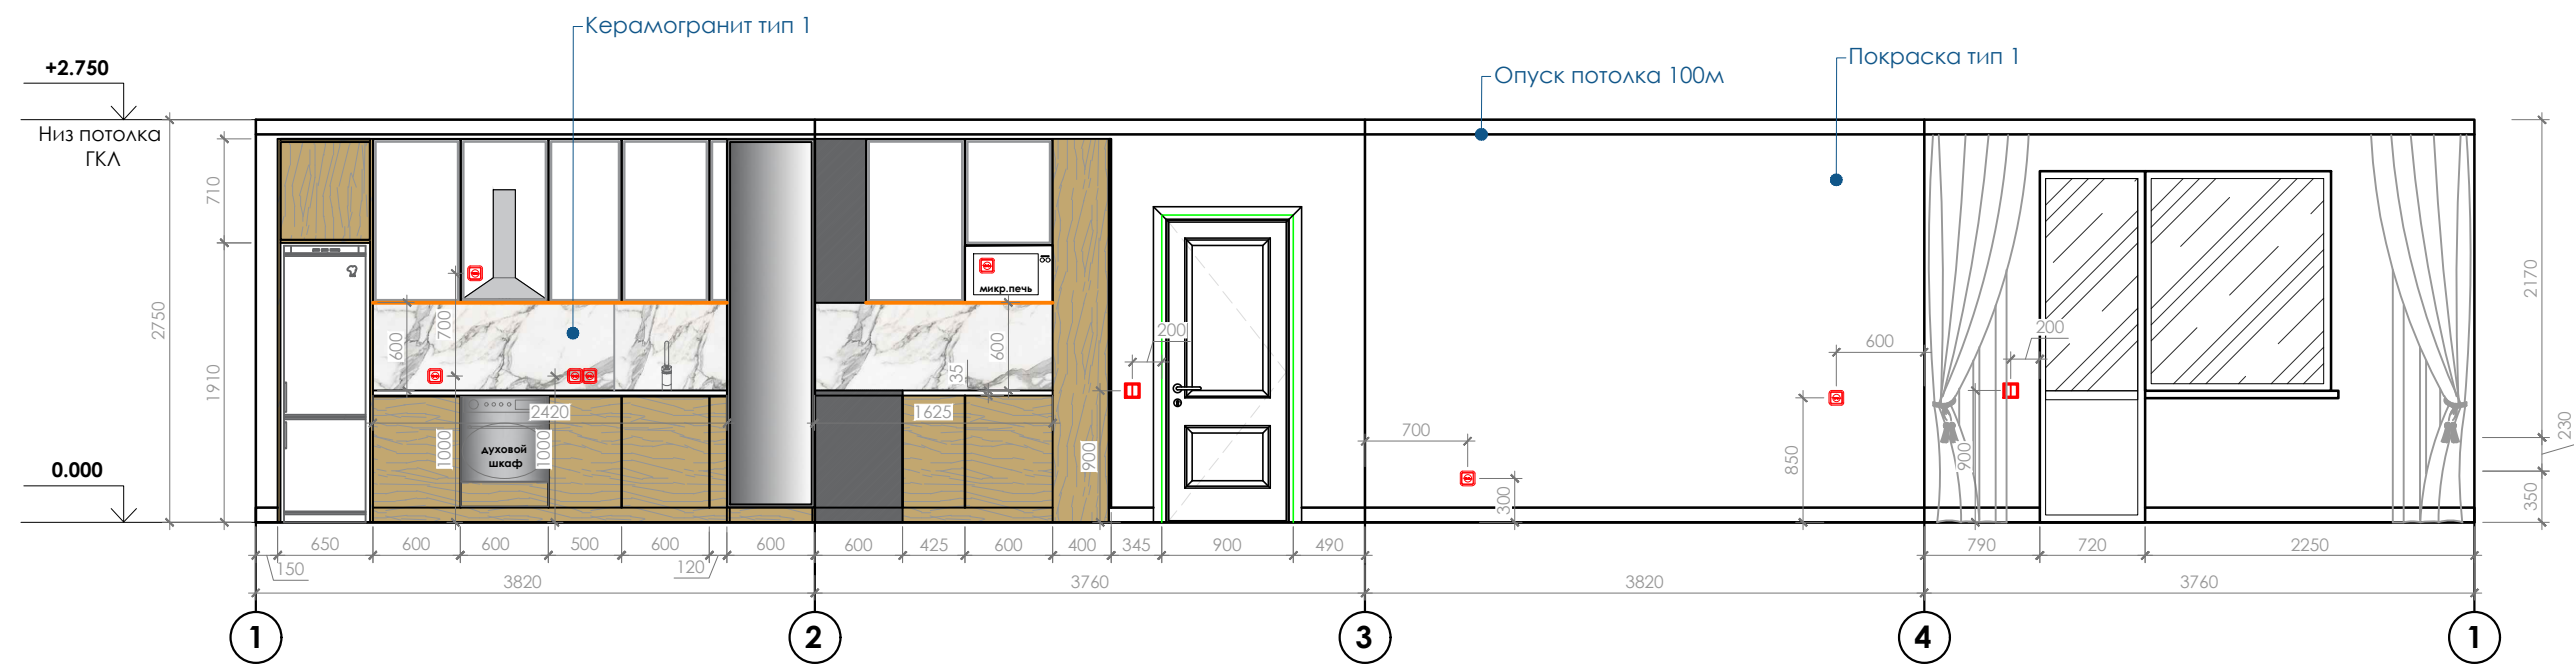

Фрагмент плана

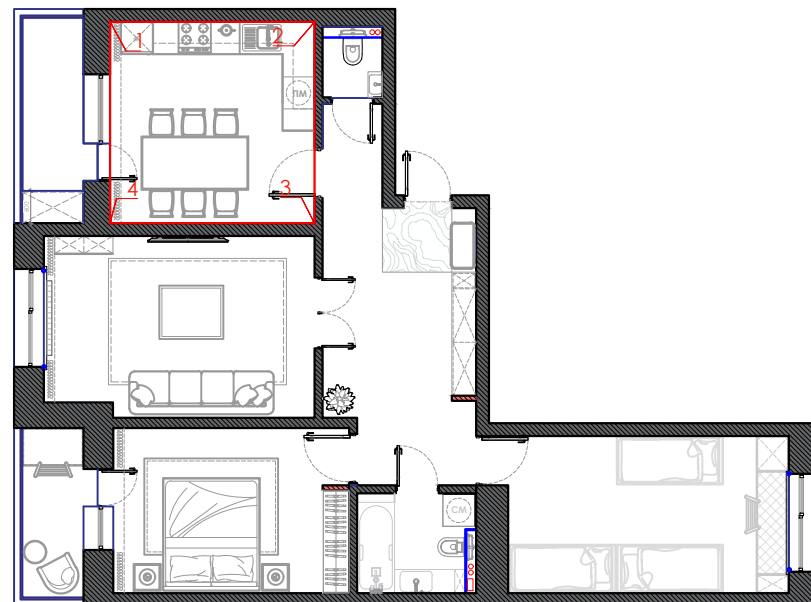


Спецификация материалов					Дизайн проект 90м2			Стадия	Лист	Листов
Обозначение	Материал	S, м²	Выполнил	Проверил				АИ	12	16
	Покраска тип 4 NCS S 1002-B	260м²								
	Керамогранит тип 1 1200x600	4шт.								
					Развертка стен					

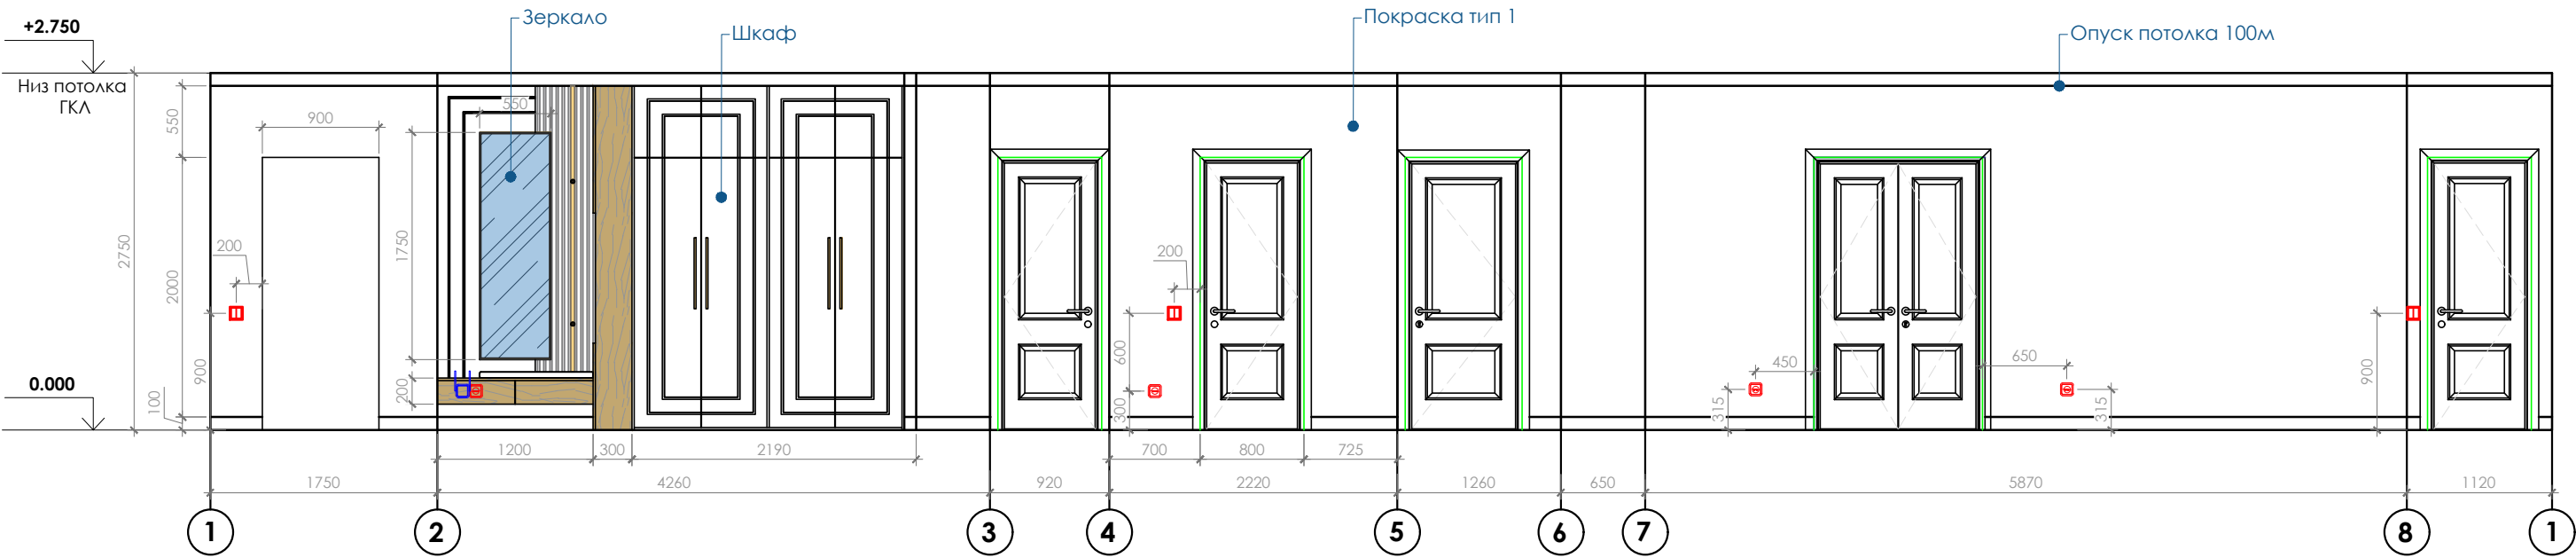


Спецификация материалов		
Обозначение	Материал	S,м²
	Покраска тип 4 NCS S 1002-B	260м²
	Керамогранит тип 1 1200x600	5шт.

Фрагмент плана

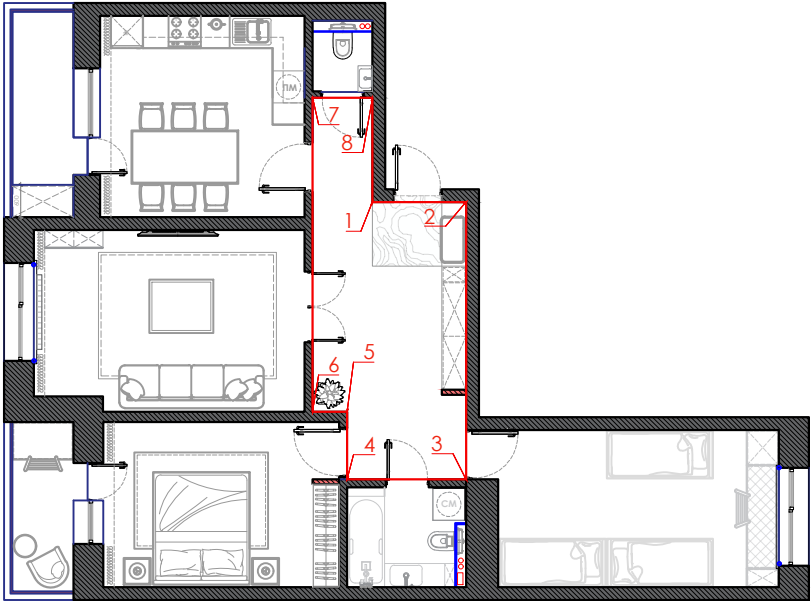


				Дизайн проект 90м²	Стадия	Лист	Листов
					АИ	13	16
Выполнил				Развертка стен			
Проверил							

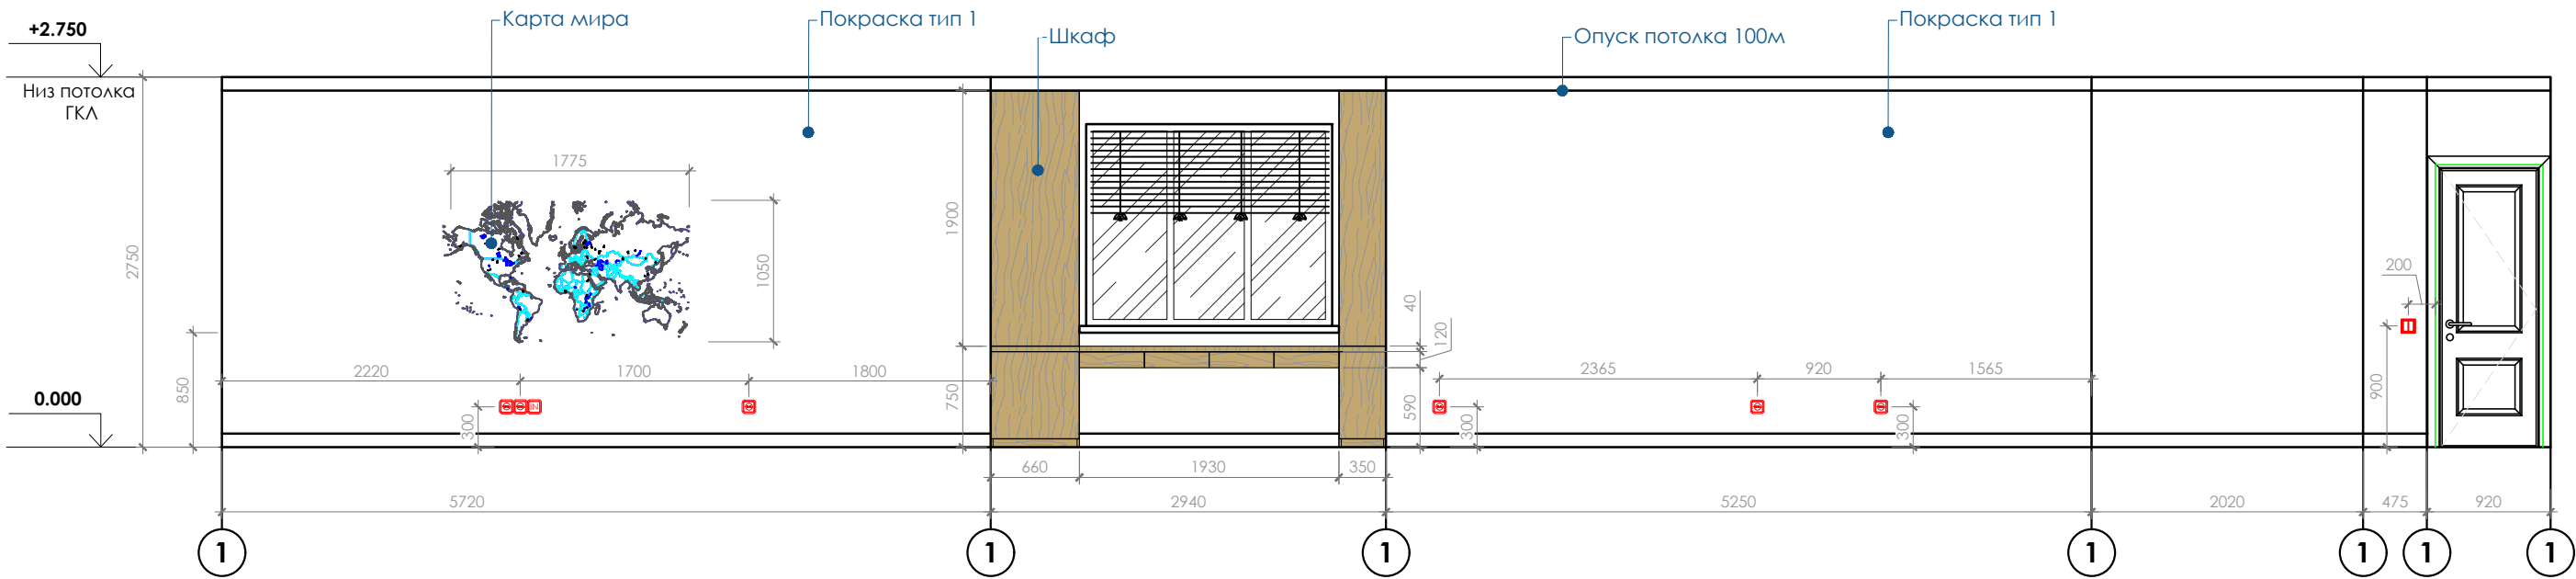


Спецификация материалов		
Обозначение	Материал	S,м²
	Краска RAL 9016	260м2

Фрагмент плана


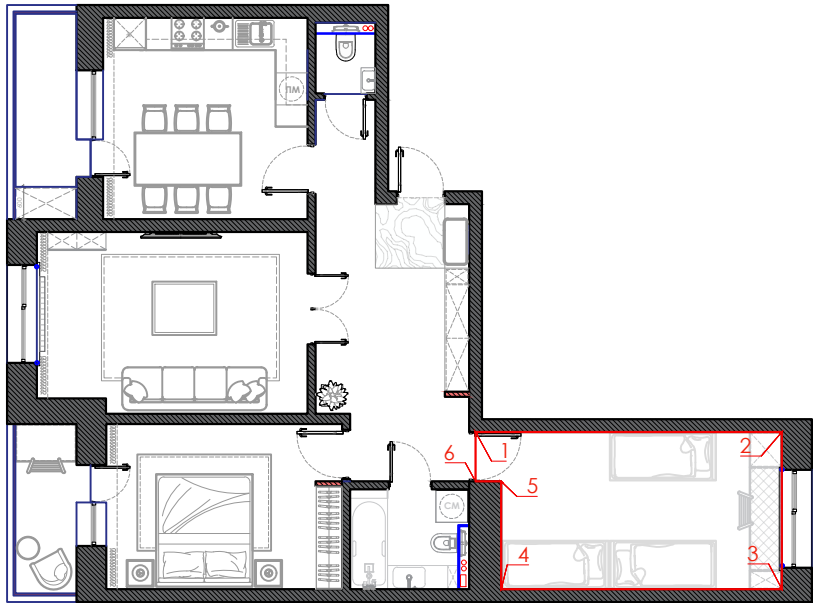


				Дизайн проект 90м2	Стадия	Лист	Листов
					АИ	14	16
Выполнил				Развертка стен			
Проверил							

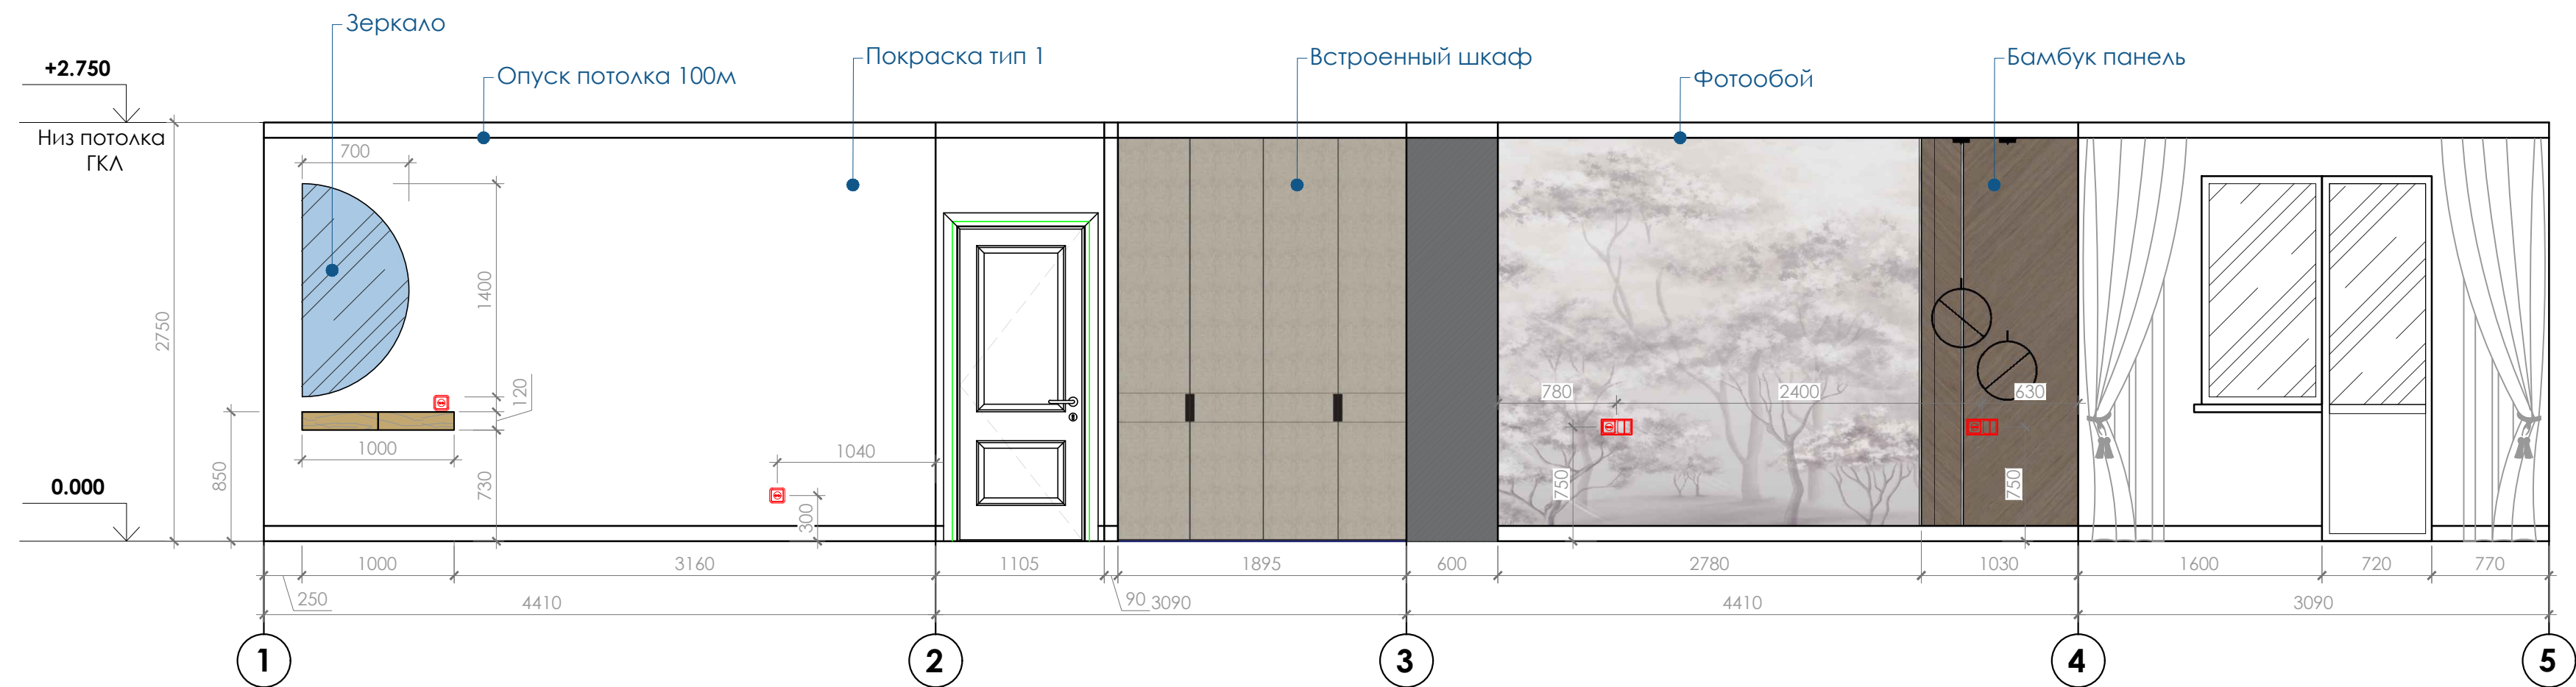


Спецификация материалов		
Обозначение	Материал	S, м²
	Бамбук панель	2,6 м2
	Фото обой 2780x2650мм	7,1м2
	Краска RAL 9016	260м2

Фрагмент плана

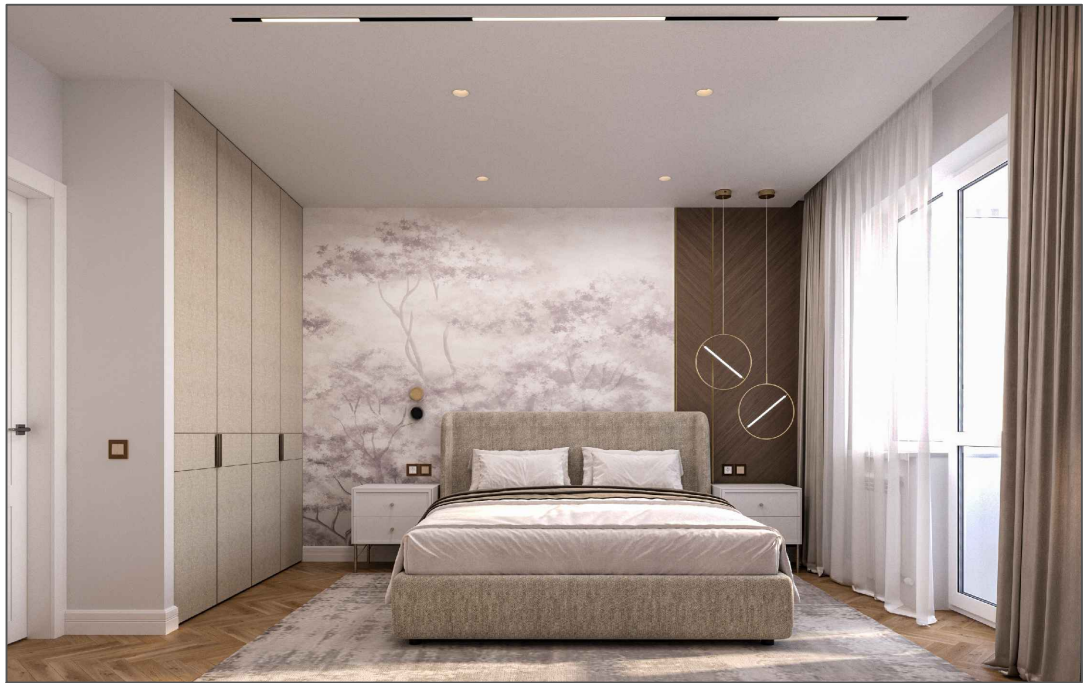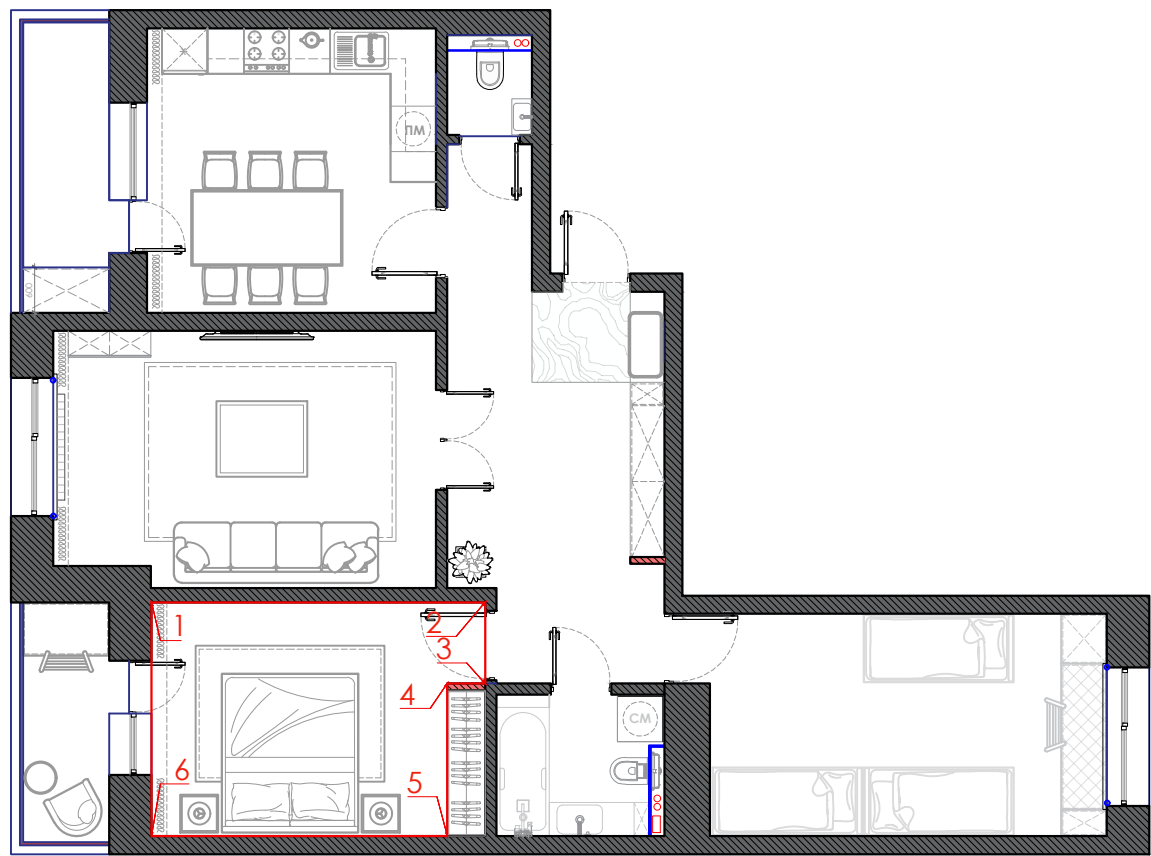




				Дизайн проект 90м2	Стадия	Лист	Листов
					АИ	15	16
Выполнил				Развертка стен			
Проверил							

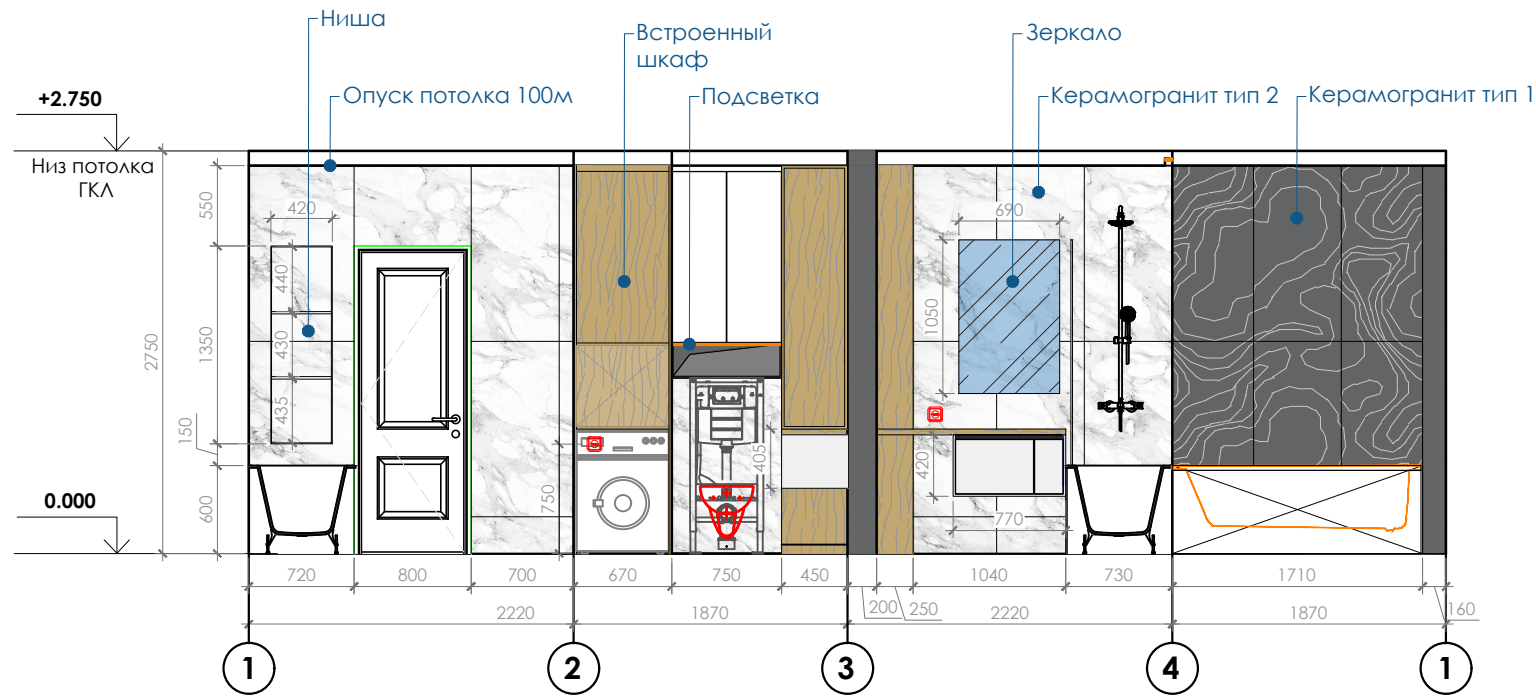

Спецификация материалов		
Обозначение	Материал	S, м²
	Керамогранит тип 1 1200x600	6 шт.
	Керамогранит тип 2 1200x600	15 шт.
	Покраска тип 4 NCS S 1002-B	0.9 м²



Фрагмент плана

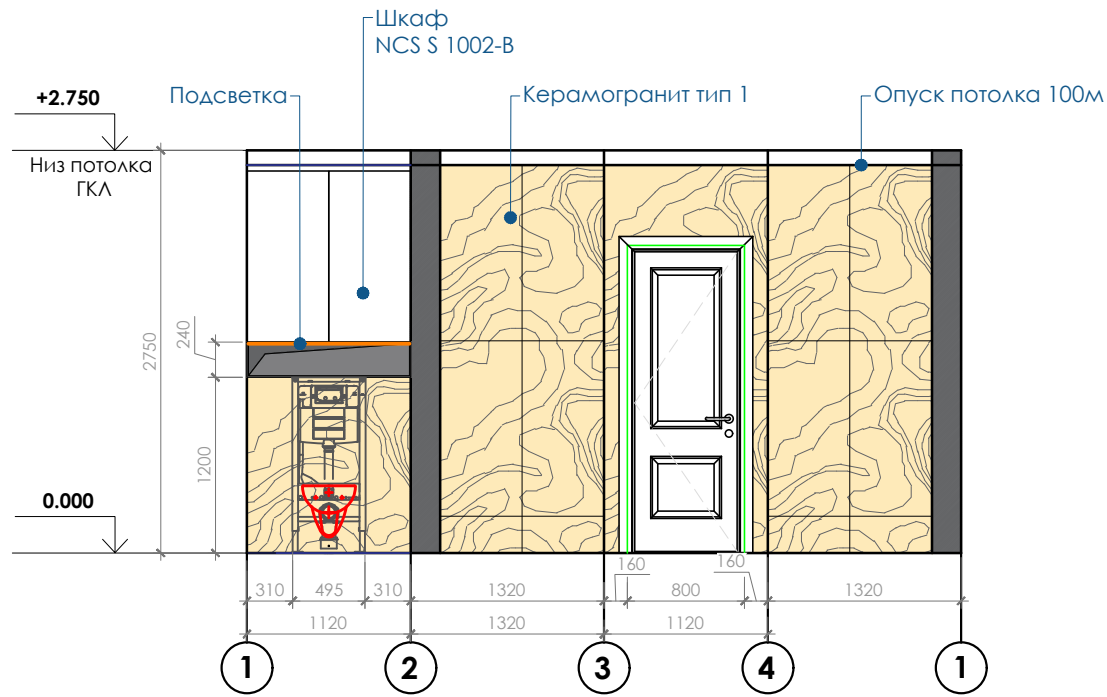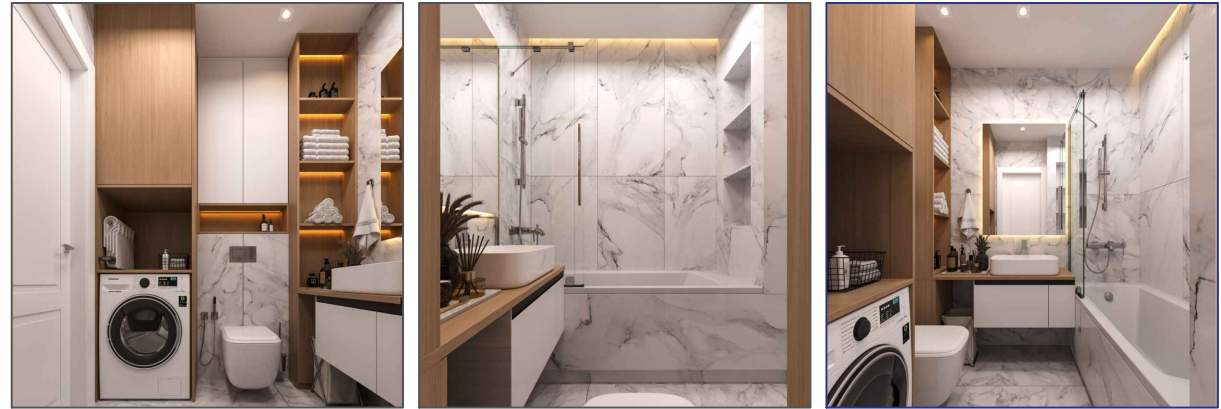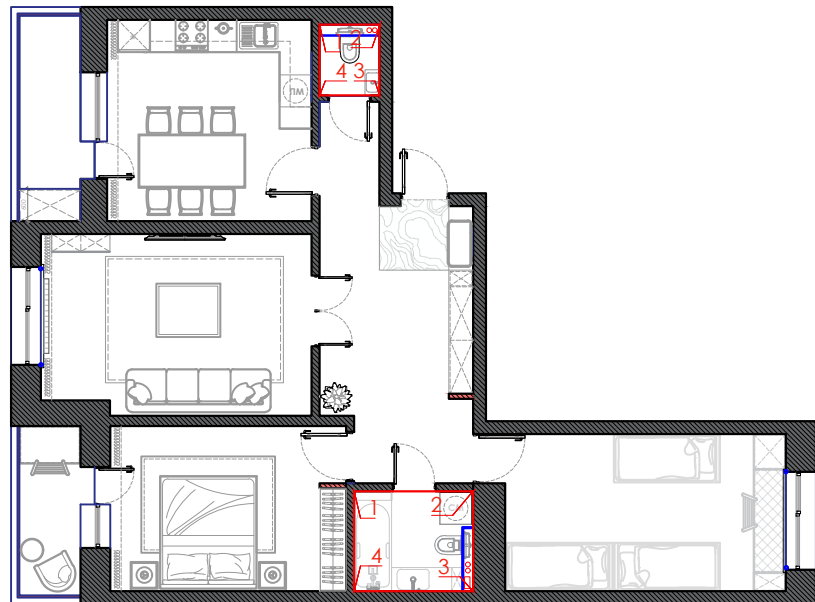

Спецификация материалов		
Обозначение	Материал	S, м²
	Покраска тип 4 NCS S 1002-B	1.3 м²
	Керамогранит тип 1 1200x600	13 шт.

				Дизайн проект 90м2	Стадия	Лист	Листов
					АИ	16	16
Выполнил				Развертка стен			
Проверил							