

РАБОЧИЙ ПРОЕКТ

Пакет: Comfort Smart / 231 |
Comfort База / 114

ID 9829
ЖК Shabyt

Пояснительная записка

1. Общие данные

Настоящий проект разработан отделом проектирования компании ТОО “Smart Remont”.
Трехкомнатная квартира, общей площадью 93,94 кв.м.
предназначена для постоянного проживания. Пакет Comfort Smart / 231 | Comfort База / 114.

2. Водоснабжение и канализация

Уклон канализационной трубы должен соответствовать 2–3 градусам.
Зона унитаза указана в проекте.
Предусмотреть доступ к счетчикам.
Предусмотреть люк для доступа к ванной.

3. Электромонтажные работы

Все электромонтажные работы должны быть выполнены согласно СНиП и ПУЭ.
Кабельную разводку использовать предоставленную застройщиком.
Розетки установить на высоте 300 мм. (если иное не указано в проекте).
Розетки для ТВ зоны установить на высоте 1500 мм. (если не указано иное в проекте)
Розетки на фартуке установить на высоте 1100 мм. (если иное не указано в проекте).
Выключатели установить на высоте – 900 мм. (если иное не указано в проекте).


4. Отделочные работы

Объект поступает в работу в улучшенной черновой отделке.
Обработку стен выполнить в соответствии с схемой на листе отделке стен.
Укладку ламината и кафельной плитки выполнить в соответствии со схемой на листе Плана полов.

Проектные размеры от фактических могут отличаться, смотреть по факту.
При укладке кафеля, при отклонении проектных размеров от фактических, предусмотреть
соблюдение центровки кафеля и пропорции подрезок кафеля.
Все высотные размеры в проекте указаны от уровня чистого пола.

Ведомость чертежей	
Титульный лист	1
Пояснительная записка	2
Предремонтное состояние объекта	3
Обмерный план	4
План демонтажа и монтажа	5
План расстановки мебели	6
План сантехнического оборудования	7
План потолка	8
План пола	9
План теплого пола	10
План освещения	11
План расстановки розеток	12
План отделки стен	13
План развертки стен ванной 1 часть	14
План развертки стен ванной 2 часть	15
План развертки стен санузла 1 часть	16
План развертки стен санузла 2 часть	17
План развертки фартука кухни	18

Экспликация помещений до монтажных работ		
№	Наименование помещения	Площадь, м²
1	Прихожая	13,61
2	Гостиная	21,55
3	Кухня	15,37
4	Спальня	16,57
5	Спальня 2	13,32
6	Ванная	4,52
7	Санузел	2,75
8	Гардеробная	2,5
9	Балкон	3,75
Рабочий проект		
ЖК Shabyt	Лист	Листов
	2	18
Пояснительная записка		

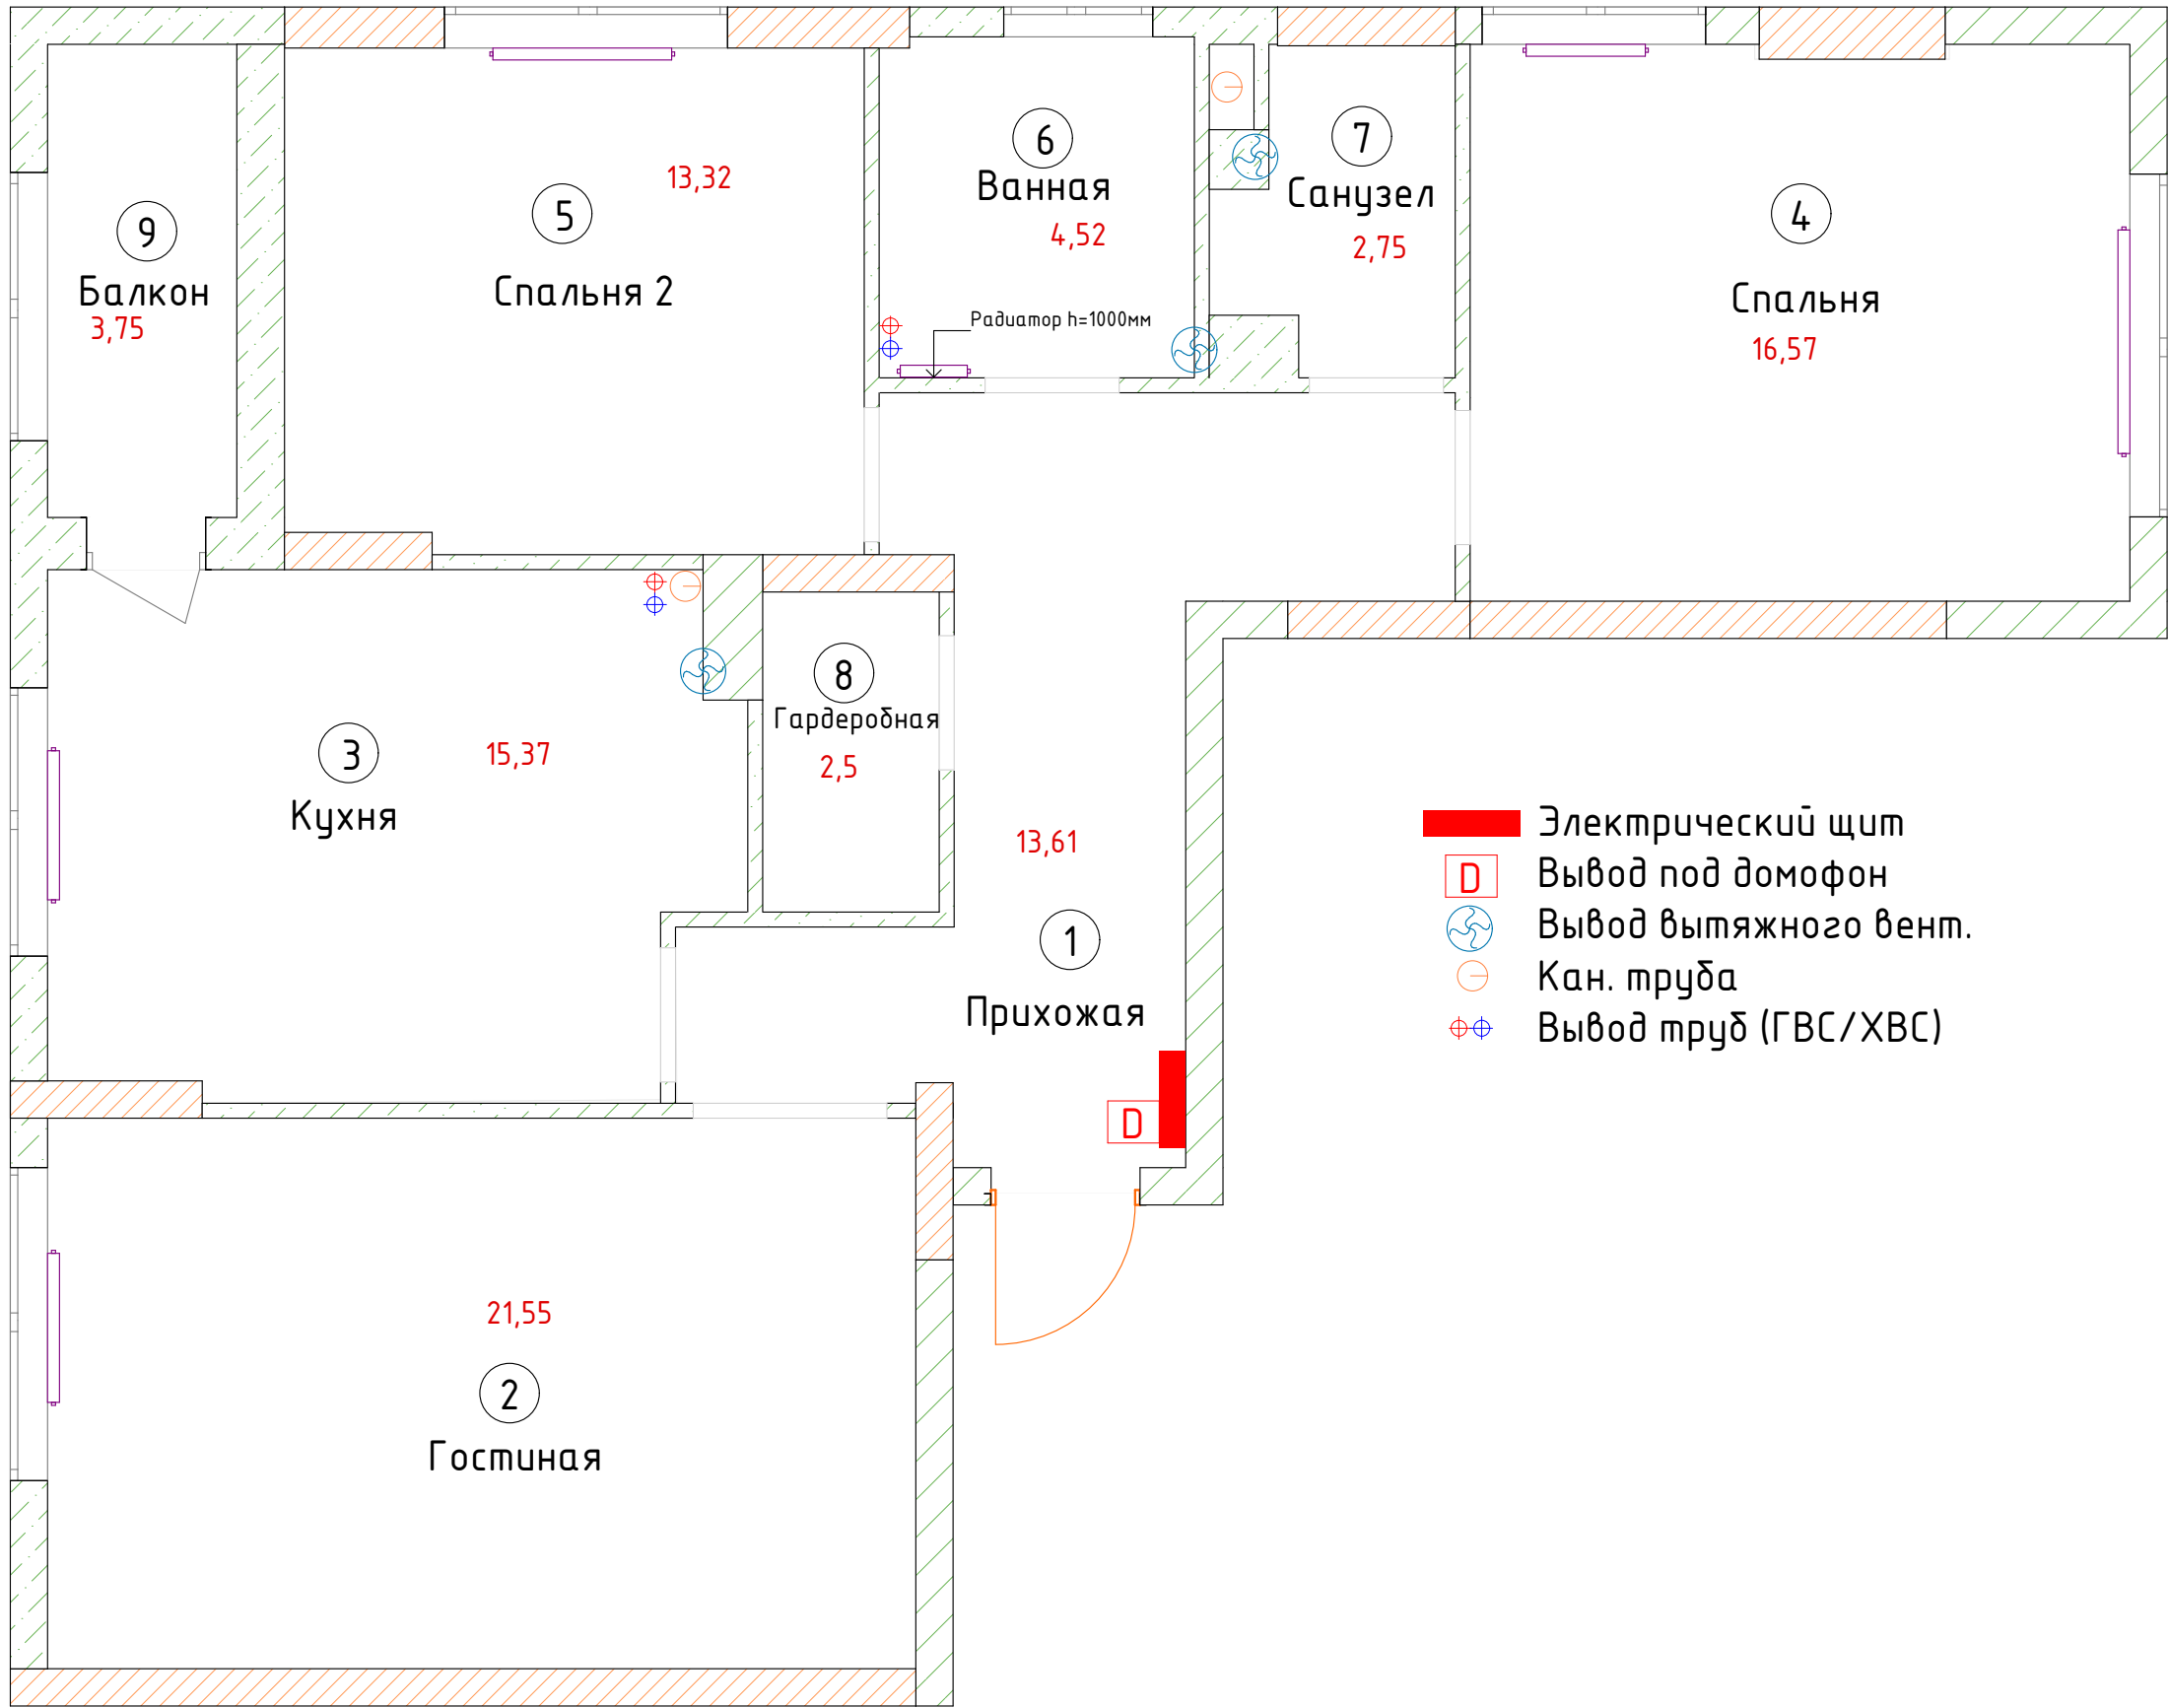


- Электрический щит
- Вывод под домофон
- Вывод вытяжного вент.
- Кан. труба
- Вывод труб (ГВС/ХВС)

Экспликация помещений до монтажных работ		
№	Наименование помещения	Площадь, м²
1	Прихожая	13,61
2	Гостиная	21,55
3	Кухня	15,37
4	Спальня	16,57
5	Спальня 2	13,32
6	Ванная	4,52
7	Санузел	2,75
8	Гардеробная	2,5
9	Балкон	3,75

- Монолит 400мм
- Газоблок 200мм
- Газоблок 100мм
- ГКЛ 100мм

Рабочий проект		
ЖК Shabyt	Лист	Листов
	3	18
Предремонтное состояние объекта		

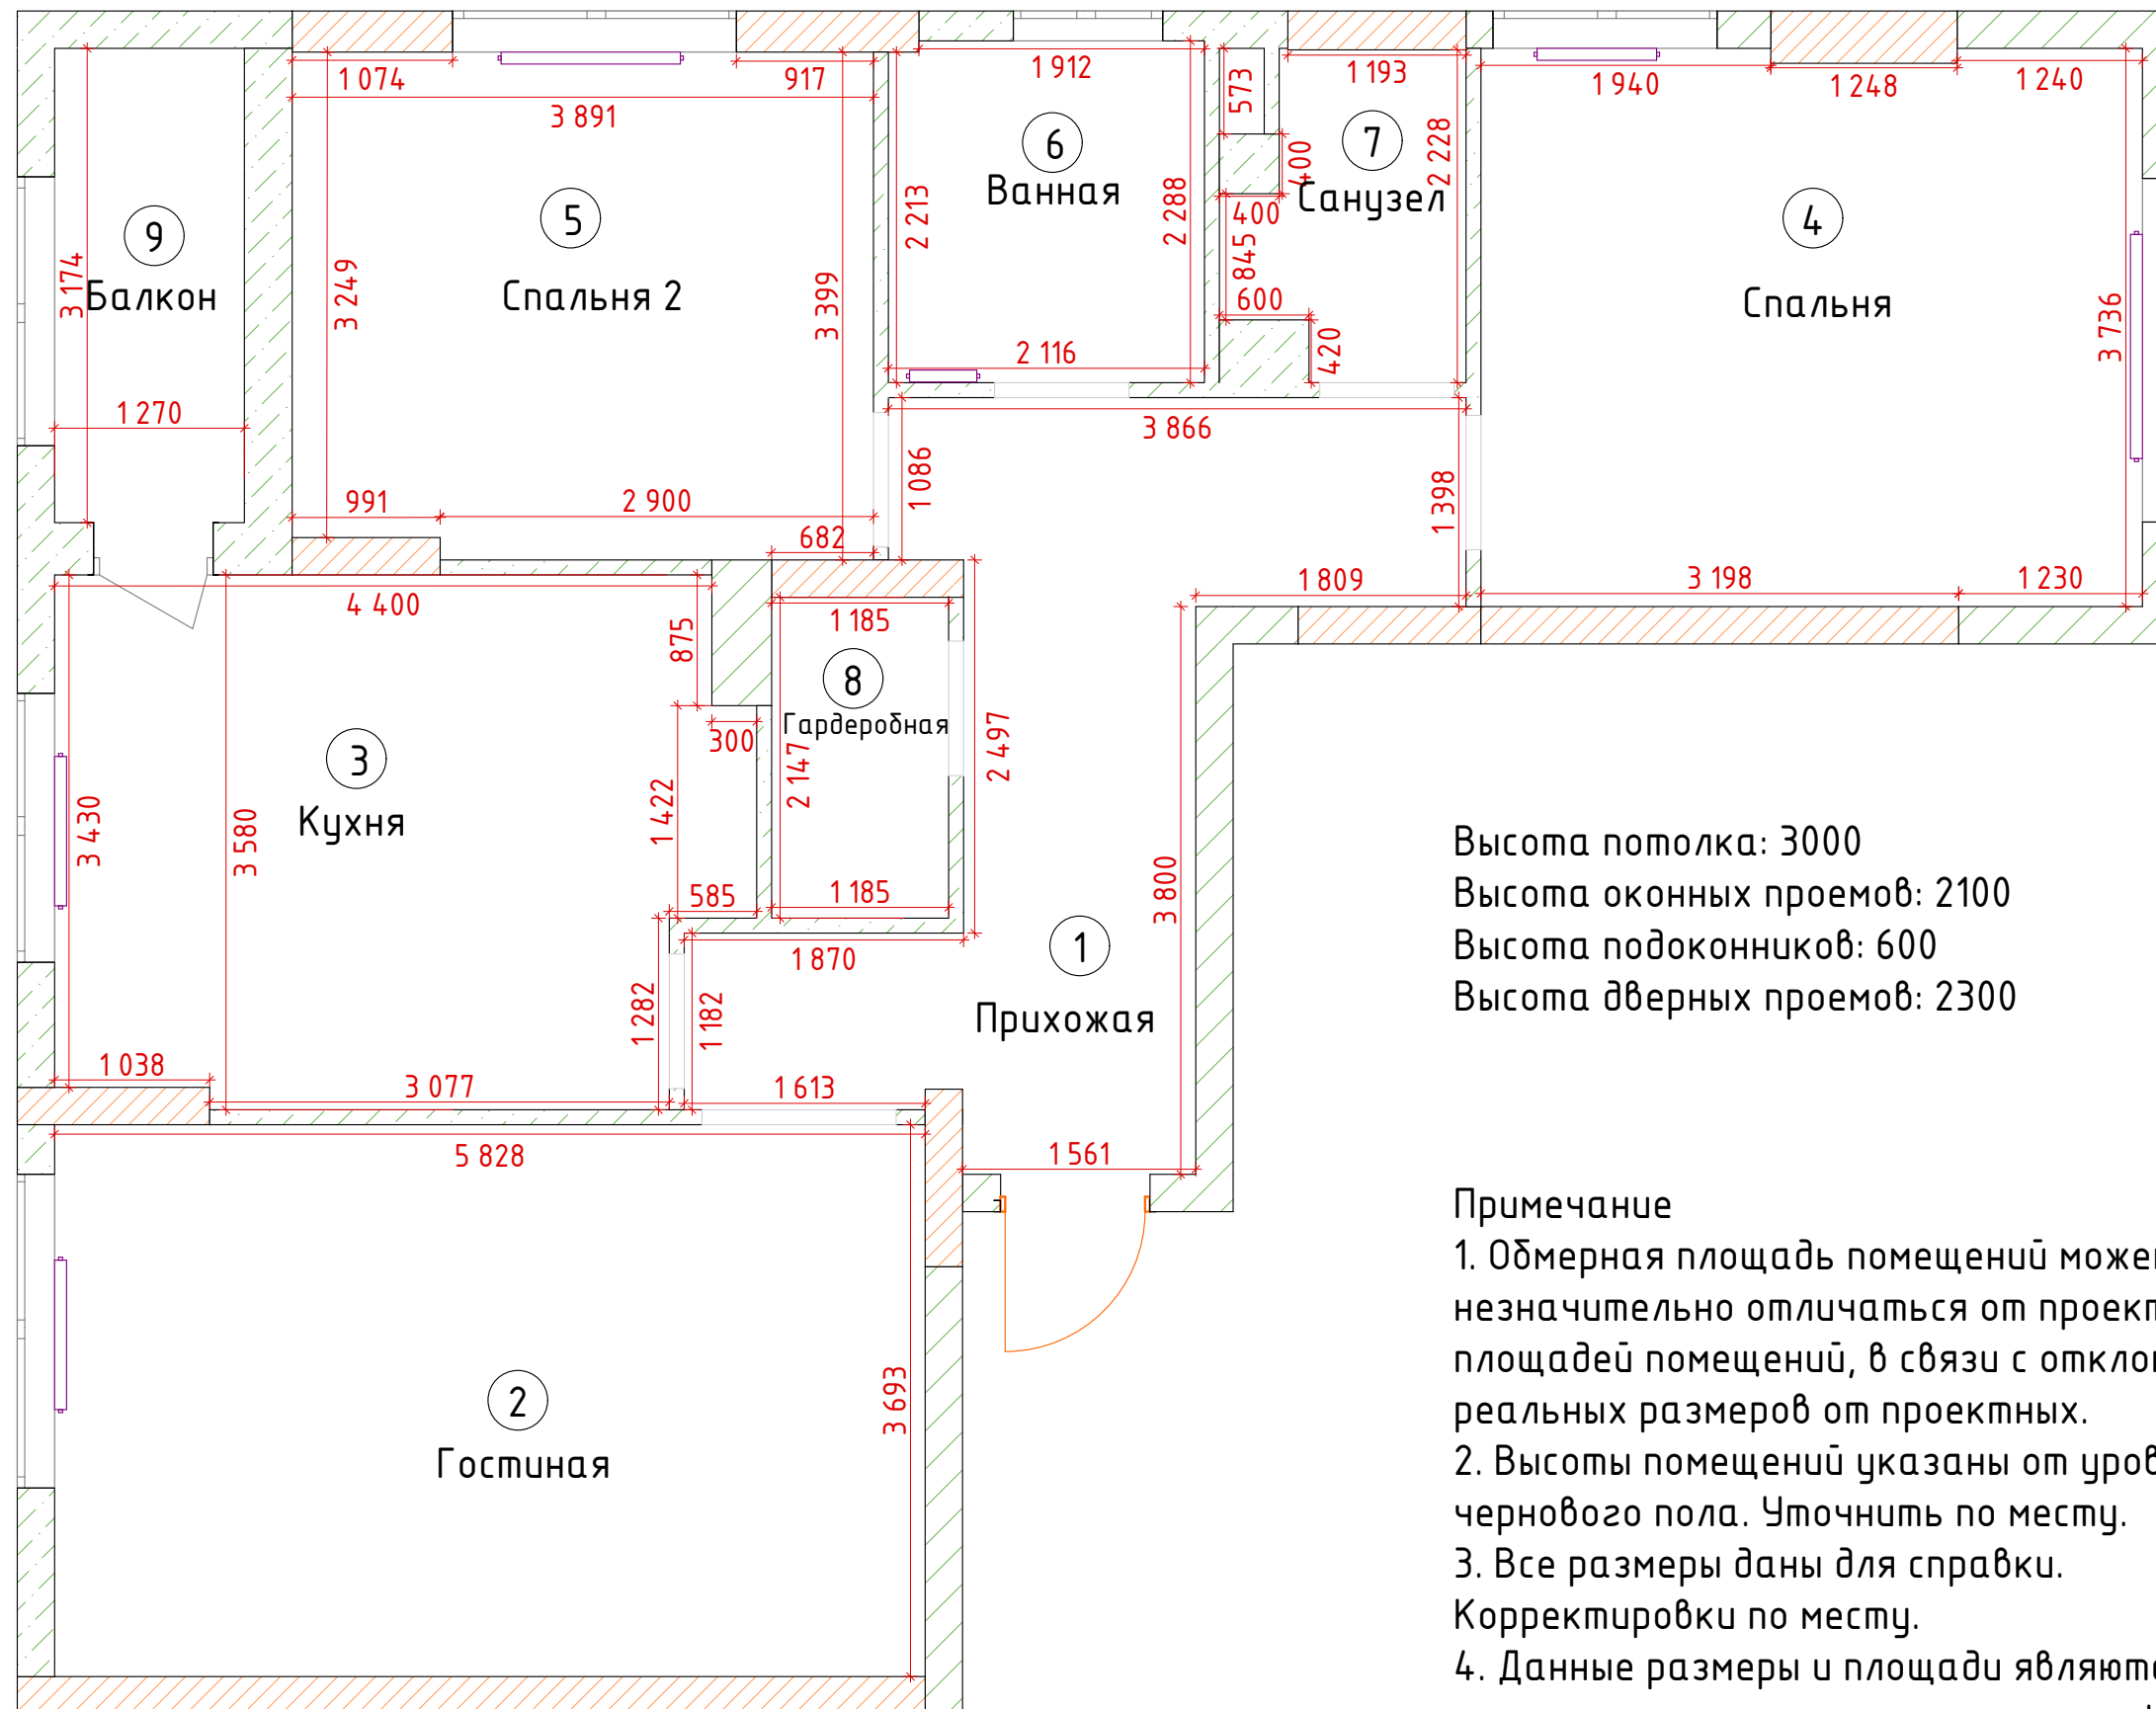

Высота потолка: 3000
Высота оконных проемов: 2100
Высота подоконников: 600
Высота дверных проемов: 2300

Примечание
1. Обмерная площадь помещений может незначительно отличаться от проектных площадей помещений, в связи с отклонением реальных размеров от проектных.
2. Высоты помещений указаны от уровня чернового пола. Уточнить по месту.
3. Все размеры даны для справки. Корректировки по месту.
4. Данные размеры и площади являются проектными и могут отличаться от фактических после возведения стен и перегородок, в соответствии с нормами допусками на отклонение от проектных размеров.

Экспликация помещений до монтажных работ		
№	Наименование помещения	Площадь, м²
1	Прихожая	13,61
2	Гостиная	21,55
3	Кухня	15,37
4	Спальня	16,57
5	Спальня 2	13,32
6	Ванная	4,52
7	Санузел	2,75
8	Гардеробная	2,5
9	Балкон	3,75

	Монолит 400мм
	Газоблок 200мм
	Газоблок 100мм
	ГКЛ 100мм


Рабочий проект

ЖК Shabyt

Лист
4


Листов
18


Обмерный план

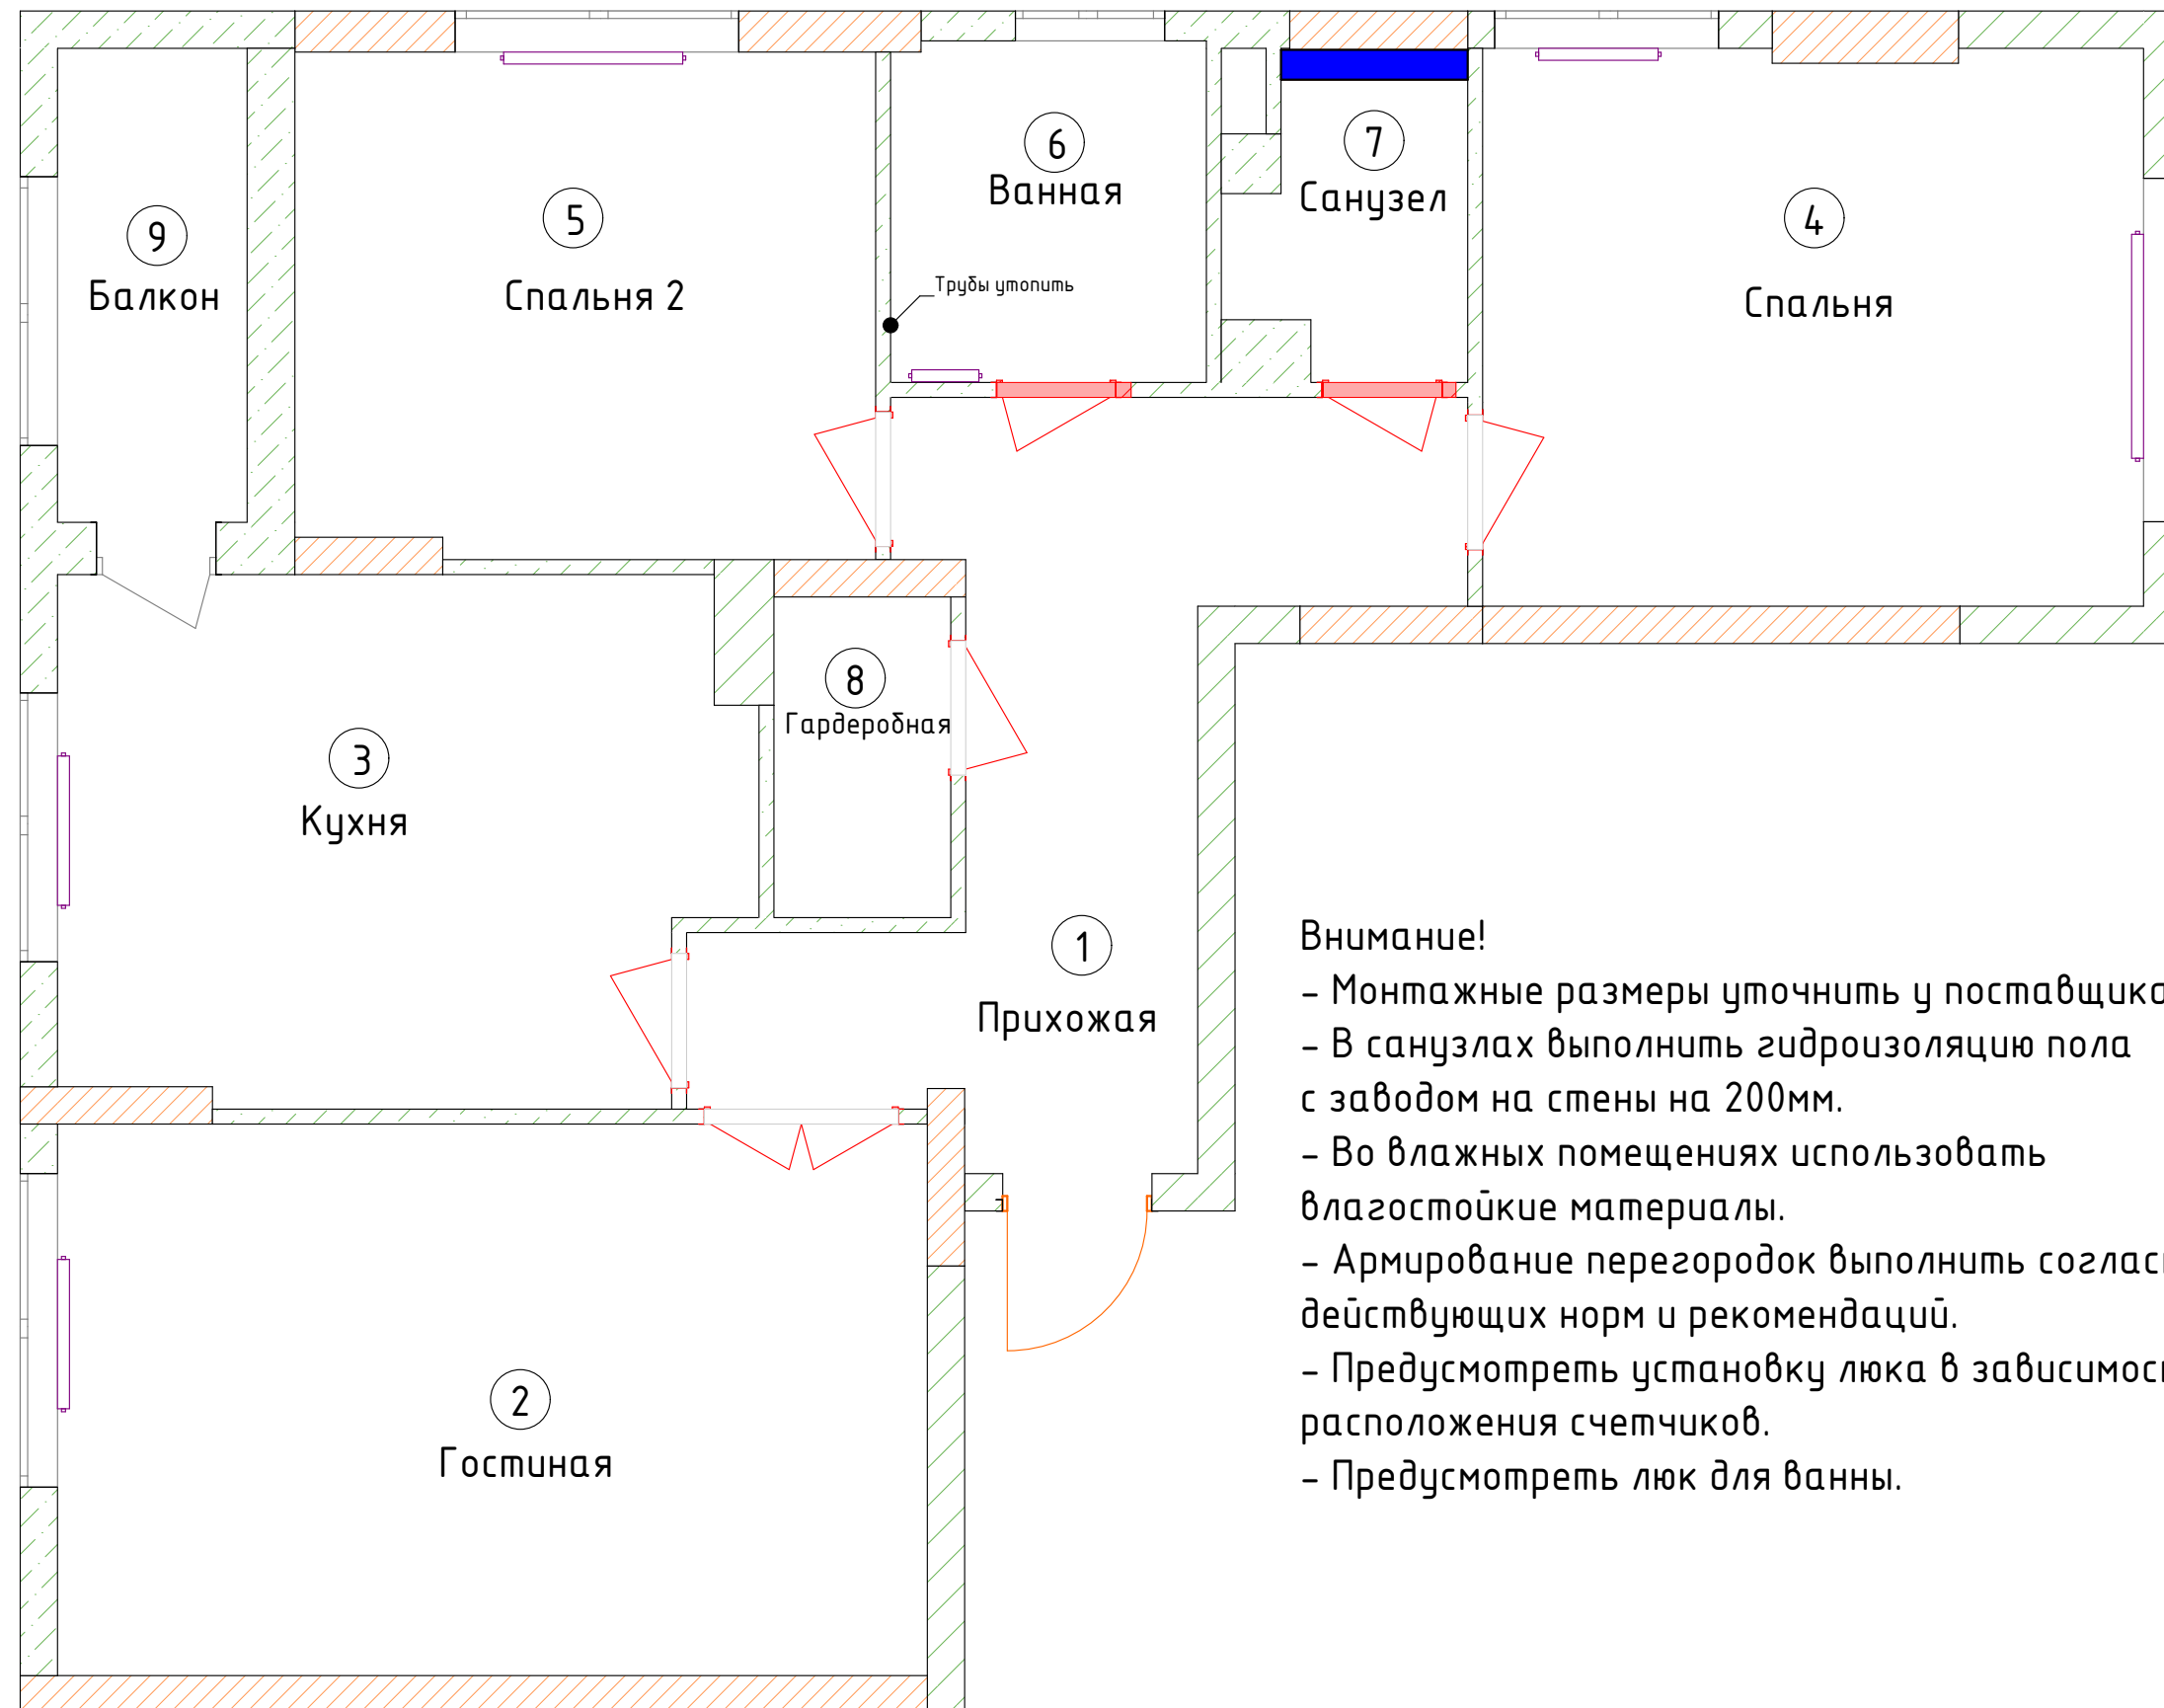

- Внимание!
- Монтажные размеры уточнить у поставщика дверей.
 - В санузлах выполнить гидроизоляцию пола с заводом на стены на 200мм.
 - Во влажных помещениях использовать влагостойкие материалы.
 - Армирование перегородок выполнить согласно действующих норм и рекомендаций.
 - Предусмотреть установку люка в зависимости от расположения счетчиков.
 - Предусмотреть люк для ванны.

Экспликация помещений до монтажных работ		
№	Наименование помещения	Площадь, м²
1	Прихожая	13,61
2	Гостиная	21,55
3	Кухня	15,37
4	Спальня	16,57
5	Спальня 2	13,32
6	Ванная	4,52
7	Санузел	2,75
8	Гардеробная	2,5
9	Балкон	3,75

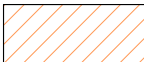 Монолит 400мм

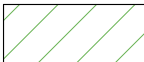 Газоблок 200мм

 Газоблок 100мм

 ГКЛ 100мм


 Инсталляция, h=1200мм, если иное не указано

 Монтируемые перегородки и стены

Рабочий проект

ЖК Shabyt	Лист	Листов
	5	18

План демонтажа и монтажа

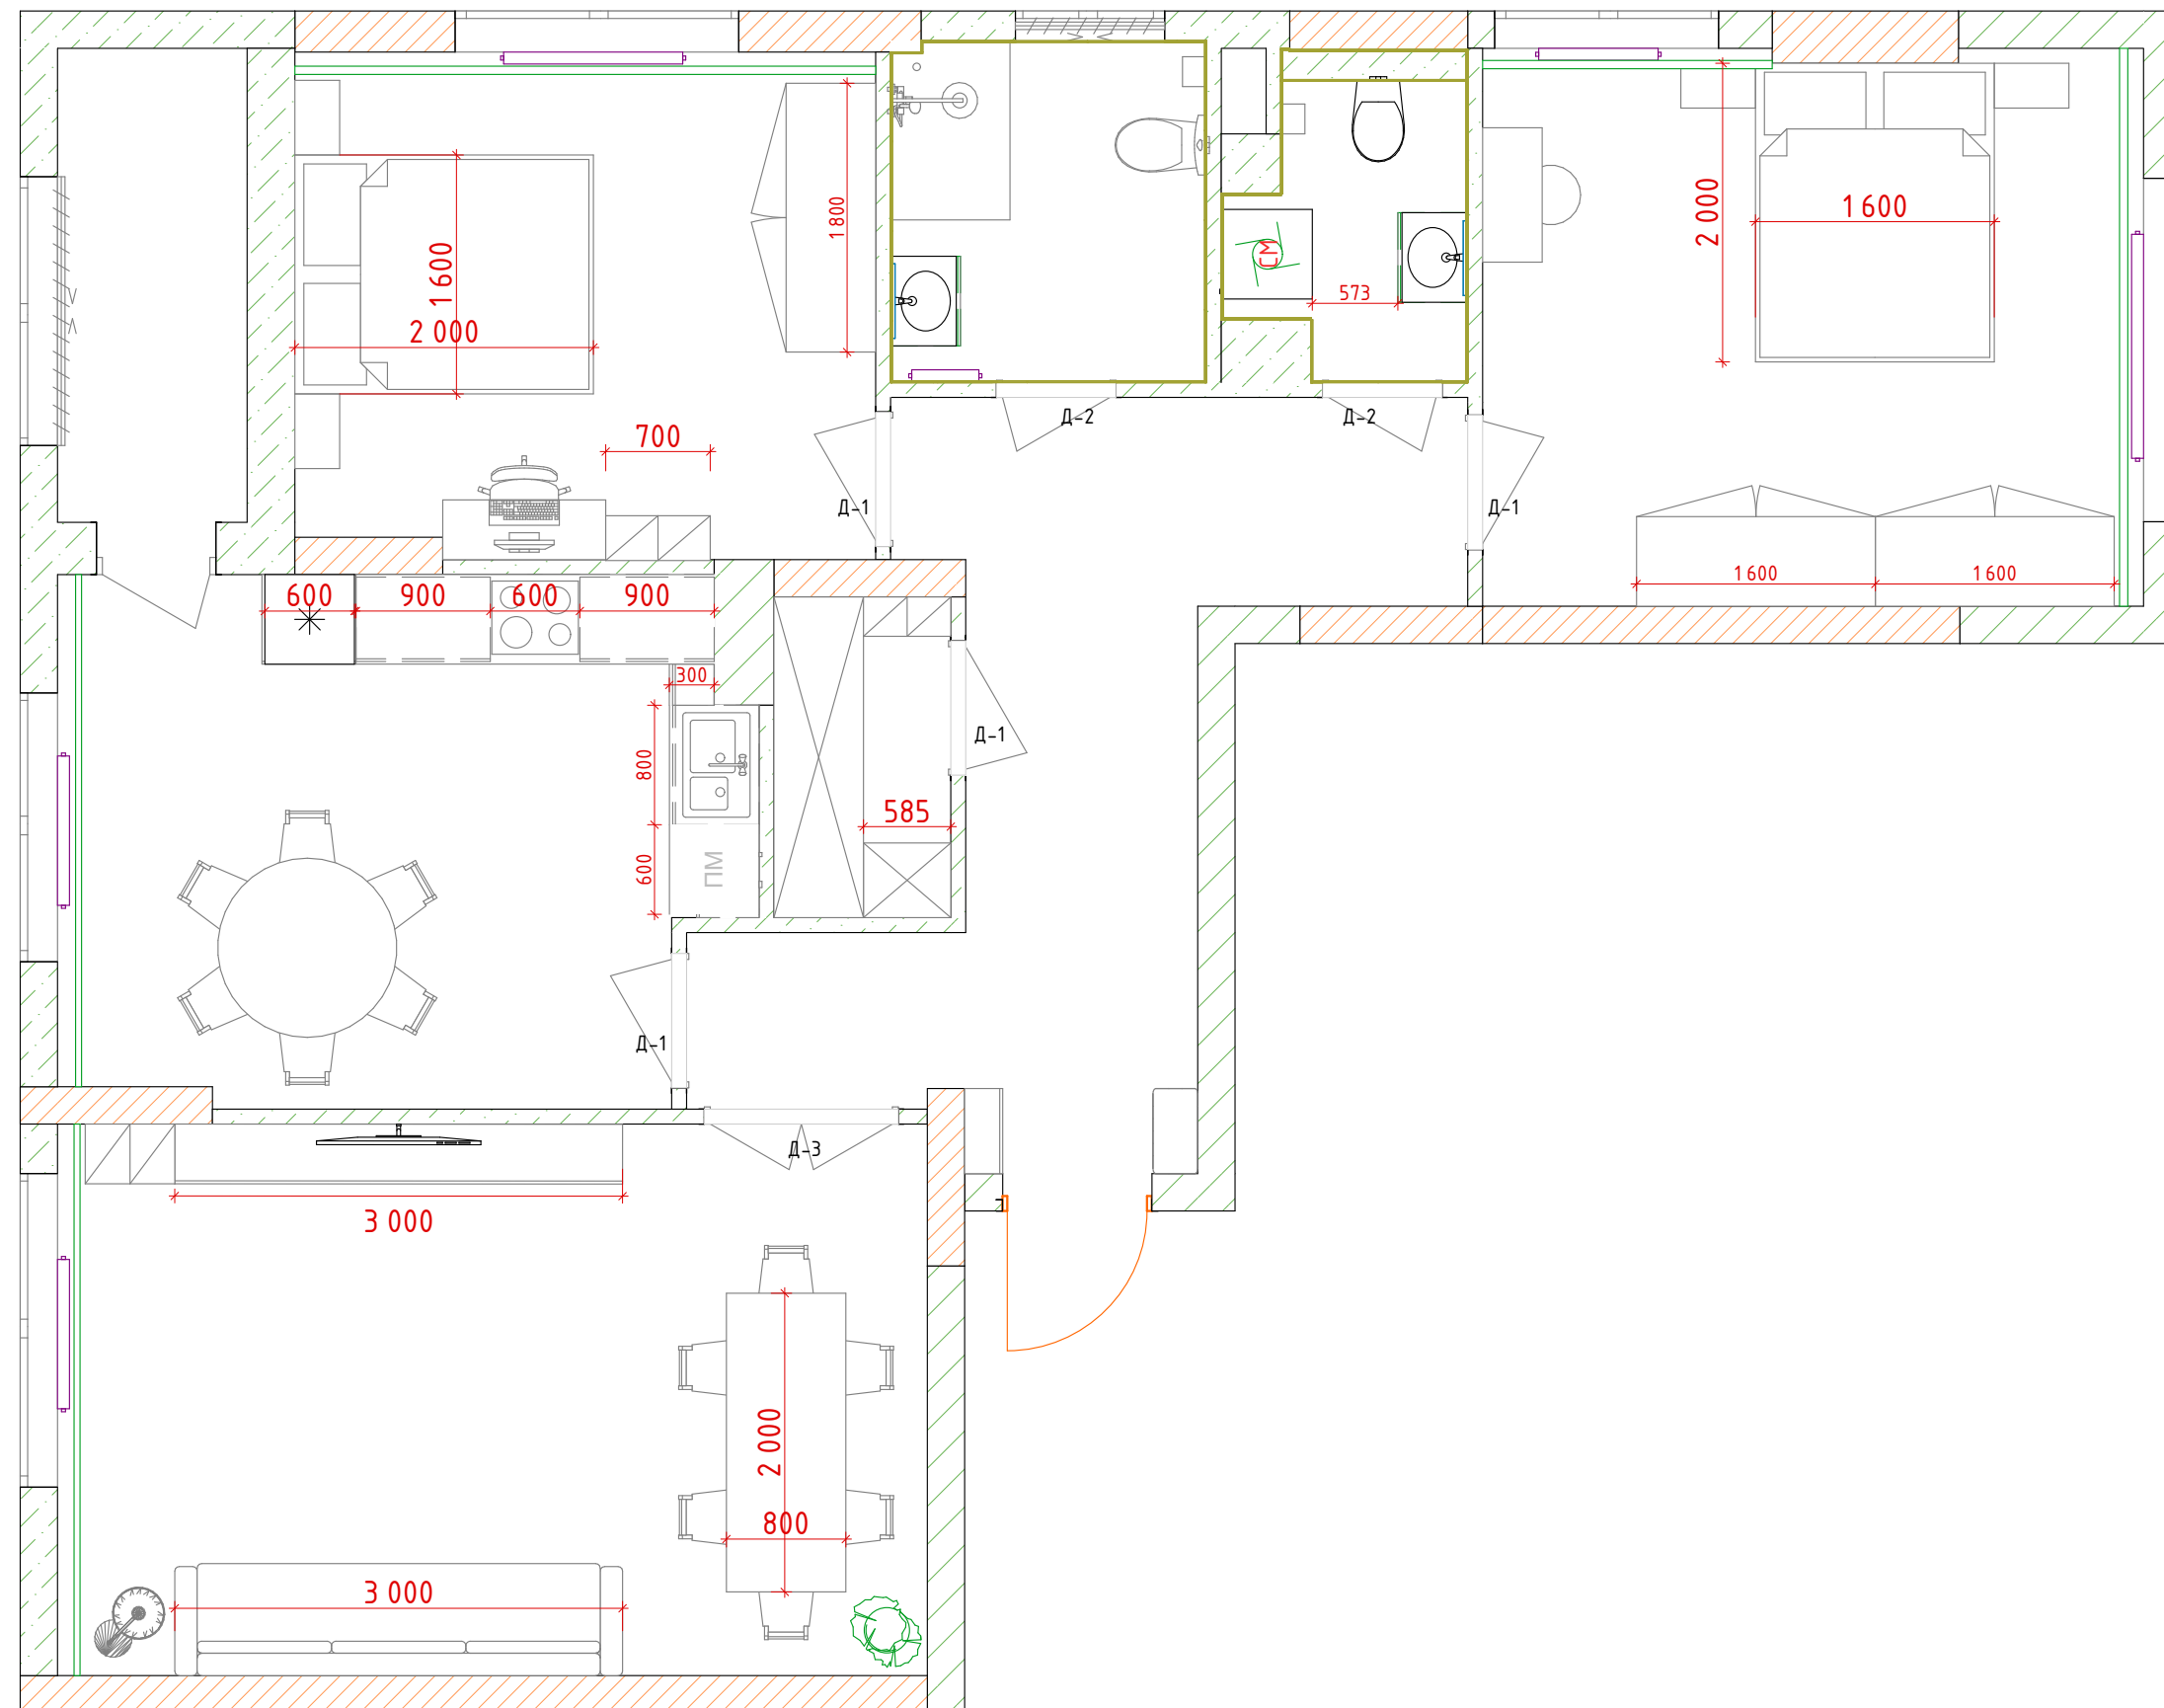

№	Спецификация дверей	Ширина, мм	Высота, мм	Кол-во, шт
Д-1	Дверное полотно Эрмитаж-7, покрытие Vinyl, цвет белый. Глухая.	800	2200	4
Д-2	Дверное полотно Эрмитаж-7, покрытие Vinyl, цвет белый. Глухая.	700	2200	2
Д-3	Двустворчатая дверь Эрмитаж-7, покрытие Vinyl, цвет белый. Глухая.	1200	2200	1

Экспликация помещений после монтажных работ		
№	Наименование помещения	Площадь, м²
1	Прихожая	13,61
2	Гостиная	21,55
3	Кухня	15,37
4	Спальня	16,57
5	Спальня 2	13,32
6	Ванная	4,52
7	Санузел	2,75
8	Гардеробная	2,5
9	Балкон	3,75

Рабочий проект		
ЖК Shabyt	Лист	Листов
	6	18
План расстановки мебели		

LM0462C "Линара" Смеситель
для ванны
с верхней душевой лейкой
Тропический дождь,с пов. изливом

Душ кабина до 1,2 м.
Прозрачное стекло,
фурнитура черная,
двери раздвижные


Смеситель для раковины 100,
со сливным гарнитуром
Hansgrohe Vernis Shape 71561000,
хром

Зеркало ECLIPSE smart 50x122
с подсветкой овальное



Подвесная тумба под раковину
60 см., 2 ящика, раковина на
столешницу СОМО 60


Унитаз компакт ART SL D
с двухрежимной арматурой GEBERIT,
сиденьем из дюропласта

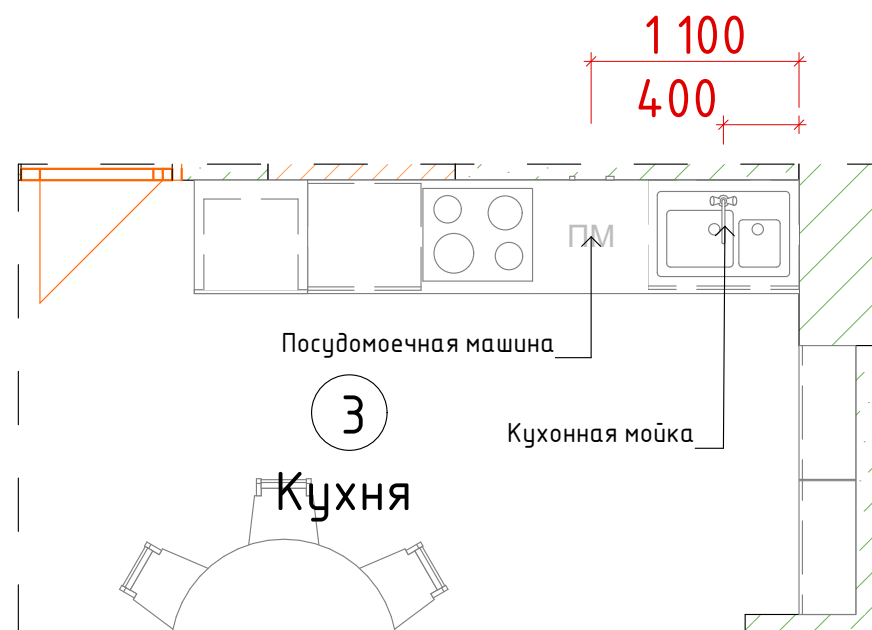

Посудомоечная машина

Кухонная мойка

Кухня

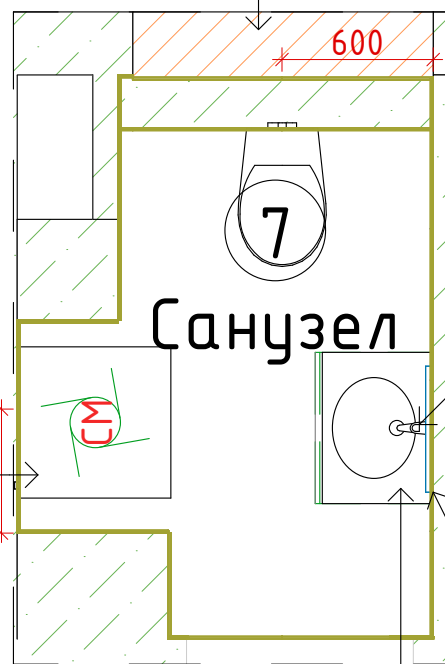

Стиральная машина

Подвесная тумба под раковину
Руана 60 см., 2 ящика, раковина
на столешницу СОМО 60

Унитаз подвесной Greavit
35.5*49.8 см
с инсталляцией,
кнопкой и сиденьем

Смеситель для раковины 100,
со сливным гарнитуром
Hansgrohe Vernis Shape
71561000, хром

Зеркало ECLIPSE
smart 50x122
с подсветкой овальное

Экспликация помещений после монтажных работ		
№	Наименование помещения	Площадь, м²
1	Прихожая	13,61
2	Гостиная	21,55
3	Кухня	15,37
4	Спальня	16,57
5	Спальня 2	13,32
6	Ванная	4,52
7	Санузел	2,75
8	Гардеробная	2,5
9	Балкон	3,75

Примечание:
Размеры установки сан.
тех. оборудования
указаны от черновой
стены

Рабочий проект

ЖК Shabyt


Лист

7

Листов

18


План сантехнического
оборудования

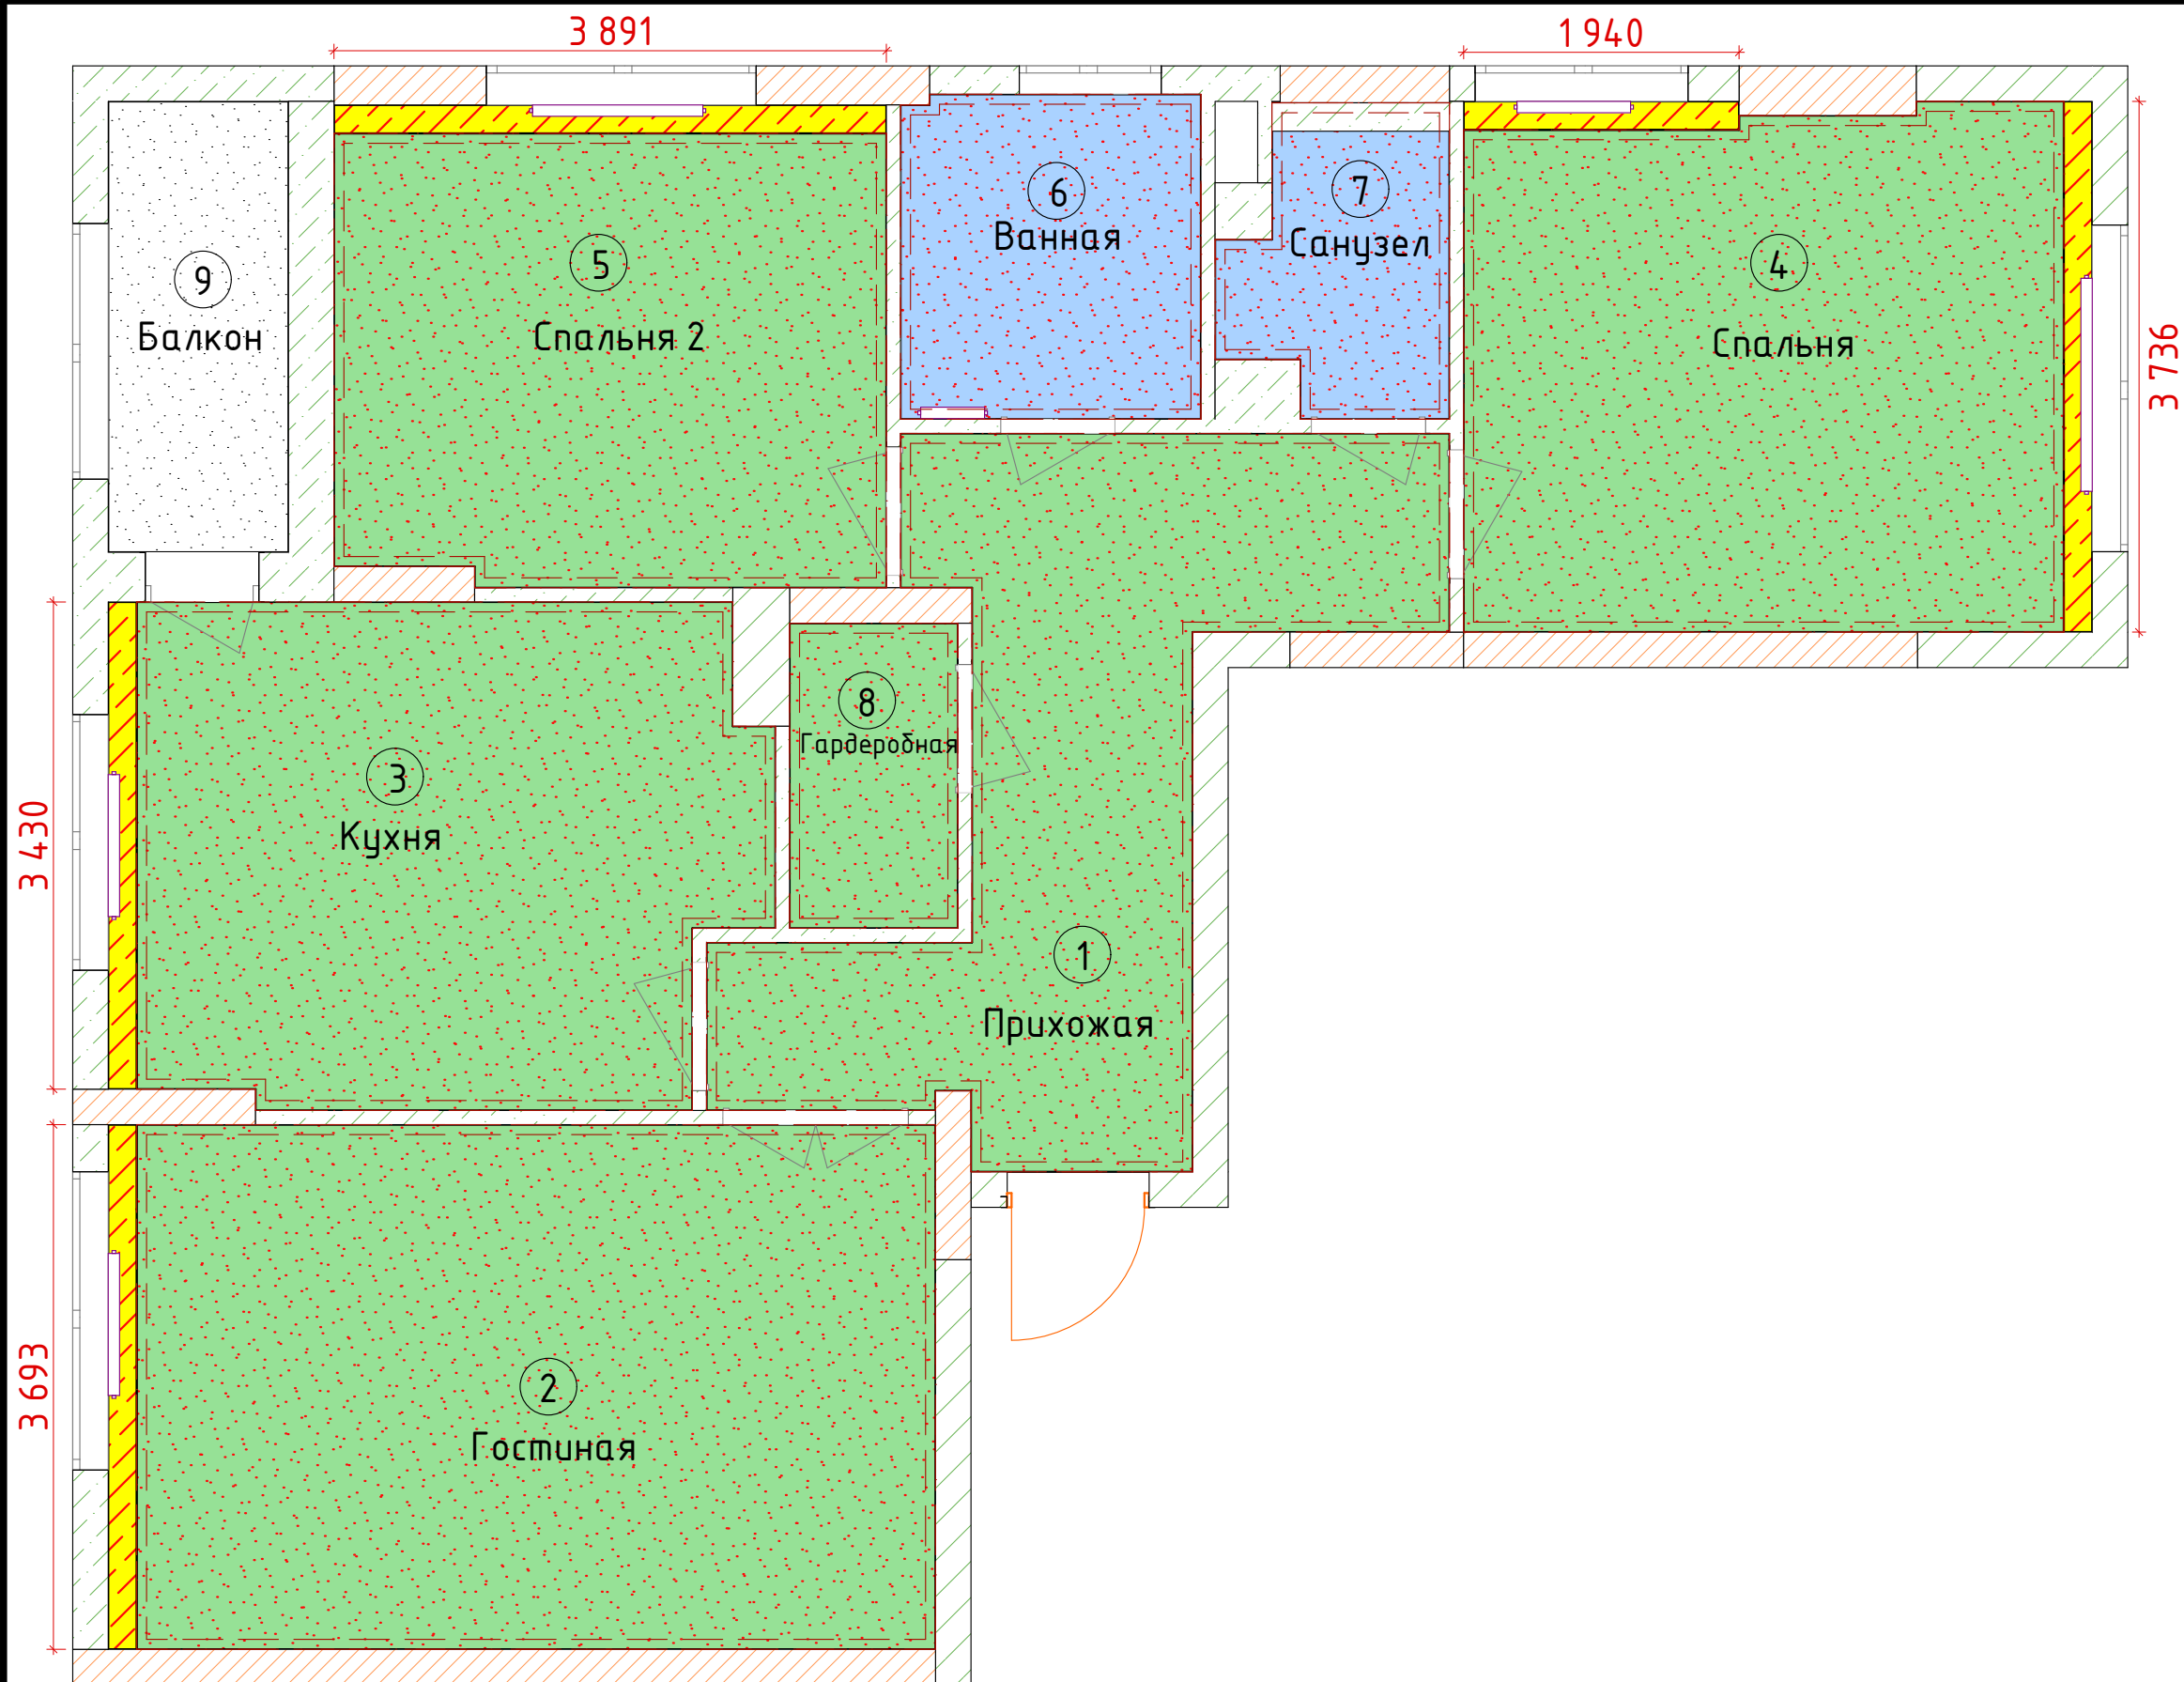

Экспликация помещений после монтажных работ		
№	Наименование помещения	Площадь, м²
1	Прихожая	13,61
2	Гостиная	21,55
3	Кухня	15,37
4	Спальня	16,57
5	Спальня 2	13,32
6	Ванная	4,52
7	Санузел	2,75
8	Гардеробная	2,5
9	Балкон	3,75

- ГКЛ
- Натяжной потолок
- Левкас
- Подшторник
- Галтель 70/70

Рабочий проект		
ЖК Shabyt	Лист	Листов
	8	18
План потолка		

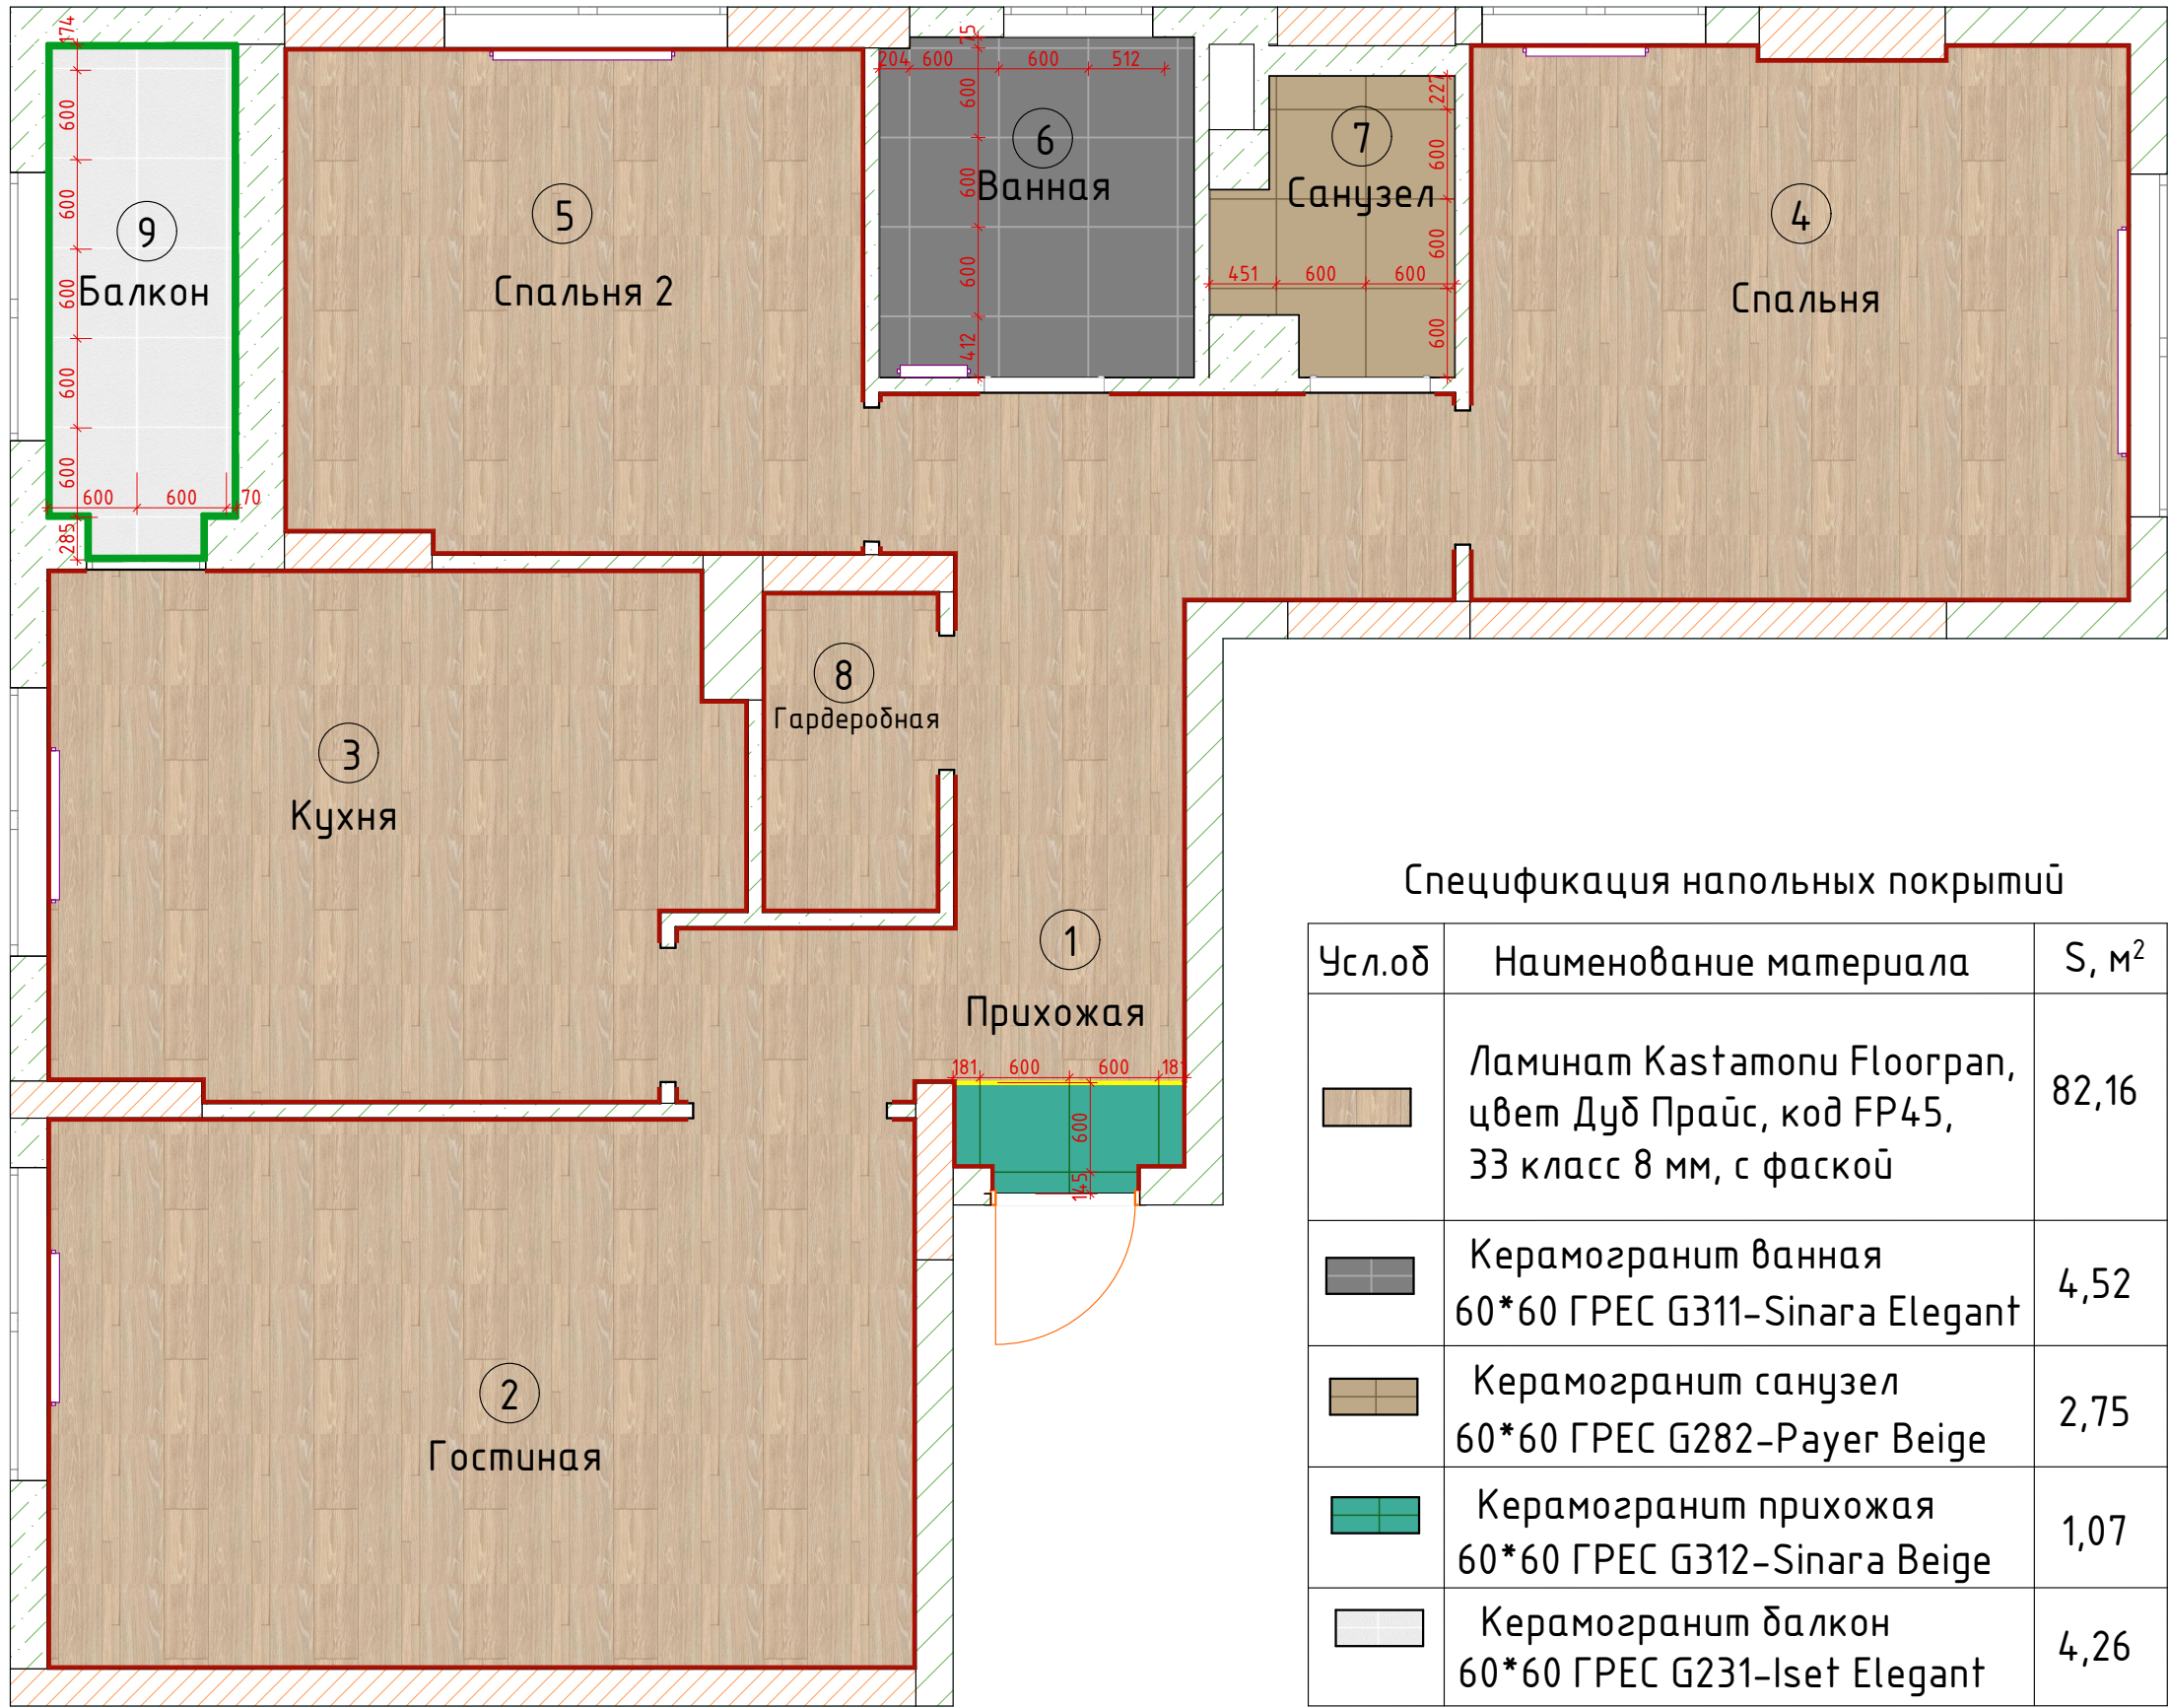


Спецификация напольных покрытий

Усл.об	Наименование материала	S, м²
	Ламинат Kastamonu Floorplan, цвет Дуб Прайс, код FP45, 33 класс 8 мм, с фаской	82,16
	Керамогранит ванная 60*60 ГРЕС G311-Sinara Elegant	4,52
	Керамогранит санузел 60*60 ГРЕС G282-Payer Beige	2,75
	Керамогранит прихожая 60*60 ГРЕС G312-Sinara Beige	1,07
	Керамогранит балкон 60*60 ГРЕС G231-Iset Elegant	4,26

Экспликация помещений после монтажных работ		
№	Наименование помещения	Площадь, м²
1	Прихожая	13,61
2	Гостиная	21,55
3	Кухня	15,37
4	Спальня	16,57
5	Спальня 2	13,32
6	Ванная	4,52
7	Санузел	2,75
8	Гардеробная	2,5
9	Балкон	3,75

- Плинтус Полиуретан h=80mm 84,5 п.м.
- Плинтус из плитки h=50mm 9,5 п.м.
- Т-профиль 1,6 м

Примечание:
Объём указан без запаса!

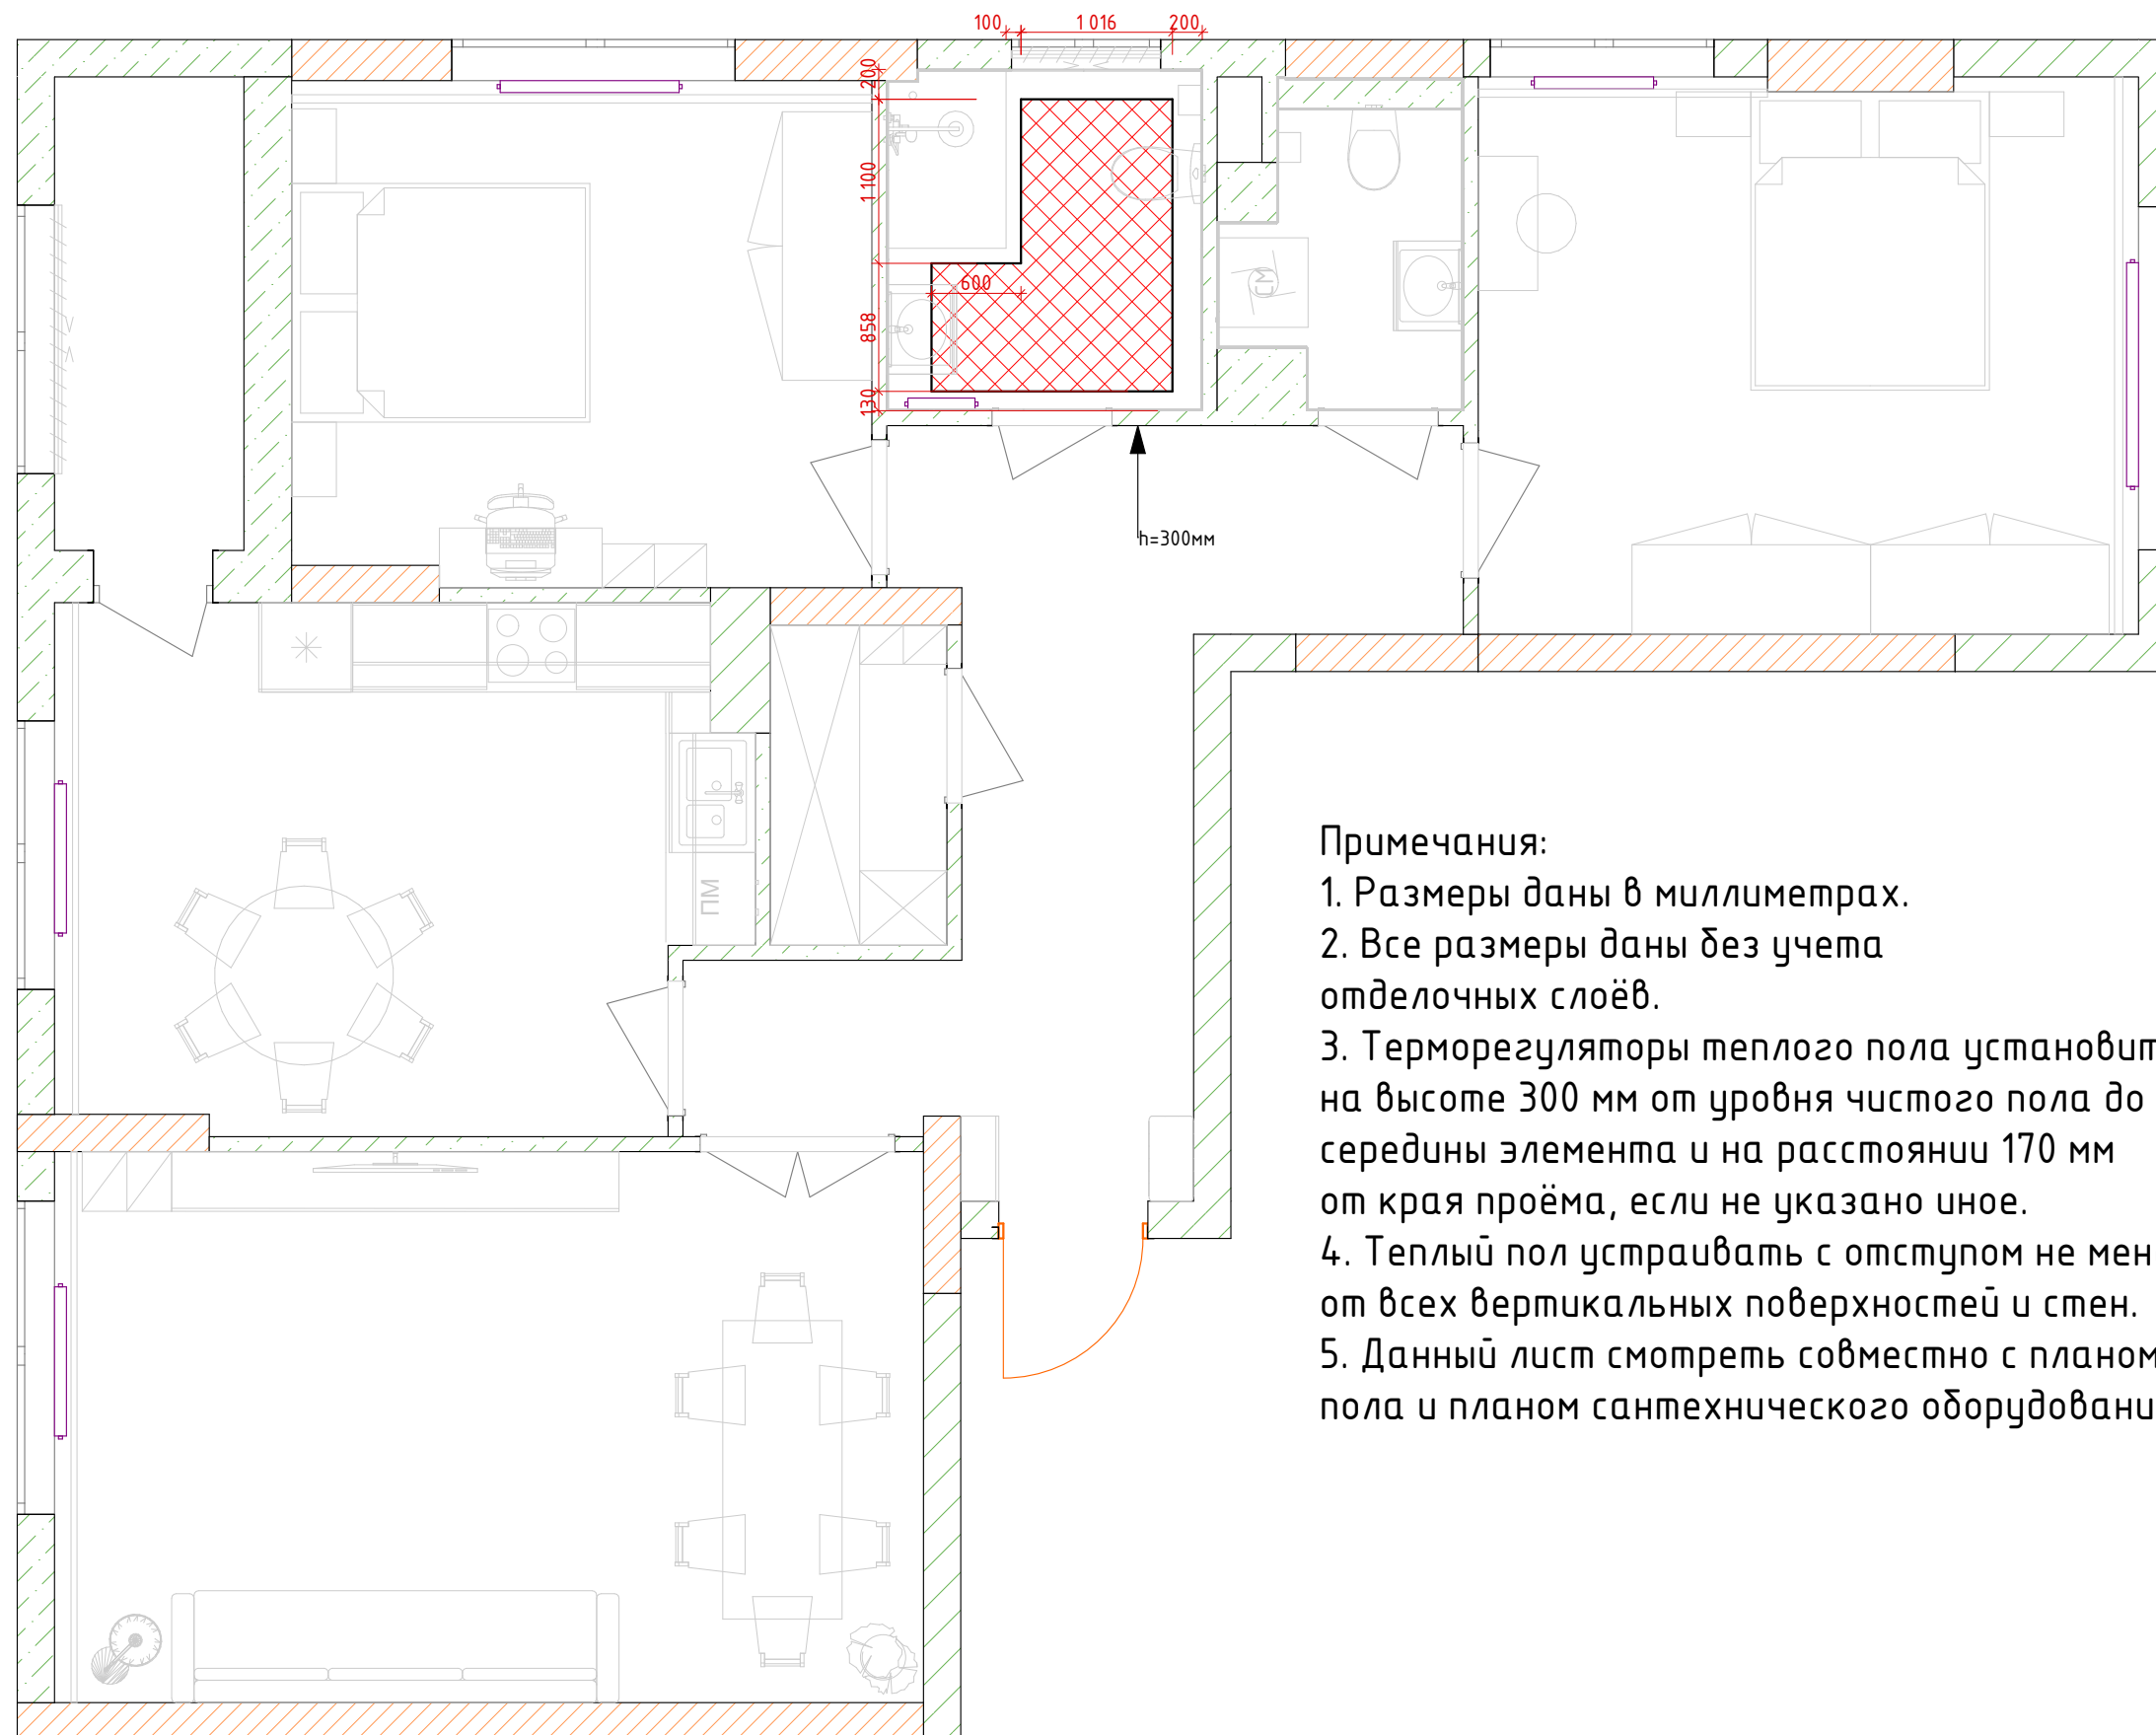


Примечания:


1. Размеры даны в миллиметрах.
2. Все размеры даны без учета отделочных слоёв.
3. Терморегуляторы теплого пола установить на высоте 300 мм от уровня чистого пола до середины элемента и на расстоянии 170 мм от края проёма, если не указано иное.
4. Теплый пол устраивать с отступом не менее 100 мм от всех вертикальных поверхностей и стен.
5. Данный лист смотреть совместно с планом пола и планом сантехнического оборудования.

Экспликация помещений после монтажных работ		
№	Наименование помещения	Площадь, м²
1	Прихожая	13,61
2	Гостиная	21,55
3	Кухня	15,37
4	Спальня	16,57
5	Спальня 2	13,32
6	Ванная	4,52
7	Санузел	2,75
8	Гардеробная	2,5
9	Балкон	3,75

Условные обозначения:

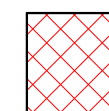

Зона укладки
теплого пола

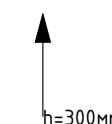

Терморегулятор
теплого пола


Рабочий проект

ЖК Shabyt

Лист
10

Листов
18

План теплого пола

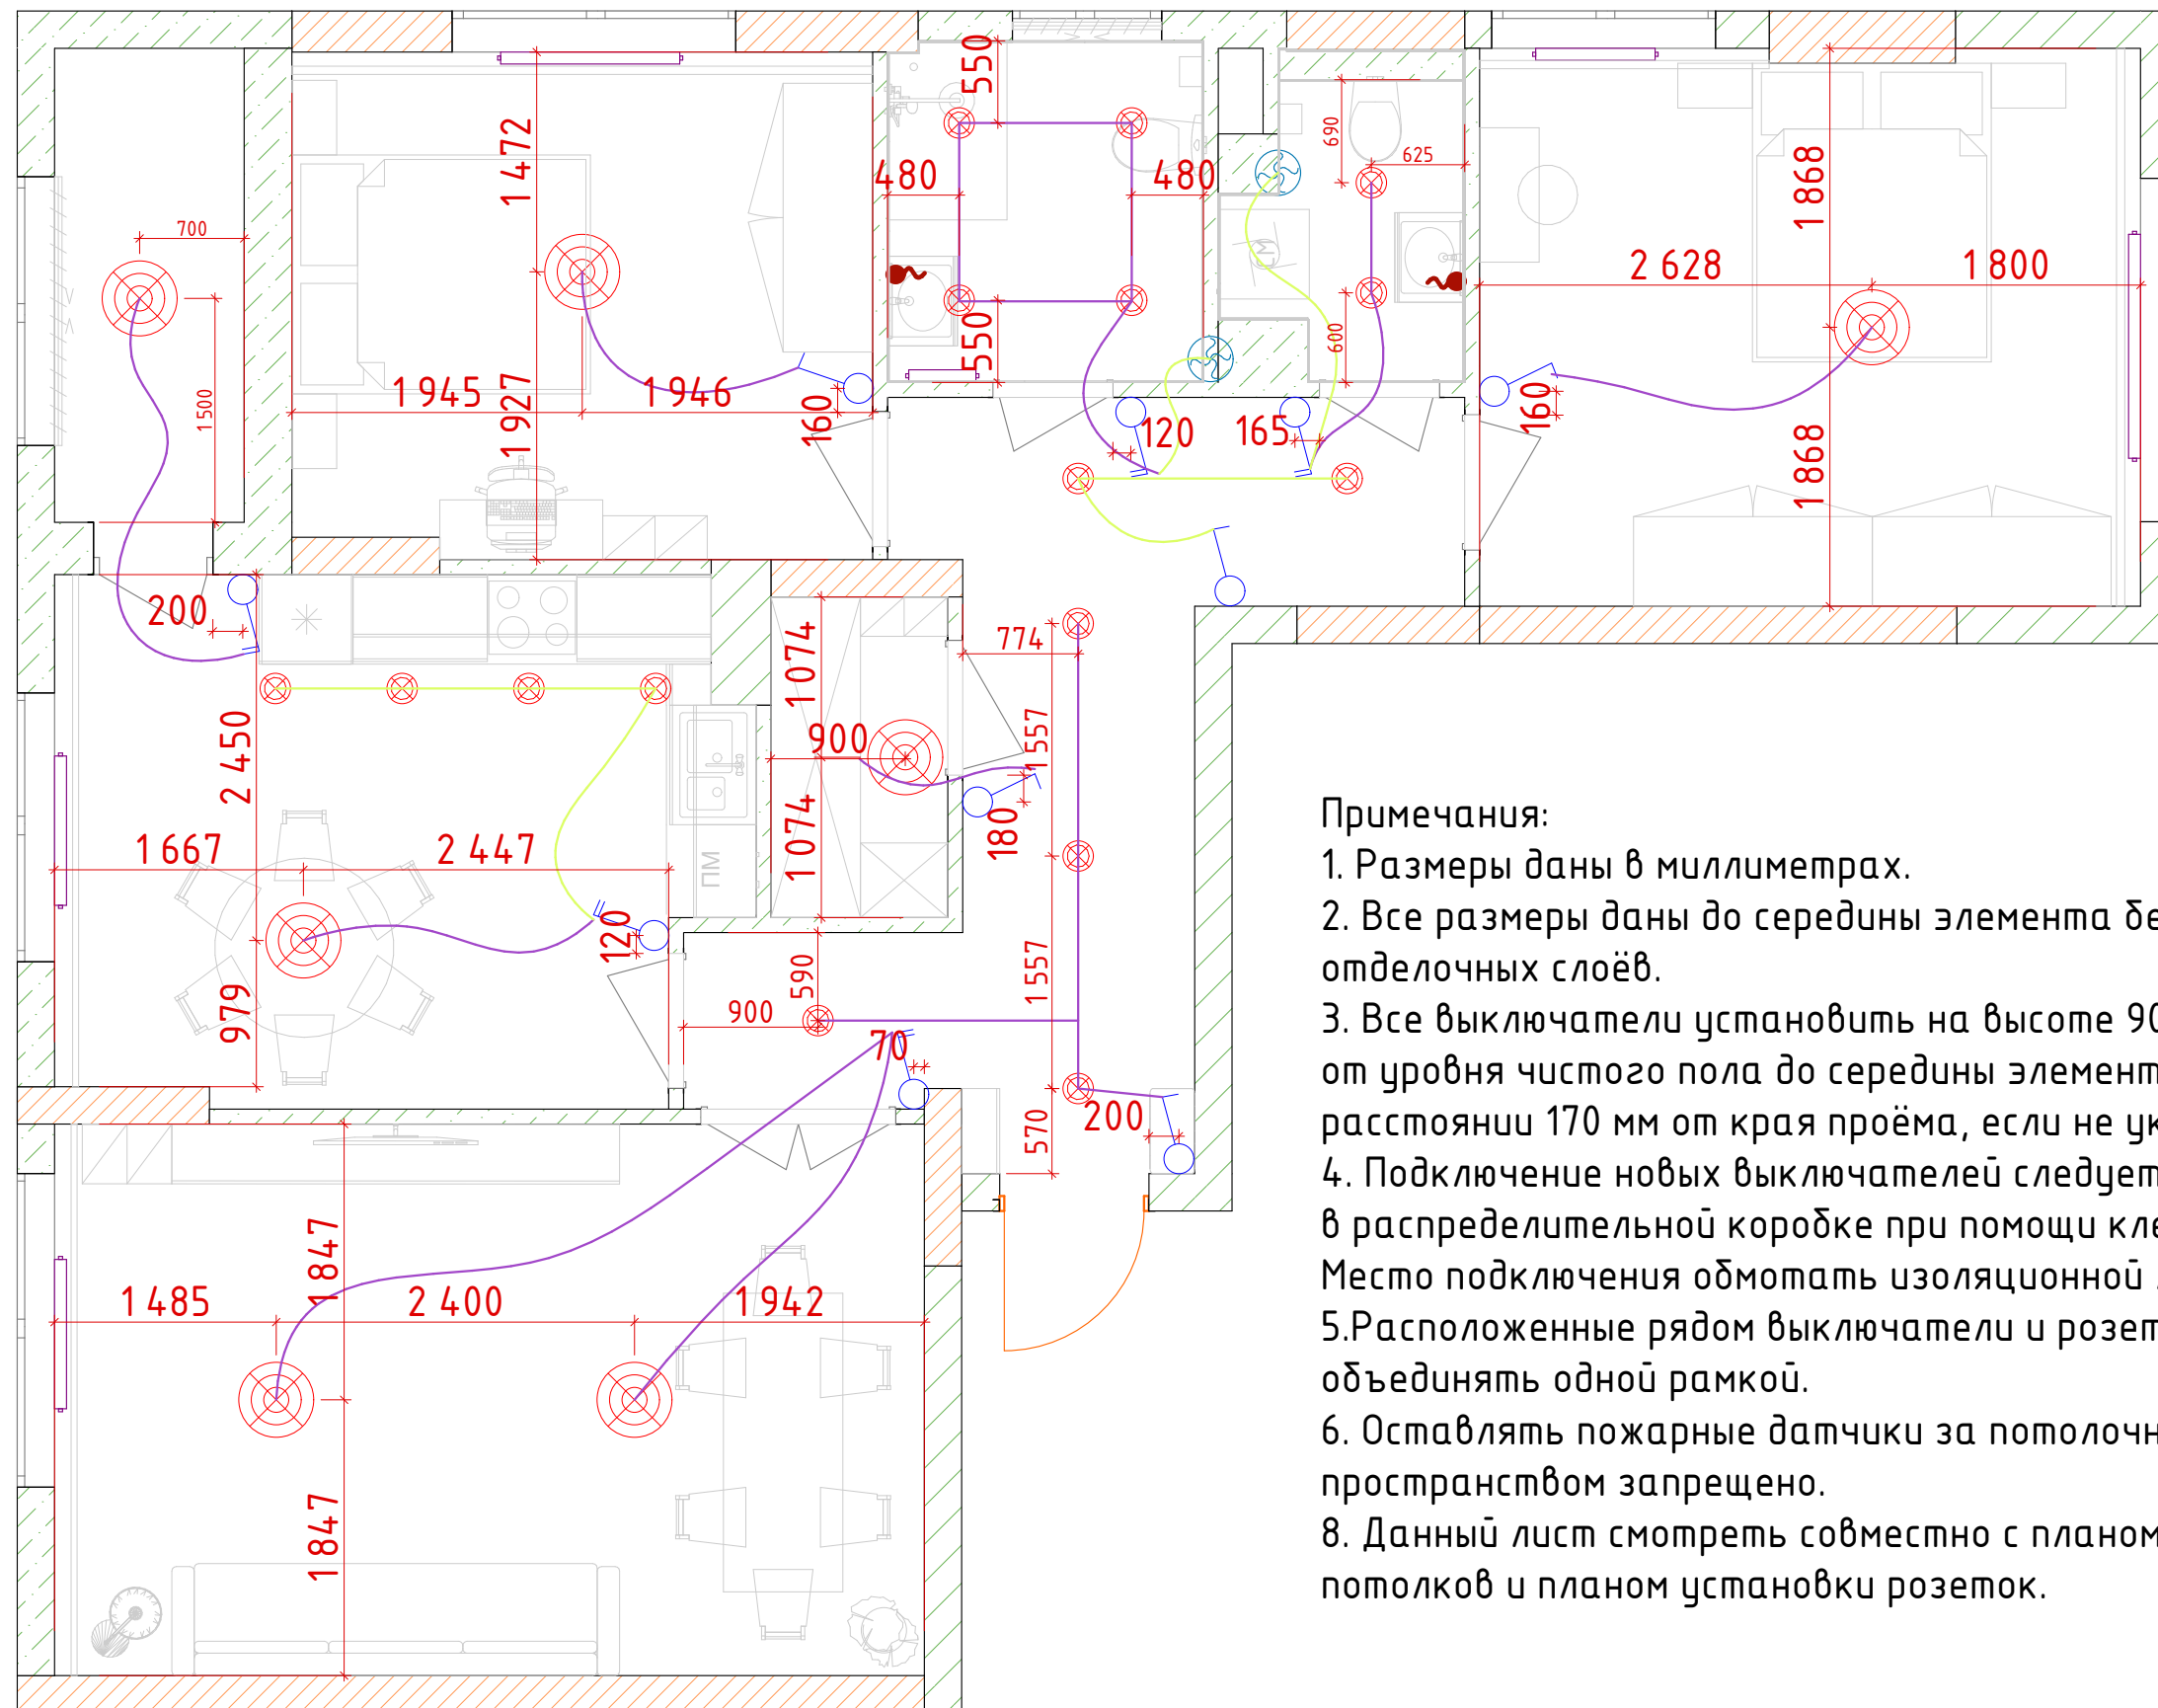


- Примечания:
1. Размеры даны в миллиметрах.
 2. Все размеры даны до середины элемента без учета отделочных слоёв.
 3. Все выключатели установить на высоте 900 мм от уровня чистого пола до середины элемента и на расстоянии 170 мм от края проёма, если не указано иное.
 4. Подключение новых выключателей следует выполнять в распределительной коробке при помощи клеммников. Место подключения обмотать изоляционной лентой.
 5. Расположенные рядом выключатели и розетки объединять одной рамкой.
 6. Оставлять пожарные датчики за потолочным пространством запрещено.
 8. Данный лист смотреть совместно с планом потолков и планом установки розеток.

Экспликация помещений после монтажных работ		
№	Наименование помещения	Площадь, м²
1	Прихожая	13,61
2	Гостиная	21,55
3	Кухня	15,37
4	Спальня	16,57
5	Спальня 2	13,32
6	Ванная	4,52
7	Санузел	2,75
8	Гардеробная	2,5
9	Балкон	3,75

Усл. обозначения	
	Люстра
	Софиты
	Выключатель 1-клавишный
	Выключатель 2-клавишный
	Вывод для подсветки
	Вытяжной вентилятор

Внимание!
Предусмотреть
подключение
вентилятора
для вытяжки

Рабочий проект		
ЖК Shabyt	Лист	Листов
	11	18
План освещения		

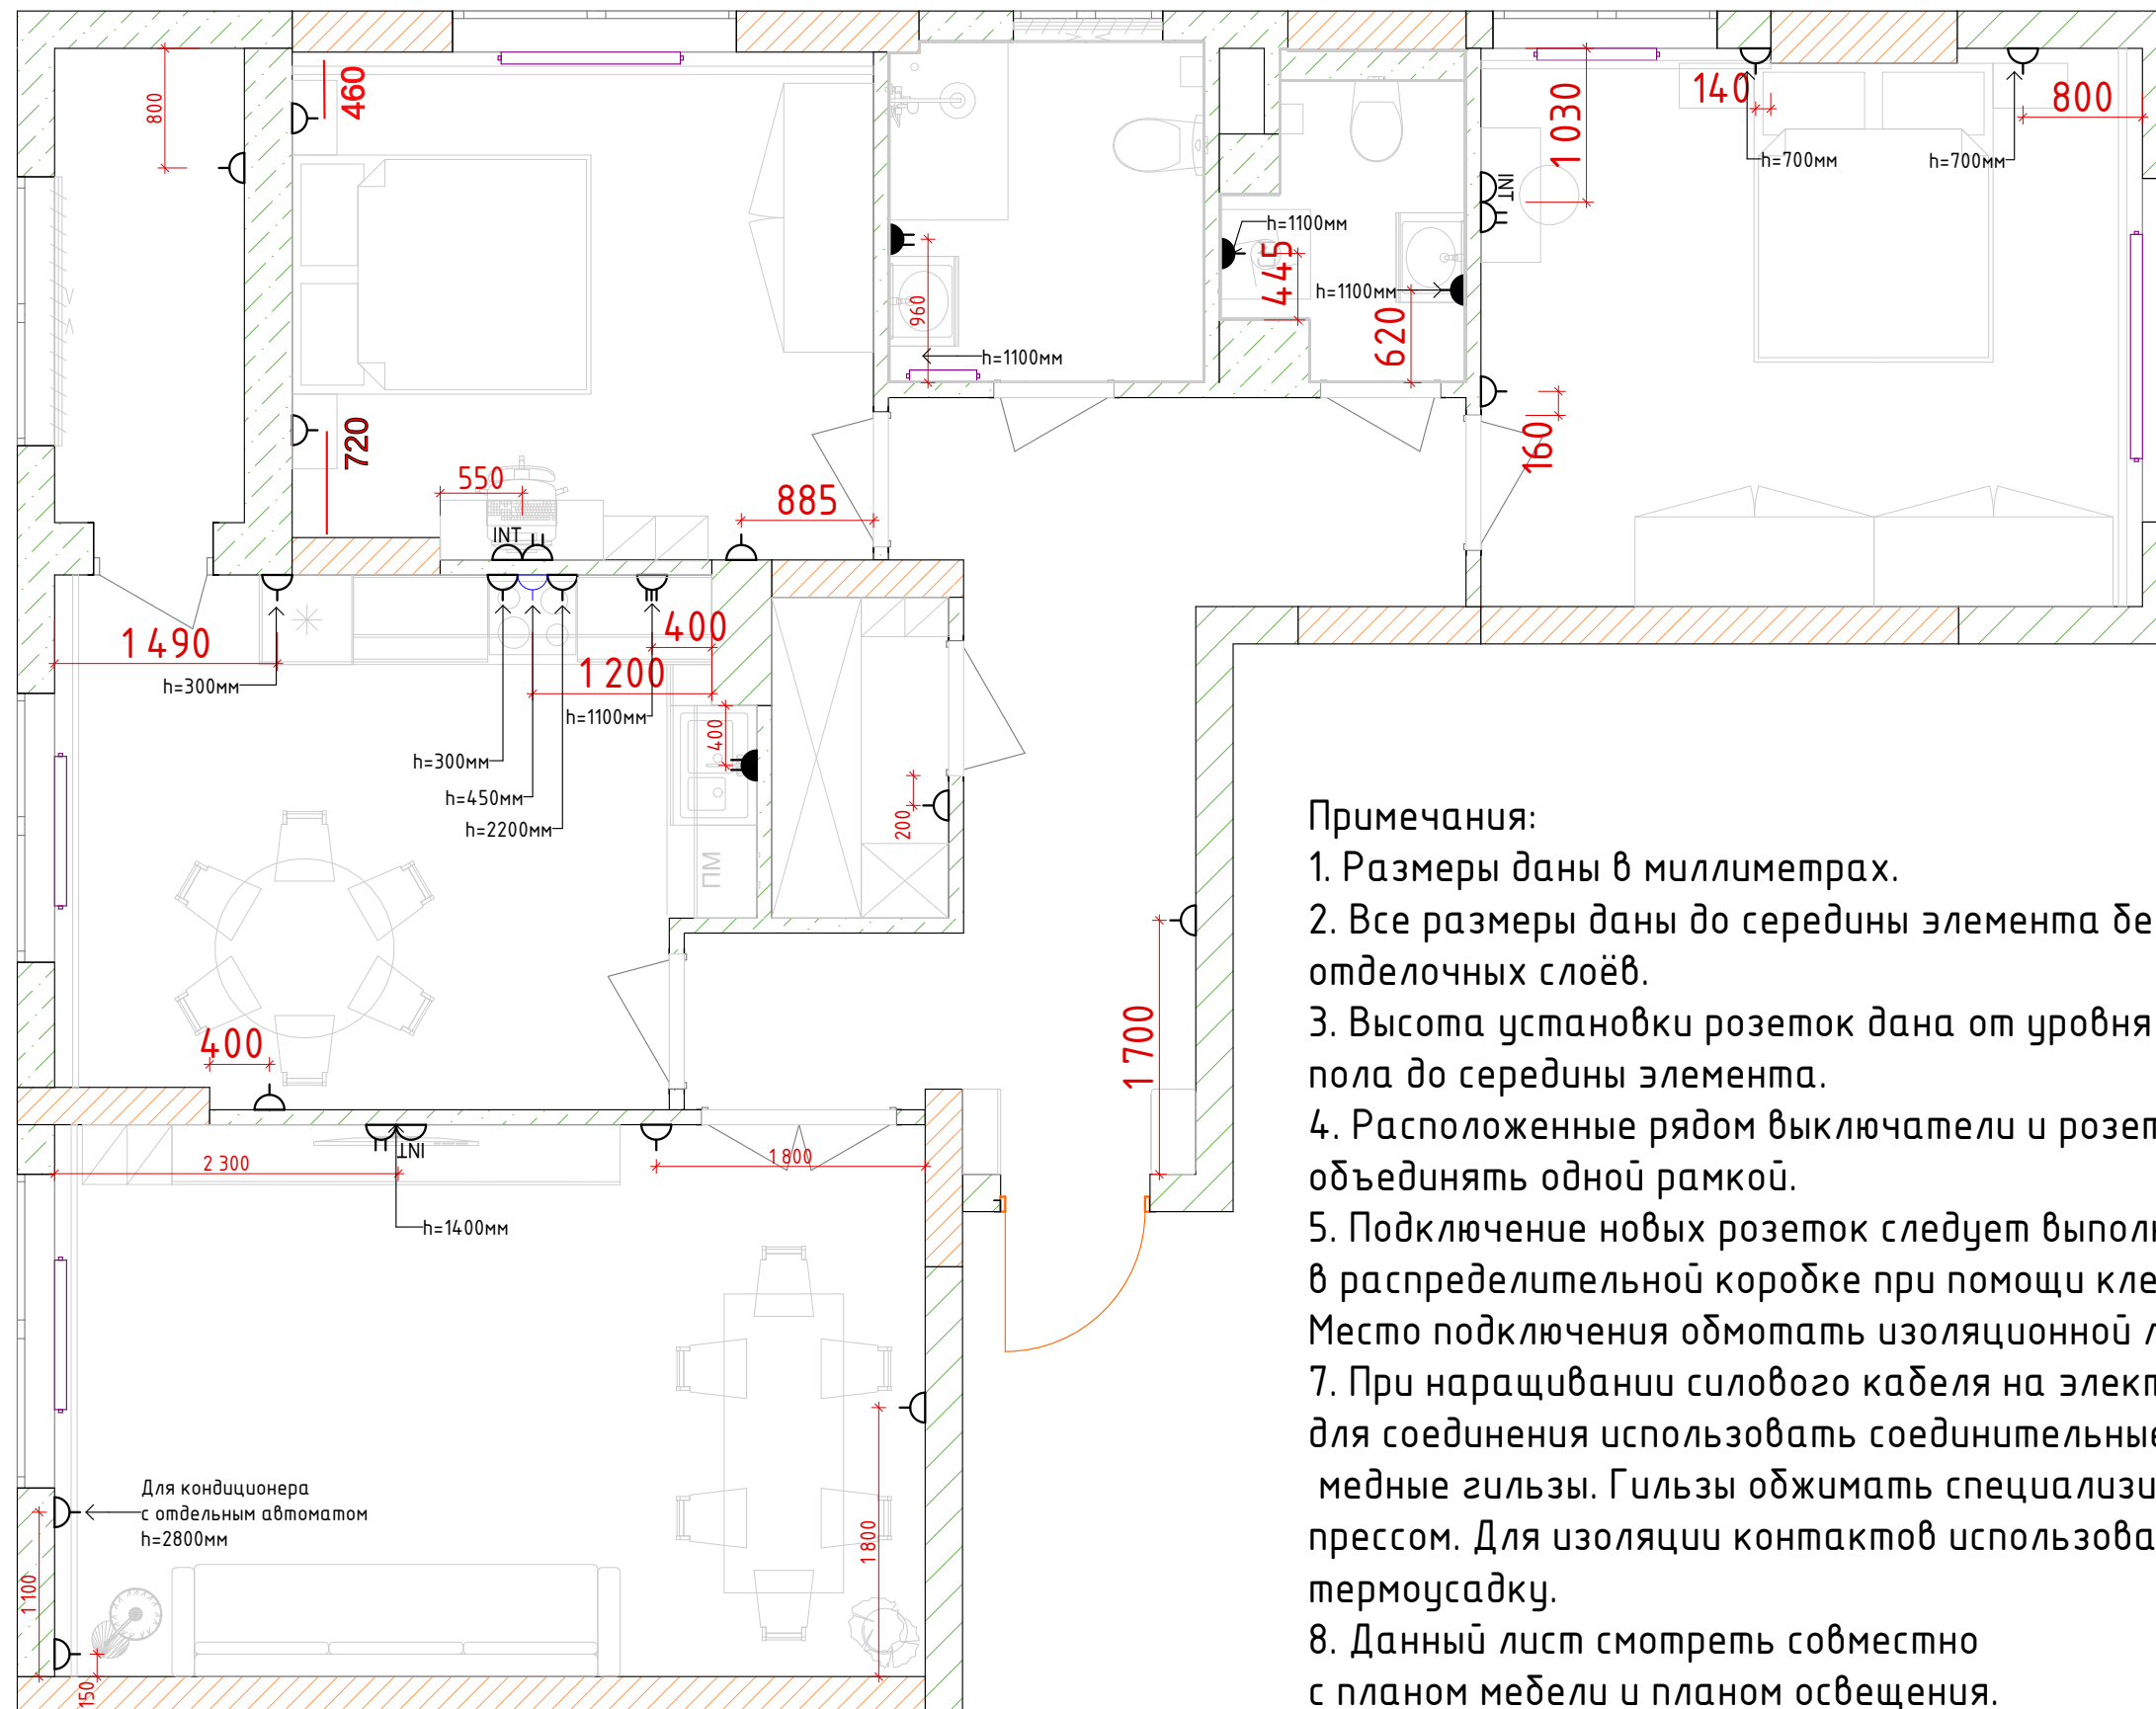

Примечания:

1. Размеры даны в миллиметрах.
2. Все размеры даны до середины элемента без учета отделочных слоёв.
3. Высота установки розеток дана от уровня чистого пола до середины элемента.
4. Расположенные рядом выключатели и розетки объединять одной рамкой.
5. Подключение новых розеток следует выполнять в распределительной коробке при помощи клеммников. Место подключения обмотать изоляционной лентой.
7. При наращивании силового кабеля на электроплиту для соединения использовать соединительные медные гильзы. Гильзы обжимать специализированным прессом. Для изоляции контактов использовать термоусадку.
8. Данный лист смотреть совместно с планом мебели и планом освещения.

Экспликация помещений после монтажных работ		
№	Наименование помещения	Площадь, м²
1	Прихожая	13,61
2	Гостиная	21,55
3	Кухня	15,37
4	Спальня	16,57
5	Спальня 2	13,32
6	Ванная	4,52
7	Санузел	2,75
8	Гардеробная	2,5
9	Балкон	3,75

Усл. обозначения

	Розетка одногнездовая 16А, IP20, 250В
	Розетка двухгнездовая 16А, IP20, 250В
	Розетка трехгнездовая накладная 16А, IP20, 250В
	Розетка одногнездовая с крышкой и шторками 16А, IP44, 250В
	Розетка двухгнездовая с крышкой и шторками 16А, IP44, 250В
	Розетка одногнездовая 32А, IP20, 250В
	Розетка RJ45 (телефон и интернет)

Внимание!
Заглушить все
розетки
не по проекту!

Рабочий проект

ЖК Shabyt


Лист

12

Листов

18

План расстановки розеток

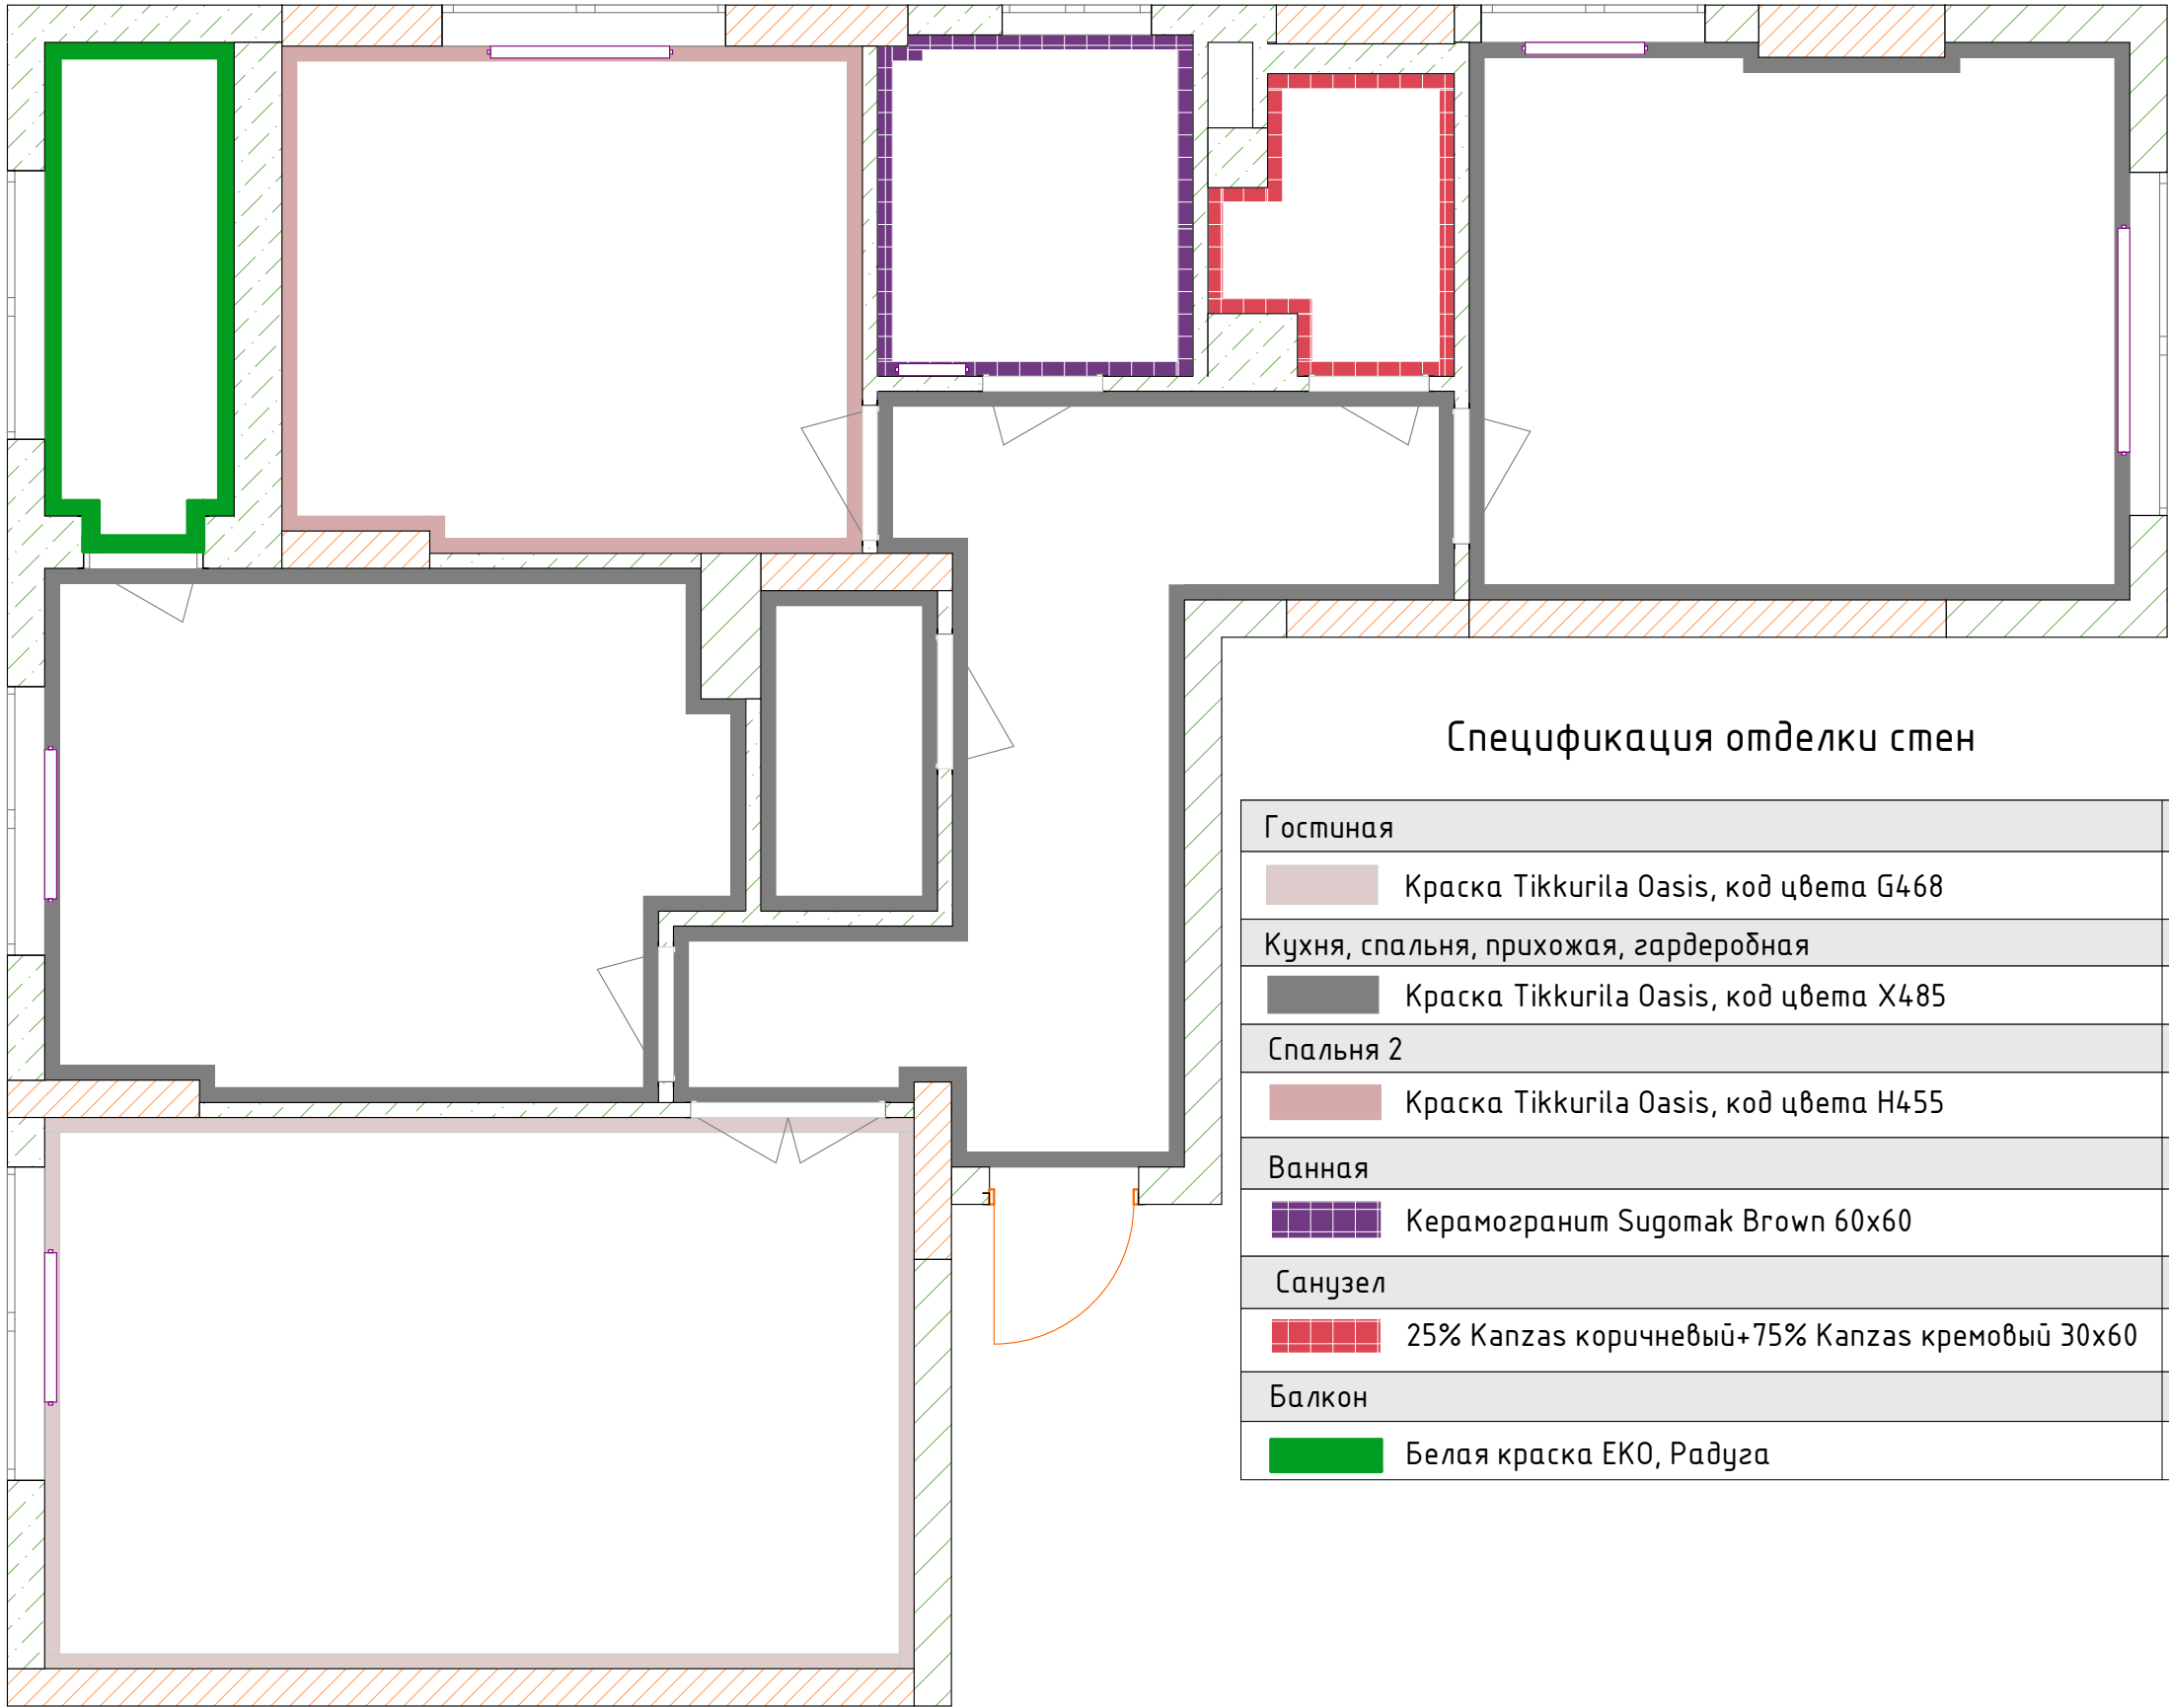

Спецификация отделки стен

Гостиная	S, м²
Краска Tikkurila Oasis, код цвета G468	49,95
Кухня, спальня, прихожая, гардеробная	
Краска Tikkurila Oasis, код цвета X485	155,26
Спальня 2	
Краска Tikkurila Oasis, код цвета H455	38,05
Ванная	
Керамогранит Sugomak Brown 60x60	22,37
Санузел	
25% Kanzas коричневый+75% Kanzas кремовый 30x60	21,42
Балкон	
Белая краска ЕКО, Радуга	23,12

Экспликация помещений после монтажных работ		
№	Наименование помещения	Площадь, м²
1	Прихожая	13,61
2	Гостиная	21,55
3	Кухня	15,37
4	Спальня	16,57
5	Спальня 2	13,32
6	Ванная	4,52
7	Санузел	2,75
8	Гардеробная	2,5
9	Балкон	3,75

Рабочий проект

ЖК Shabyt




Лист

13

Листов


18

План отделки стен

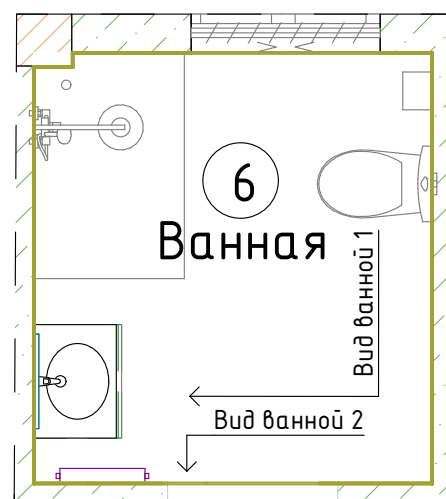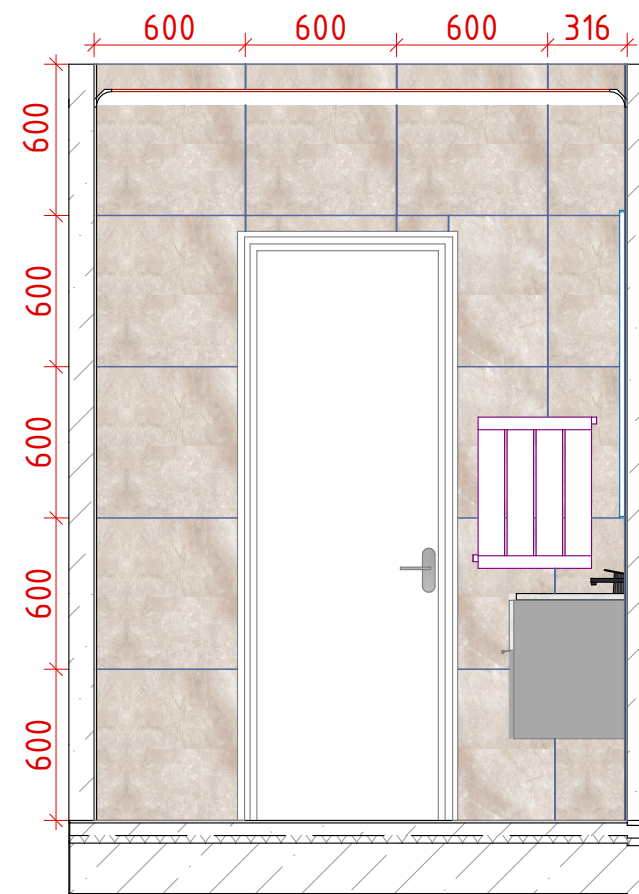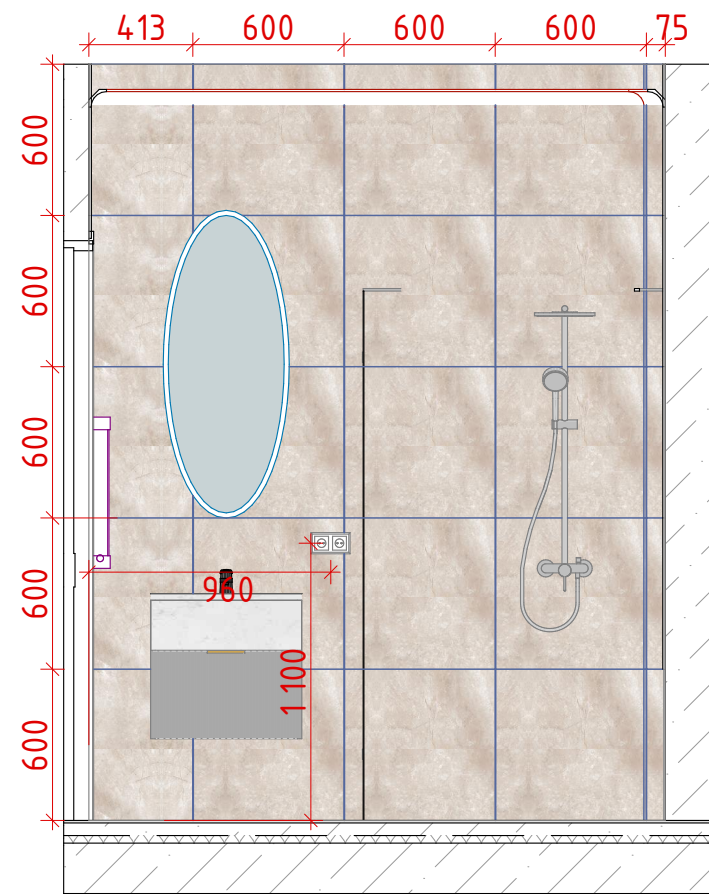


№	Наименование помещения	Площадь, м ²
1	Прихожая	13,61
2	Гостиная	21,55
3	Кухня	15,37
4	Спальня	16,57
5	Спальня 2	13,32
6	Ванная	4,52
7	Санузел	2,75
8	Гардеробная	2,5
9	Балкон	3,75


Рабочий проект		
ЖК Shabyt	Лист	Листов
	14	18
План развертки стен ванной 1 часть		

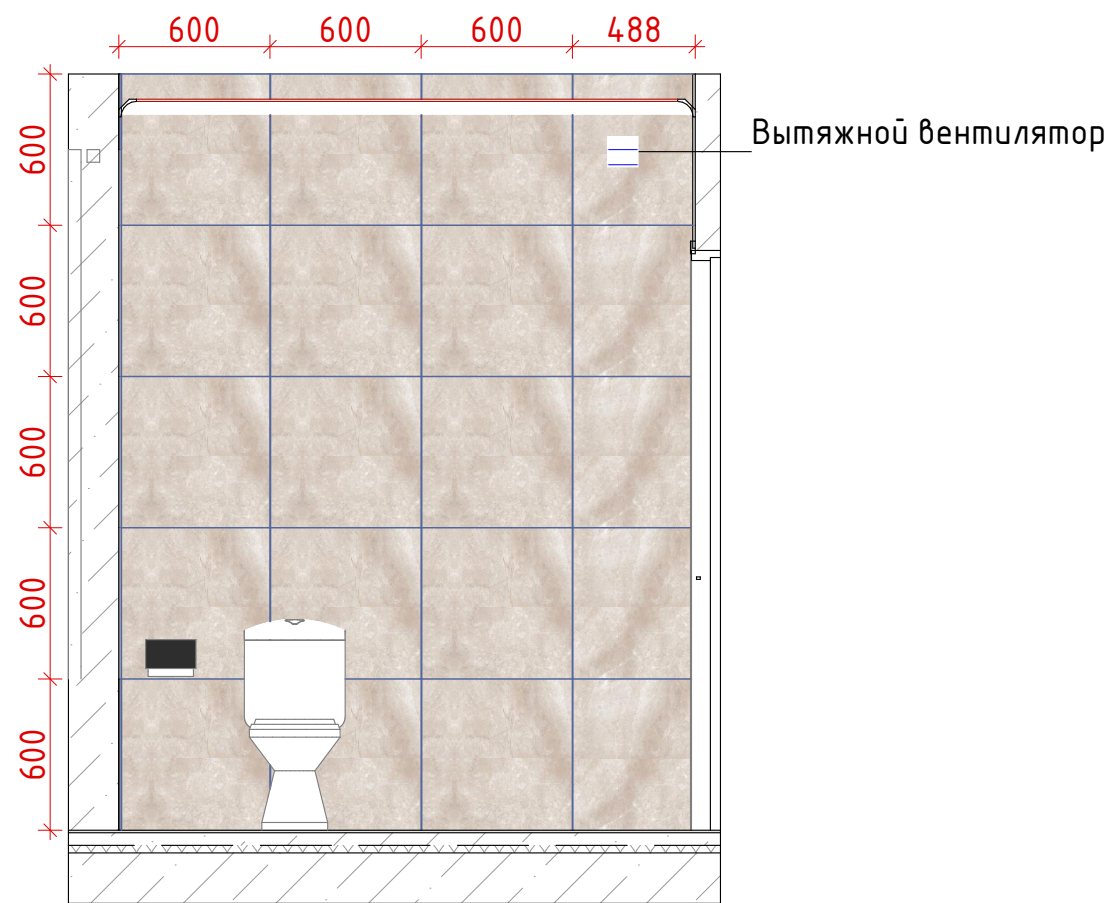

Вид Ванной 3

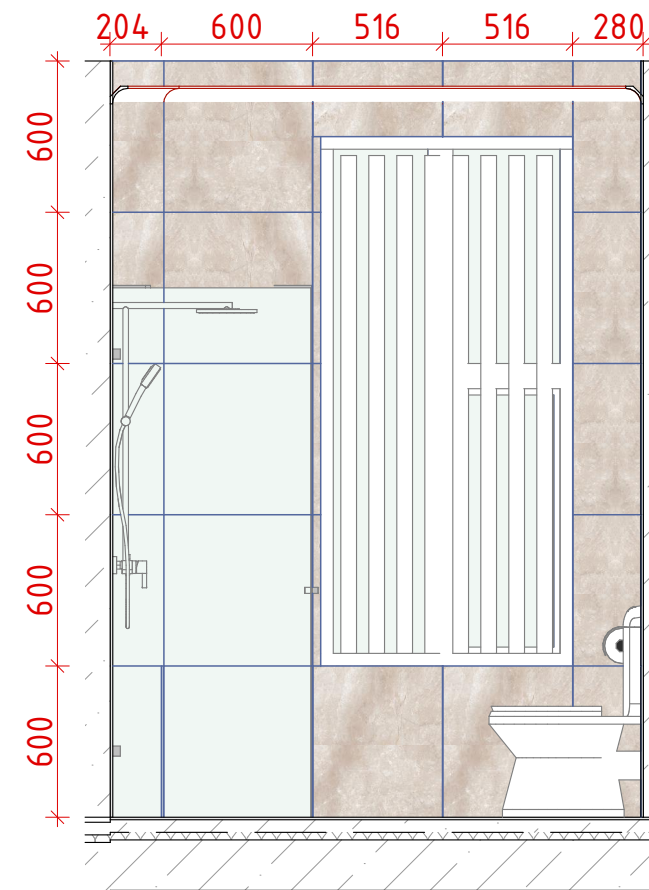

Вид ванной 4

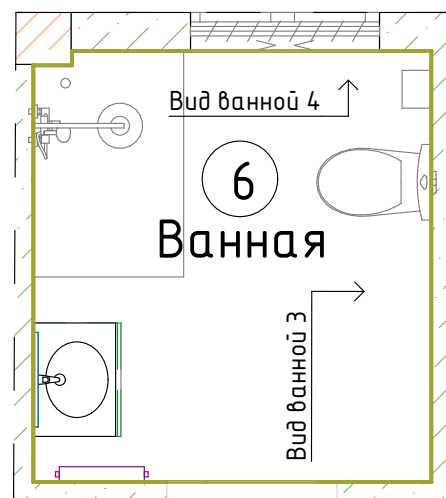

Наименование материала	S, м²	Кол-во, шт
Керамогранит Sugomak brown 60x60	22,37	72


Экспликация помещений после монтажных работ		
№	Наименование помещения	Площадь, м²
1	Прихожая	13,61
2	Гостиная	21,55
3	Кухня	15,37
4	Спальня	16,57
5	Спальня 2	13,32
6	Ванная	4,52
7	Санузел	2,75
8	Гардеробная	2,5
9	Балкон	3,75

Примечание:


Расстояние розеток
указано от чистой стены.

Высота установки розеток
300мм от чистового пола,
если иное не указано.

Рабочий проект		
ЖК Shabyt	Лист	Листов
	15	18
План развертки стен ванной 2 часть		

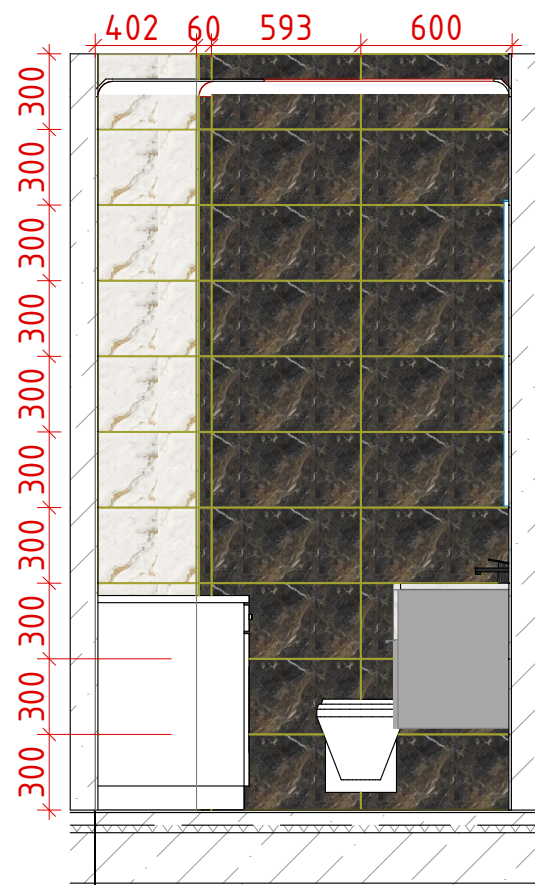


Вид санузла 1

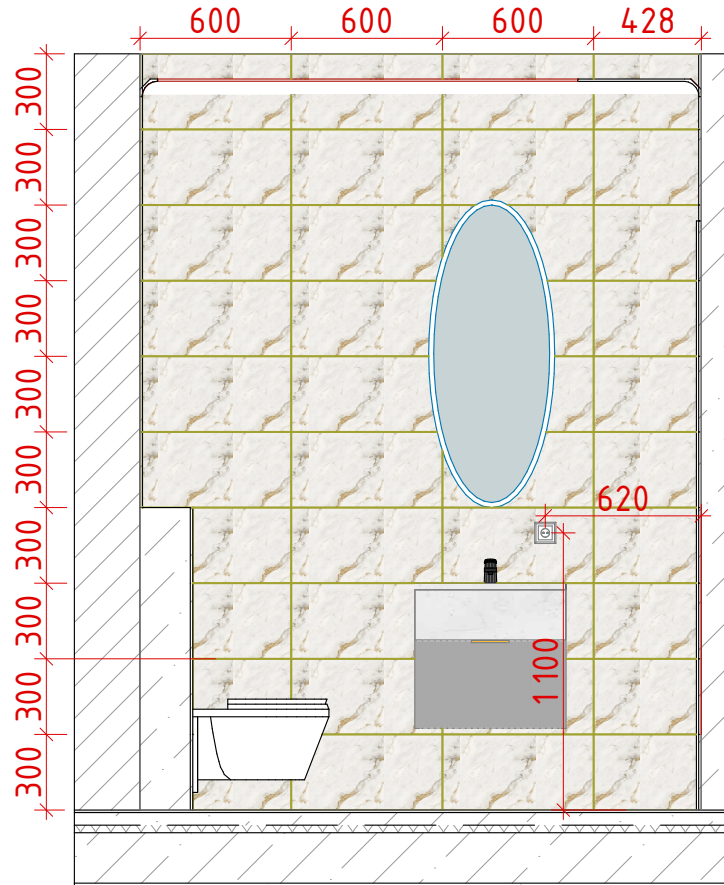

Вид санузла 2

7
Санузел

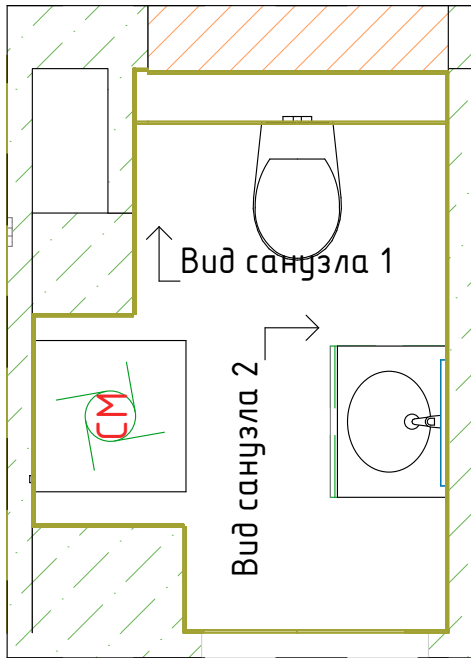

Экспликация помещений после монтажных работ		
№	Наименование помещения	Площадь, м²
1	Прихожая	13,61
2	Гостиная	21,55
3	Кухня	15,37
4	Спальня	16,57
5	Спальня 2	13,32
6	Ванная	4,52
7	Санузел	2,75
8	Гардеробная	2,5
9	Балкон	3,75

Рабочий проект		
ЖК Shabyt	Лист	Листов
	16	18
План развертки стен санузла 1 часть		



Наименование материала	S, м ²	Кол-во, шт
Плитка настенная Kanzas коричневый 30x60	3,75	22
Плитка настенная Kanzas кремовый 30x60	17,67	103

Экспликация помещений после монтажных работ		
№	Наименование помещения	Площадь, м ²
1	Прихожая	13,61
2	Гостиная	21,55
3	Кухня	15,37
4	Спальня	16,57
5	Спальня 2	13,32
6	Ванная	4,52
7	Санузел	2,75
8	Гардеробная	2,5
9	Балкон	3,75

Примечание:

Расстояние розеток
указано от чистовой стены.


Высота установки розеток
300мм от чистового пола,
если иное не указано.

Рабочий проект		
ЖК Shabyt	Лист	Листов
	17	18

План развертки стен санузла 2 часть
--



Вид кухни 1

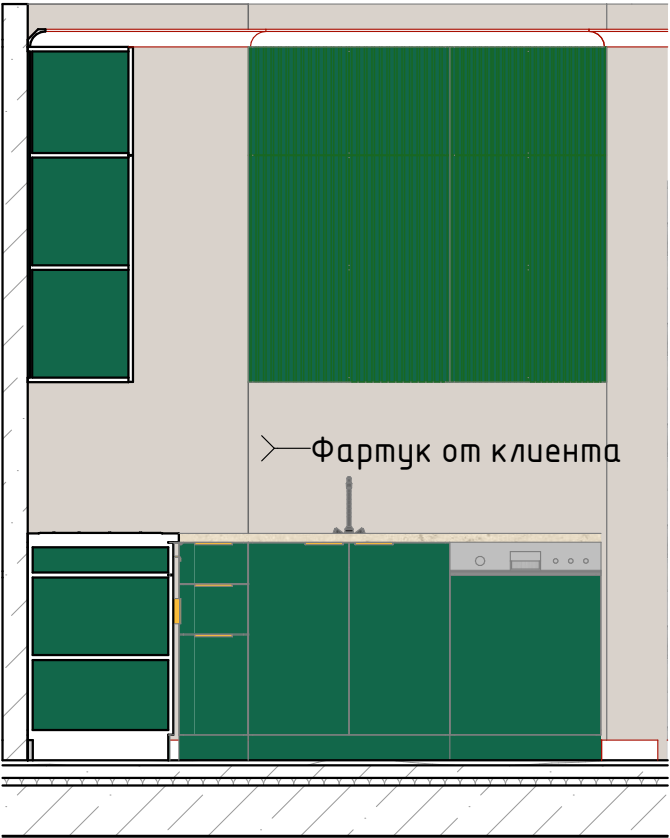


Вид кухни 2

Экспликация помещений после монтажных работ		
№	Наименование помещения	Площадь, м²
1	Прихожая	13,61
2	Гостиная	21,55
3	Кухня	15,37
4	Спальня	16,57
5	Спальня 2	13,32
6	Ванная	4,52
7	Санузел	2,75
8	Гардеробная	2,5
9	Балкон	3,75

Примечание:

Расстояние розеток
указано от чистой
стены.

Высота установки
розеток 300мм от
чистового пола,
если иное не указано.

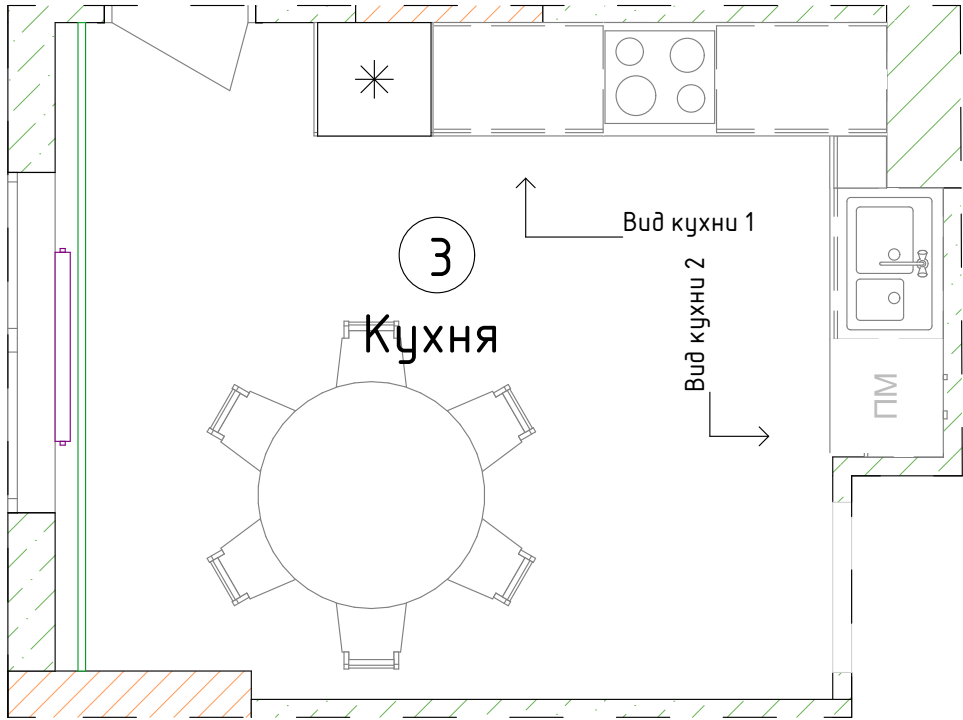

Рабочий проект		
ЖК Shabyt	Лист	Листов
	18	18
План развертки стен кухни		