

Рабочий проект
Квартиры
в ЖК Monaco Residence
130 м2

Заказчик:

Разработчик проекта:
Акмарал Қалиева

Астана 2024

Общие данные

Объект: г.Астана ЖК Monaco Residence. Проект разработан на основании задания на проектирование и согласованной заказчиком планировочной схемы, с учетом обмерочных чертежей существующих помещений, в соответствии с действующими нормами и правилами.

Данный эскизный проект не затрагивает интересы смежных собственников.

Расчетная прочность конструкций не снижается

Архитектурно-эстетические, противопожарные, противовзрывные и санитарные качества не ухудшаются.

Вредное воздействие на окружающую среду не оказывается.

Нормы инсоляции и освещенности не нарушаются.

Перепланировка квартиры осуществляется в пределах существующих помещений, вследствие чего их назначение остается неизменным.

Проектом предусмотрен:

- демонтаж внутренних стен и перегородок, не нарушающий несущих конструкций.

Конструктивная схема:

- каркас - монолитный
- перекрытие - монолитное
- внутренние стены - газоблок

Работа по сносу, перепланировке и реконструкции несущих стен на данном объекте не ведется.

Инженерные системы и оборудование не переносятся.

Общие указания:

В случае выявления, при производстве работ, несоответствий по заявленной конструктивной схеме, аварийного состояния сущ.конструкций, распределение нагрузок на несущие элементы здания, не учтенные проектом - работы немедленно остановить. Не допускать производство работ по разрушению механизированными методами. Разработку (разрушение)вести с применением ручных инструментов и машин.

Демонтаж вести поэлементно, не допуская дополнительных напряжений и деформаций в сохраняемых конструкциях.

Чертежи выполнены по результатам натурных обмеров.

Творческая мастерская "adilova design


График работ:

ПН-ПТ 10:00-18:00

СБ-ВС Выходной


Тел: +7 708 668 23 38 Акмарал

Звонить в рабочее время.

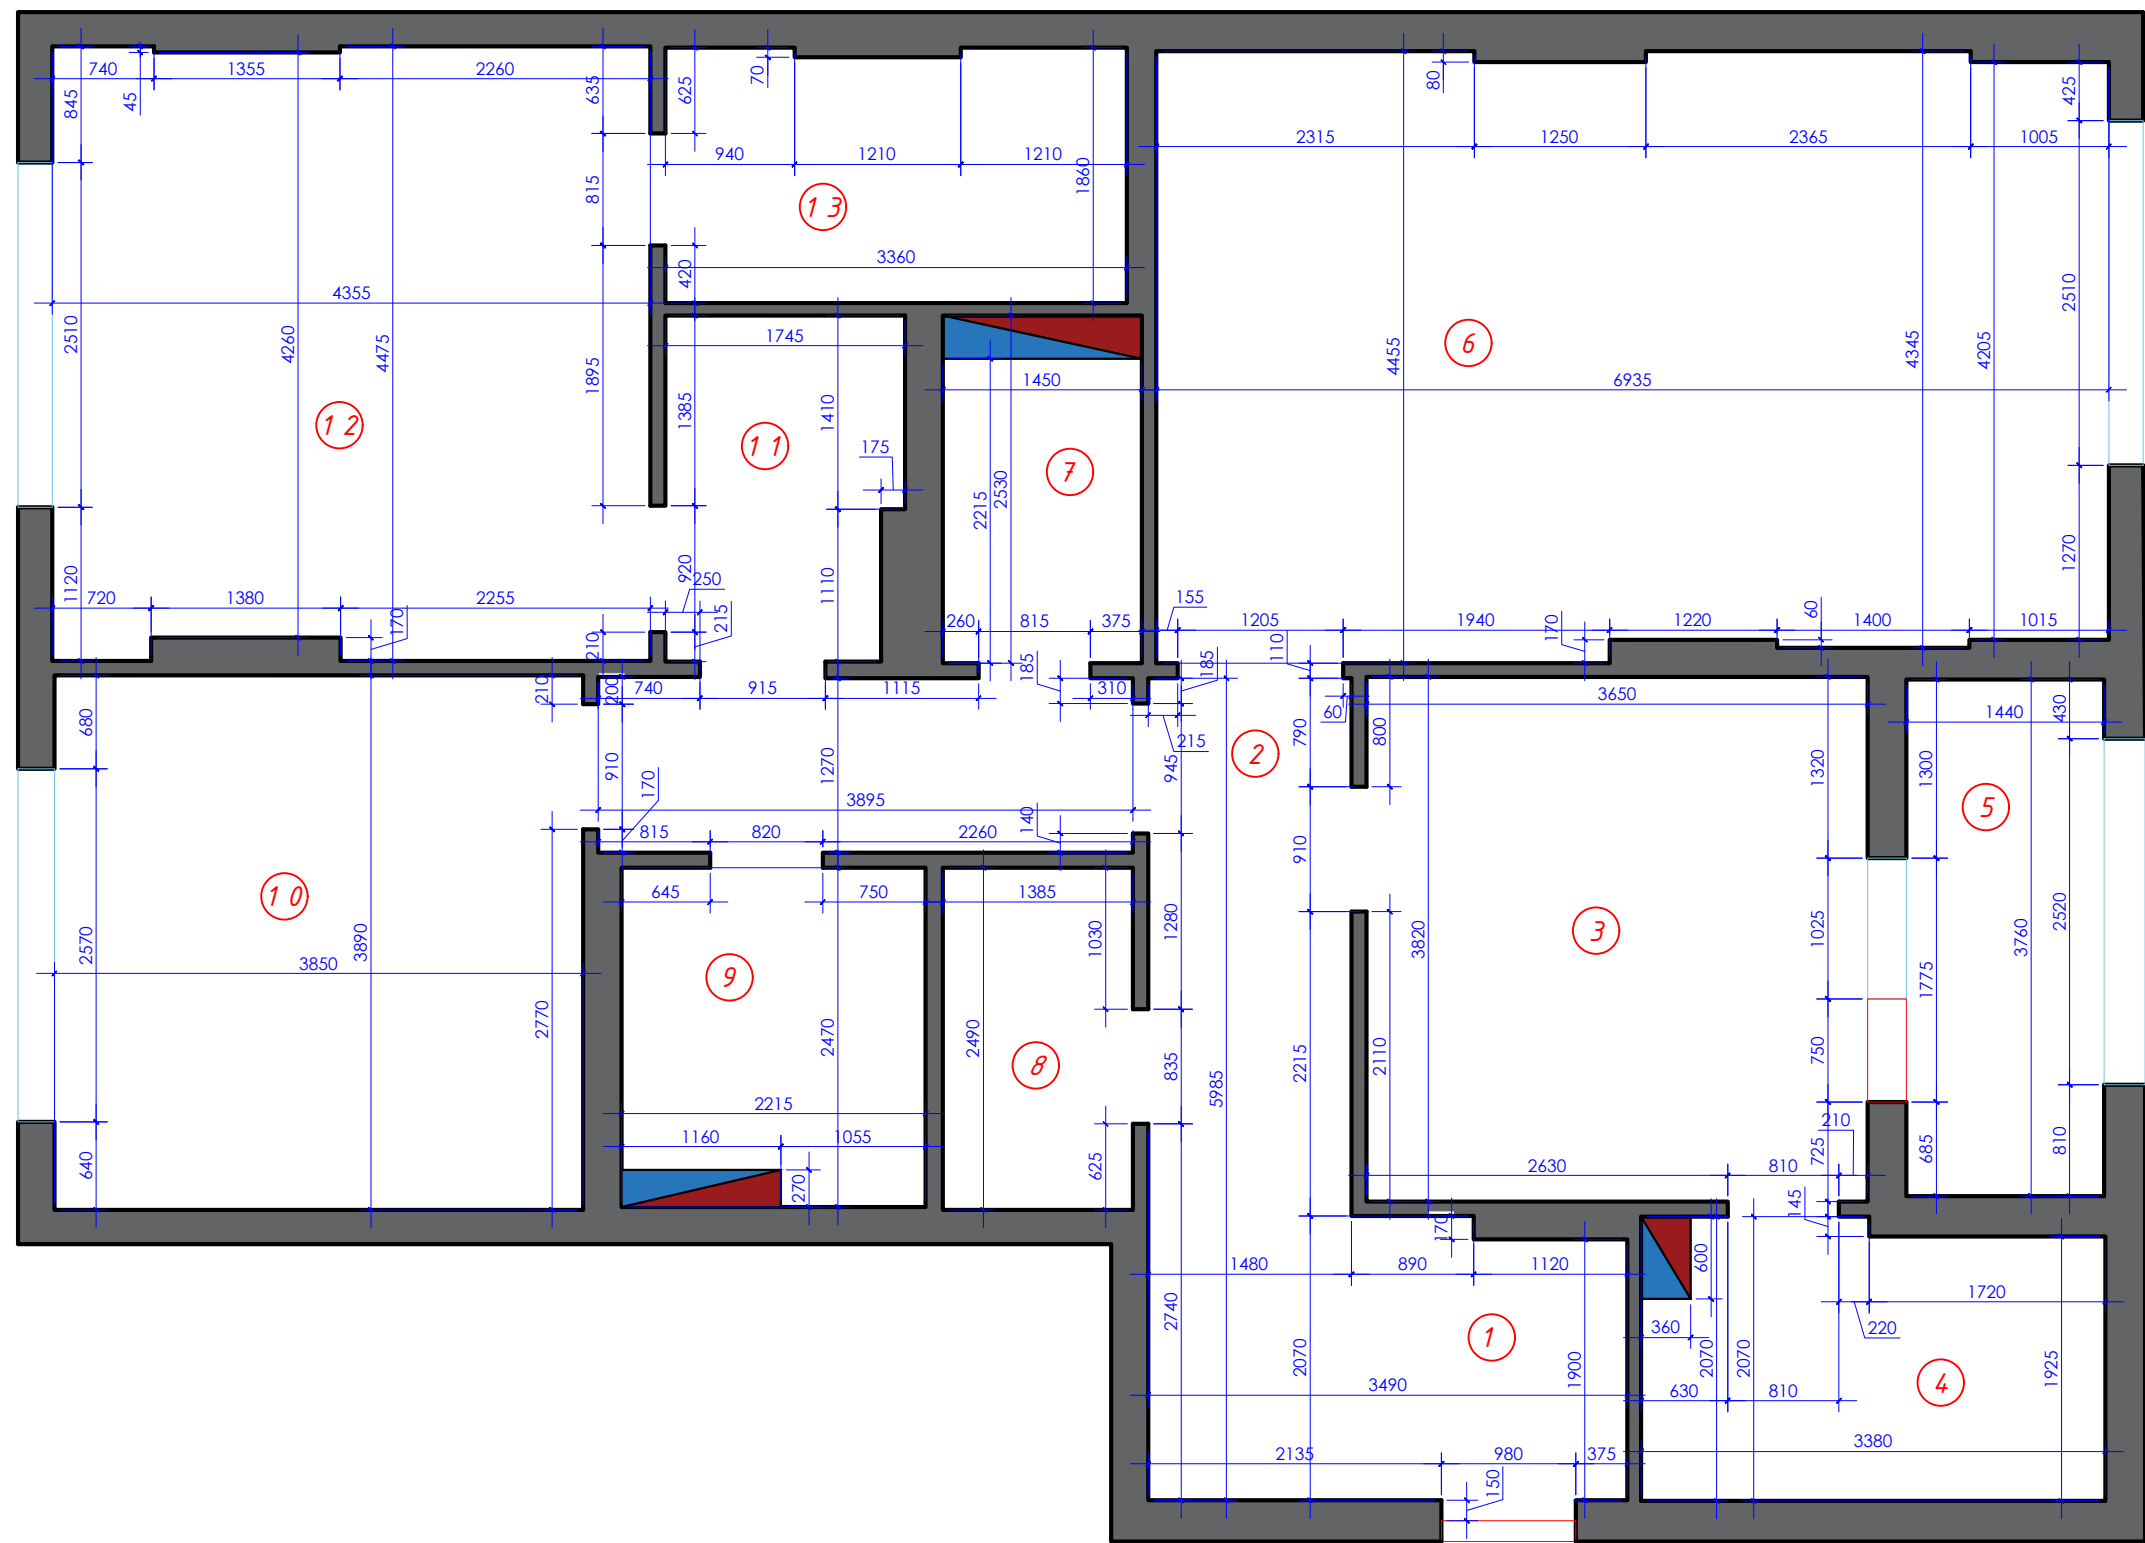

№	Экспликация помещений	м2
1	Прихожая	7,0
2	Зал	10,8
3	Кухня	14,0
4	Коридор	6,5
5	Гост.санузел	5,4
6	Кладовая	30,0
7	Мастер спальня	3,2
8	Мастер гардероб	3,4
9	Мастер санузел	5,1
10	Детская комната девочки	15,0
11	Гардероб мальчиков	4,2
12	Комната мальчиков	19,1
13	Спортивная зона мальчиков	6,2
Итого		130


Н потолка=3020мм
Н сан.узла=3060мм
Н дверных проемов= 2100

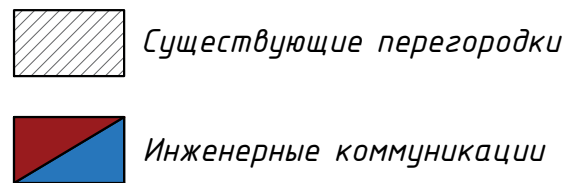

Примечания:
1. Обмер выполнен по существующим размерам.

Рабочий проект квартиры в ЖК Monaco Residence	Стадия	Лист	Листов
	РП		
Обмерный план		adilova_design творческая мастерская	

№	Экспликация помещений	м2
1	Прихожая	7,0
2	Зал	10,8
3	Кухня	14,0
4	Коридор	6,5
5	Гост.санузел	5,4
6	Кладовая	30,0
7	Мастер спальня	3,2
8	Мастер гардероб	3,4
9	Мастер санузел	5,1
10	Детская комната девочки	15,0
11	Гардероб мальчиков	4,2
12	Комната мальчиков	19,1
13	Спортивная зона мальчиков	6,2
Итого		130

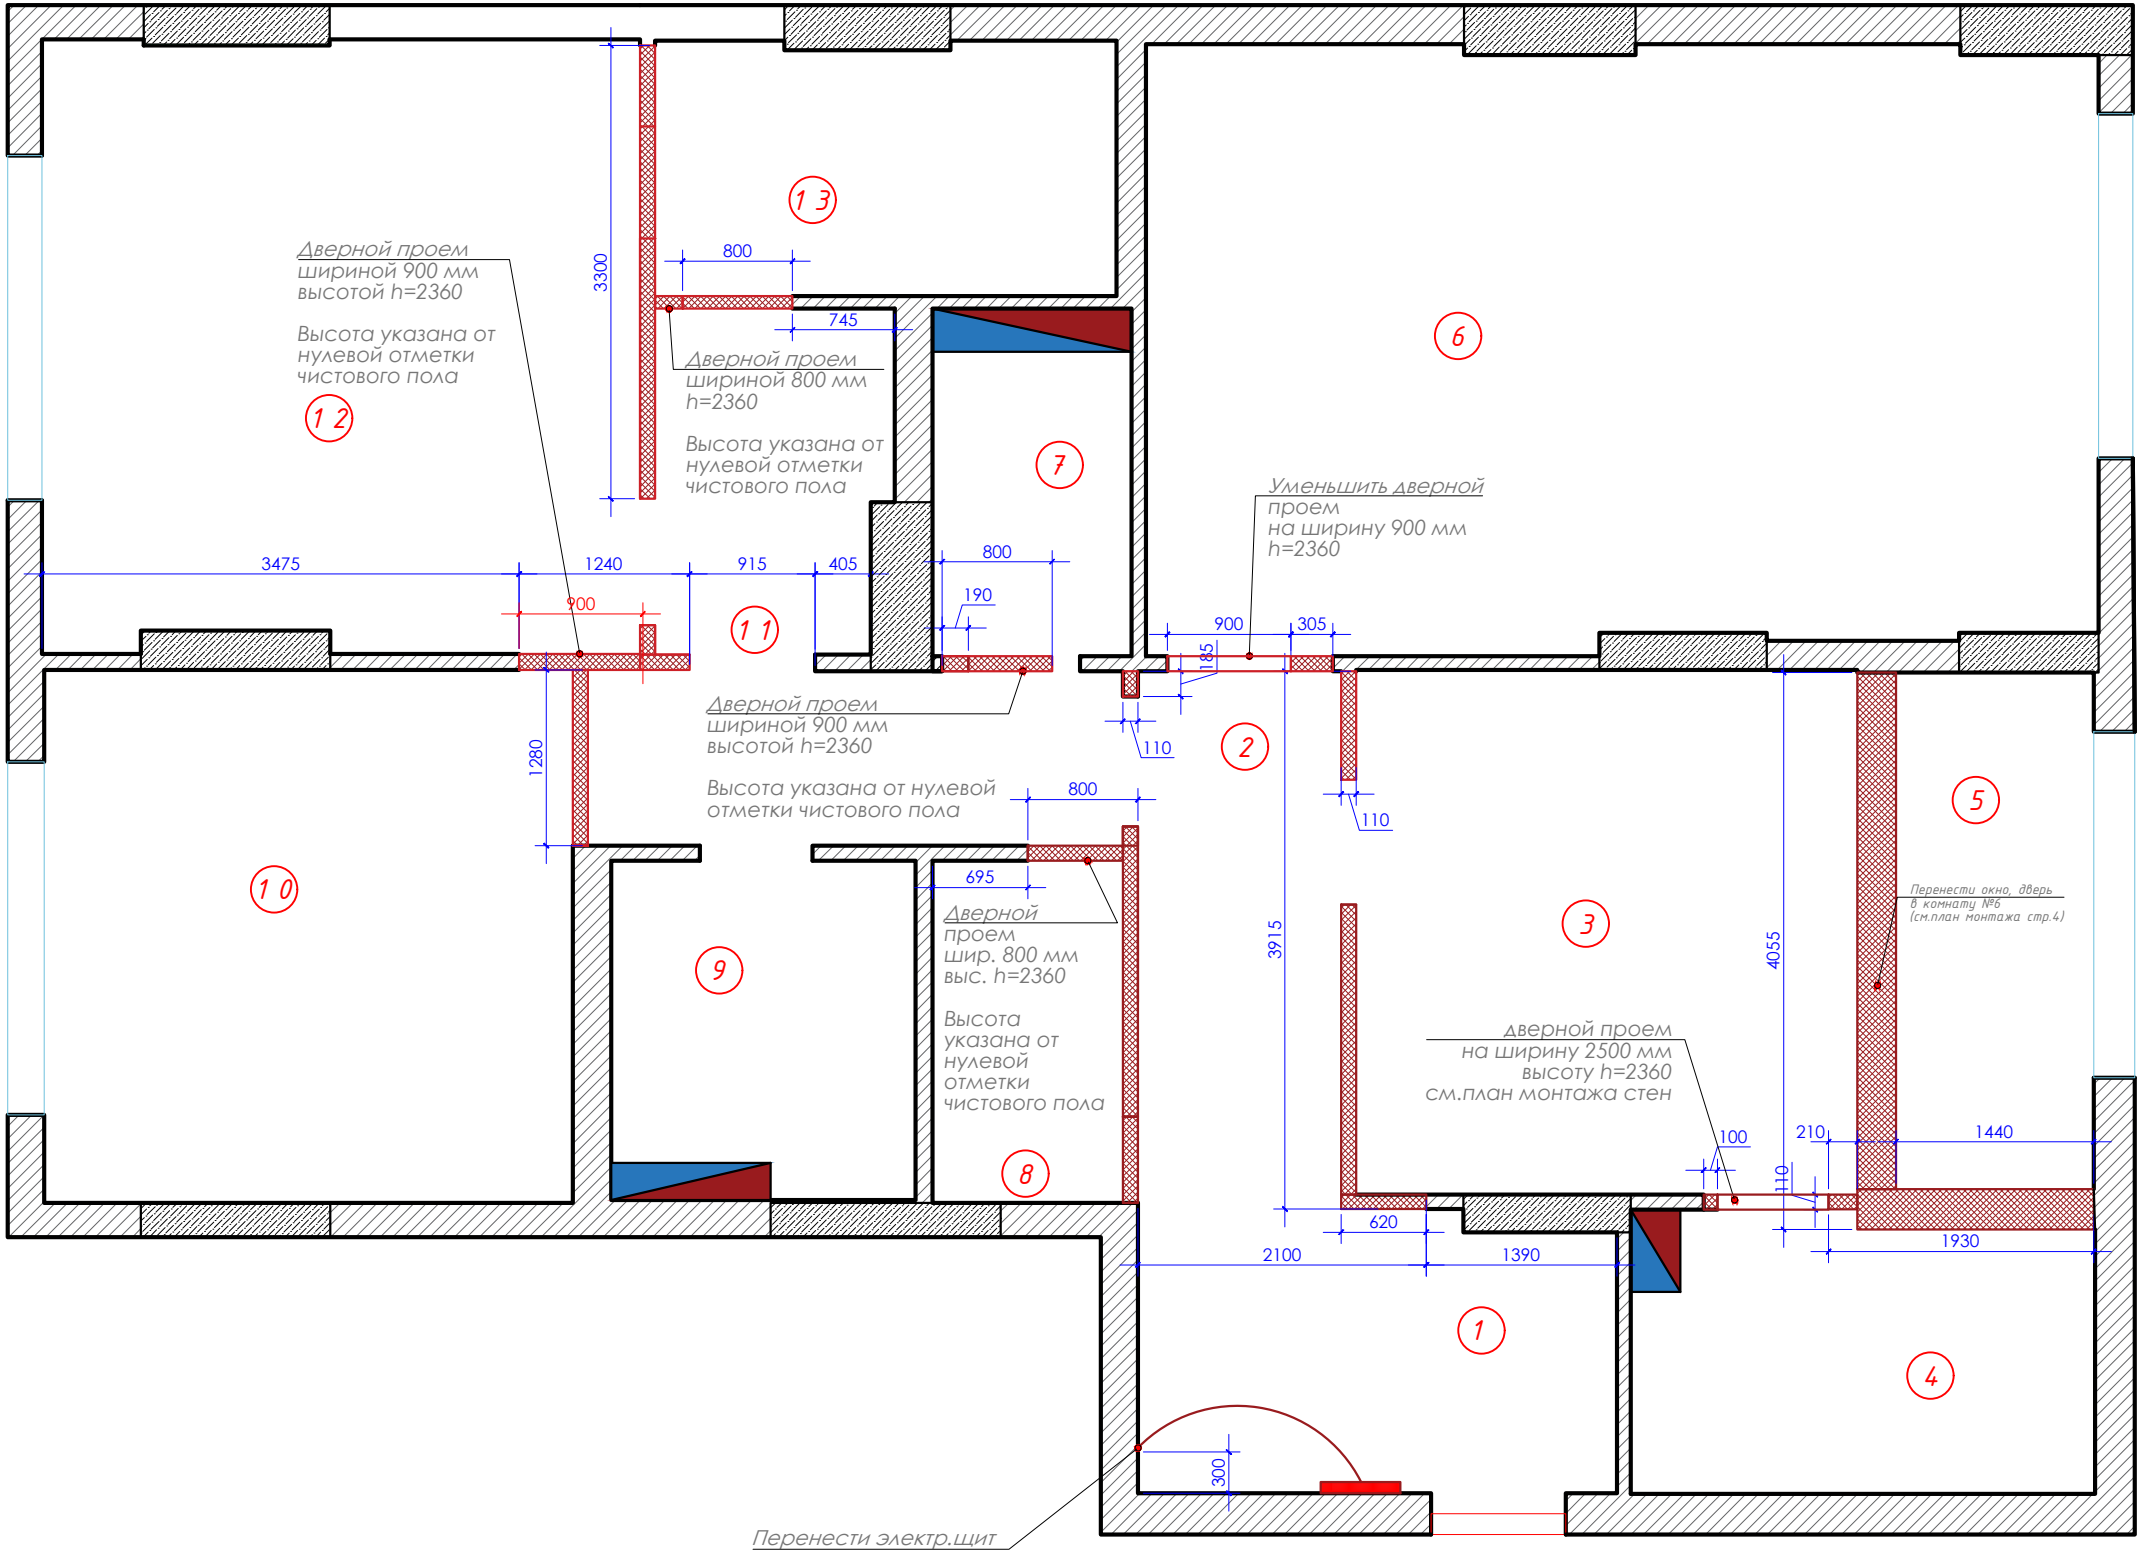

Несущие стены

Существующие перегородки

Инженерные коммуникации

Н потолка=3020мм
Н сан.узла=3060мм
Н дверных проемов= 2100


Условные обозначения.

Демонтируемые стены


Примечание.
1.Чертеж выполнен по результатам натурных обмеров.

Рабочий проект квартиры в ЖК Monaco Residence	Стадия	Лист	Листов
	РП		
План демонтажа		adilova_design творческая мастерская	

№	Экспликация помещений	м2
1	Прихожая	7,0
2	Зал	10,8
3	Кухня	14,0
4	Коридор	6,5
5	Гост.санузел	5,4
6	Кладовая	30,0
7	Мастер спальня	3,2
8	Мастер гардероб	3,4
9	Мастер санузел	5,1
10	Детская комната девочки	15,0
11	Гардероб мальчиков	4,2
12	Комната мальчиков	19,1
13	Спортивная зона мальчиков	6,2
Итого		130

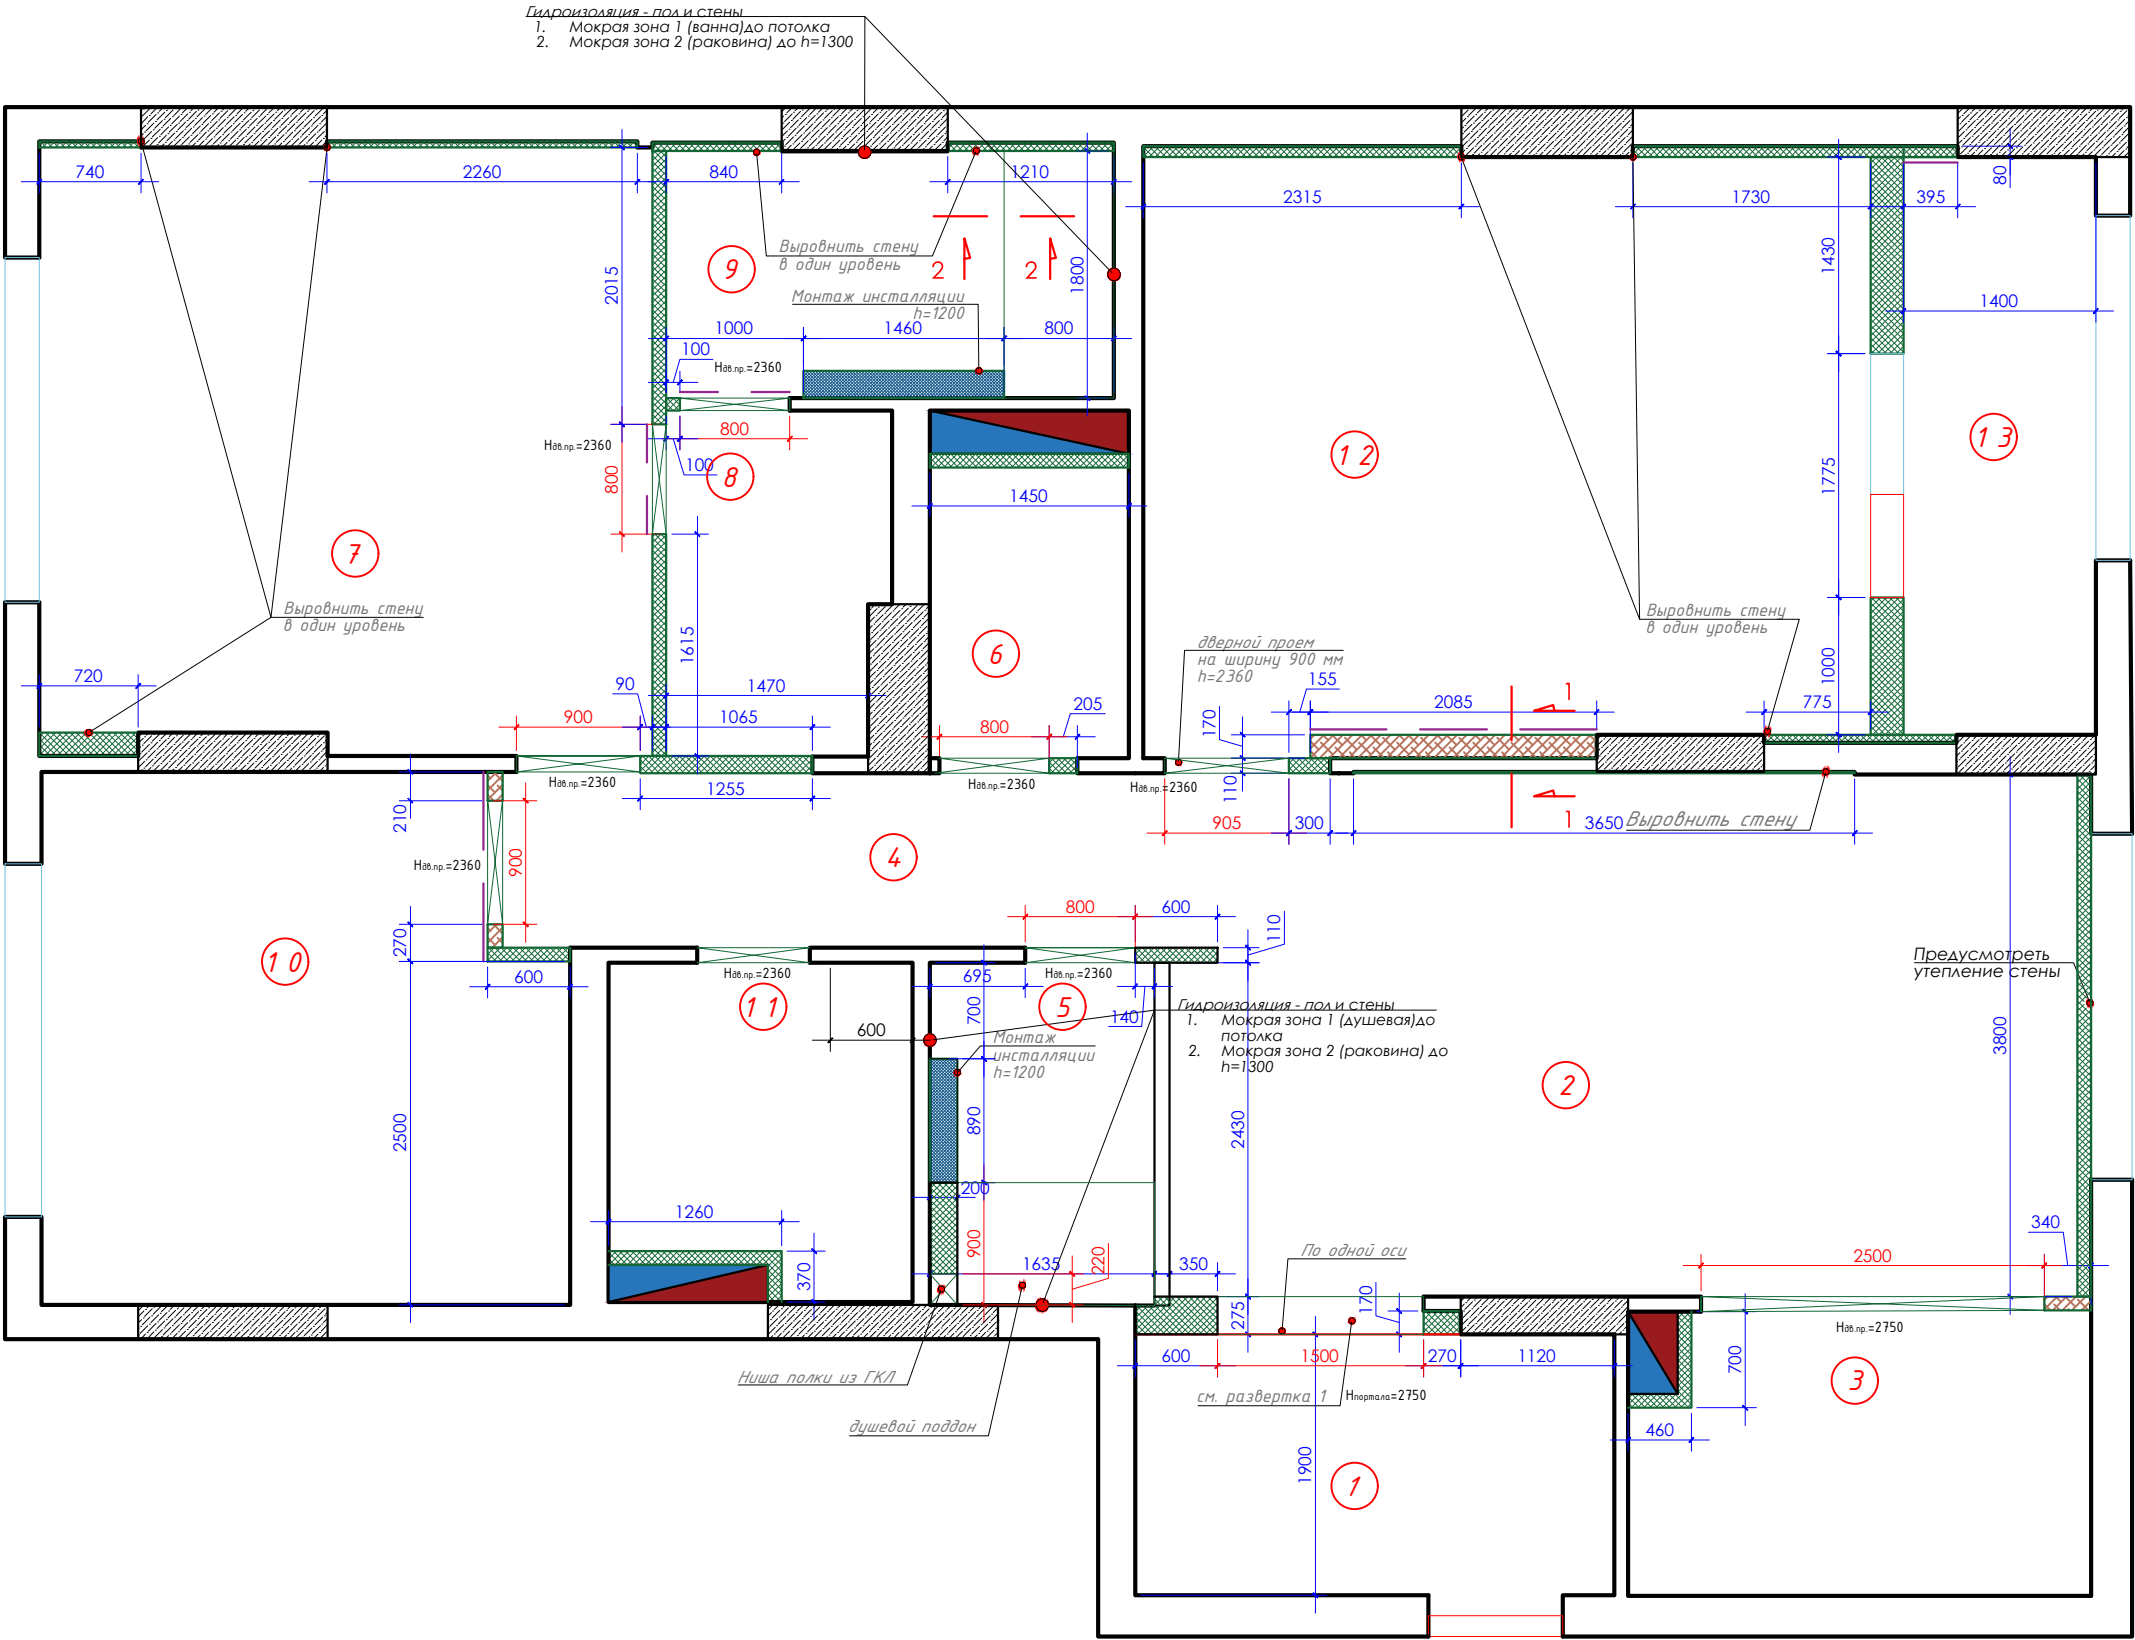

Развертка 1

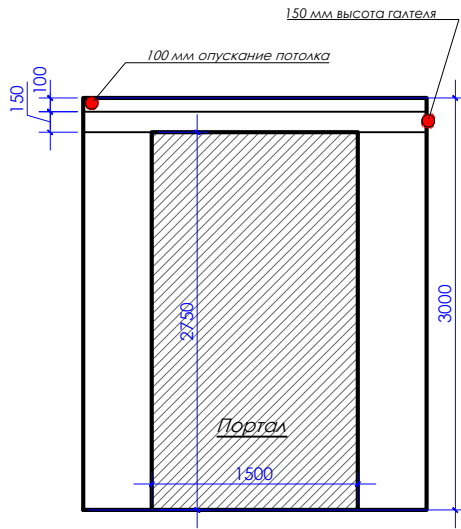

Условные обозначения:


№	Наименование	Обозначение
1	Несущие конструкции	
2	Возводимые стены	
3	Возводимый короб ГКЛ с усилением	
4	Решетка вентиляции	
5	Монтаж инсталляции	
6	Возводимые дверные проемы	
7	Усиление	

Примечания:


- 1.Размеры, показанные на чертеже являются проектными, по факту строительства могут изменяться в большую или меньшую сторону.
- 2.Вентиляционные короба и канализационные стояки необходимо изолировать звукоизолирующим материалом.
- 3.Проверить звуко-/гидроизоляцию в зоне кухни/санузла и заложить заново где необходимо.
- 4.Привязку для монтажа перегородок вести по колоннам, инженерным коммуникация и существующим конструкциям.
- 5.При возведении коробов из гипсокартона максимально ближе прижиматься к коммуникациям.
- 6.В сан.узле и ванной комнате применить влагостойкий гипсокартон.
- 7.Перед возведением перегородок сначала желательно нарисовать все перегородки на полу по проектным размерам.
- 8.ГКЛ перегородки нужно заполнить звукоизолирующей ватой.
- 9.Размеры отмеченные красным цветом не следует делать меньше, чем указано на проекте
10. Принять высоту рабочих дверных проемов **равной 2360 мм** (чистовой отметкой считать уровень покрытия пола *спс* или ламинат).

Рабочий проект квартиры в ЖК Monaco Residence	Стадия	Лист	Листов
	РП		
План возведения стен и перегородок		adilova_design творческая мастерская	


Сечение 1-1

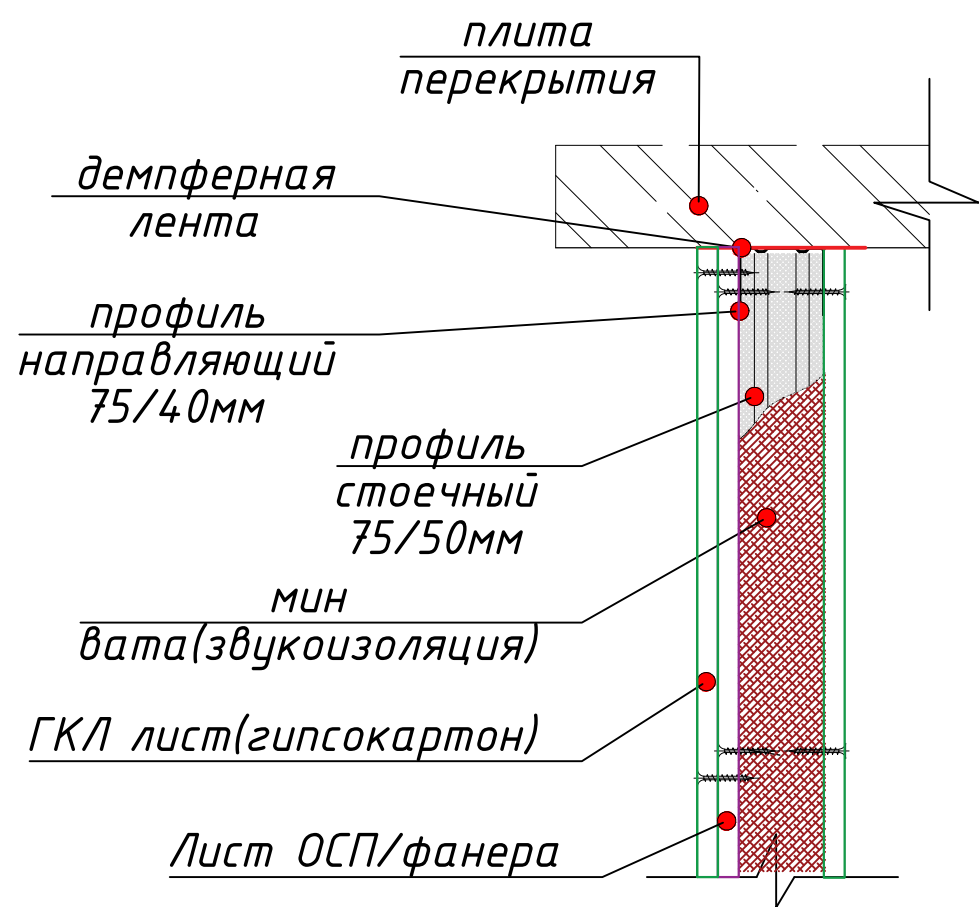

Сечение 2-2
НИША ДЛЯ НОГ В ВАННОЙ С
ПОДСВЕТКОЙ

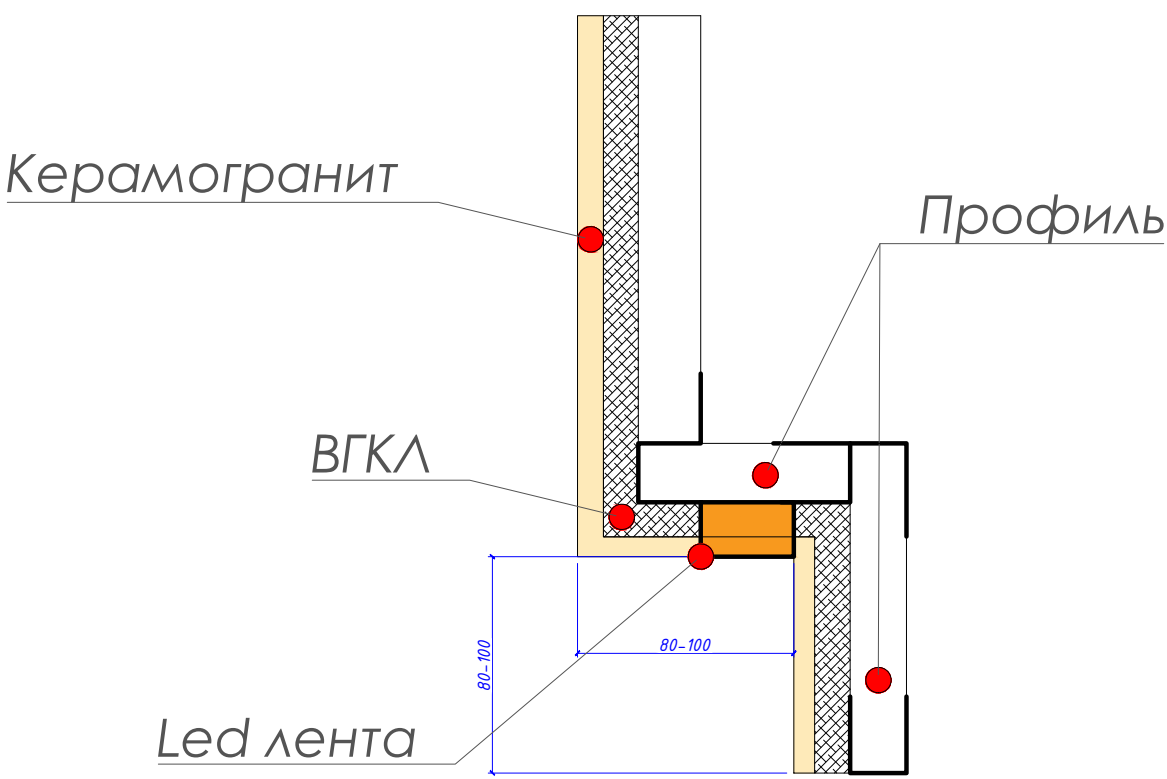


Рабочий проект квартиры в ЖК Monaco Residence	Стадия	Лист	Листов
	РП		
Узлы	adilova_design творческая мастерская		

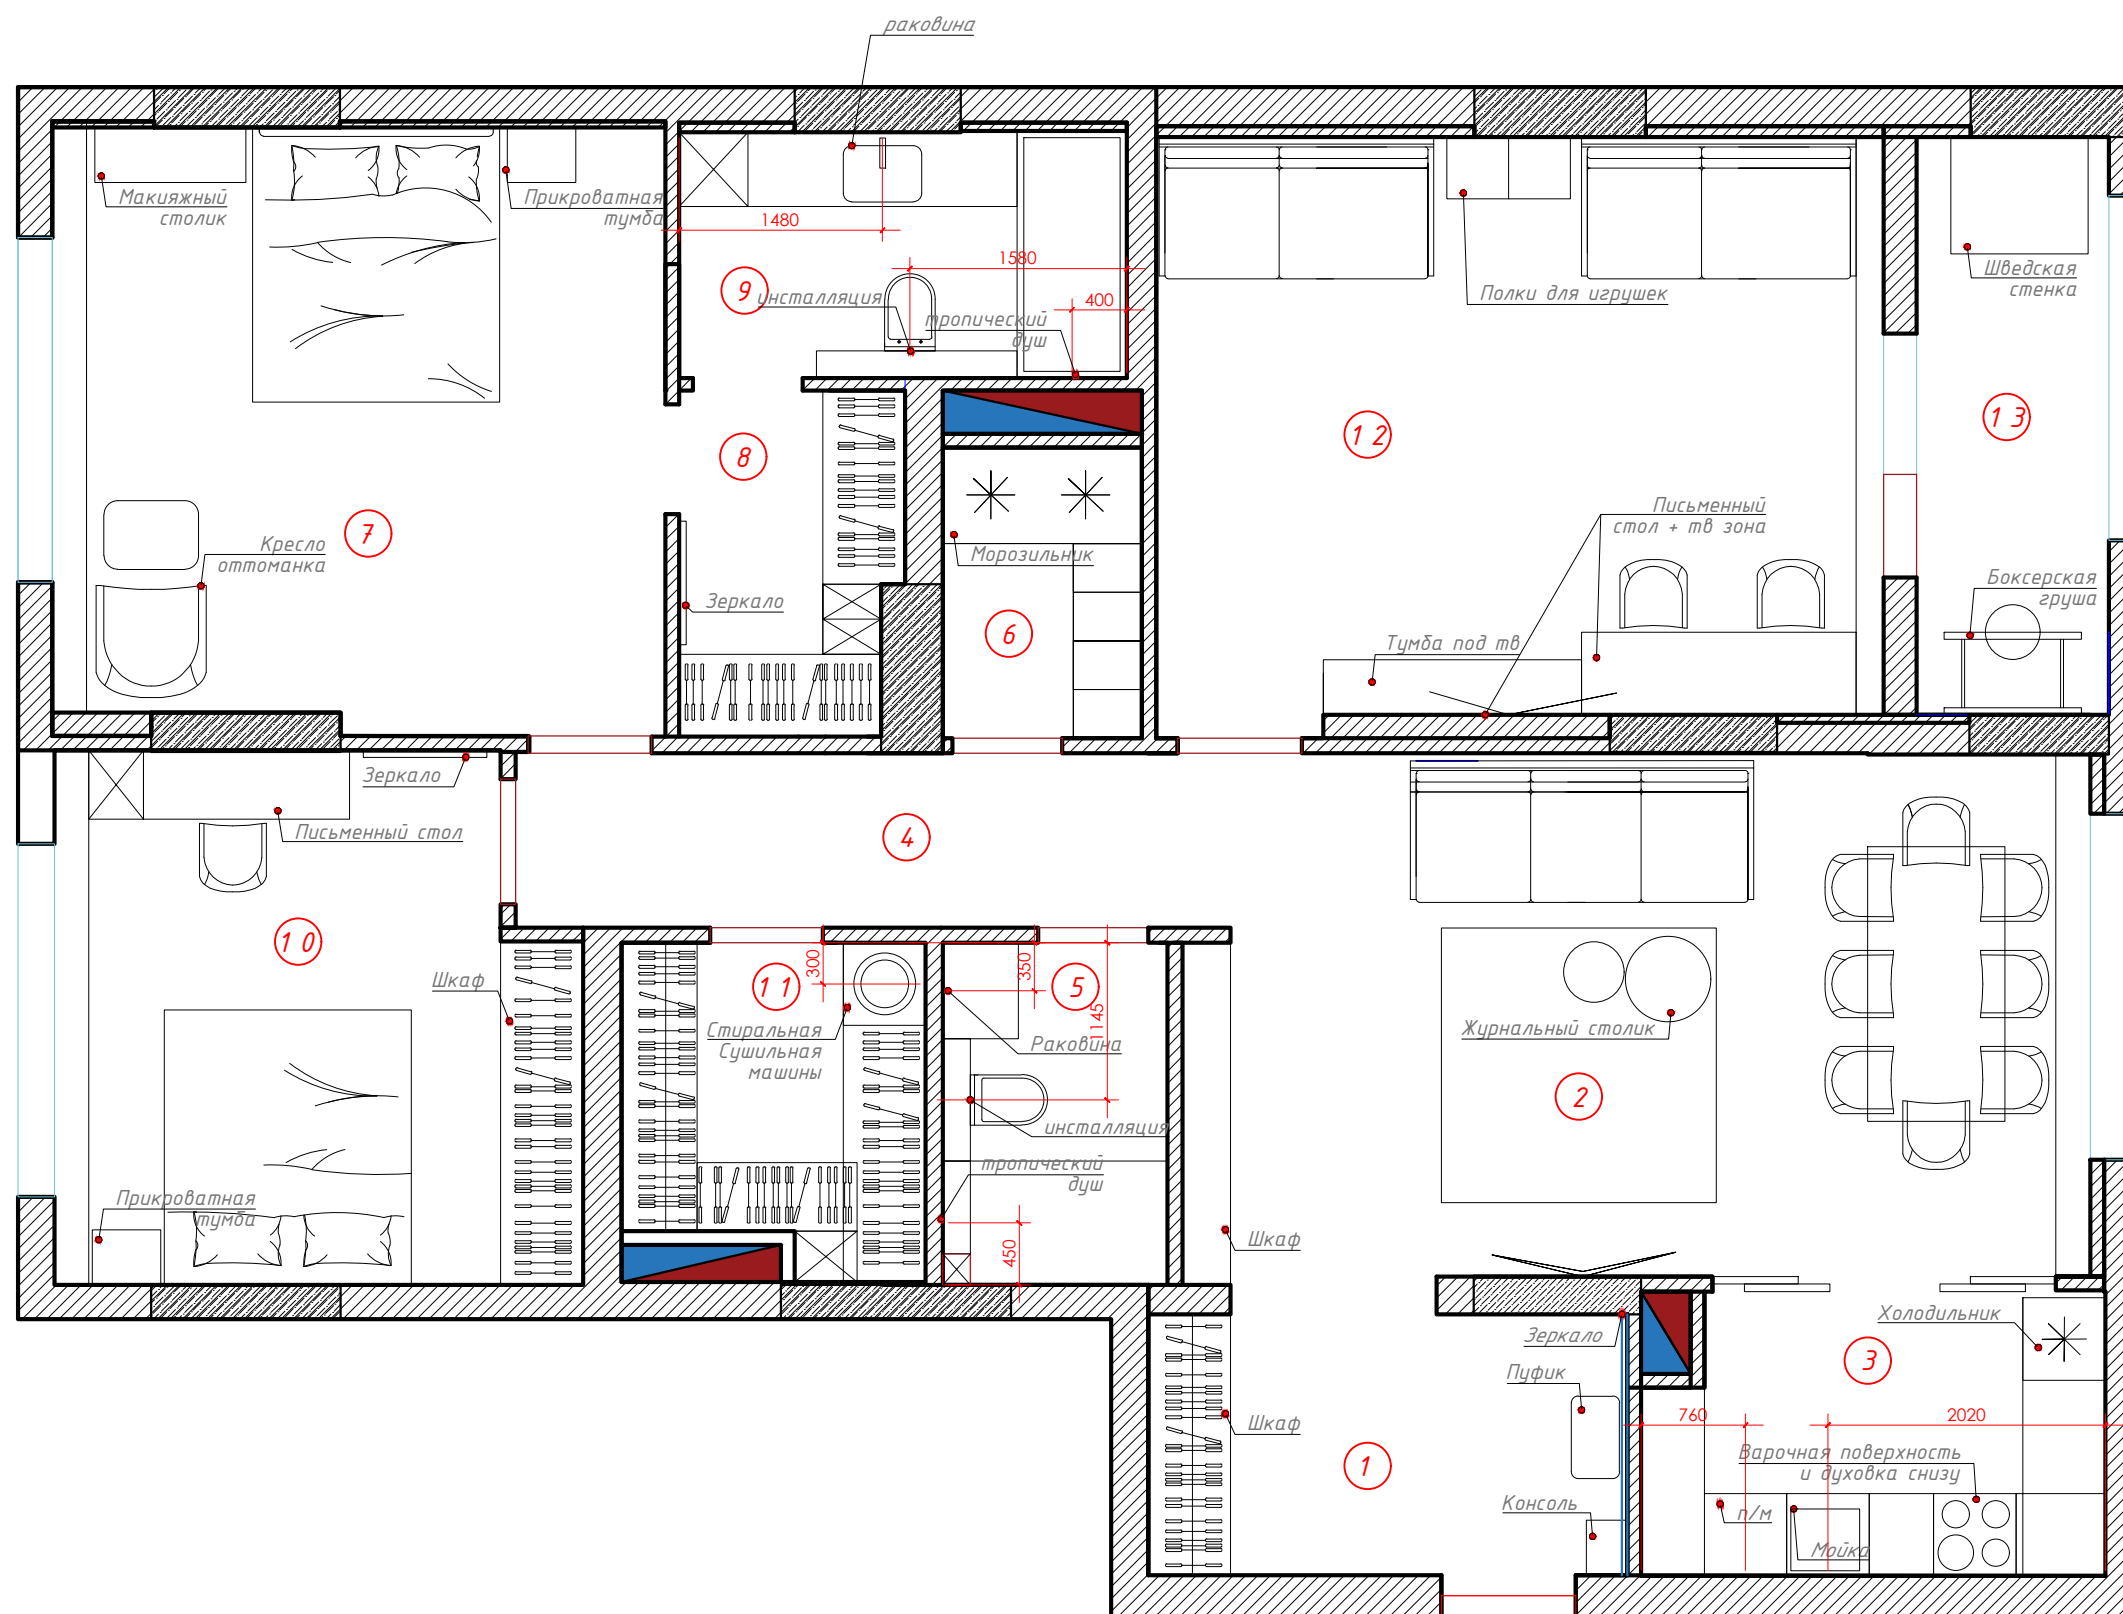


№	Экспликация помещений	м2
1	Прихожая	7,0
2	Зал	10,8
3	Кухня	14,0
4	Коридор	6,5
5	Гост.санузел	5,4
6	Кладовая	30,0
7	Мастер спальня	3,2
8	Мастер гардероб	3,4
9	Мастер санузел	5,1
10	Детская комната девочки	15,0
11	Гардероб мальчиков	4,2
12	Комната мальчиков	19,1
13	Спортивная зона мальчиков	6,2
Итого		130

Рабочий проект квартиры в ЖК Monaco Residence	Стадия	Лист	Листов
	РП		
План расстановки мебели		adilova_design творческая мастерская	

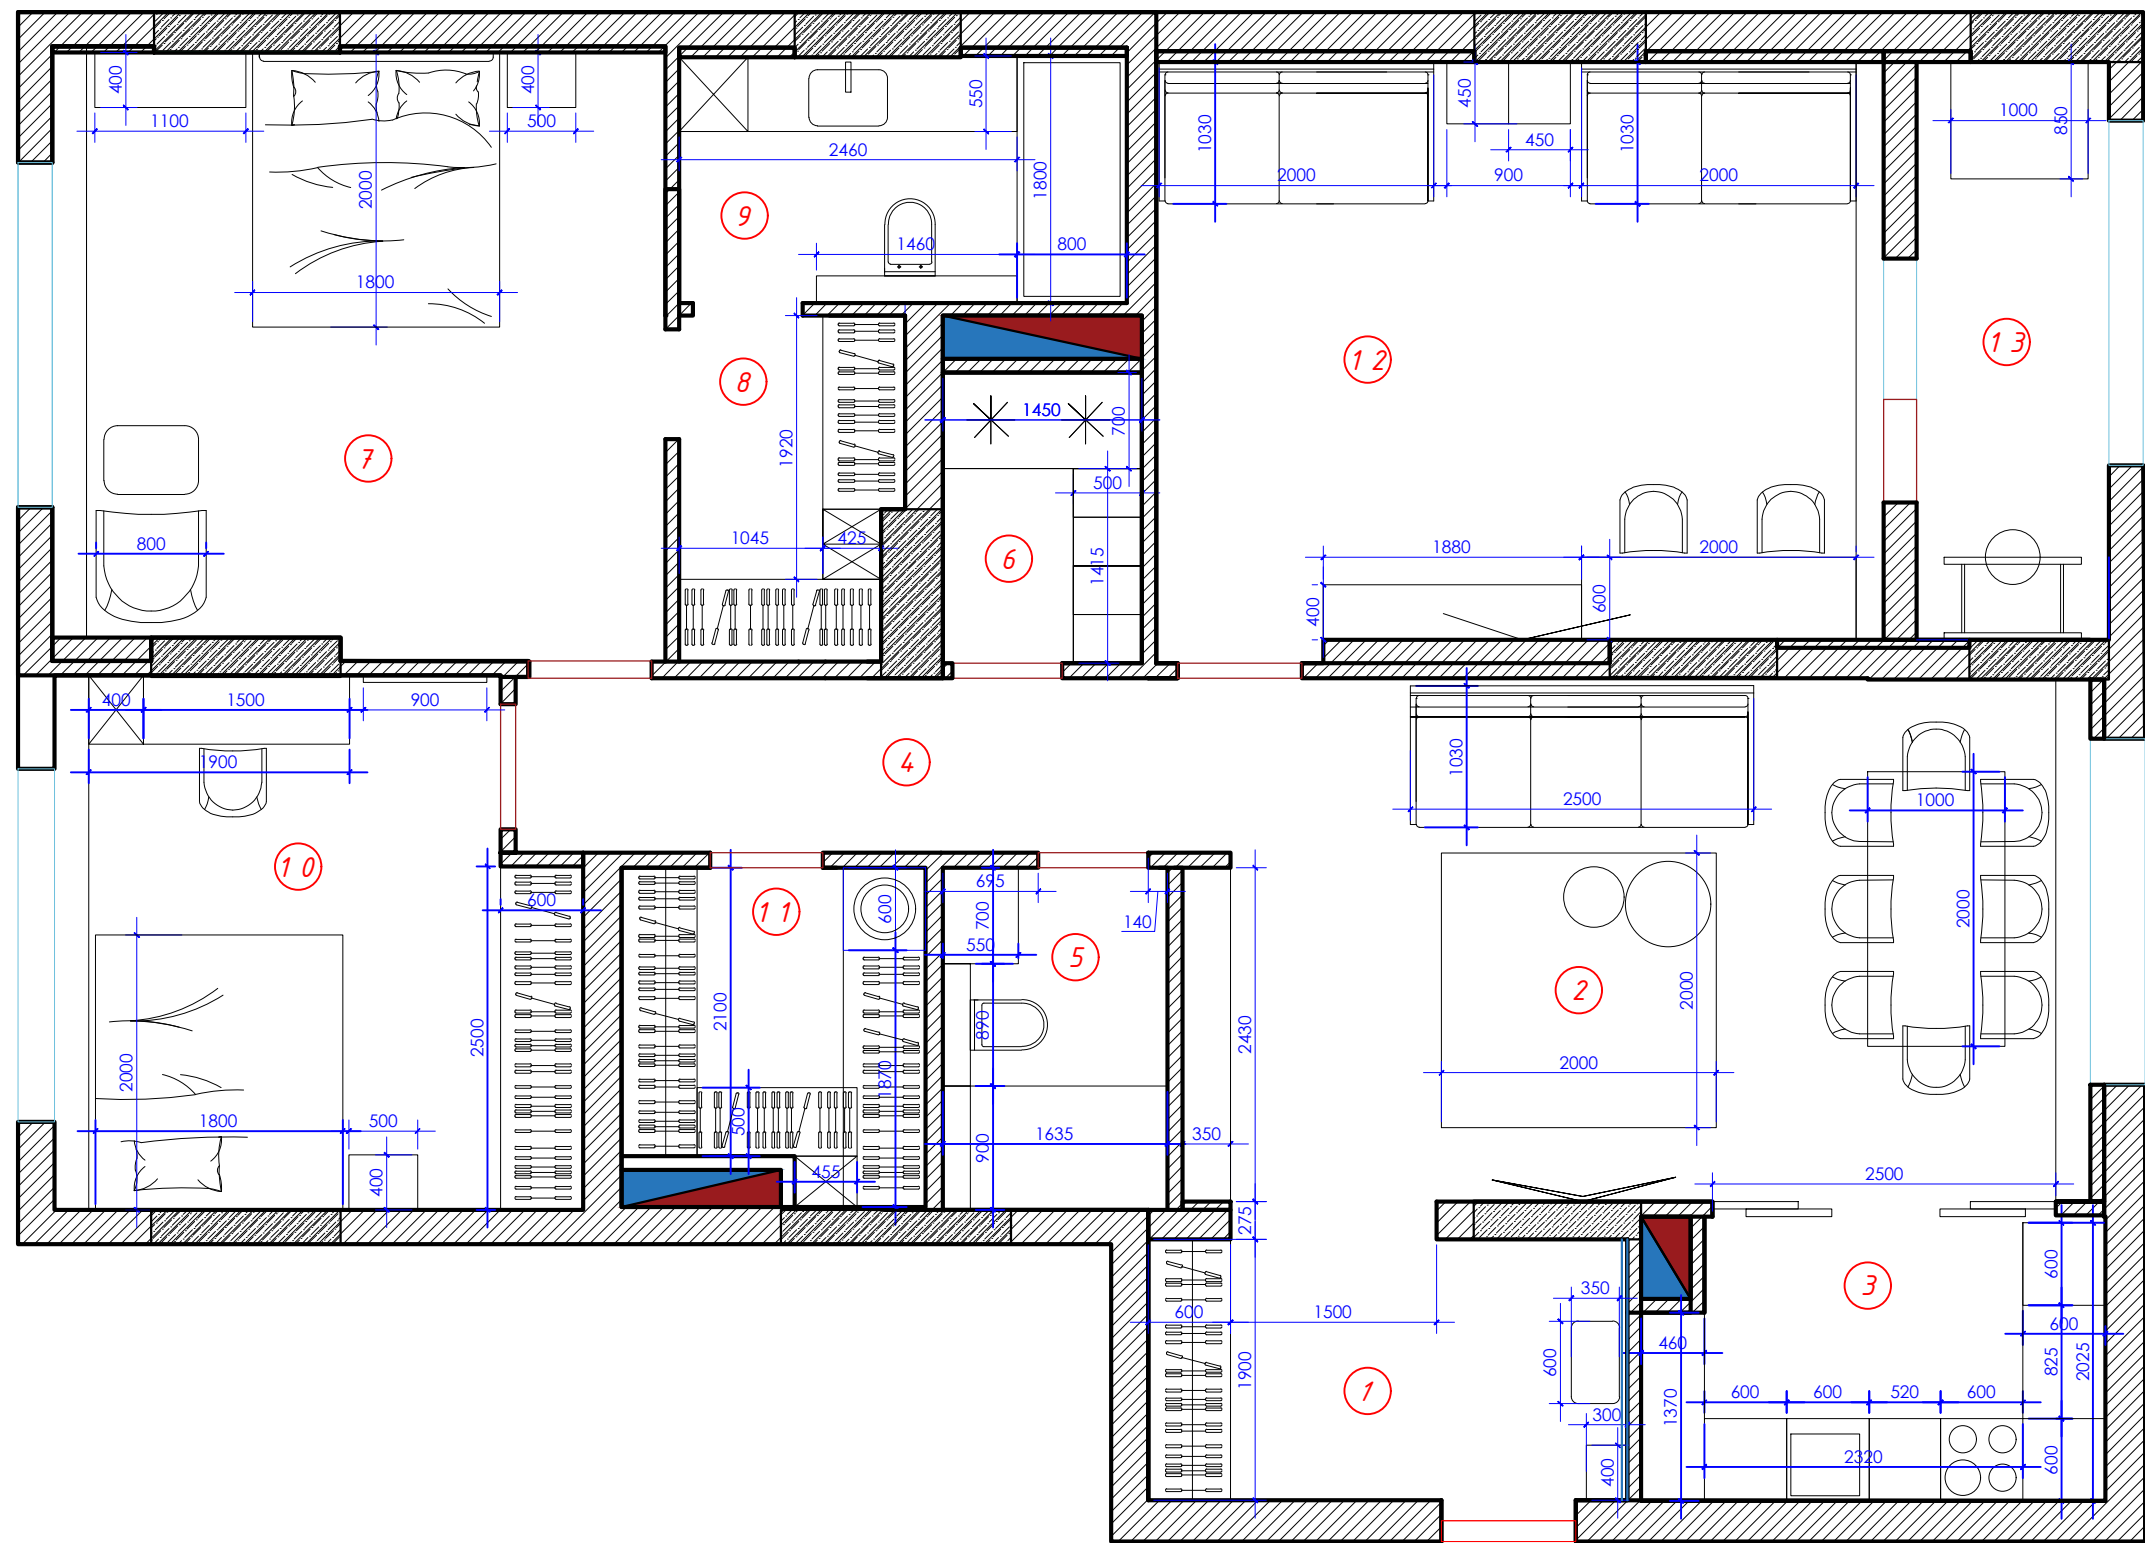

№	Экспликация помещений	м2
1	Прихожая	7,0
2	Зал	10,8
3	Кухня	14,0
4	Коридор	6,5
5	Гост.санузел	5,4
6	Кладовая	30,0
7	Мастер спальня	3,2
8	Мастер гардероб	3,4
9	Мастер санузел	5,1
10	Детская комната девочки	15,0
11	Гардероб мальчиков	4,2
12	Комната мальчиков	19,1
13	Спортивная зона мальчиков	6,2
Итого		130

Рабочий проект квартиры в ЖК Monaco Residence	Стадия	Лист	Листов
	РП		
План мебели с размерами		adilova_design творческая мастерская	

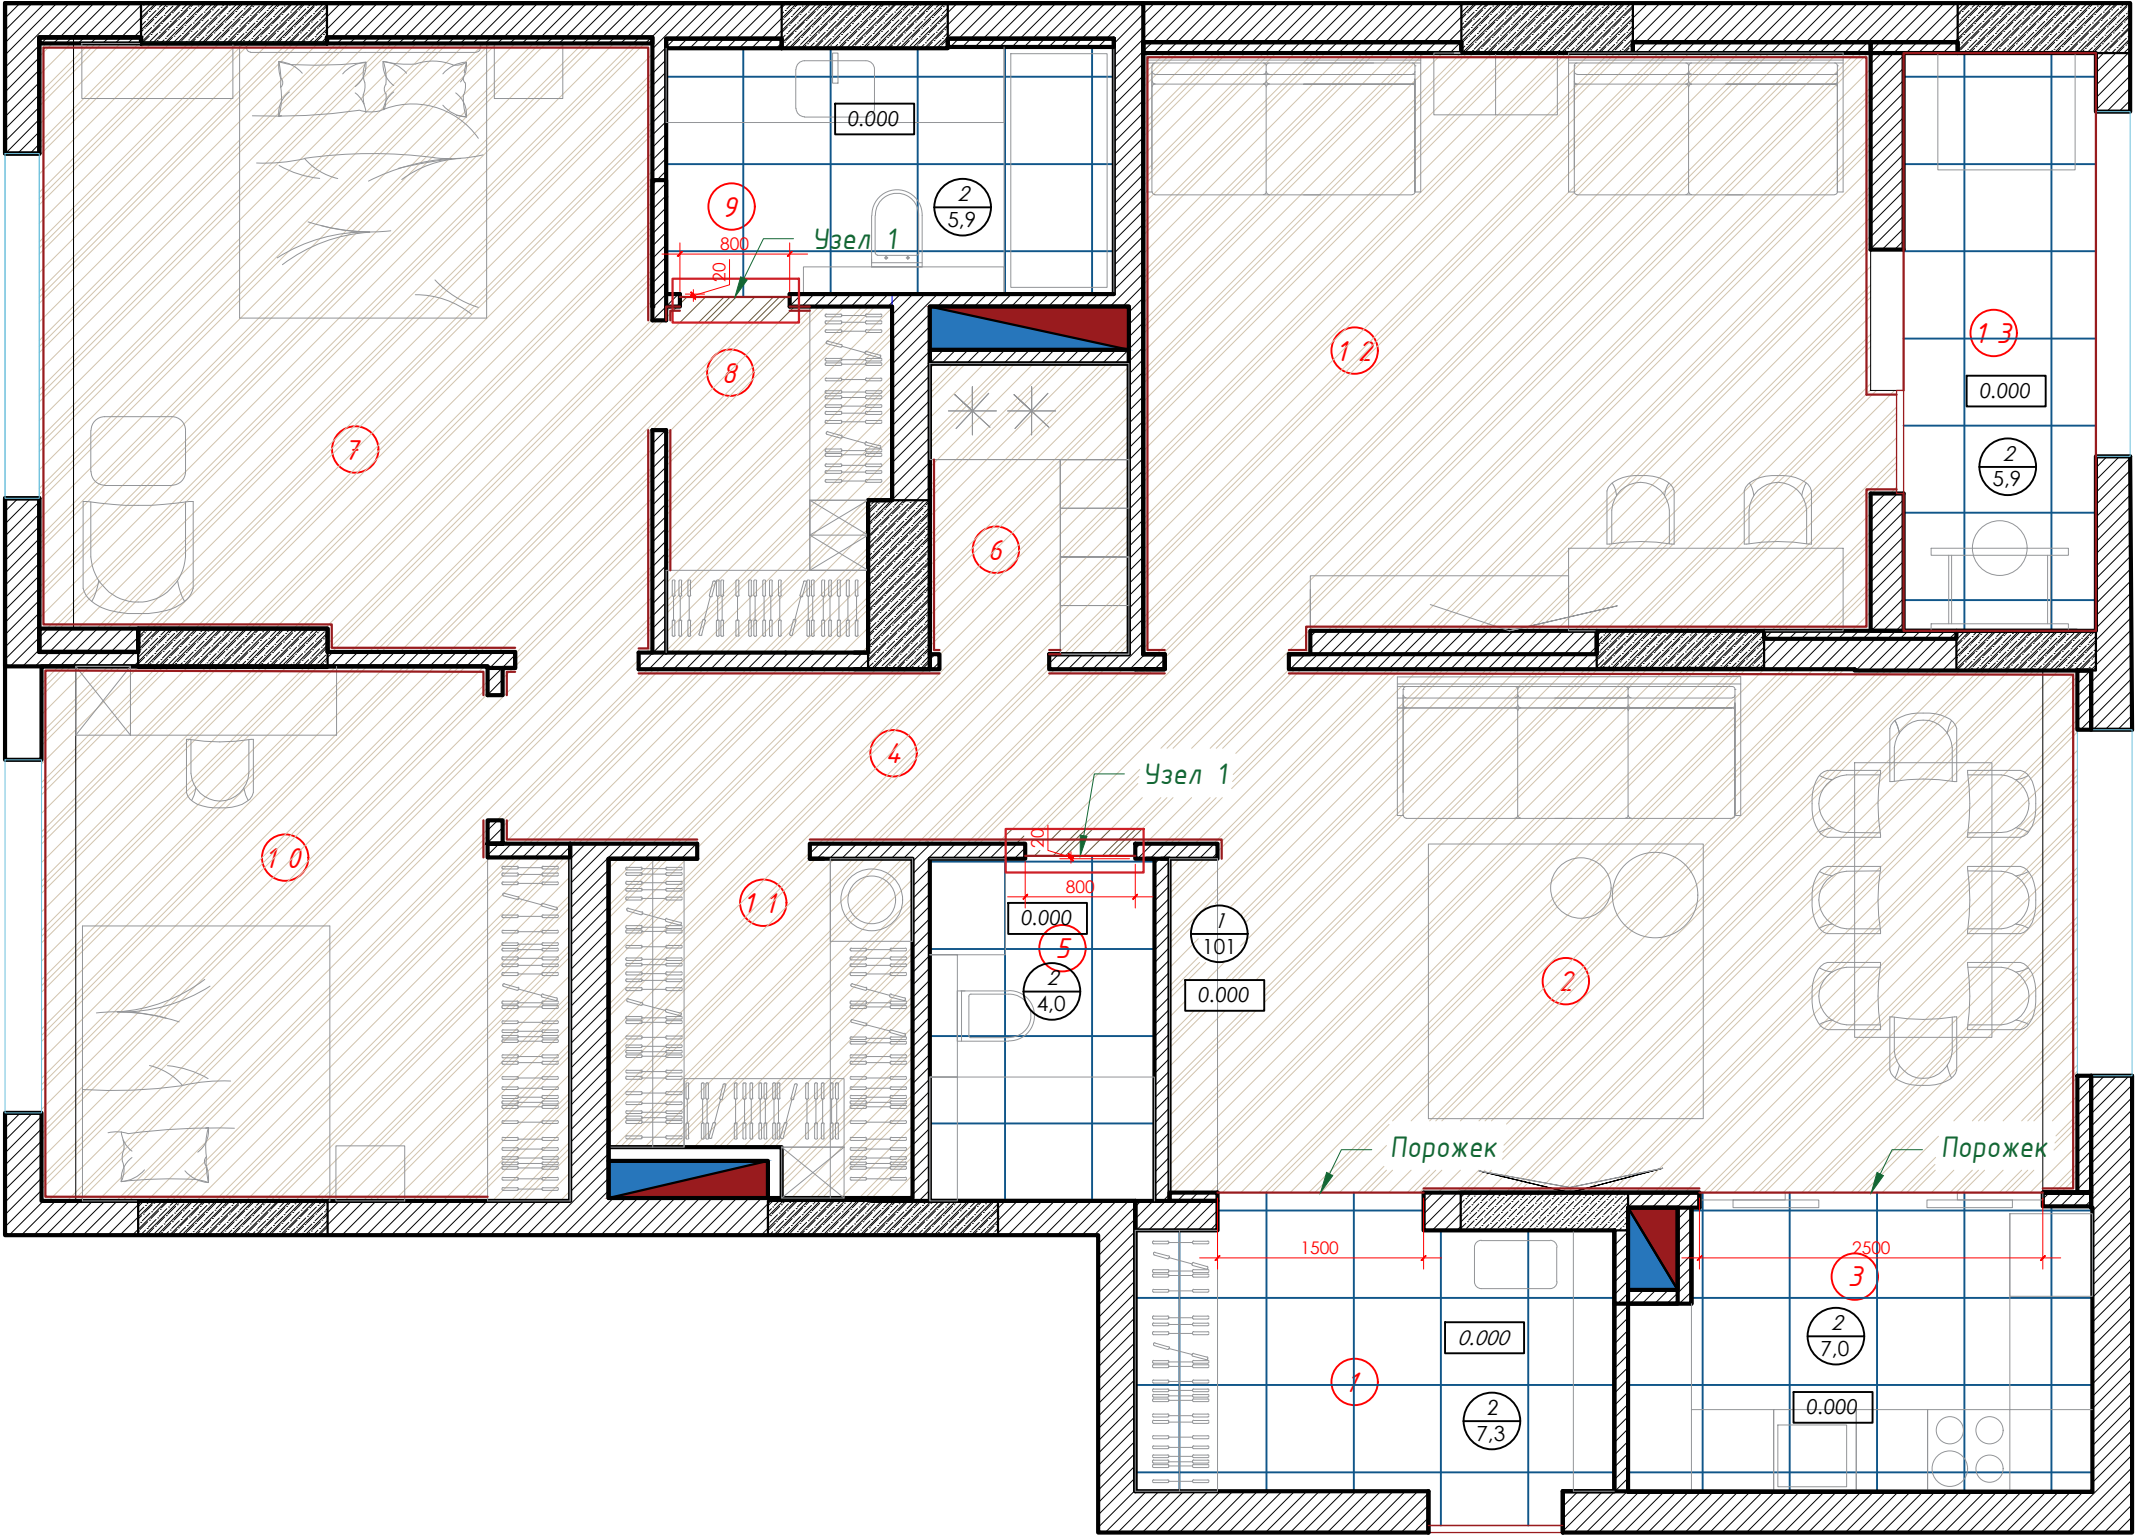

№	Экспликация помещений	м2
1	Прихожая	7.0
2	Зал	10,8
3	Кухня	14,0
4	Коридор	6.5
5	Гост.санузел	5,4
6	Кладовая	30,0
7	Мастер спальня	3,2
8	Мастер гардероб	3,4
9	Мастер санузел	5,1
10	Детская комната девочки	15,0
11	Гардероб мальчиков	4,2
12	Комната мальчиков	19,1
13	Спортивная зона мальчиков	6,2
Итого		130


Условные обозначения:

№	Наименование	Обозначение
1	SPC / Ламинат 100 м2	
2	Керамическая плитка	
3	Тип покрытия Площадь помещения	
4	Уровень пола	
5	Плинтус 69,8	


- Примечания:
- Расчет материала напольного покрытия произвести с учетом % надбавки на спил и скол.
 - Примыкание плинтуса к мебели произвести после установки мебели

Рабочий проект квартиры в ЖК Monaco Residence	Стадия	Лист	Листов
	РП		
План пола		adilova_design творческая мастерская	


Конструкция пола 1

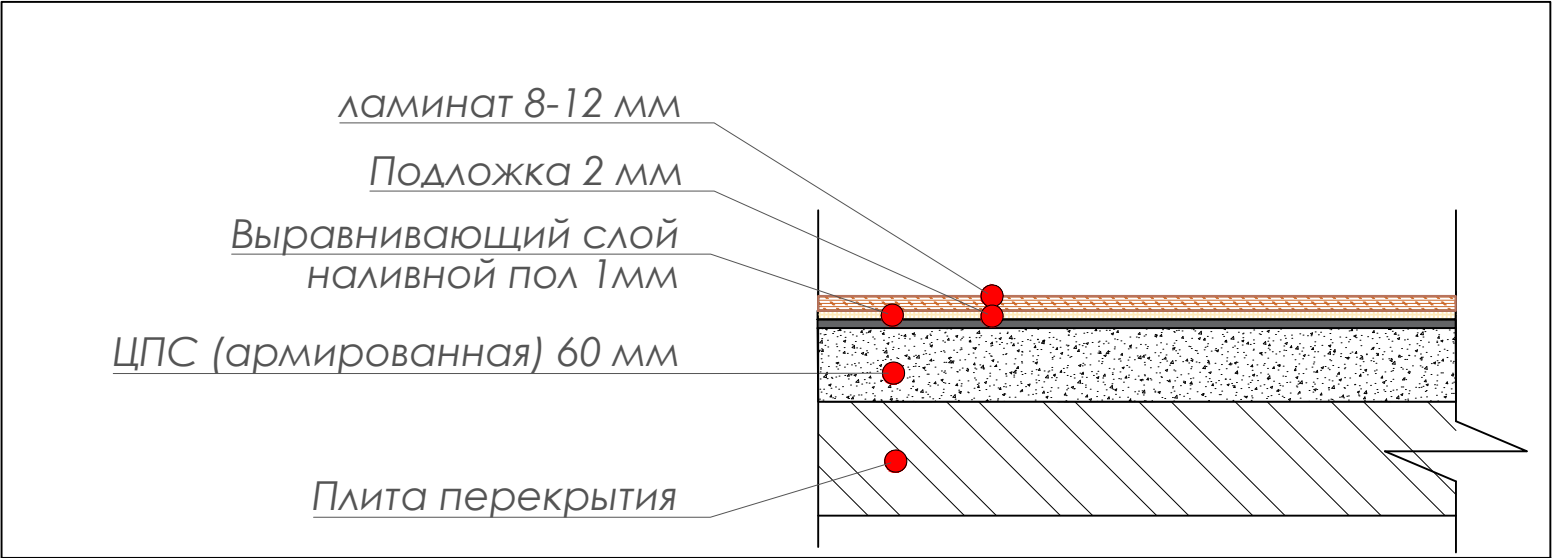

Конструкция пола 2

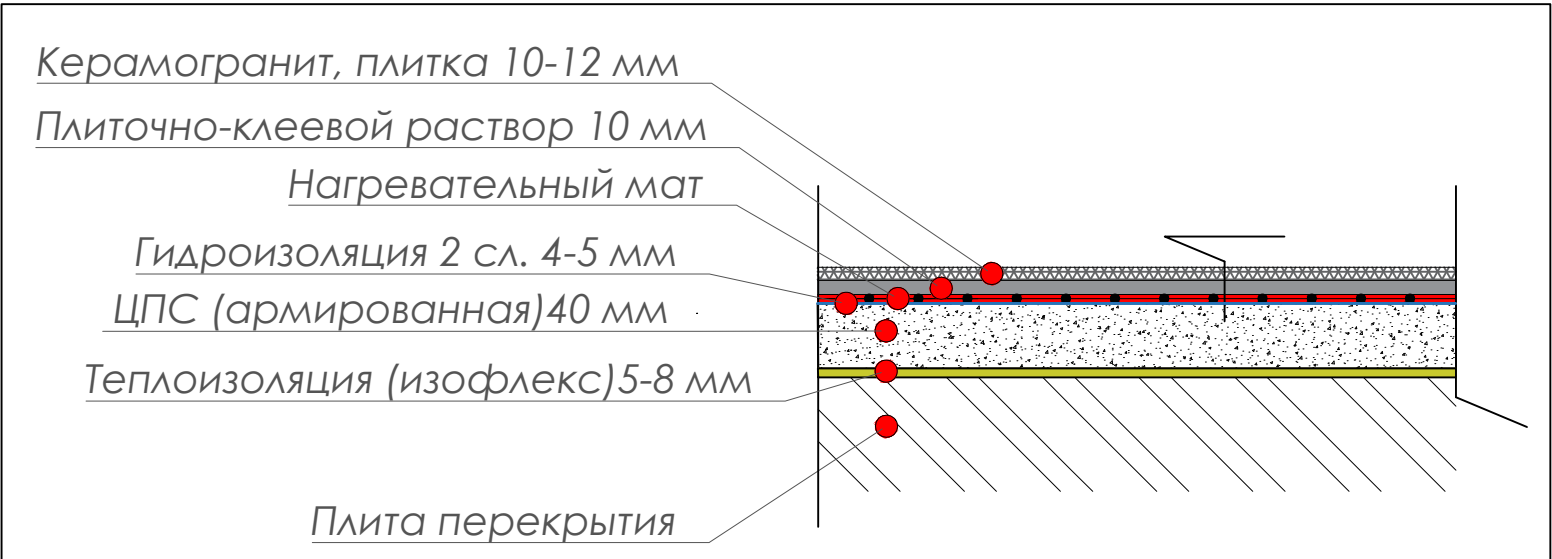


Узел 1

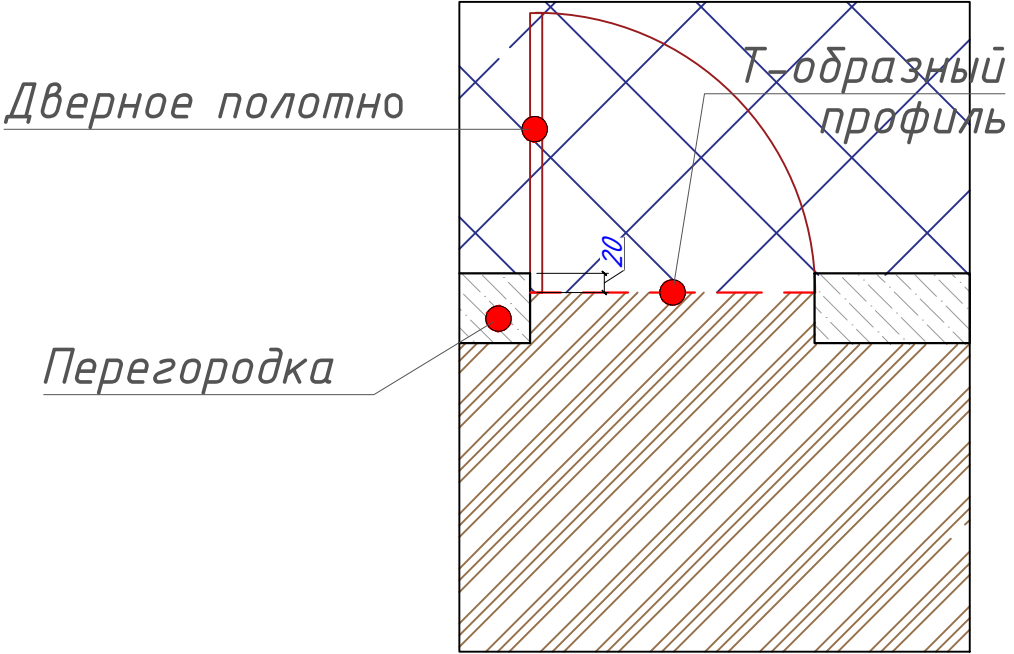

Рабочий проект квартиры в ЖК Monaco Residence	Стадия	Лист	Листов
	РП		
Узлы	adilova_design творческая мастерская		

№	Экспликация помещений	м2
1	Прихожая	7.0
2	Зал	10.8
3	Кухня	14.0
4	Коридор	6.5
5	Гост.санузел	5.4
6	Кладовая	30.0
7	Мастер спальня	3.2
8	Мастер гардероб	3.4
9	Мастер санузел	5.1
10	Детская комната девочки	15.0
11	Гардероб мальчиков	4.2
12	Комната мальчиков	19.1
13	Спортивная зона мальчиков	6.2
Итого		130

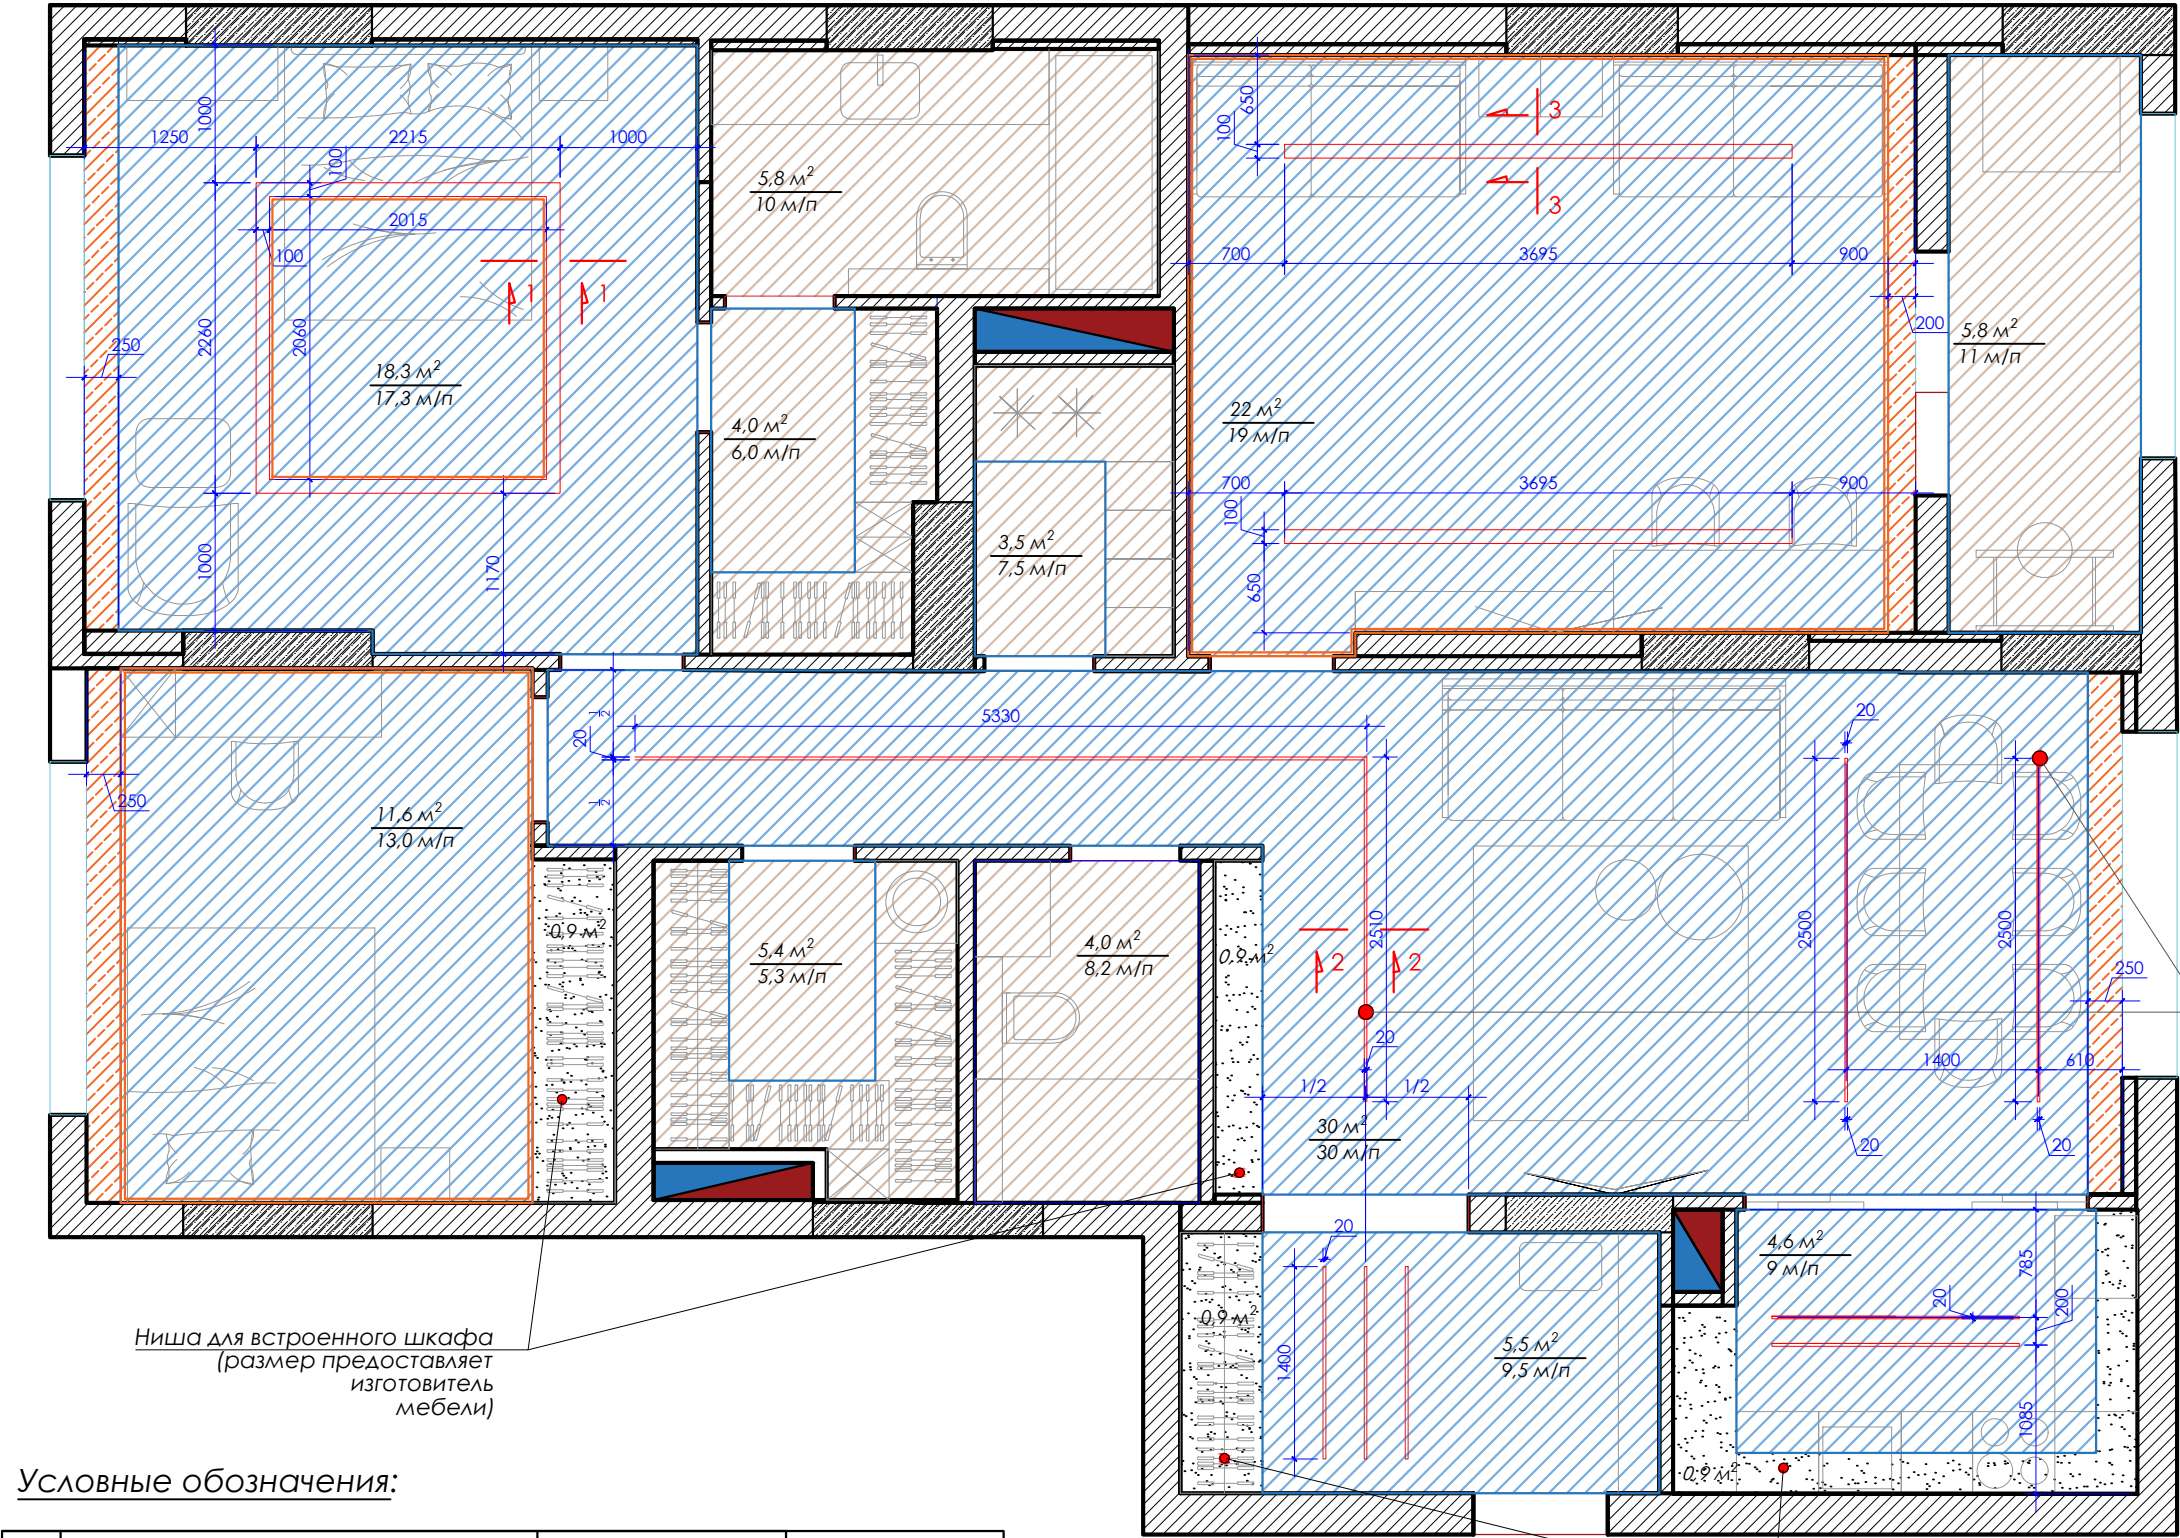

Монтаж потолка производится
только после закупа
магнитных треков

Ниша для встроенного шкафа
(размер предоставляет
изготовитель
мебели)

Ниша для встроенного шкафа
(размер предоставляет
изготовитель
мебели)


Условные обозначения:

№	Наименование	Обозначение	Примечания
1	ГКЛ на отм. -100 мм от потолка		91,2 м ²
2	Натяжной потолок на отм. -100 мм от потолка		27,8 м ²
3	Левкас по сущ. потолку		3,9 м ²
4	Потолок ГКЛ под встраиваемый шкаф		5,5 м ²
5	Карнизы потолочные		90,5 м/п

Рабочий проект квартиры в ЖК Monaco Residence	Стадия	Лист	Листов
	РП		
План потолочного покрытия		adilova_design творческая мастерская	


Разрез 1-1

монтаж потолка в спальне

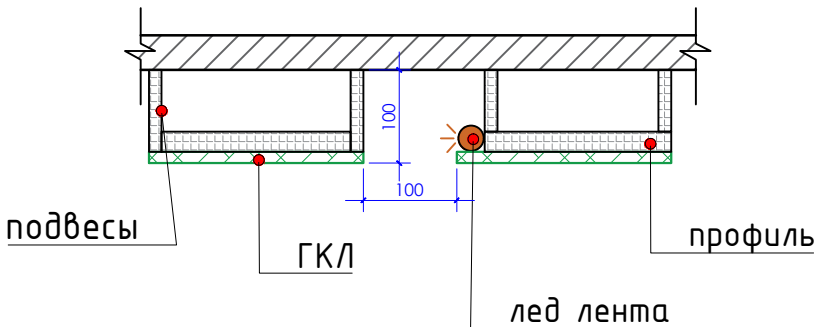


Разрез 3-3

монтаж потолка в детской мальчиков

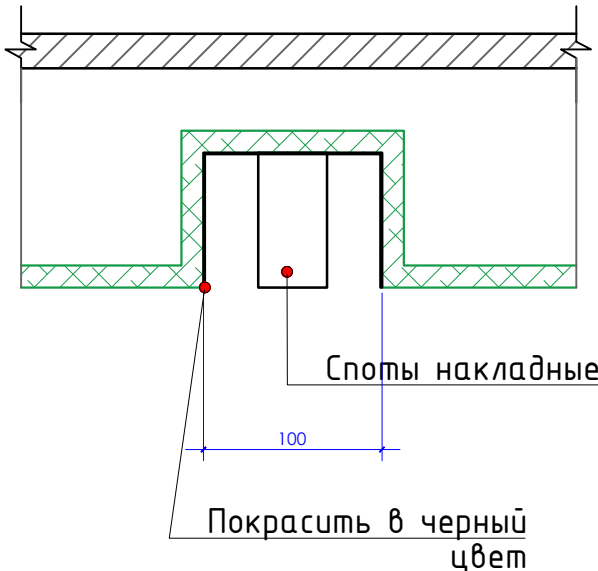


Разрез 2-2

монтаж магнитного трекового освещения

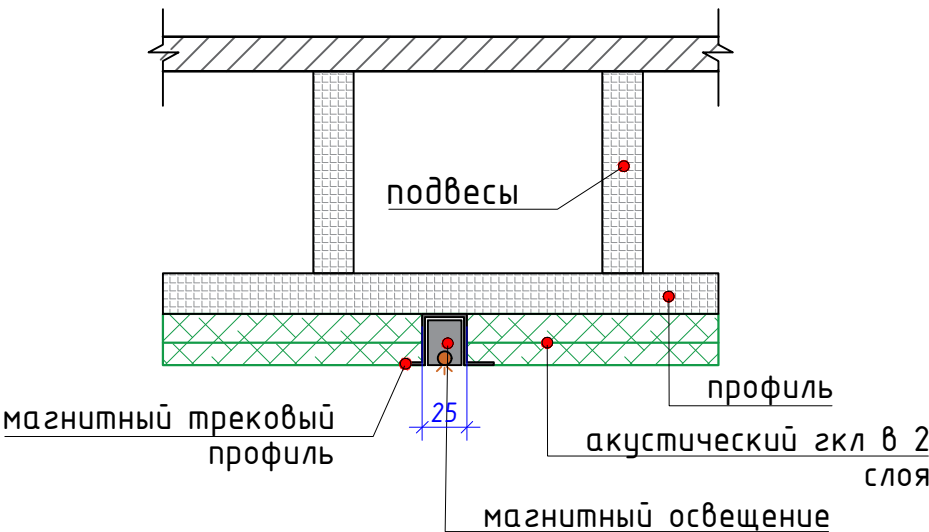

Рабочий проект квартиры в ЖК Monaco Residence	Стадия	Лист	Листов
	РП		
Сечения	adilova_design творческая мастерская		

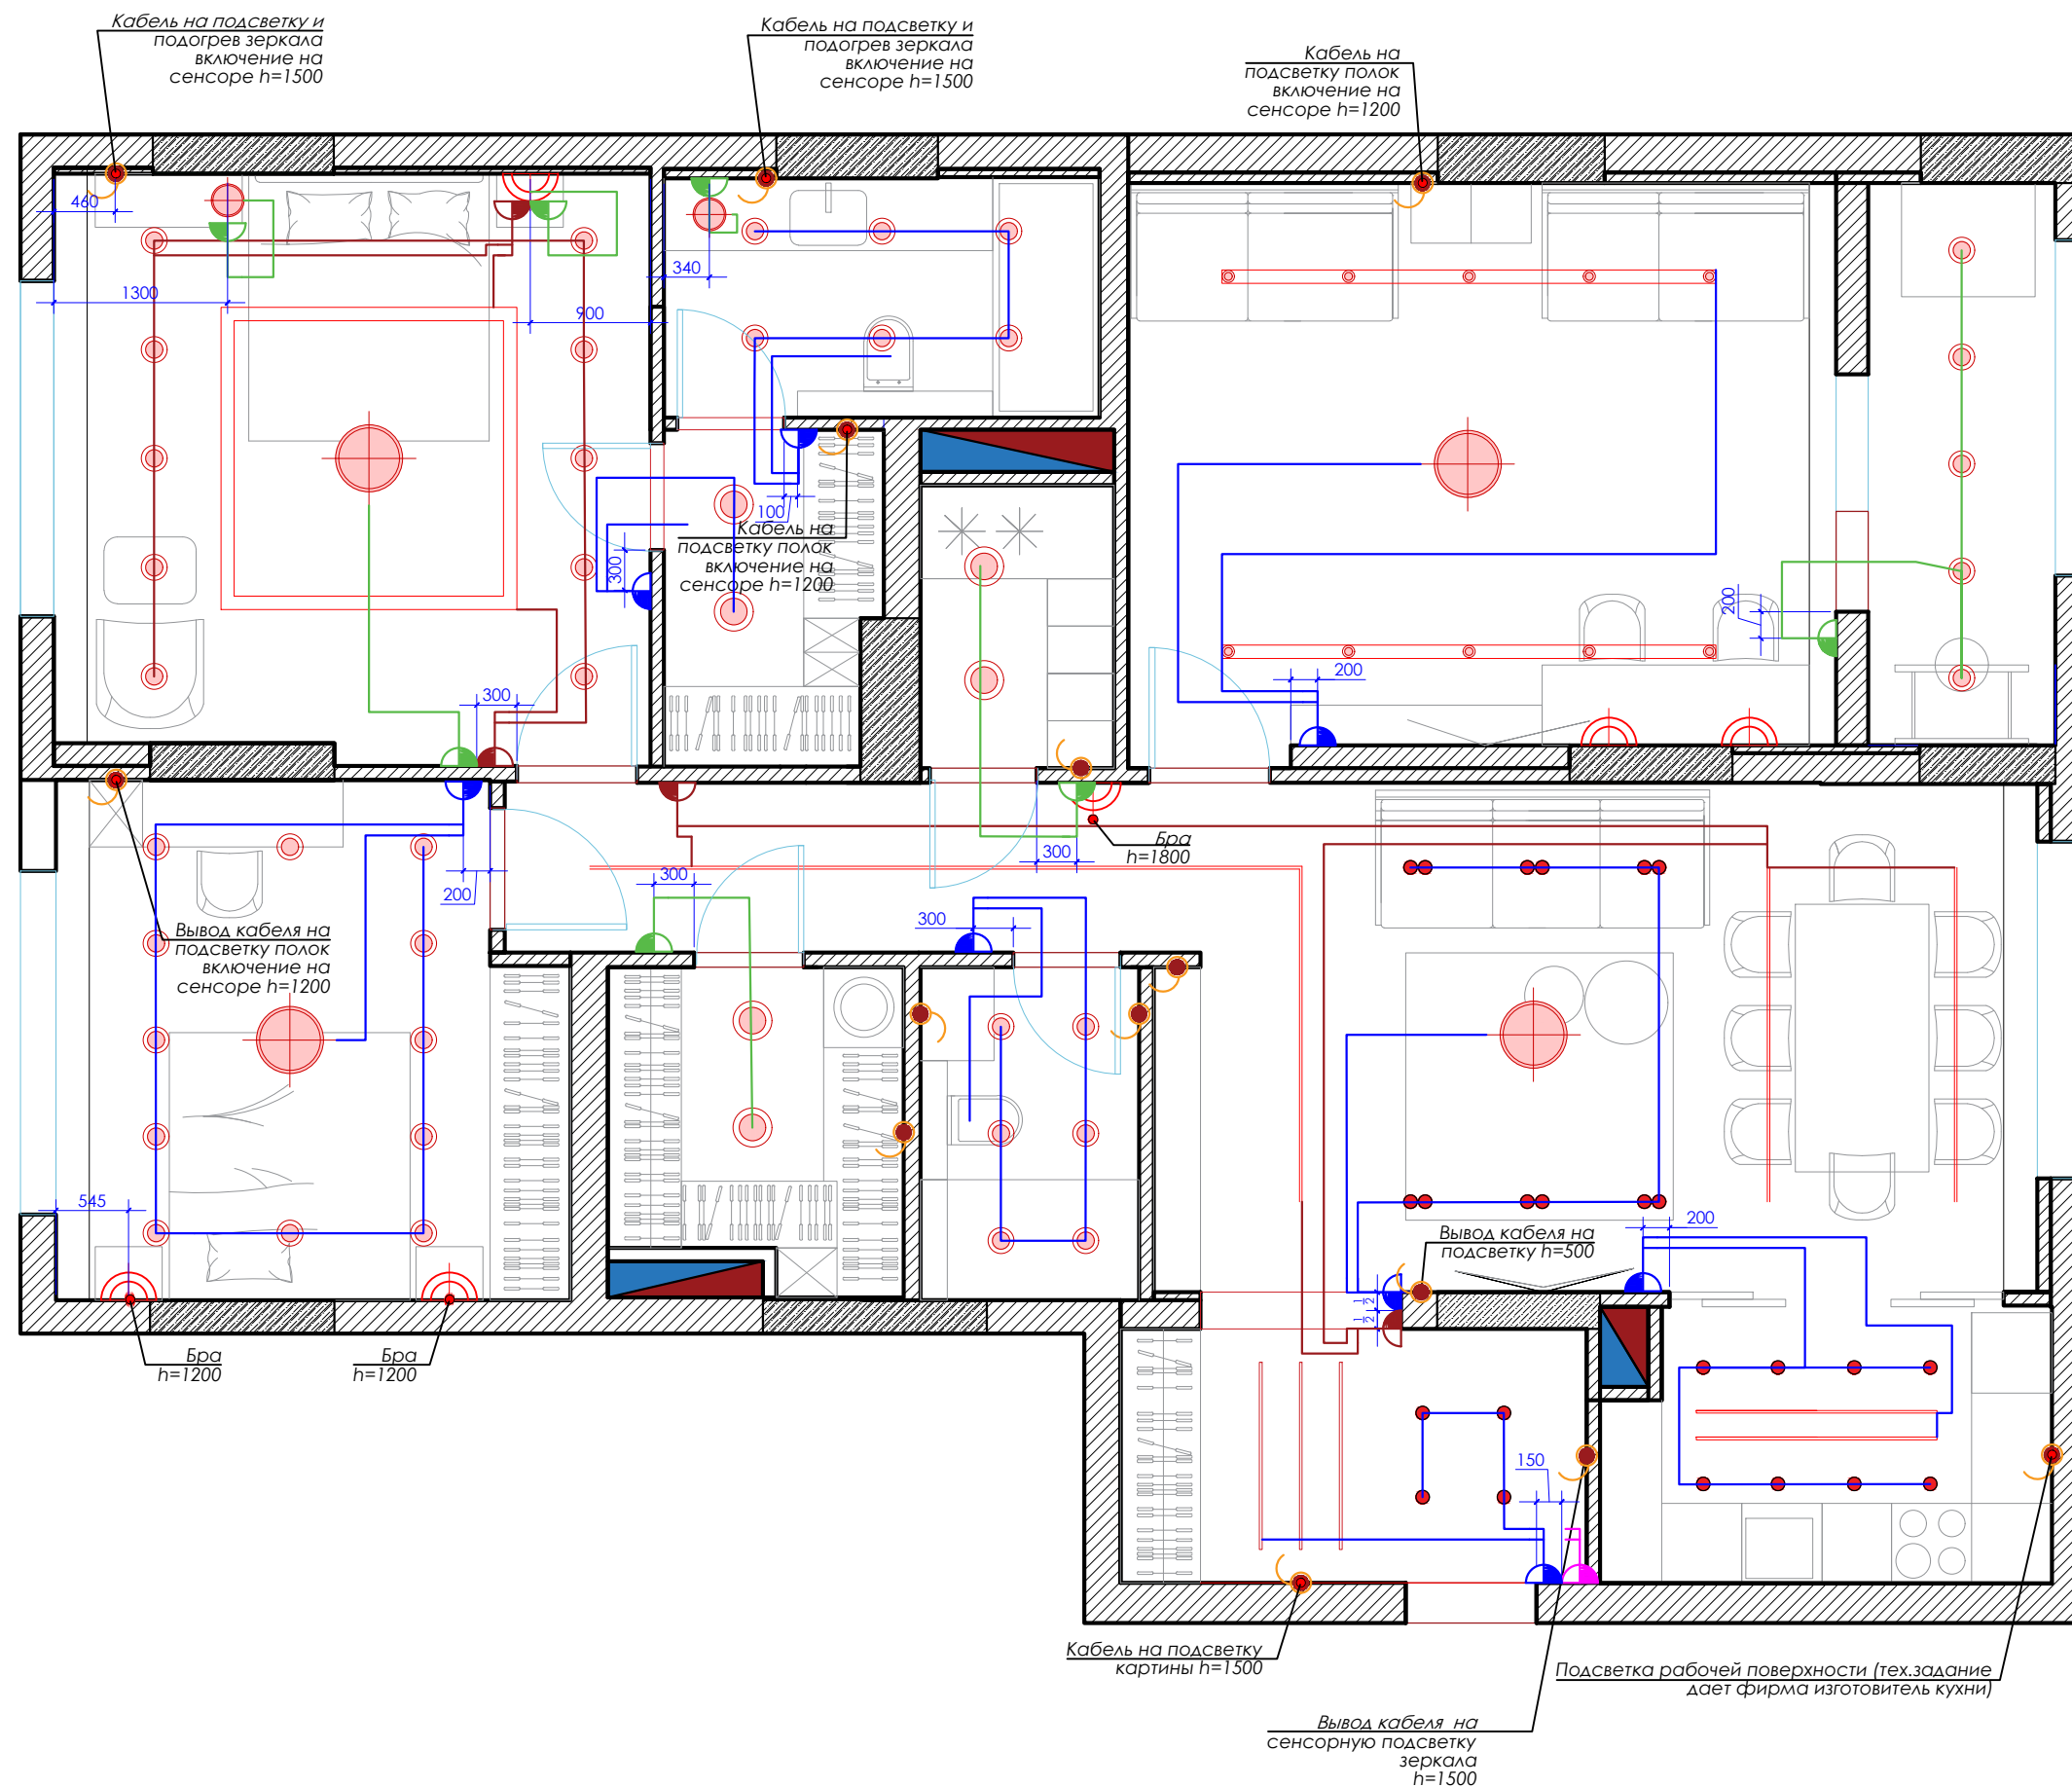


№	Экспликация помещений	м2
1	Прихожая	7.0
2	Зал	10.8
3	Кухня	14.0
4	Коридор	6.5
5	Гост.санузел	5.4
6	Кладовая	30.0
7	Мастер спальня	3.2
8	Мастер гардероб	3.4
9	Мастер санузел	5.1
10	Детская комната девочки	15.0
11	Гардероб мальчиков	4.2
12	Комната мальчиков	19.1
13	Спортивная зона мальчиков	6.2
Итого		130

Спецификация оборудования		
Обозначение на плане	Наименование	Кол-во
	Выкл.одноклавишный	7
	Выкл.двухклавишный	8
	Мастер вкл.	1
	Переходной двухклавишный вкл.	4

Примечания:
1. Все выключатели, кроме отдельно указанных устанавливаются на высоте +0.900мм от чистовой отделки пола
2. Питание теплого пола вывести на отдельный автомат.

Рабочий проект квартиры в ЖК Monaco Residence	Стадия	Лист	Листов
	РП		
План выключателей		adilova_design творческая мастерская	

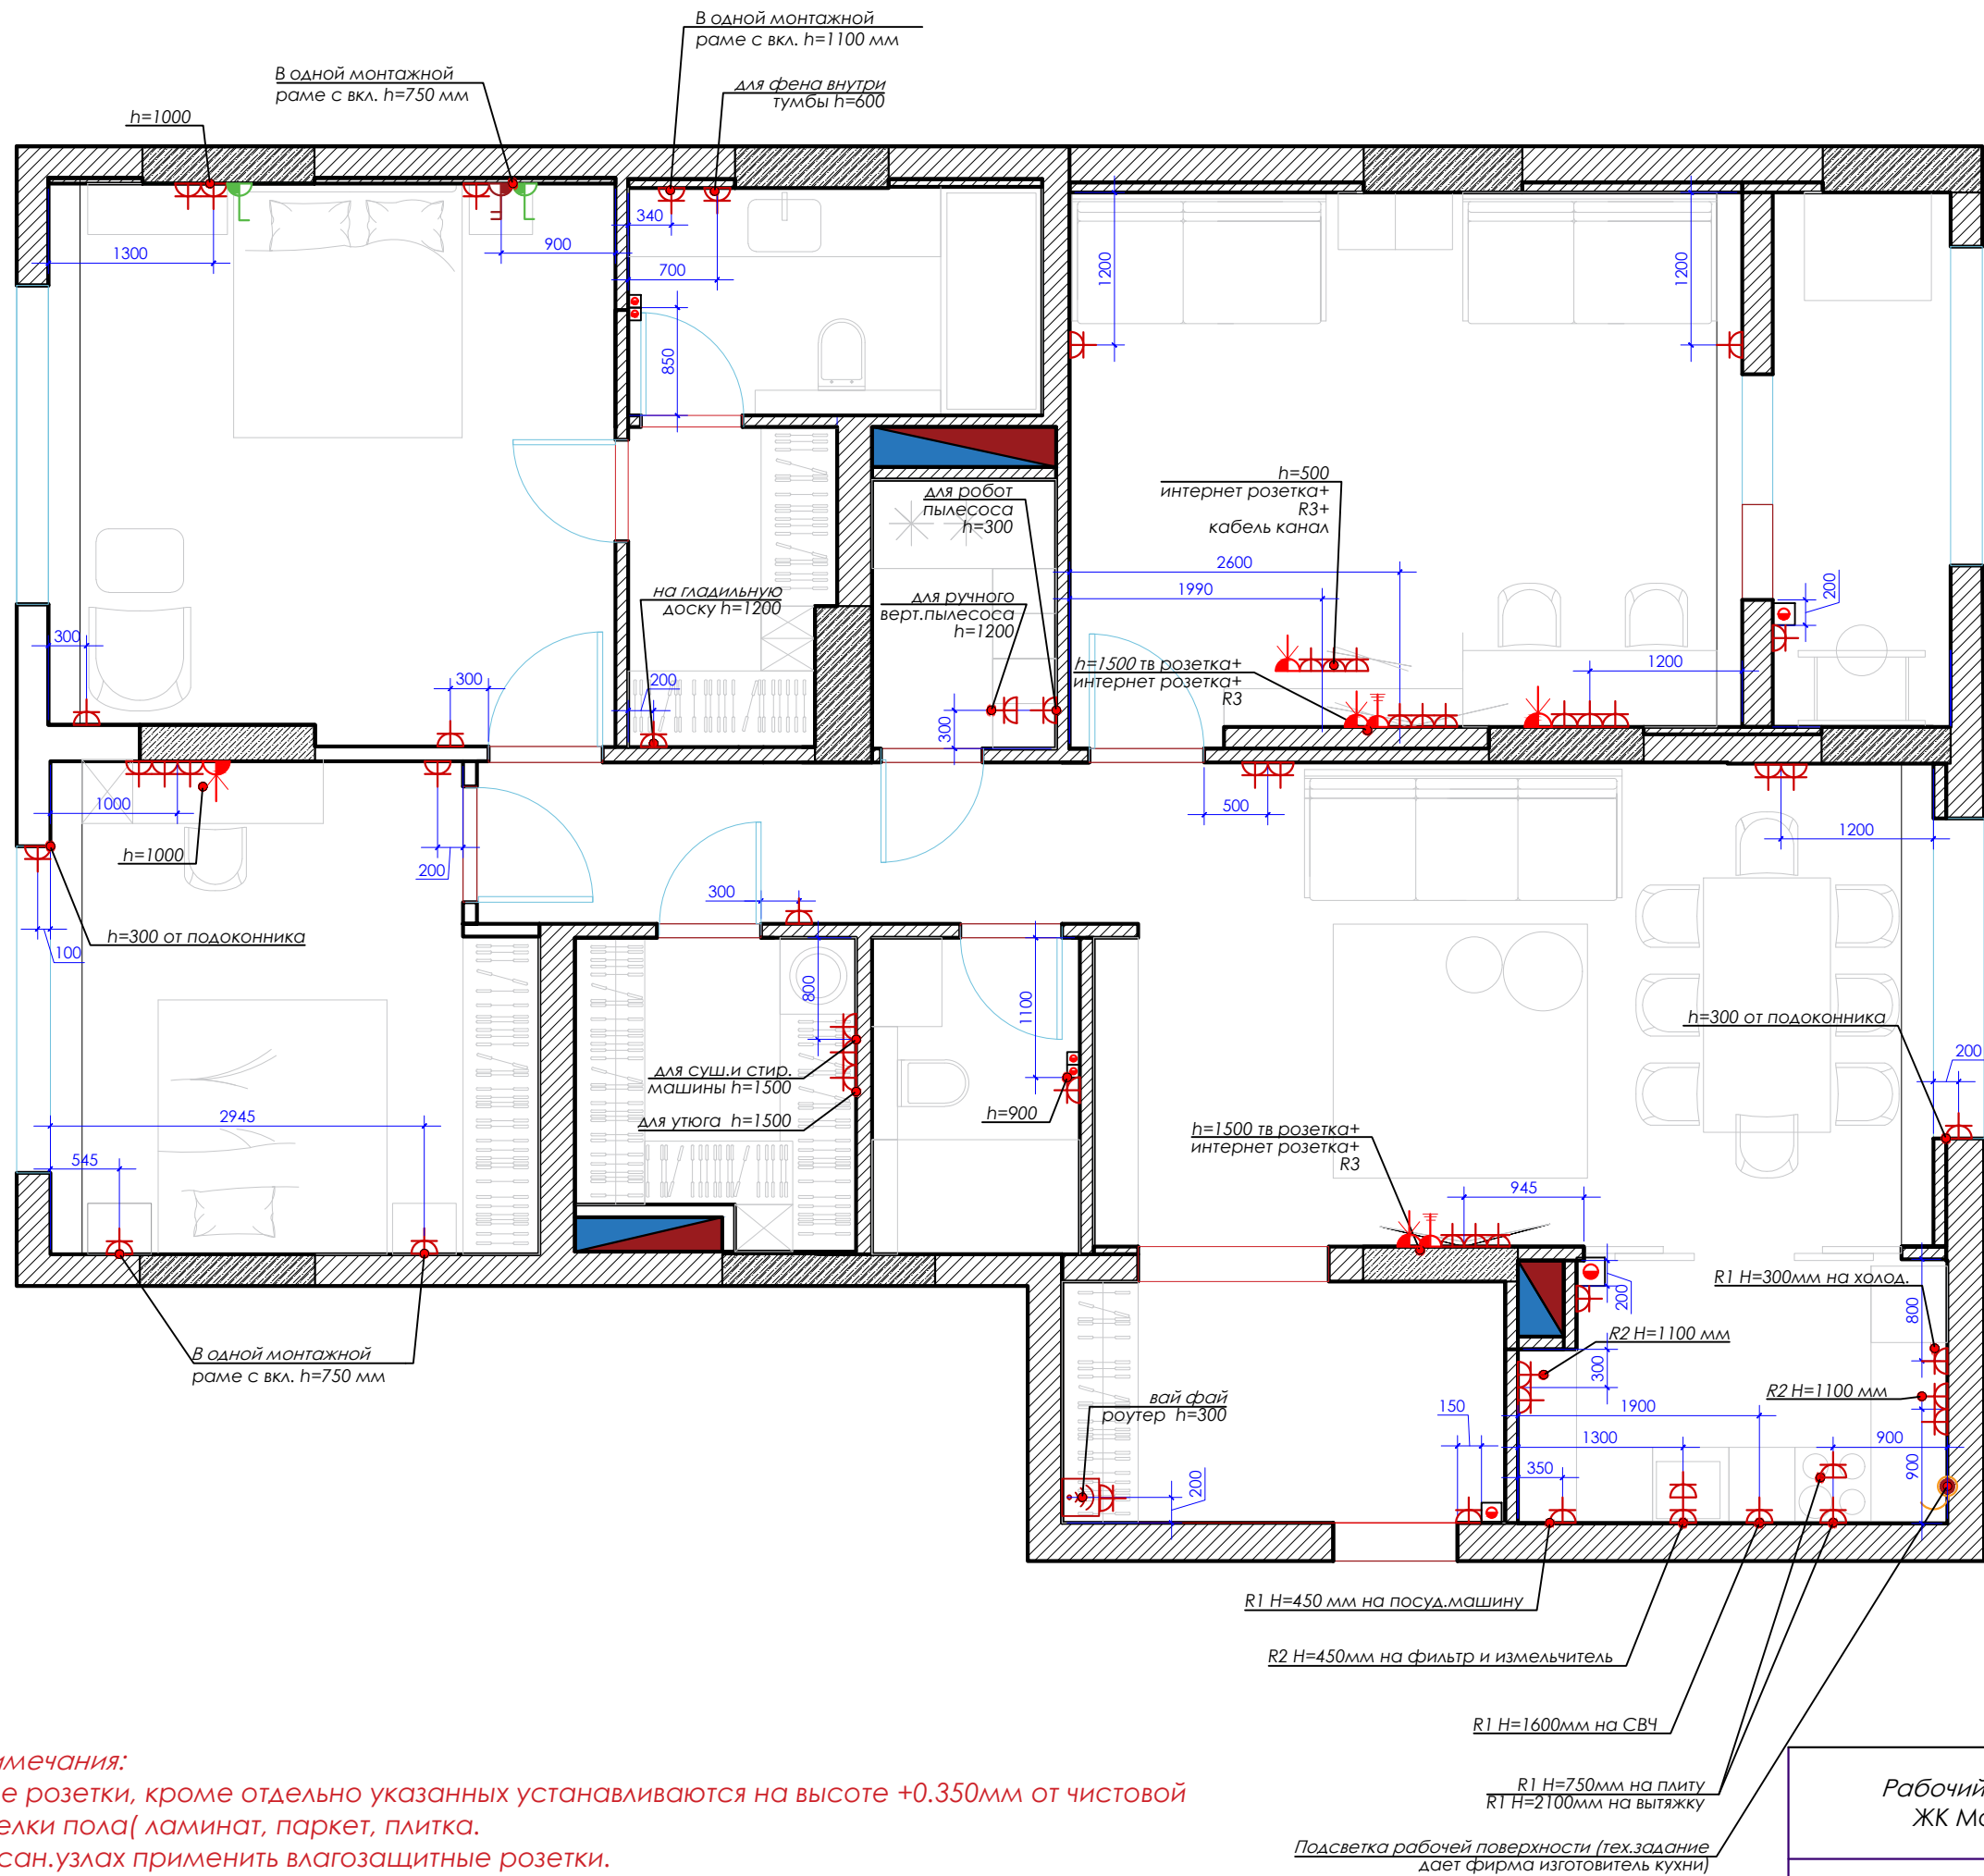


Примечания:
1. Все розетки, кроме отдельно указанных устанавливаются на высоте +0.350мм от чистовой отделки пола(ламинат, паркет, плитка.
2. В сан.узлах применить влагозащитные розетки.
3. Расположение розеток на кух. оборудование уточнить у подрядной организации.

№	Экспликация помещений	м2
1	Прихожая	7.0
2	Зал	10,8
3	Кухня	14,0
4	Коридор	6.5
5	Гост.санузел	5,4
6	Кладовая	30,0
7	Мастер спальня	3,2
8	Мастер гардероб	3,4
9	Мастер санузел	5,1
10	Детская комната девочки	15,0
11	Гардероб мальчиков	4,2
12	Комната мальчиков	19,1
13	Спортивная зона мальчиков	6.2
Итого		130

Спецификация оборудования

Обозн-ние на плане	Наименование	Кол-во шт
	Розетка R1	25
	Розетка R2	6
	Интернер - розетка	5
	WIFI роутер	1
	Розетка телевизионная	1
	Домофон	1
	Розетка R3	6

Рабочий проект квартиры в ЖК Monaco Residence	Стадия	Лист	Листов
	РП		
План розеток		adilova_design творческая мастерская	

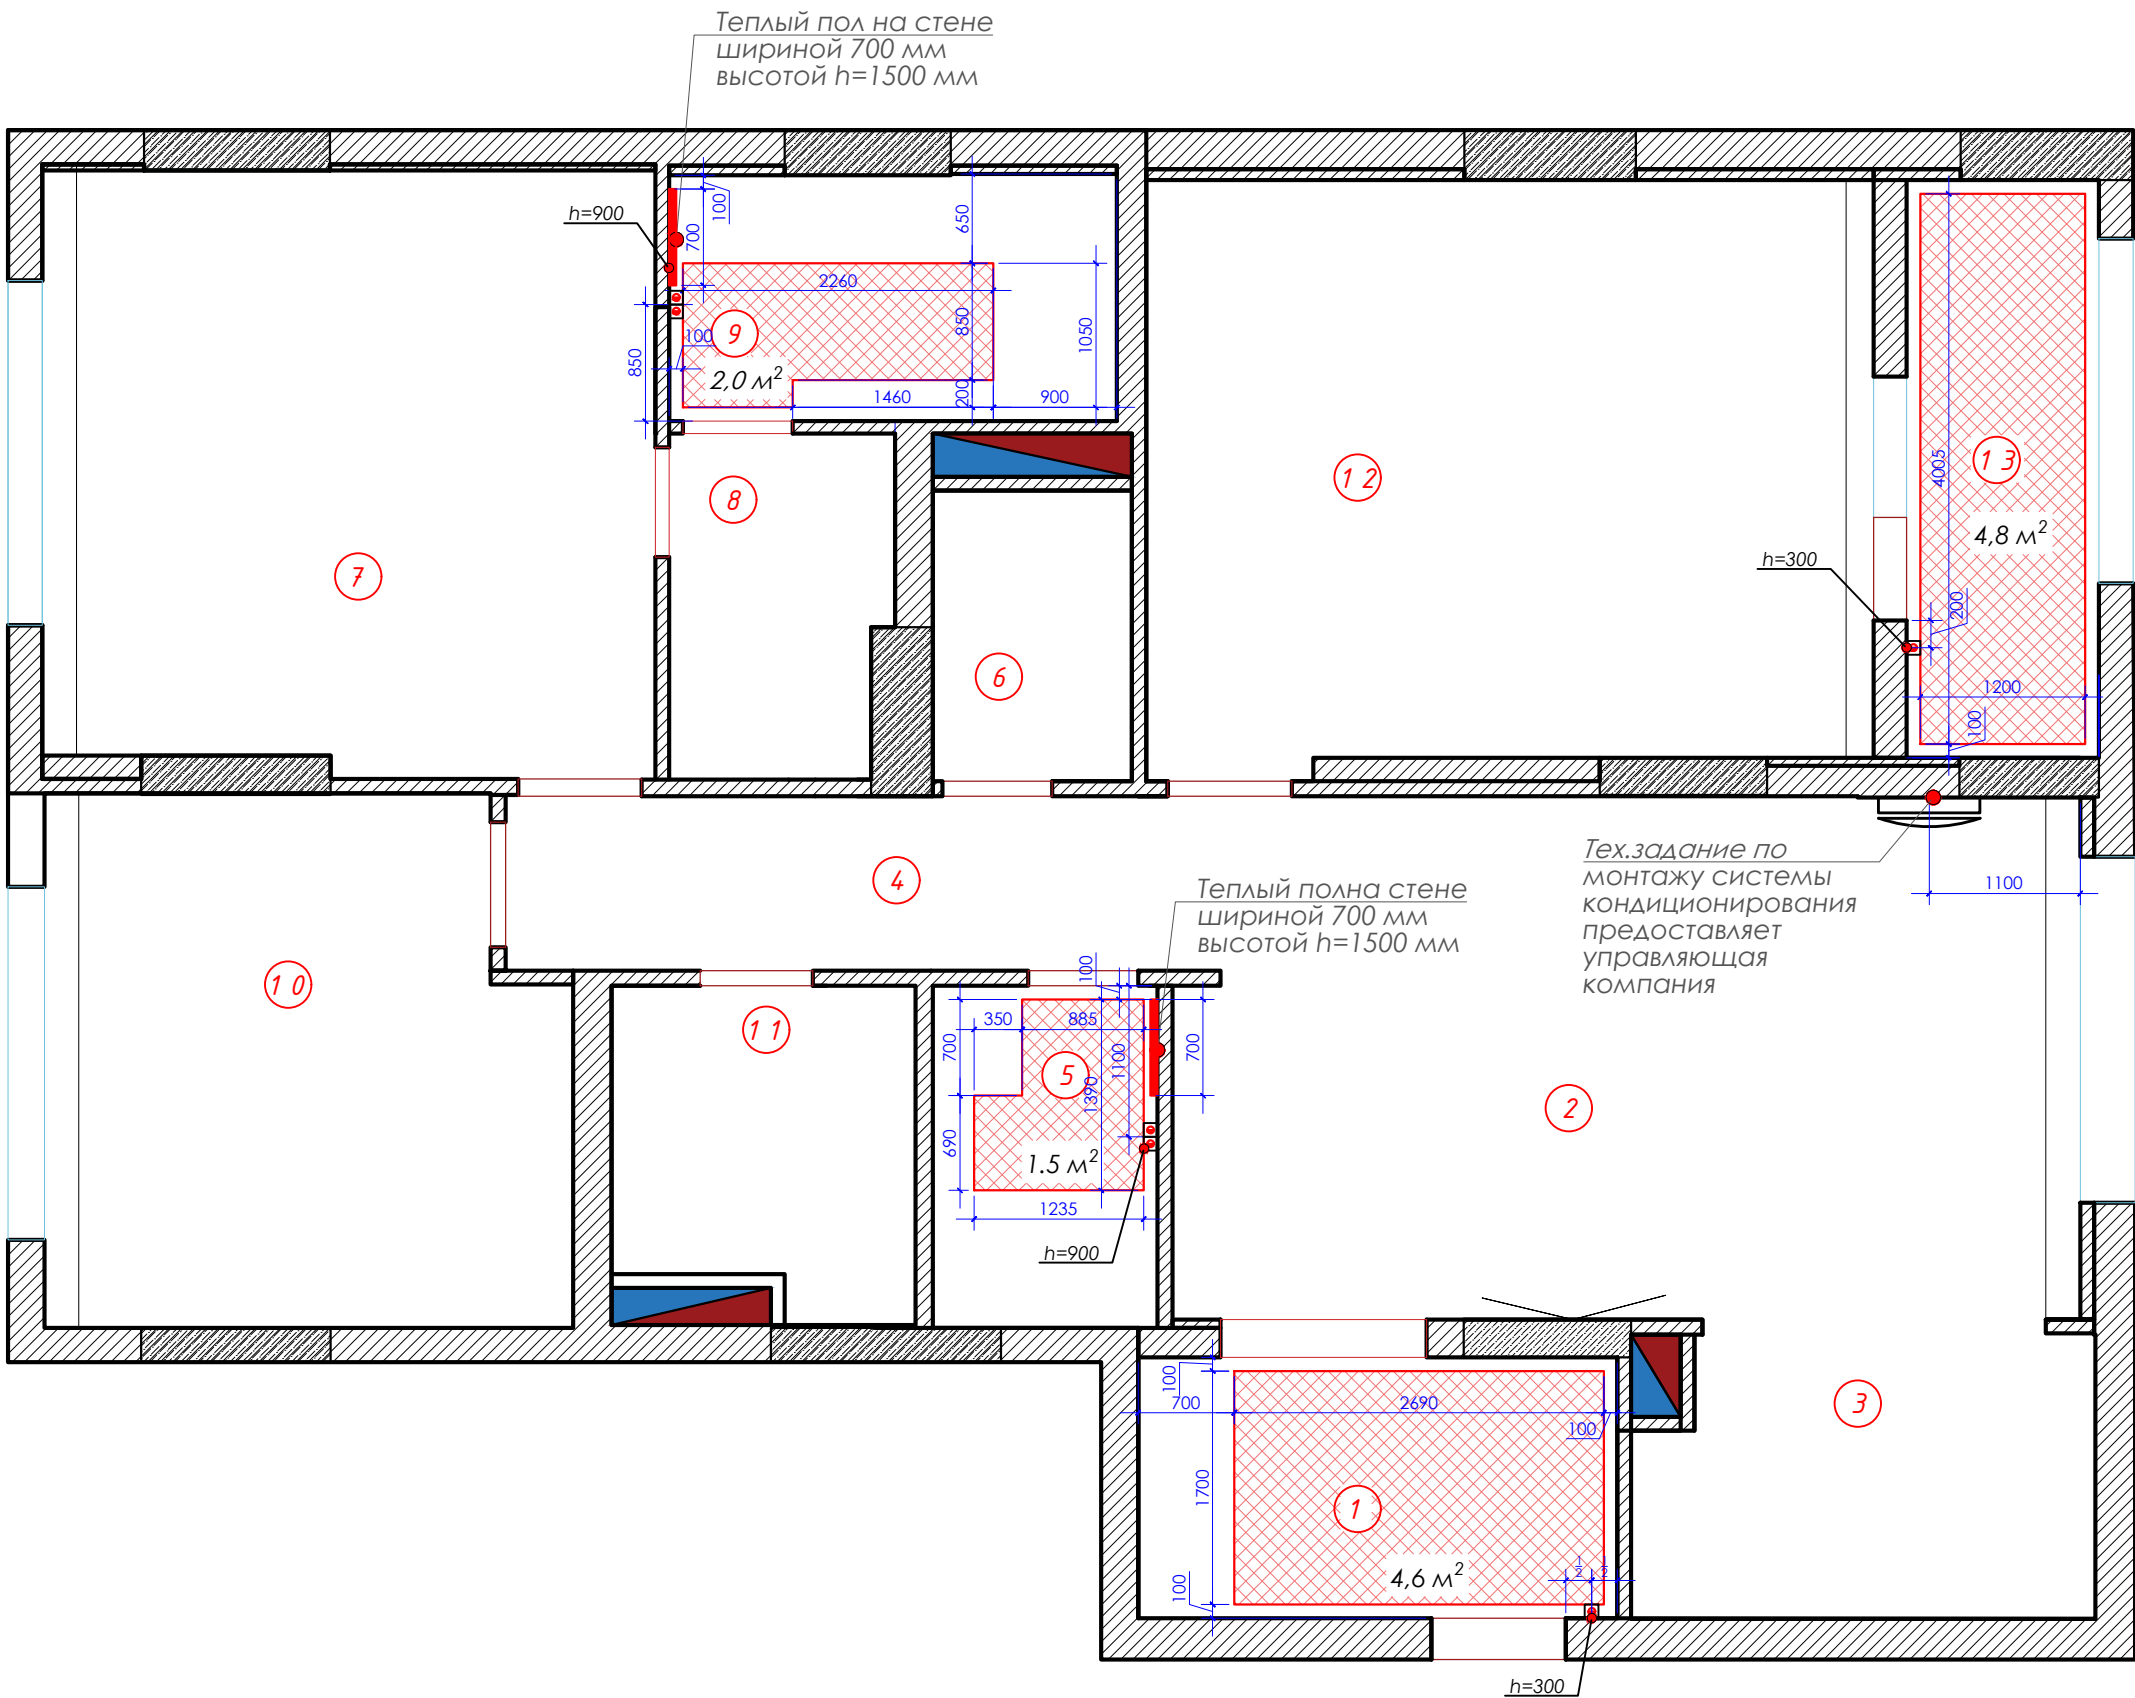


№	Экспликация помещений	м2
1	Прихожая	7.0
2	Зал	10.8
3	Кухня	14.0
4	Коридор	6.5
5	Гост.санузел	5.4
6	Кладовая	30.0
7	Мастер спальня	3.2
8	Мастер гардероб	3.4
9	Мастер санузел	5.1
10	Детская комната девочки	15.0
11	Гардероб мальчиков	4.2
12	Комната мальчиков	19.1
13	Спортивная зона мальчиков	6.2
Итого		130

- Примечания:
- Расчет мощности кондиционеров и радиаторов отопления вести с учетом площади помещения.
 - Питание на каждую единицу кондиционера вывести на отдельный автомат.
 - Регулятор теплого пола разместить на высоте с выключателем, на указанной высоте под выключателем.
 - Регулятор теплого пола монтируется в отдельной монтажной рамке с выключателем данного помещения.
 - См совместно с листом 15 (план размещения выключателей).
 - Питание на систему теплый вывести на отдельный автомат.
 - Тех.задание по монтажу системы кондиционирования предоставляет управляющая компания

Условные обозначения:

№	Наименование	Обозначение	Примечания
1	Теплые полы		12,6 м ²
2	Кондиционер		1 шт
3	Регулятор теплого пола		6 шт
4	Теплые стены		2 м2

Рабочий проект квартиры в ЖК Monaco Residence	Стадия	Лист	Листов
	РП		
План теплых пфолов и кондиционера	adilova_design творческая мастерская		

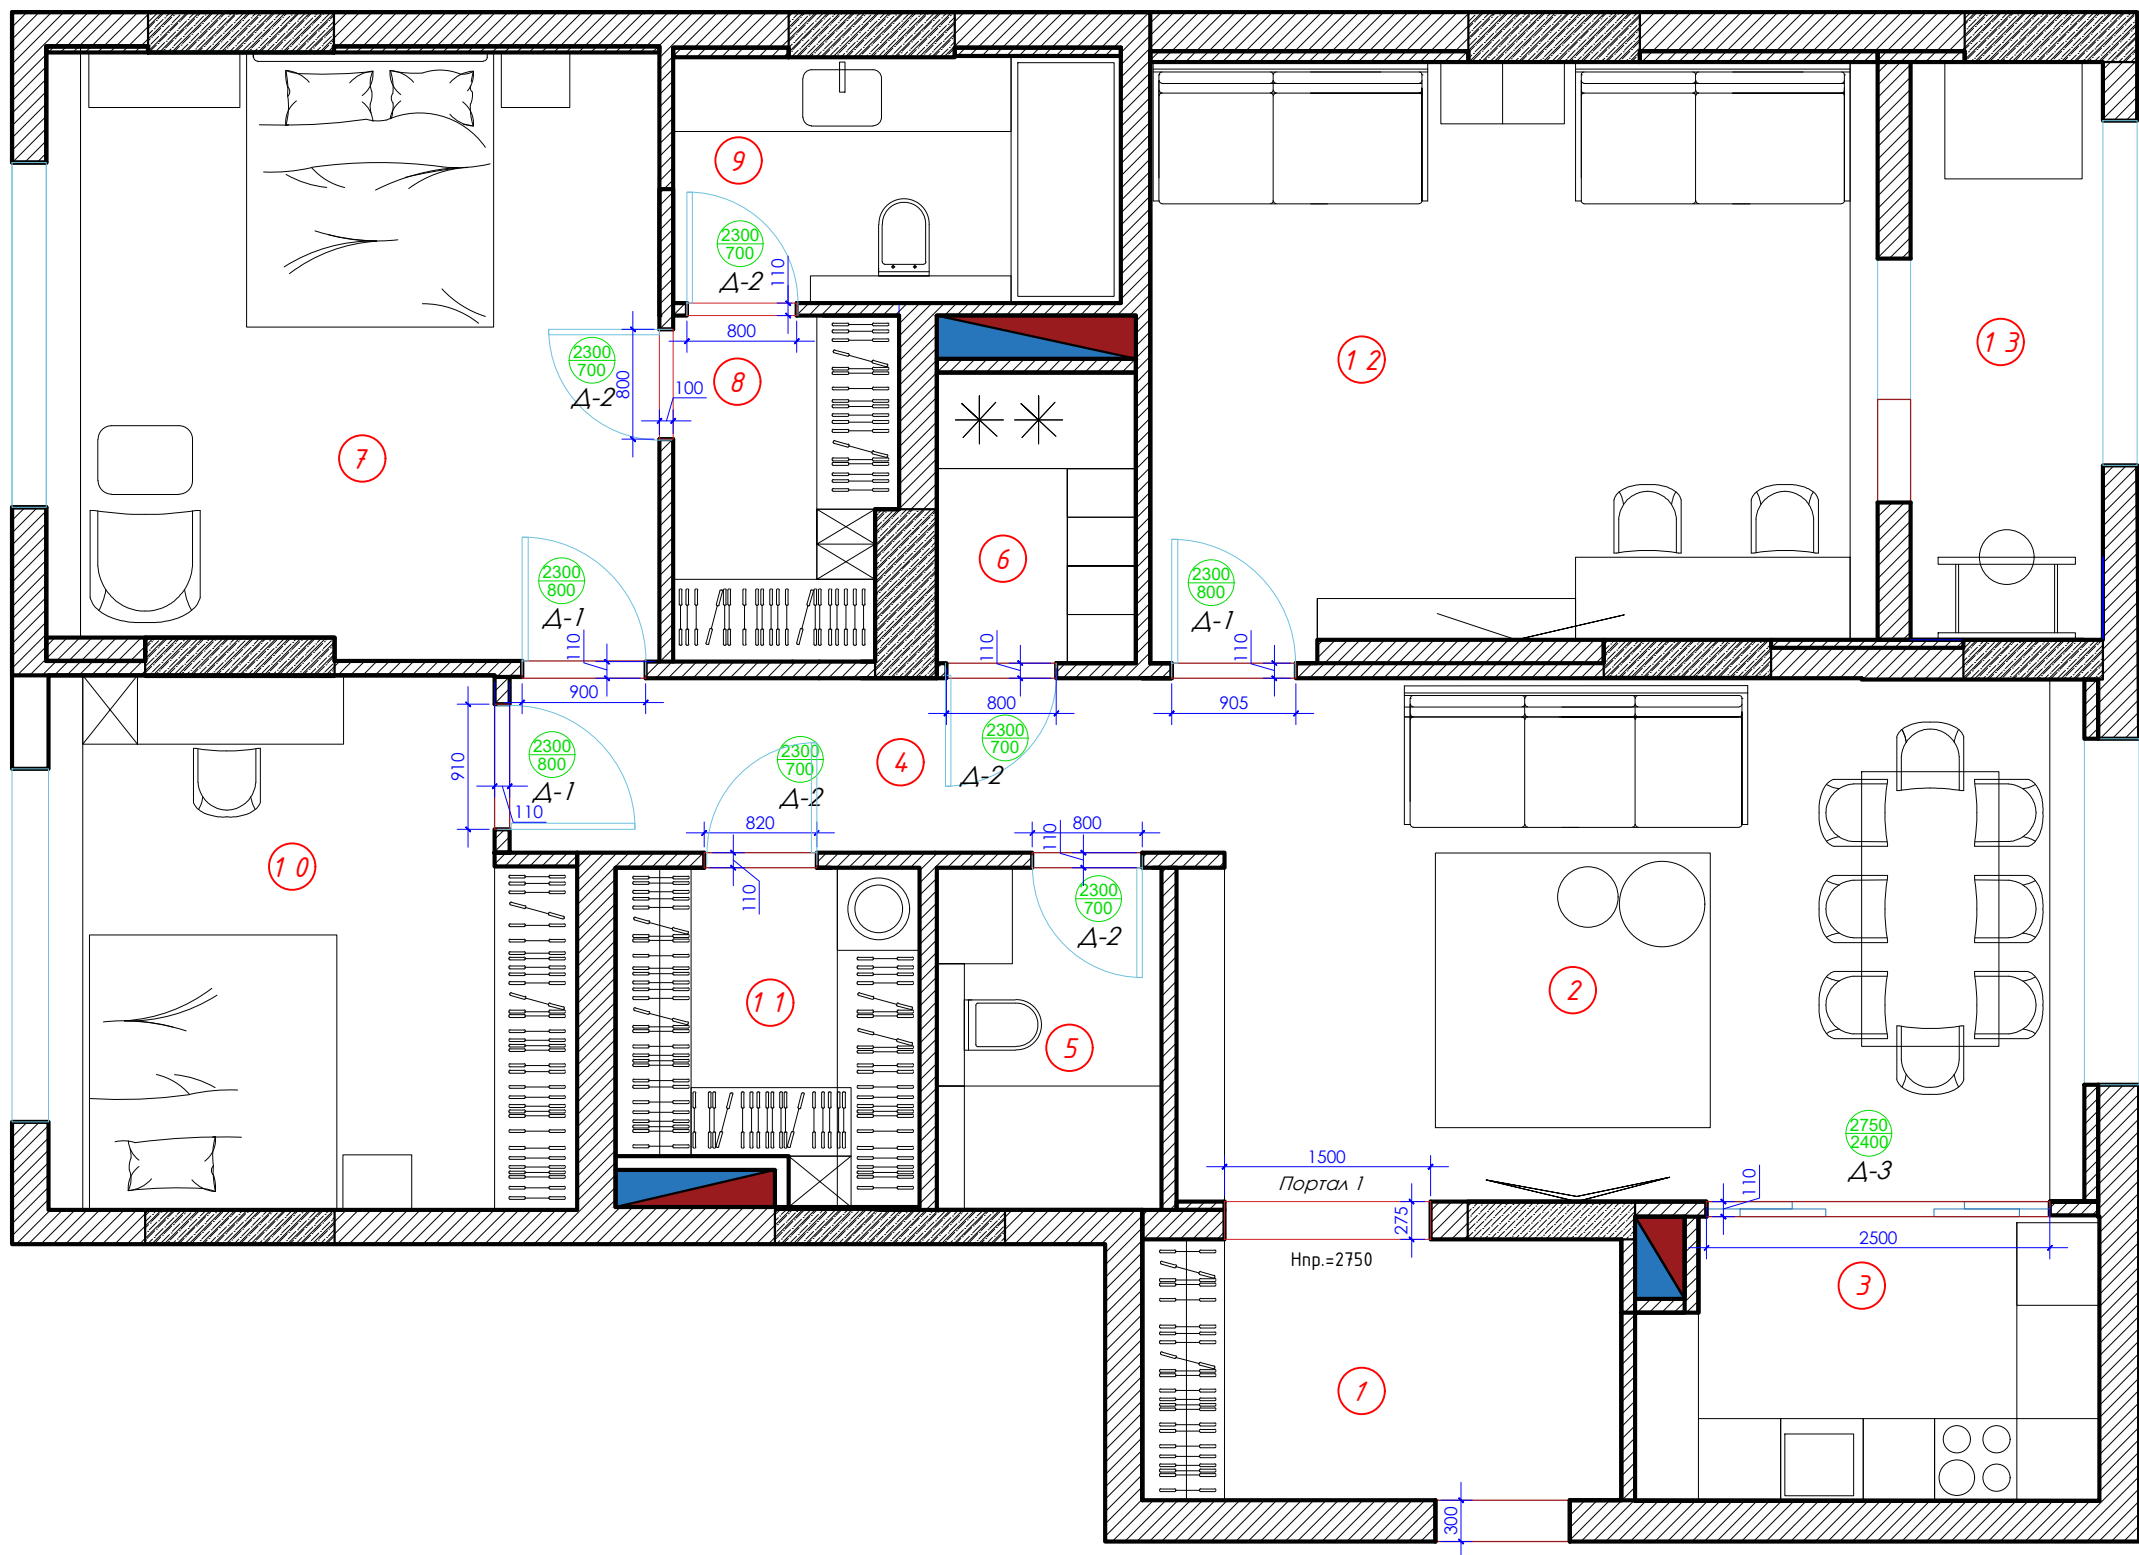

№	Экспликация помещений	м2
1	Прихожая	7,0
2	Зал	10,8
3	Кухня	14,0
4	Коридор	6,5
5	Гост.санузел	5,4
6	Кладовая	30,0
7	Мастер спальня	3,2
8	Мастер гардероб	3,4
9	Мастер санузел	5,1
10	Детская комната девочки	15,0
11	Гардероб мальчиков	4,2
12	Комната мальчиков	19,1
13	Спортивная зона мальчиков	6,2
Итого		130

№	Наименование	Обозначение
1	Высота полотна Ширина полотна	2300 800
2	Название проема	Д-1

Рабочий проект квартиры в ЖК Monaco Residence	Стадия	Лист	Листов
	РП		
План открывания дверей		adilova_design творческая мастерская	

Примечания:
1. Принять высоту рабочих дверных проемов равной 2360 мм (чистовой отметкой считать уровень покрытия пола отделочных материалов).
2. Высота входного дверного проема дается от застройщика
3. Доборные доски рекомендуется переизмерить по факту ремонтных работ