


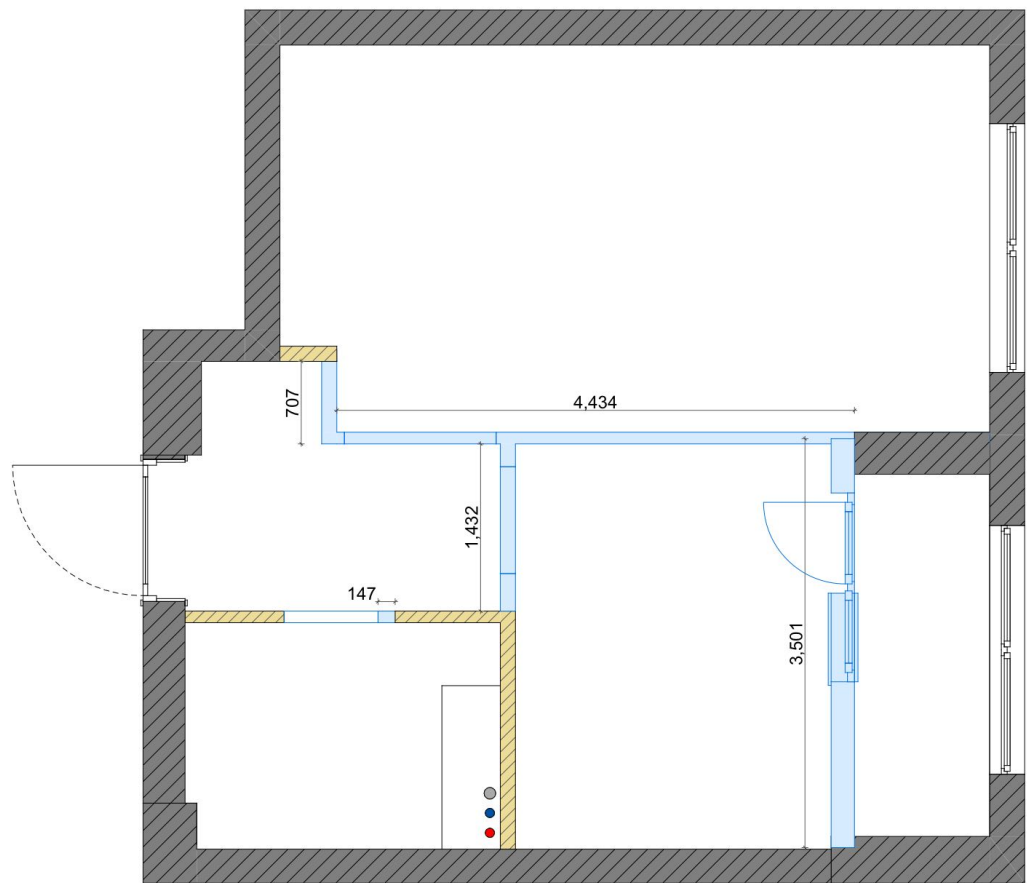

-  - канализационная труба
-  - труба подачи горячего водоснабжения
-  - труба подачи холодного водоснабжения




Условные обозначения:

- демитируемые перегородки
- существующие перегородки

Дизайнер	Мадина	Дизайн-проект квартиры по адресу:	План демонтажа	Стадия	Лист	Листов
телефон	+7 701 507 09 03	ЖК "Республика"	Масштаб 1:35	РП	03	

План возводимых перегородок с маркировкой оконных и дверных проемов

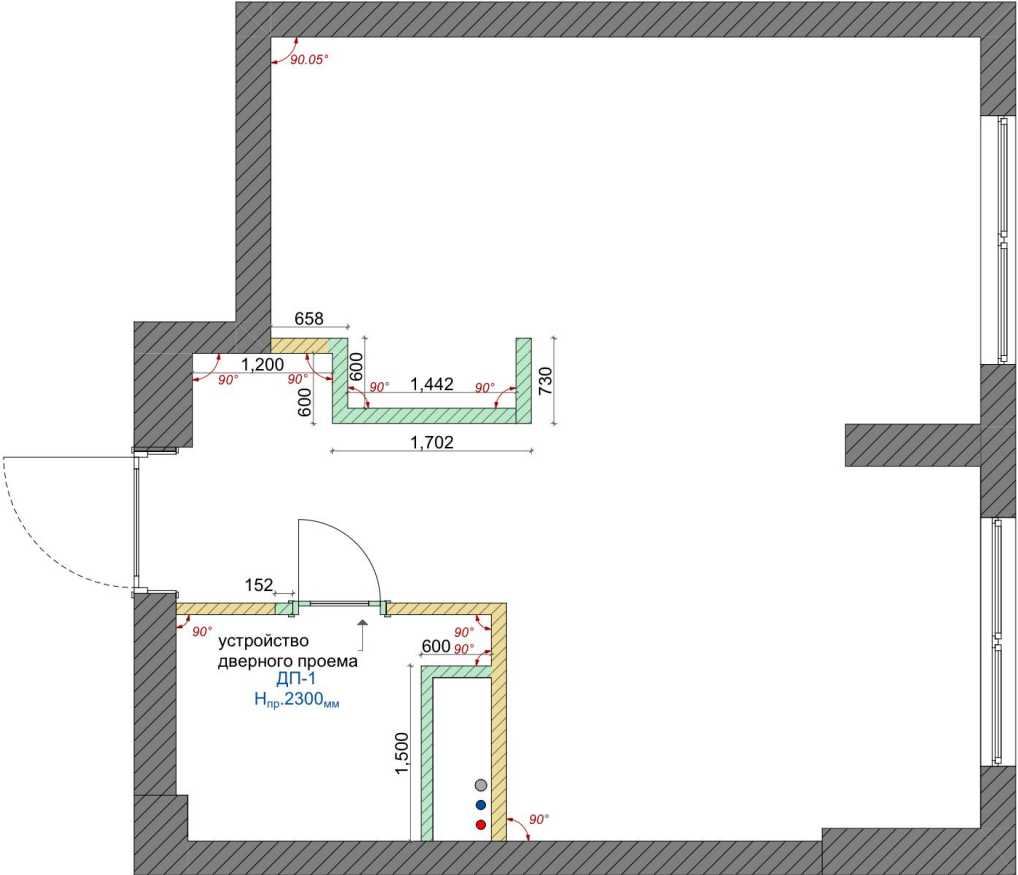


Условные обозначения:

- существующие перегородки
- новые возводимые перегородки из гипсокартона 100 мм


Примечание:

1. Возвести перегородки из гипсокартона толщиной 100 мм;
2. Высота всех проемов указана от уровня чистового пола;
3. Все стены выровнять под 90 градусов (для точного примыкания ко встроенной мебели)


Дизайнер	Мадина	Дизайн-проект квартиры по адресу:	План возводимых перегородок с маркировкой оконных и дверных проемов	Стадия	Лист	Листов
телефон	+7 701 507 09 03	ЖК "Республика"	Масштаб 1:35	РП	04	

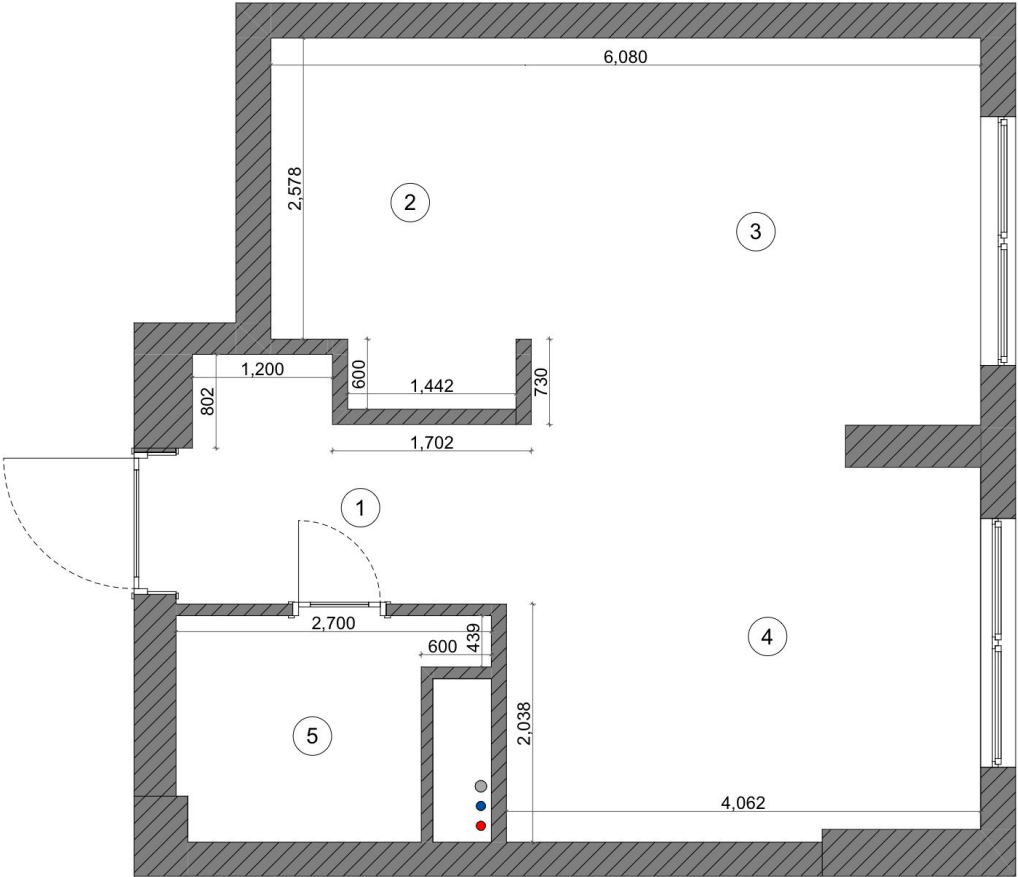

Экспликация помещений после перепланировки		
№	Название помещения	S, кв.м
1	Прихожка	5.65
2	Спальня	6.61
3	Гостиная	12.75
4	Кухня	13.78
5	Санузел	4.30
		43.09 м²

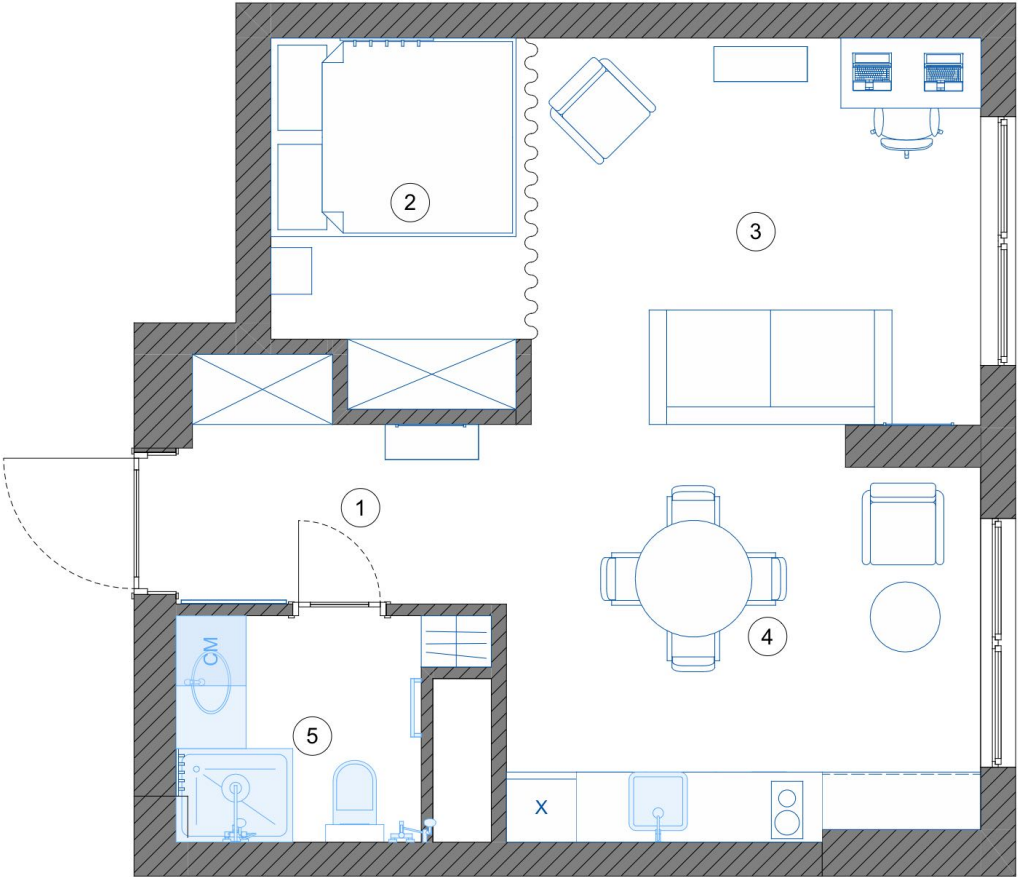


Экспликация помещений после перепланировки		
№	Название помещения	S, кв.м
1	Прихожка	5.65
2	Спальня	6.61
3	Гостиная	12.75
4	Кухня	13.78
5	Санузел	4.30
		43.09 м²

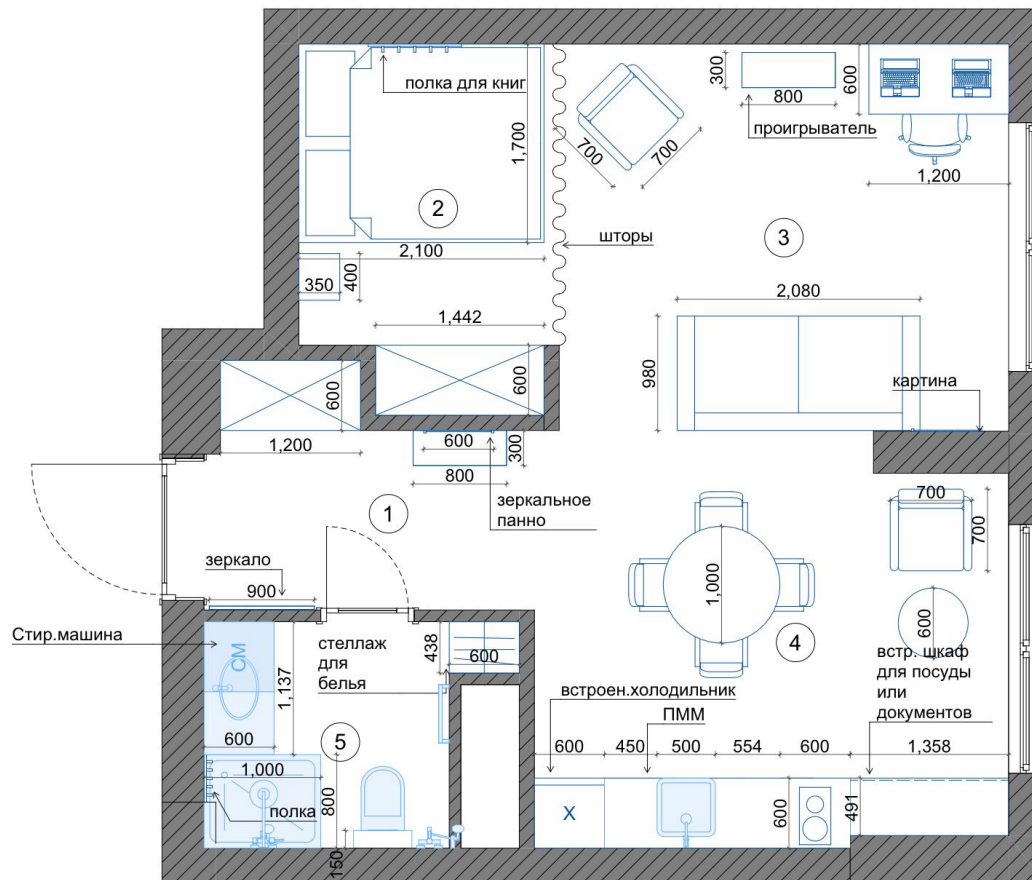

Дизайнер	Мадина	Дизайн-проект квартиры по адресу: ЖК "Республика"	План с мебельными размерами и описанием Масштаб 1:35	Стадия	Лист	Листов
телефон	+7 701 507 09 03			РП	07	

План размещения осветительных приборов, привязка выпусков освещения

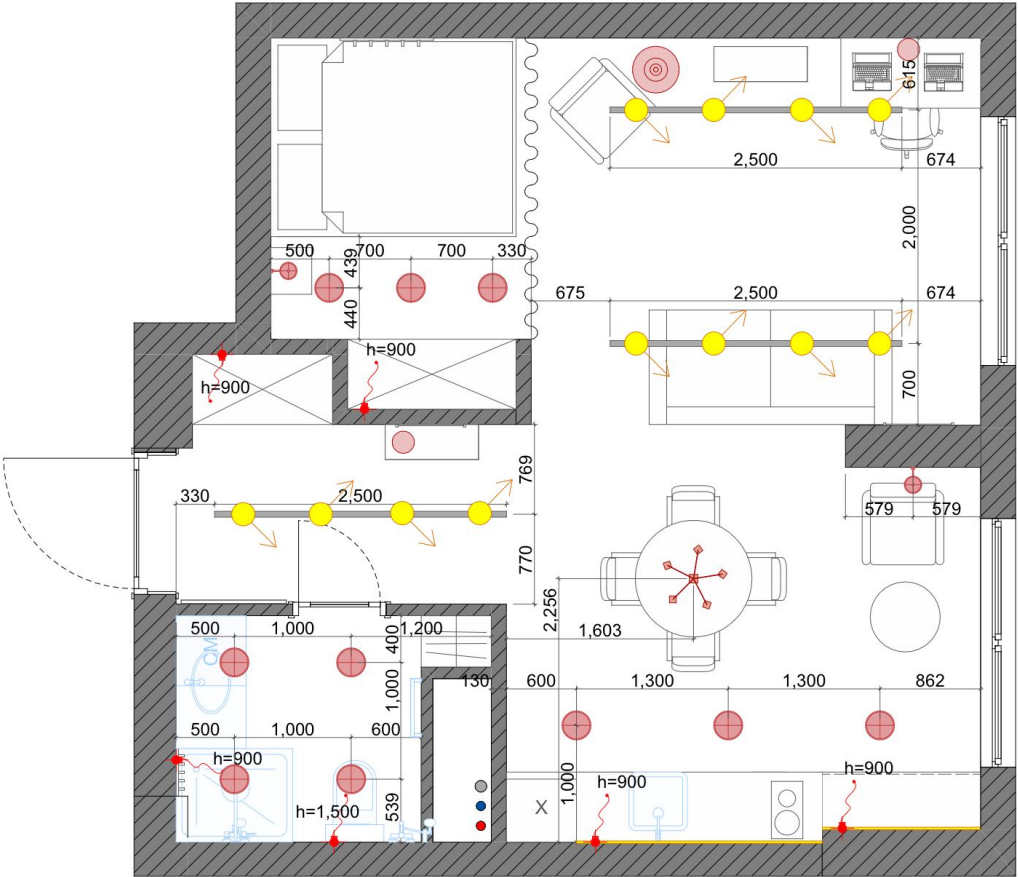

Условное обозначение светильников.		
Изображение	Тип светильника	Кол-во
	Электрический вывод	6
	Трековый светильник	12
	Люстра	1
	настенное бра	2
	накладной слот (двойной)	10
	напольная лампа	1
	настольная лампа	2
		34


Спецификация трека/шинопровода.		
ID	Условное обозначение	Наименование
Тр		Трек/Шинопровод
		Длина, мм
		7,500

Примечание:

1. В санузле установить влагозащитные светильники
2. Длина светодиодной ленты для встроенной мебели рассчитывается мебельщиками по факту
3. Все размеры даны по осям осветительных приборов
4. Светодиодная лента в прихожей и спальне включается и выкл. от датчика движения. Отработать с мебельщиками. А на кухне подсветка подключить к сенсорной кнопке, также с мебельщиками отработать.

Дизайнер	Мадина	Дизайн-проект квартиры по адресу:	План размещения осветительных приборов, привязка выпусков освещения	Стадия	Лист	Листов
телефон	+7 701 507 09 03	ЖК "Республика"	Масштаб 1:35	РП	08	

План выключателей с указанием включения групп светильников

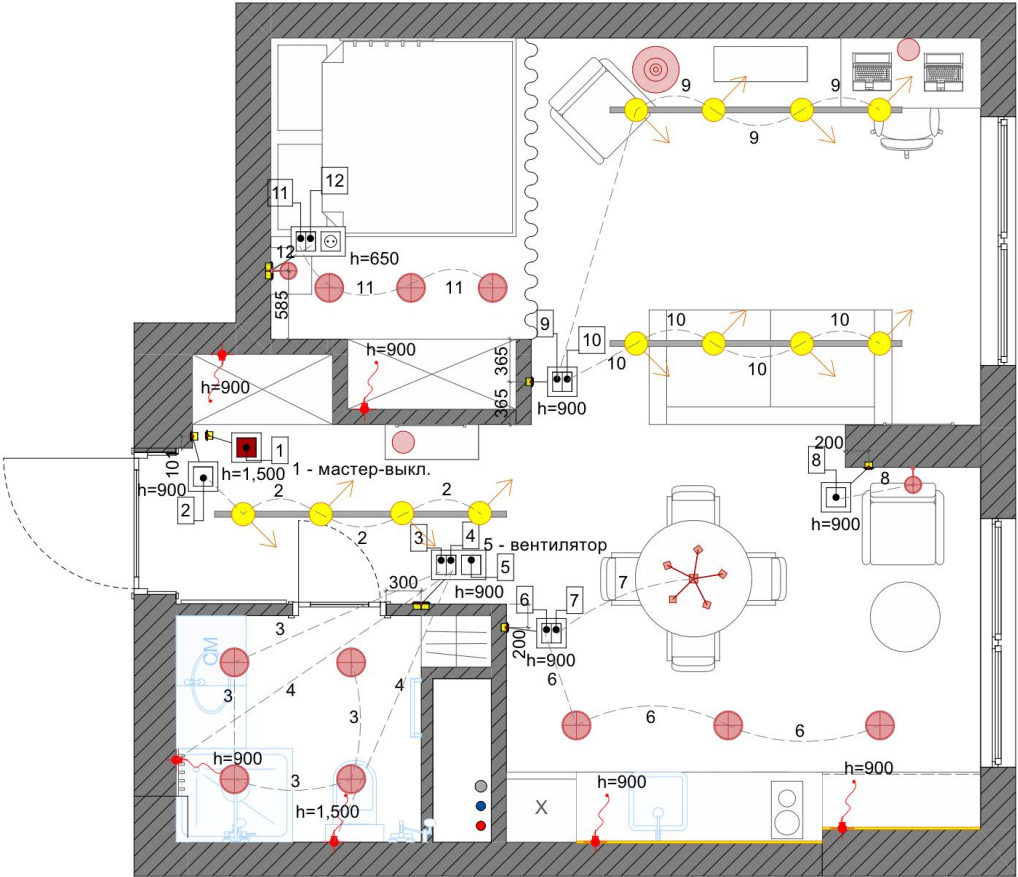

Условное обозначение светильников.		
Изображение	Тип светильника	Кол-во
	---	6
	Трековый светильник	12
	Люстра	1
	настенное бра	2
	накладной спот (двойной)	10
	напольная лампа	1
	настольная лампа	2
		34


Выключатели 1 этаж		
Условное обозначение	Наименование	Кол-во, шт
	Выключатель двухклавишный	4
	Выключатель одноклавишный	4

Примечание:

1. К клавише мастер-выкл. подключать только все источники освещения. Розетки не подсоединять.

Дизайнер	Мадина	Дизайн-проект квартиры по адресу:	План выключателей с указанием включения групп светильников	Стадия	Лист	Листов
телефон	+7 701 507 09 03	ЖК "Республика"	Масштаб 1:35	РП	09	

План размещения электрических розеток с привязкой размеров

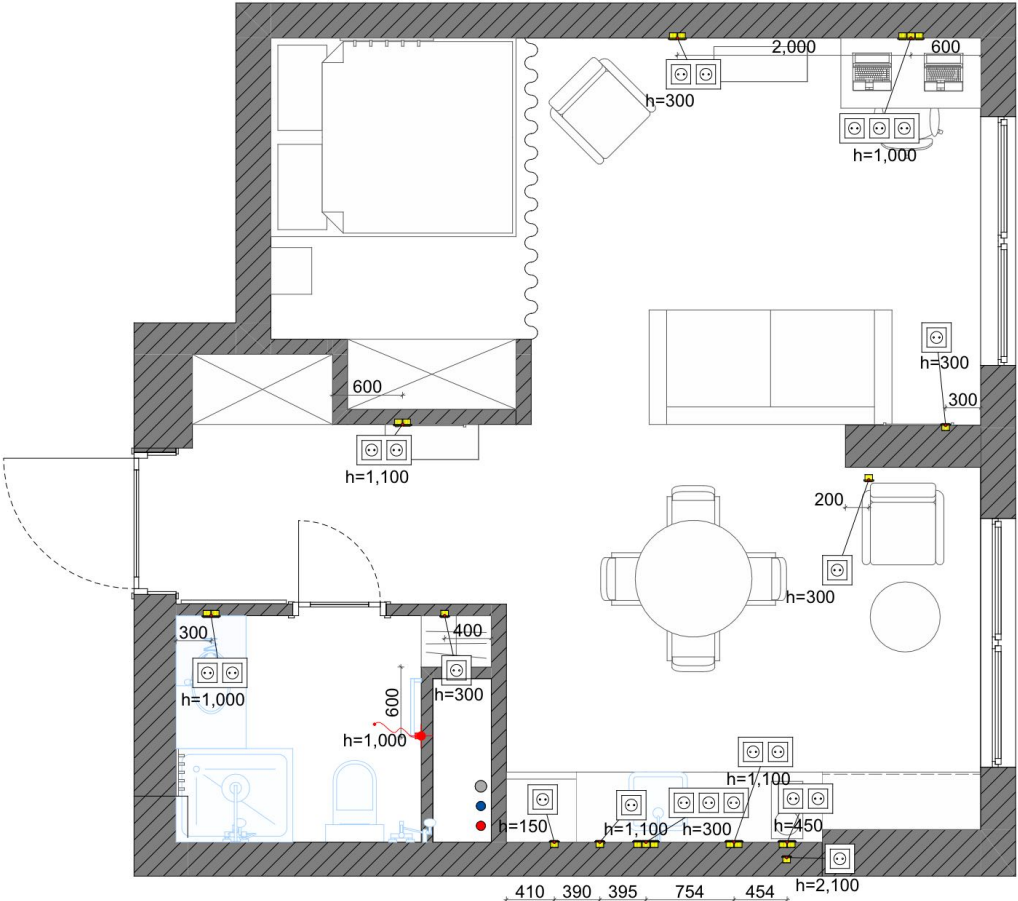

Условное обозначение	Наименование	Кол-во, шт
	Розетка бытовая	23


Рамки (общее количество) 1 этаж		
Тип рамки (блока)	Рамка ориентация	Кол-во
Рамка х1	Горизонтальная	11
Рамка х2	Горизонтальная	7
Рамка х3	Горизонтальная	2

Примечание:

1. На кухне для всех электрических приборов предусмотрены розетки. Если варочная поверхность и духовой шкаф будут подключаться напрямую, вычесть их из количества розеток и, соответственно, рамок.

Дизайнер	Мадина	Дизайн-проект квартиры по адресу:	План размещения электрических розеток с привязкой размеров	Стадия	Лист	Листов
телефон	+7 701 507 09 03	ЖК "Республика"	Масштаб 1:35	РП	10	

План полов с указанием типа напольных покрытий

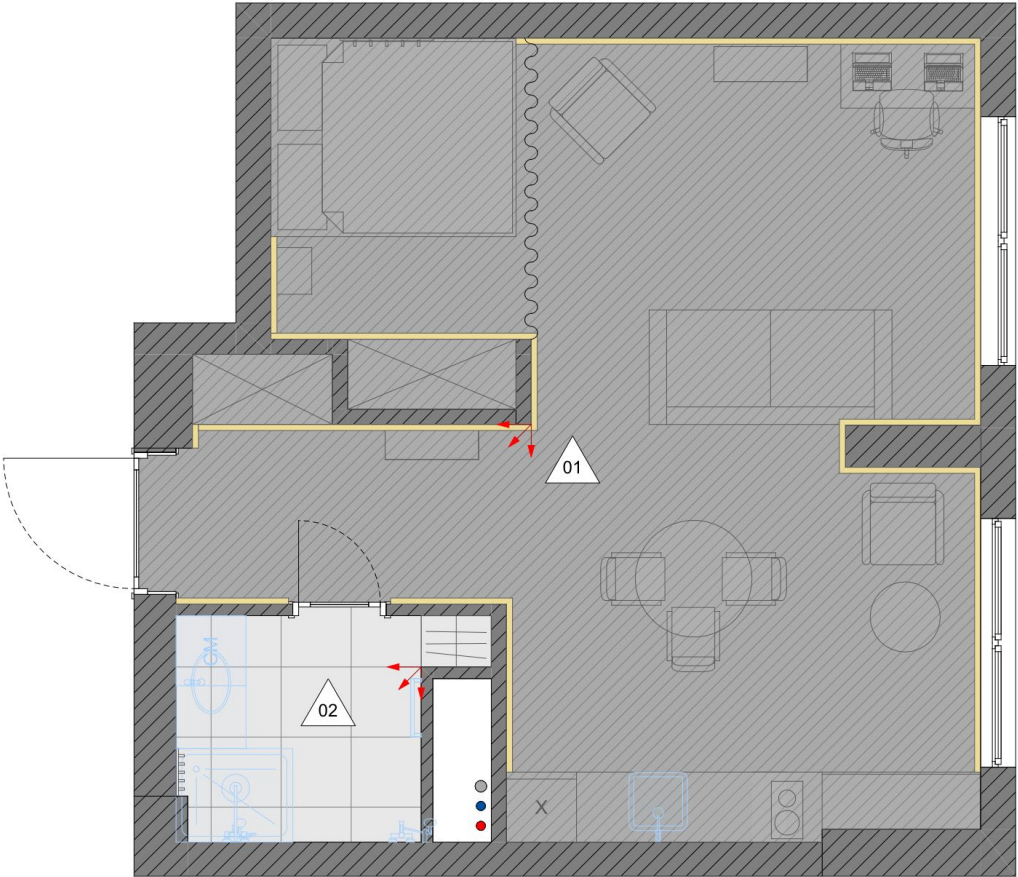

Напольные покрытия. 1 этаж					
ID	Условное обозначение	Наименование	S нетто, кв.м (без запаса)	Примечание	Изображение
01		каварзинет (укладка по диагонали)	38.83		
02		керамогранит 60*60	4.36		

Спецификация плинтуса. 1 этаж						
ID	Условное обозначение	Сечение	Изображение	Наименование	Артикул	Производитель
П01				Плинтус 100мм	123	

Условные обозначения:


- направление укладки плитки
- обозначение типа пола

Примечание:

- 1. Количество материала дано без запаса на подрезку.
- 2. Привязку стыка напольных покрытий внутри дверных проемов уточнить у поставщика дверей.

Дизайнер	Мадина	Дизайн-проект квартиры по адресу:	План полов с указанием типа напольных покрытий	Стадия	Лист	Листов
телефон	+7 701 507 09 03	ЖК "Республика"	Масштаб 1:35	РП	12	

План расположения систем отопления и вентиляции

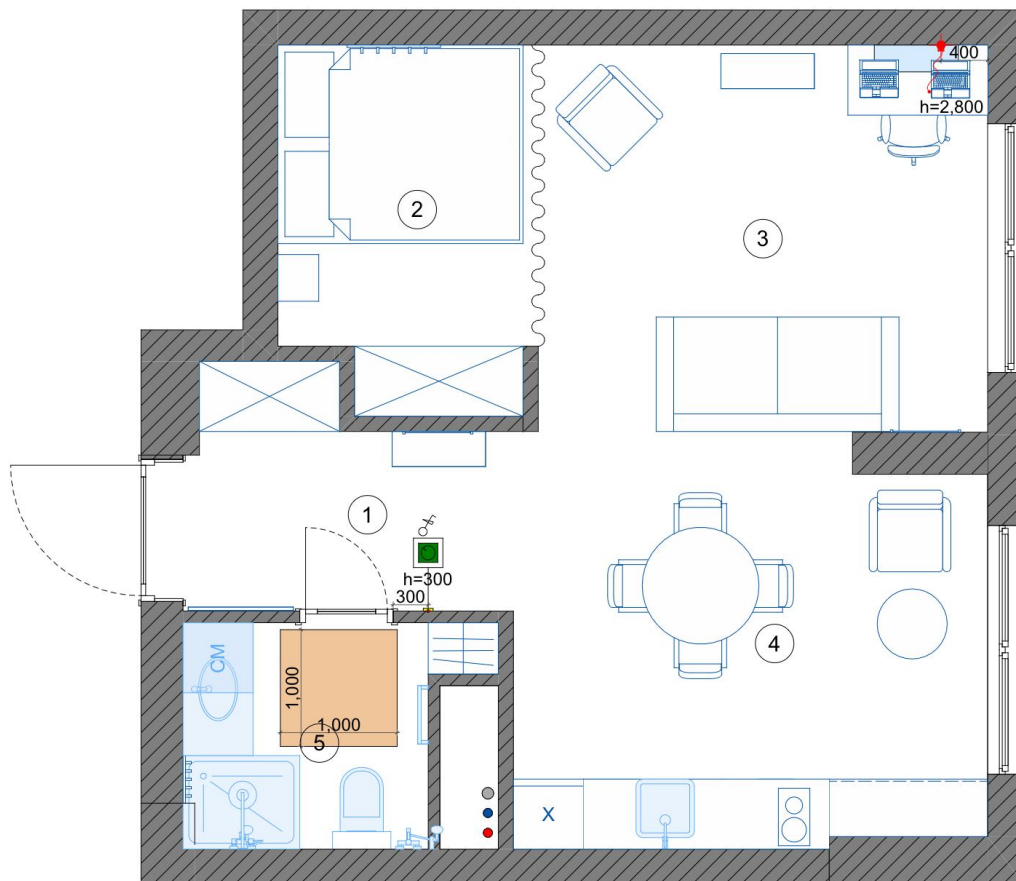

Теплый пол.		
Условное обозначение	Наименование	S, кв.м/ кол-во, шт
	Тёплый пол	
		м ²


Регулятор тёплого пола.		
Условное обозначение	Наименование	Кол-во, шт
	Регулятор теплого пола	1

Условные обозначения:



Дизайнер	Мадина	Дизайн-проект квартиры по адресу: ЖК "Республика"	План расположения систем отопления и вентиляции Масштаб 1:35	Стадия	Лист	Листов
телефон	+7 701 507 09 03			РП	13	

План отделочных материалов по стенам

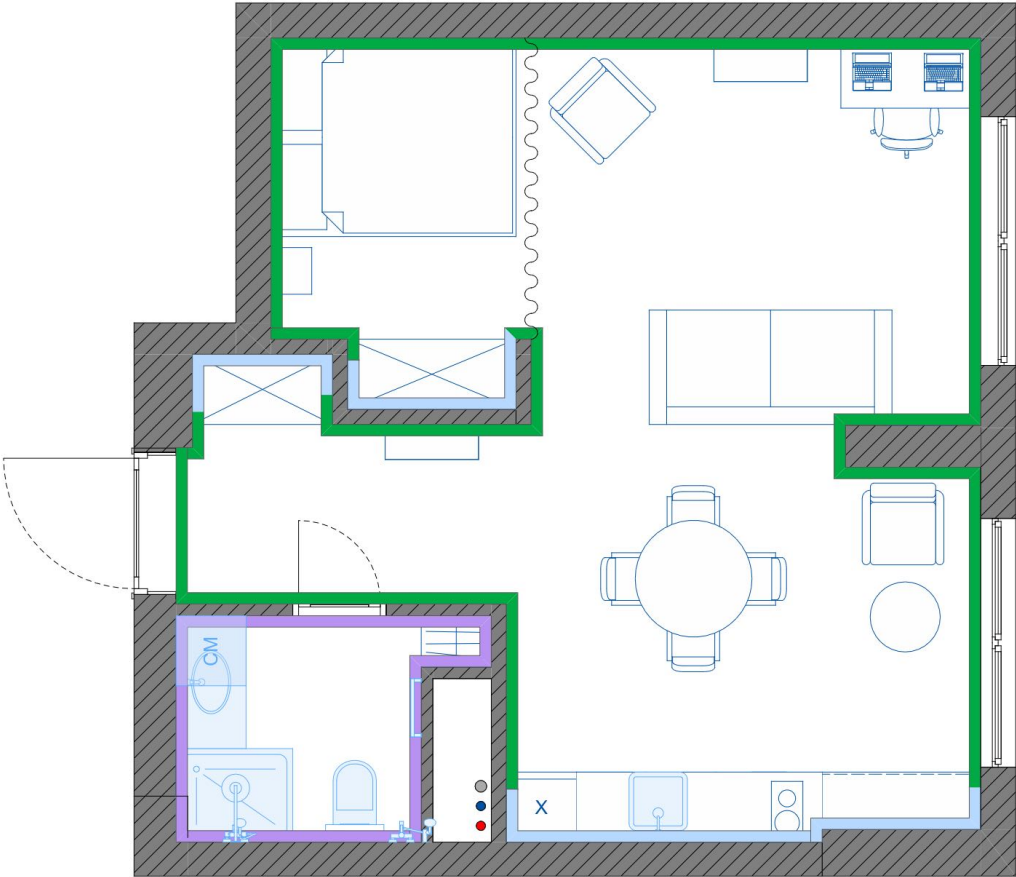

Условное обозначение	Наименование
	Покраска
	Краска колеровочная
	Керамогранит