

Технический проект

2-х комнатная квартира, ЖК Jetisu Kerbez

г. Астана 2026 г.

Ведомость чертежей

Лист	Наименование	Примечание
1	Ведомость чертежей	
2	План до перепланировки (обмерный план)	
3	План демонтажа	
4	План монтажа	
5	План после перепланировки	
6	План расстановки мебели	
7	План напольных покрытий	
8	План отделки потолков	
9	План привязки освещения	
10	План управления освещением	
11	План электрооборудования	
12	План теплого пола	
13	План сантехнического оборудования	


ОБЩИЕ УКАЗАНИЯ:

Данный комплект чертежей является рекомендательным, и должен уточняться производителем работ. Необходимые корректировки согласовать с разработчиками проекта

Перед началом производства работ внимательно ознакомиться с Примечаниями на листах Выводы и коммуникацию для кондиционера уточнить по месту и согласовать с специалистами по кондиционеру.

Электрику и коммуникацию для кухонной мебели согласовать с изготовителем кухни. Вся отделка подсчитано без запаса. При заказе брать с запасом на 10% больше.

					Стадия	Лист	Листов
					РП	1	
Дизайнер	Джамбулатов А.			Ведомость чертежей			

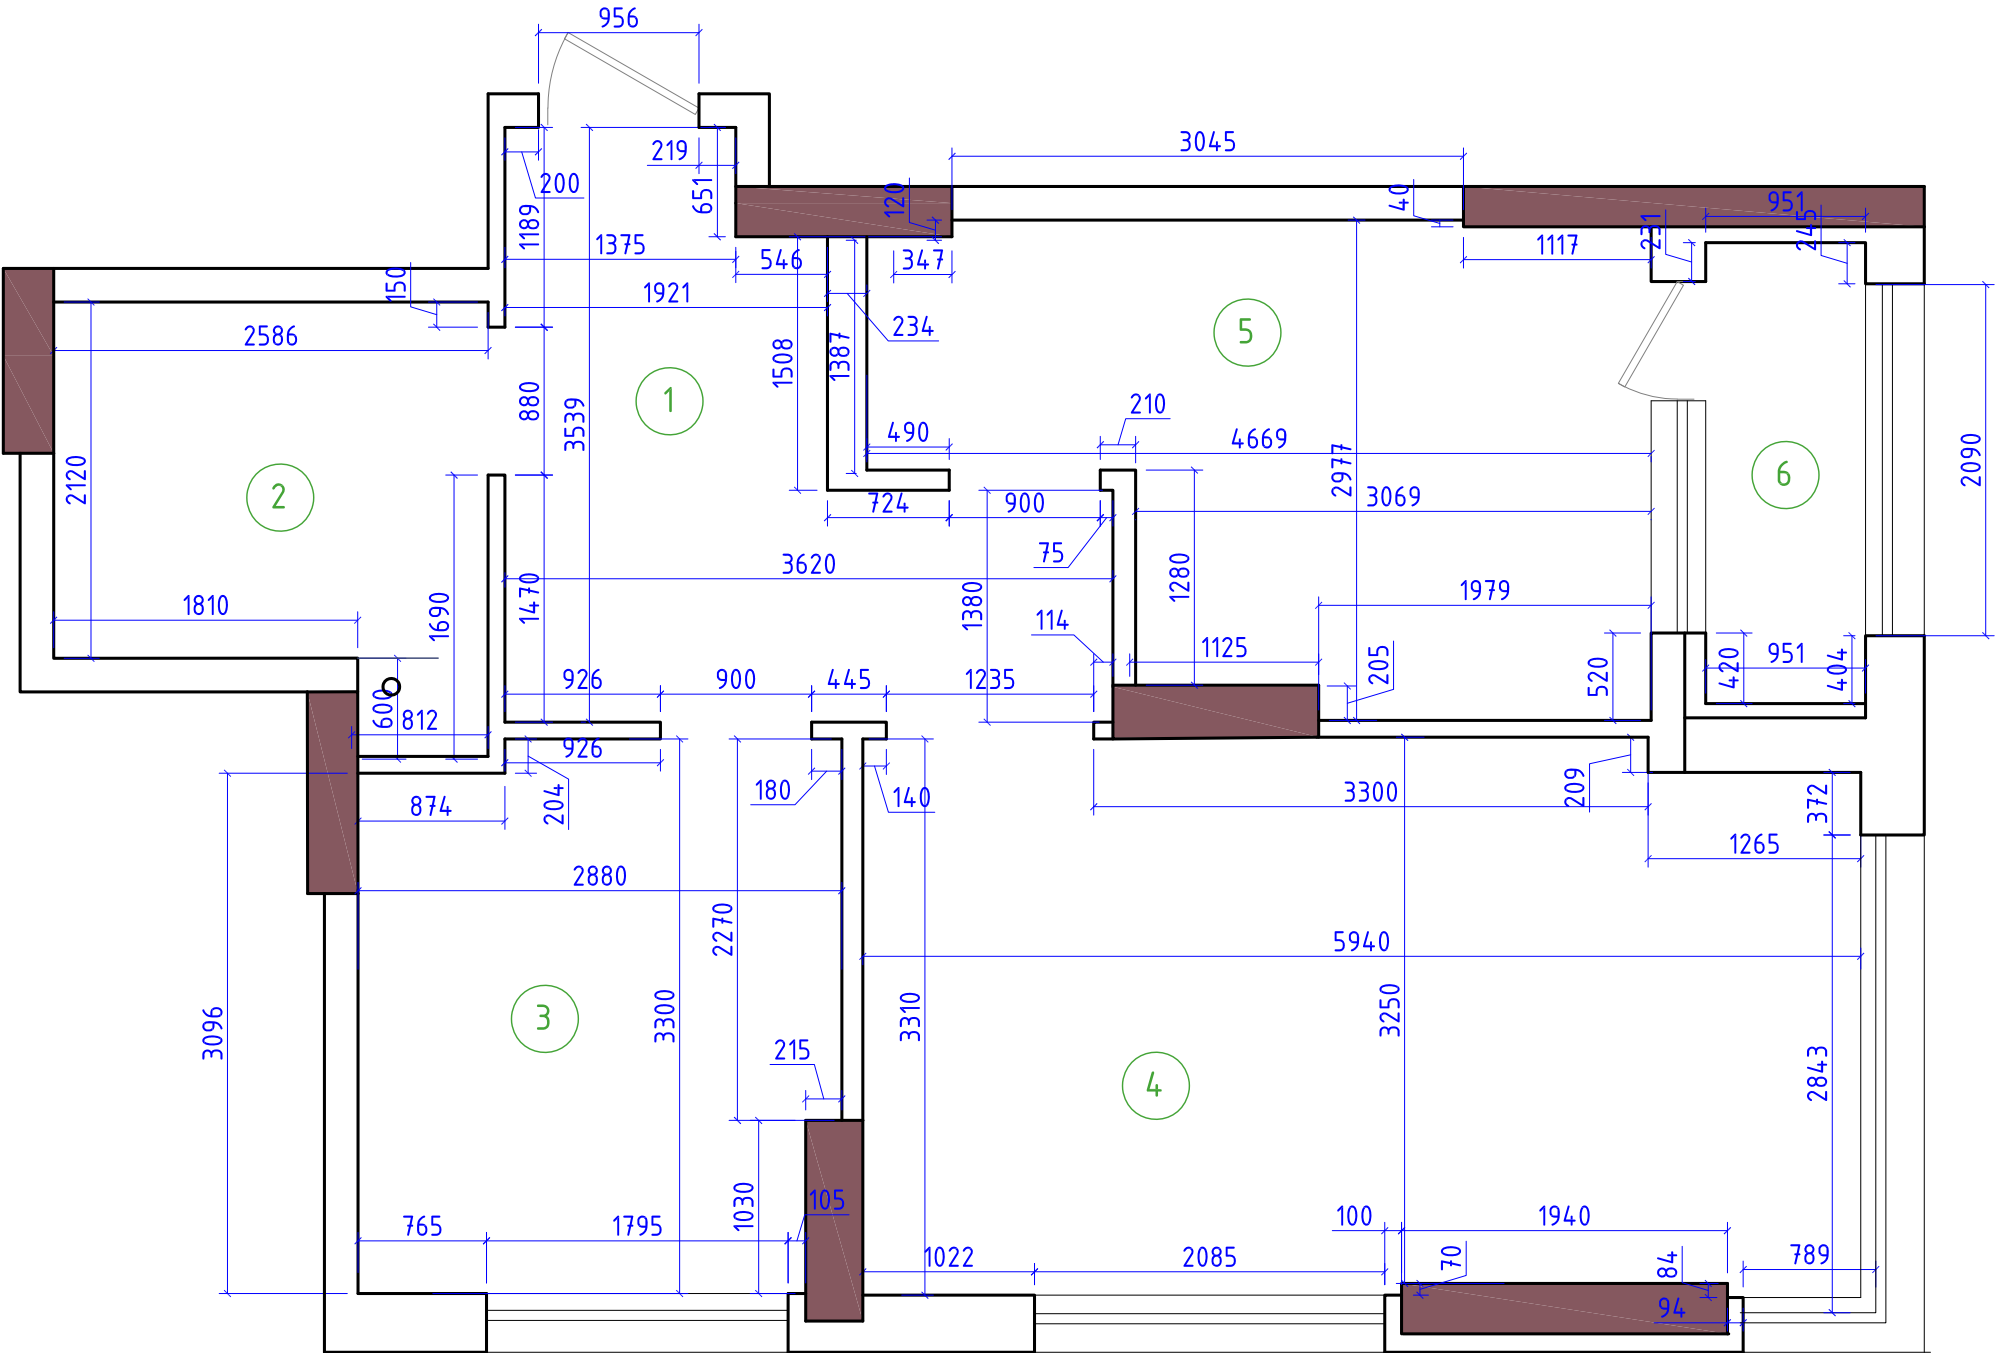


Экспликация помещений до перепланировки:

Номер	Наименование	Пл., м2
1	Прихожая	8,7
2	Санузел	5,4
3	Кухня	9,1
4	Гостиная	19,2
5	Спальня	11,0
6	Лоджия	2,6
Общая площадь		56,0

ПРИМЕЧАНИЕ

- все чертежи выполнены на основе обмеров существующих перегородок
- размеры и высоты даны от уровня чернового пола
- за отм. 0.000 дана отметка чернового пола
- все чертежи выполнены основываясь на замере объекта по "черновым" стенам, в связи с этим возможно незначительное расхождение размеров на плане и в реальности
- любые расхождения с проектом согласовать с дизайнером
- все размеры указаны в миллиметрах и являются проектными. По факту могут отличаться в большую или меньшую сторону

					Стадия	Лист	Листов
					РП	2	
Дизайнер	Джамбулатов А.			План до перепланировки (обмерный план)			

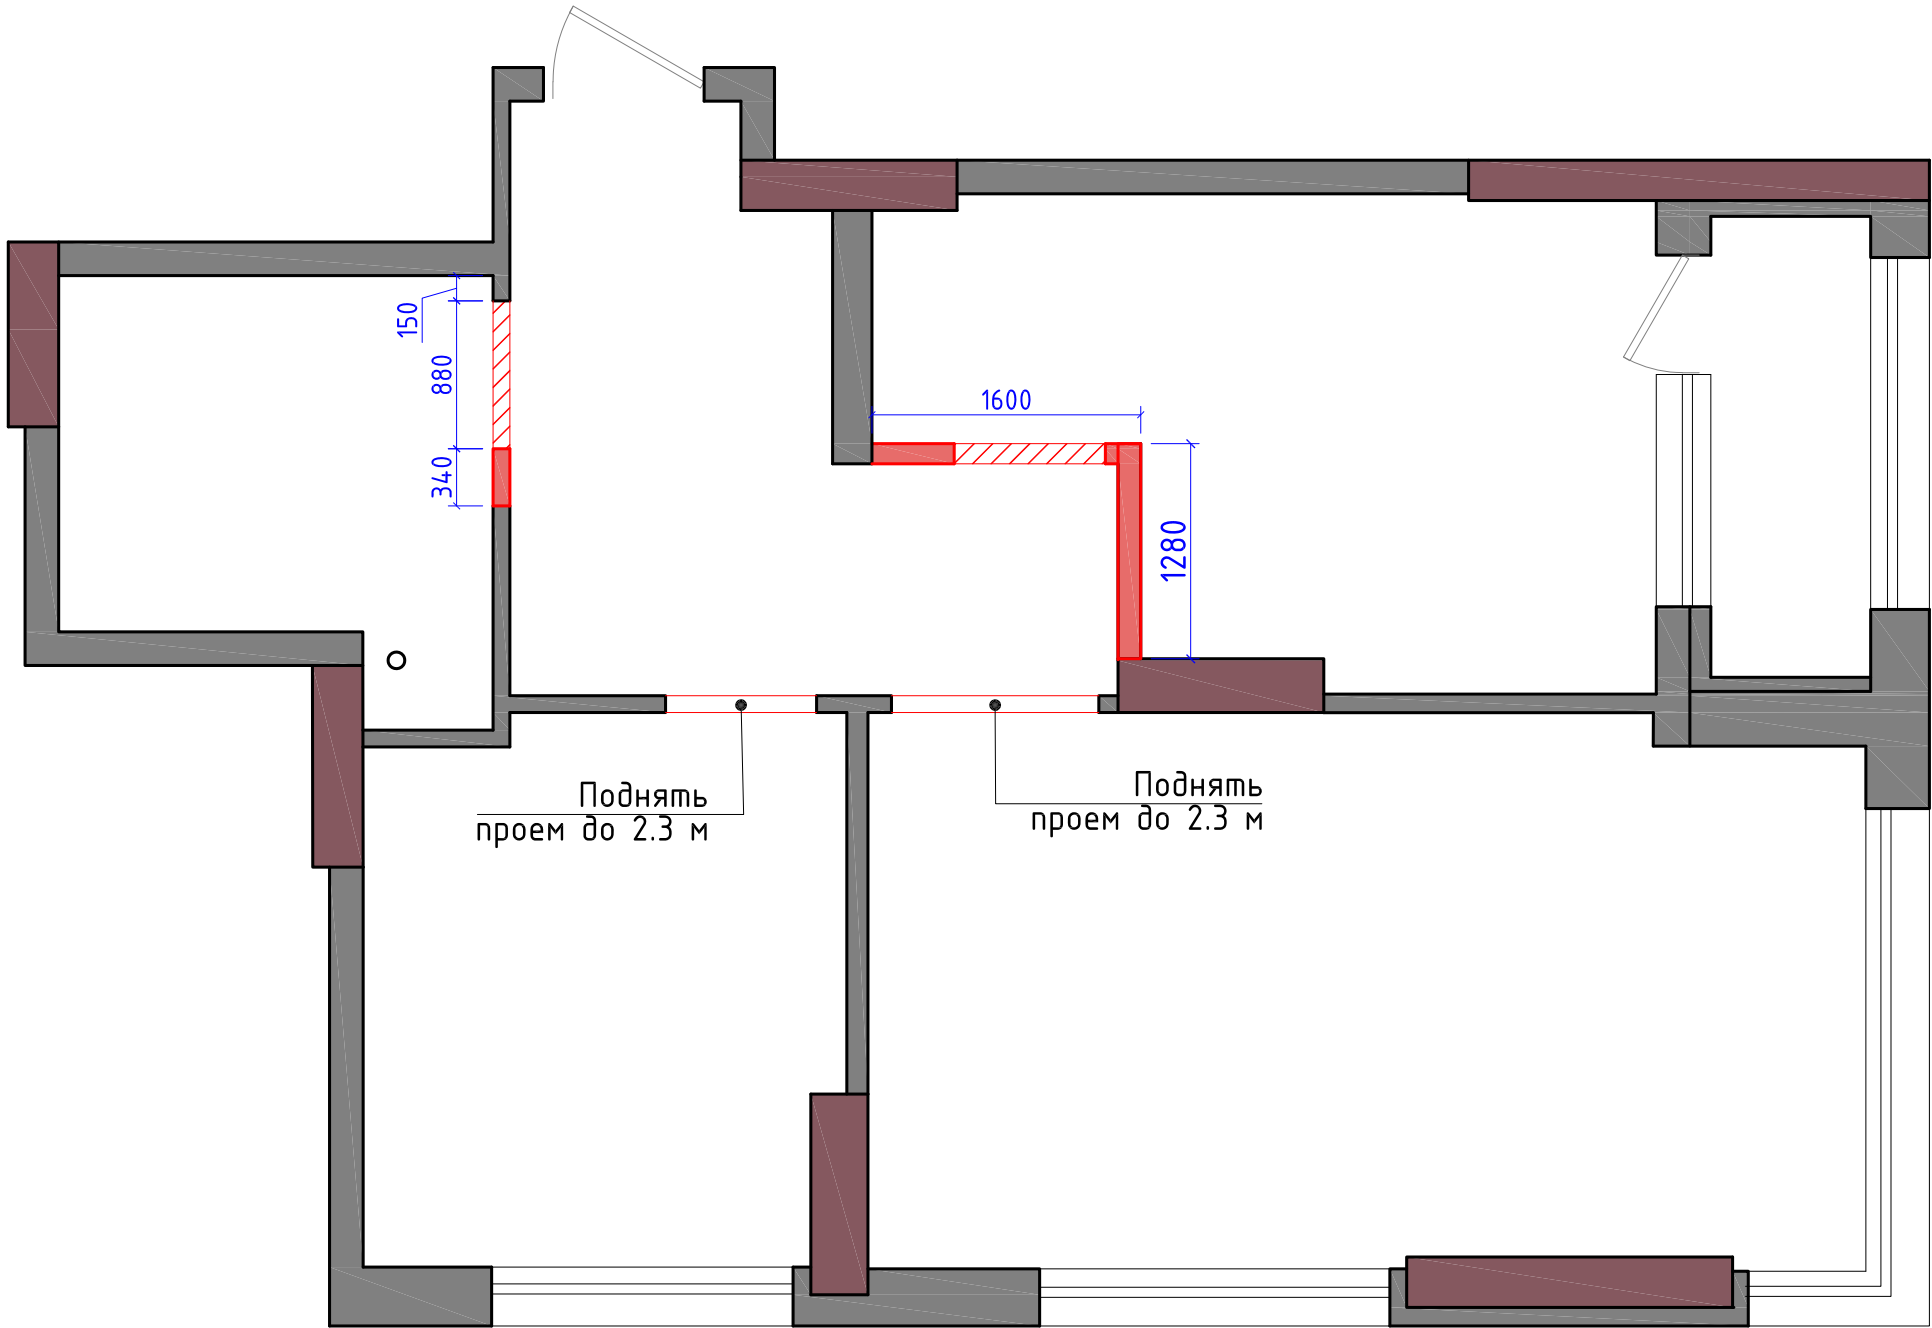


Условные обозначения:	
	Существующие стены и перегородки
	Демонтируемые перегородки
	Демонтируемые проемы
	Радиатор отопления
	Канализационный стояк
	Трубы водоснабжения ГВС/ХВС

ПРИМЕЧАНИЕ

- Все чертежи выполнены на основе обмеров существующих перегородок
- Размеры и высоты даны от уровня чернового пола
- Фактическая площадь при замерах 56,0 м2
- За отм. 0.000 дана отметка чернового пола
- Все чертежи выполнены основываясь на замере объекта по “черновым” стенам, в связи с этим возможно незначительное расхождение размеров на плане и в реальности
- Любые расхождения с проектом согласовать с дизайнером
- Все размеры указаны в миллиметрах и являются проектными. По факту могут отличаться в большую или меньшую сторону

					Стадия	Лист	Листов
					РП	3	
Дизайнер	Джамбулатов А.			План демонтажа			

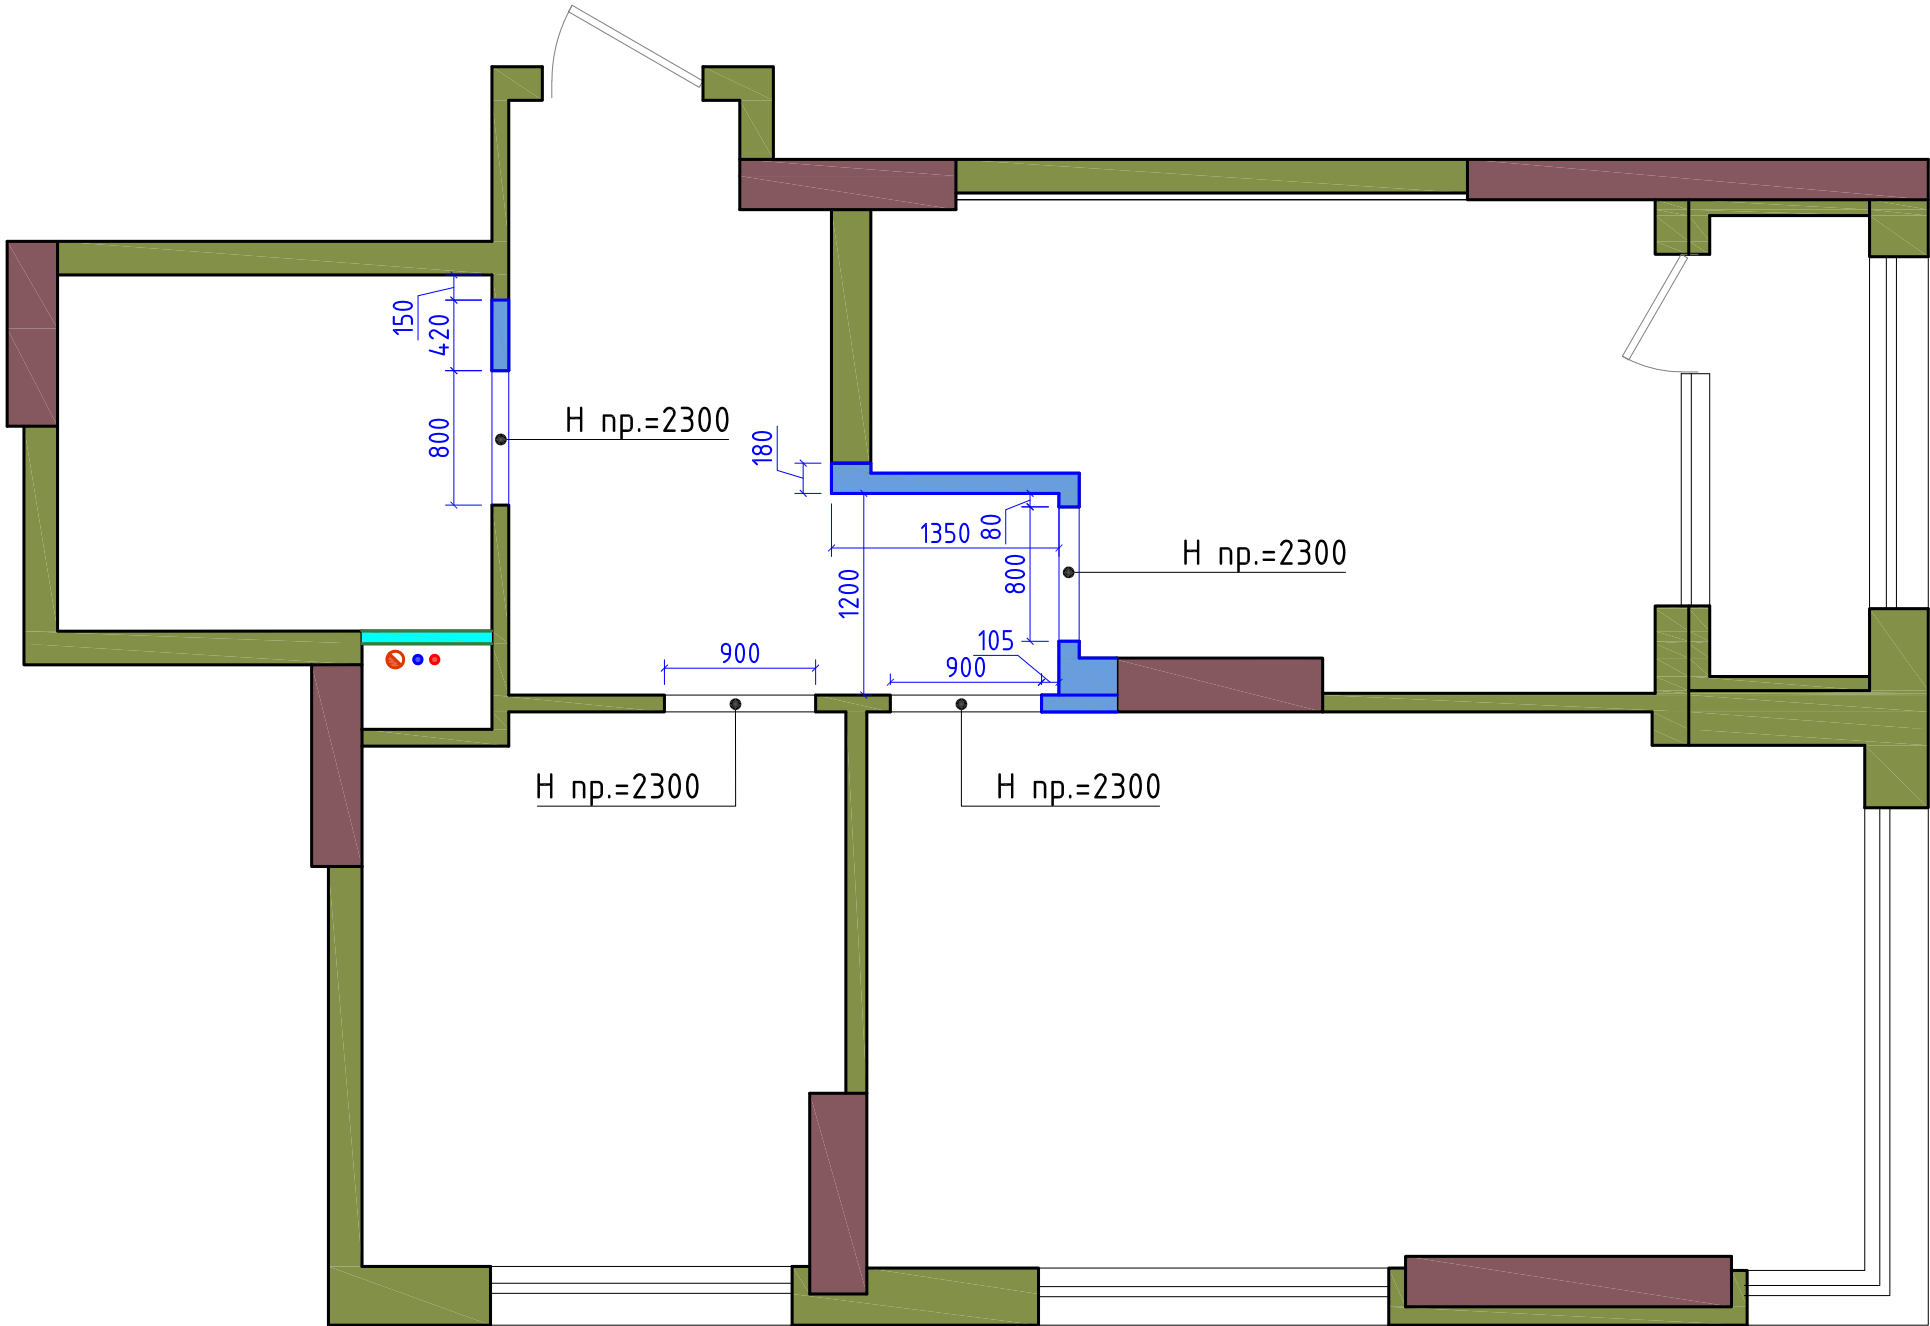

Условные обозначения:	
	Существующие стены и перегородки
	Монтируемые перегородки (газоблок)
	Монтируемые перегородки (ГКЛ)
	Монтируемые перегородки (ГКЛВ)
	Радиатор отопления
	Канализационный стояк
	Трубы водоснабжения ГВС/ХВС

ПРИМЕЧАНИЕ

1. За отм. 0.000 дана отметка чистового пола

2. Предусмотреть люки для электрощитков и доступа к водопроводным счетчикам. А так же ревизионные люки

3. Точное расположение люков утвердить с управляющим стройкой на месте

– размеры дверных проемов зависят от выбранной модели и поставщика. При замене двери размер проема может изменится

4. Монтаж проемов делать по техкарте поставщиков дверей предусмотреть все необходимые закладные под навесную мебель на стенах

смотреть совместно с развертками определить со строителями, необходимо ли использовать выравнивающую штукатурку

5. В случае использования дверей скрытого монтажа, короб монтировать до начала чистовой отделки

6. Перед заказом кухни и встраиваемой мебели необходим предварительный замер


7. Любые расхождения с проектом согласовать с дизайнером

8. Все размеры указаны в миллиметрах и являются проектными. По факту могут отличаться в большую или меньшую сторону

9. Внешние перегородки в месте установки раздвижной двери устанавливаются после монтажа закладных элементов этой двери

10. Читать совместно с планом электрооборудования и планом сантехнических приборов

					Стадия	Лист	Листов
					РП	4	
Дизайнер	Джамбулатов А.			План монтажа			

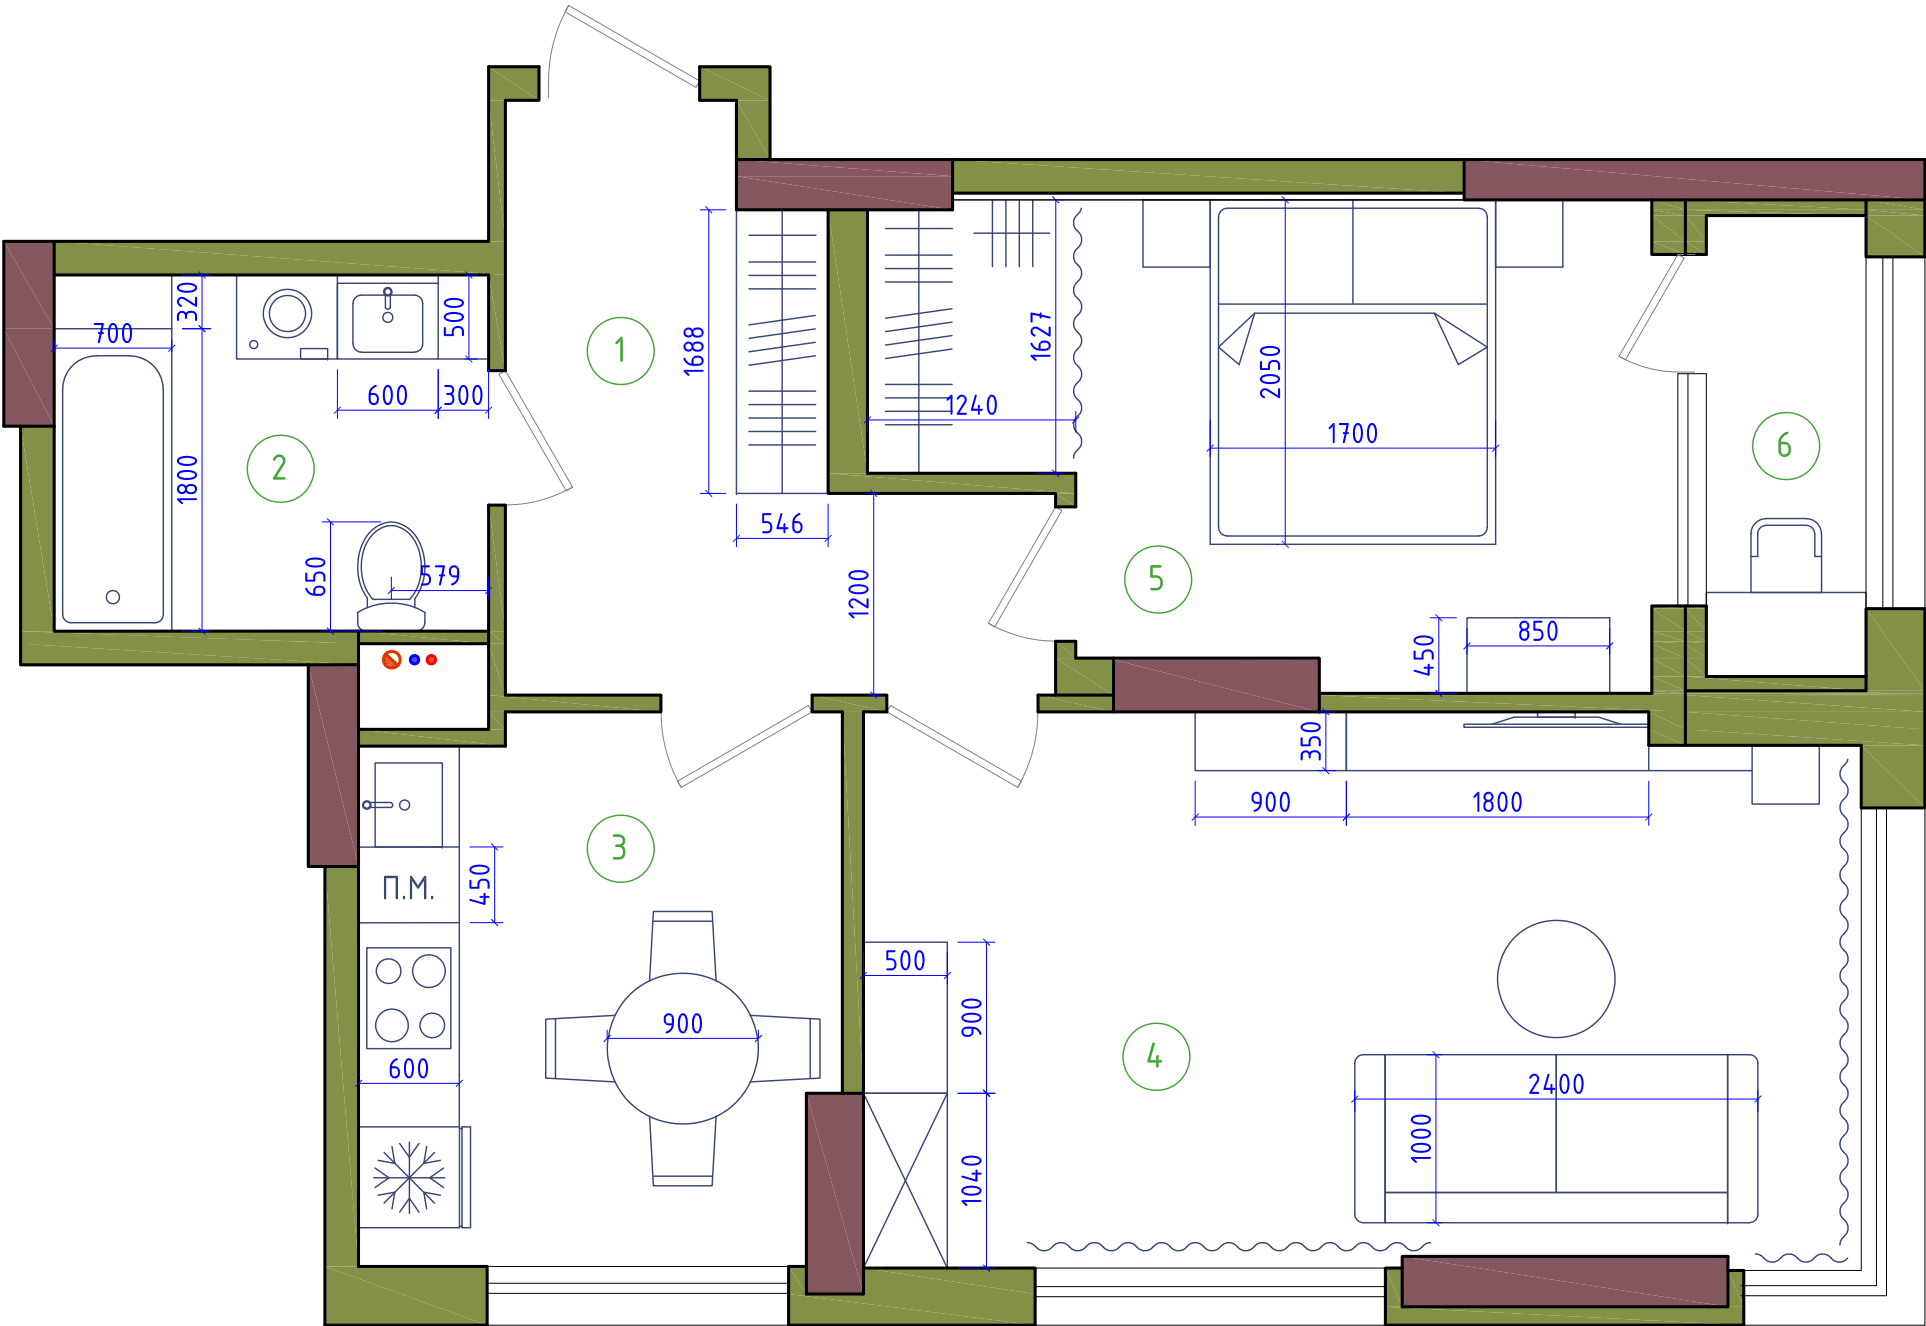


Экспликация помещений:

Номер	Наименование	Пл., м2
1	Прихожая	8,0
2	Санузел	5,4
3	Кухня	9,1
4	Гостиная	19,2
5	Спальня	11,7
6	Лоджия	2,6
Общая площадь		56,0

ПРИМЕЧАНИЕ

- Перед заказом кухонного гарнитура и встроенной мебели (шкафы, навесные шкафы) требуется предварительный замер фирмы поставщика
- Любые расхождения с проектом согласовать с дизайнером
- Все размеры указаны в миллиметрах и являются проектными. По факту могут отличаться в большую или меньшую сторону

					Стадия	Лист	Листов
					РП	7	
Дизайнер	Джамбулатов А.			План расстановки мебели с размерами			

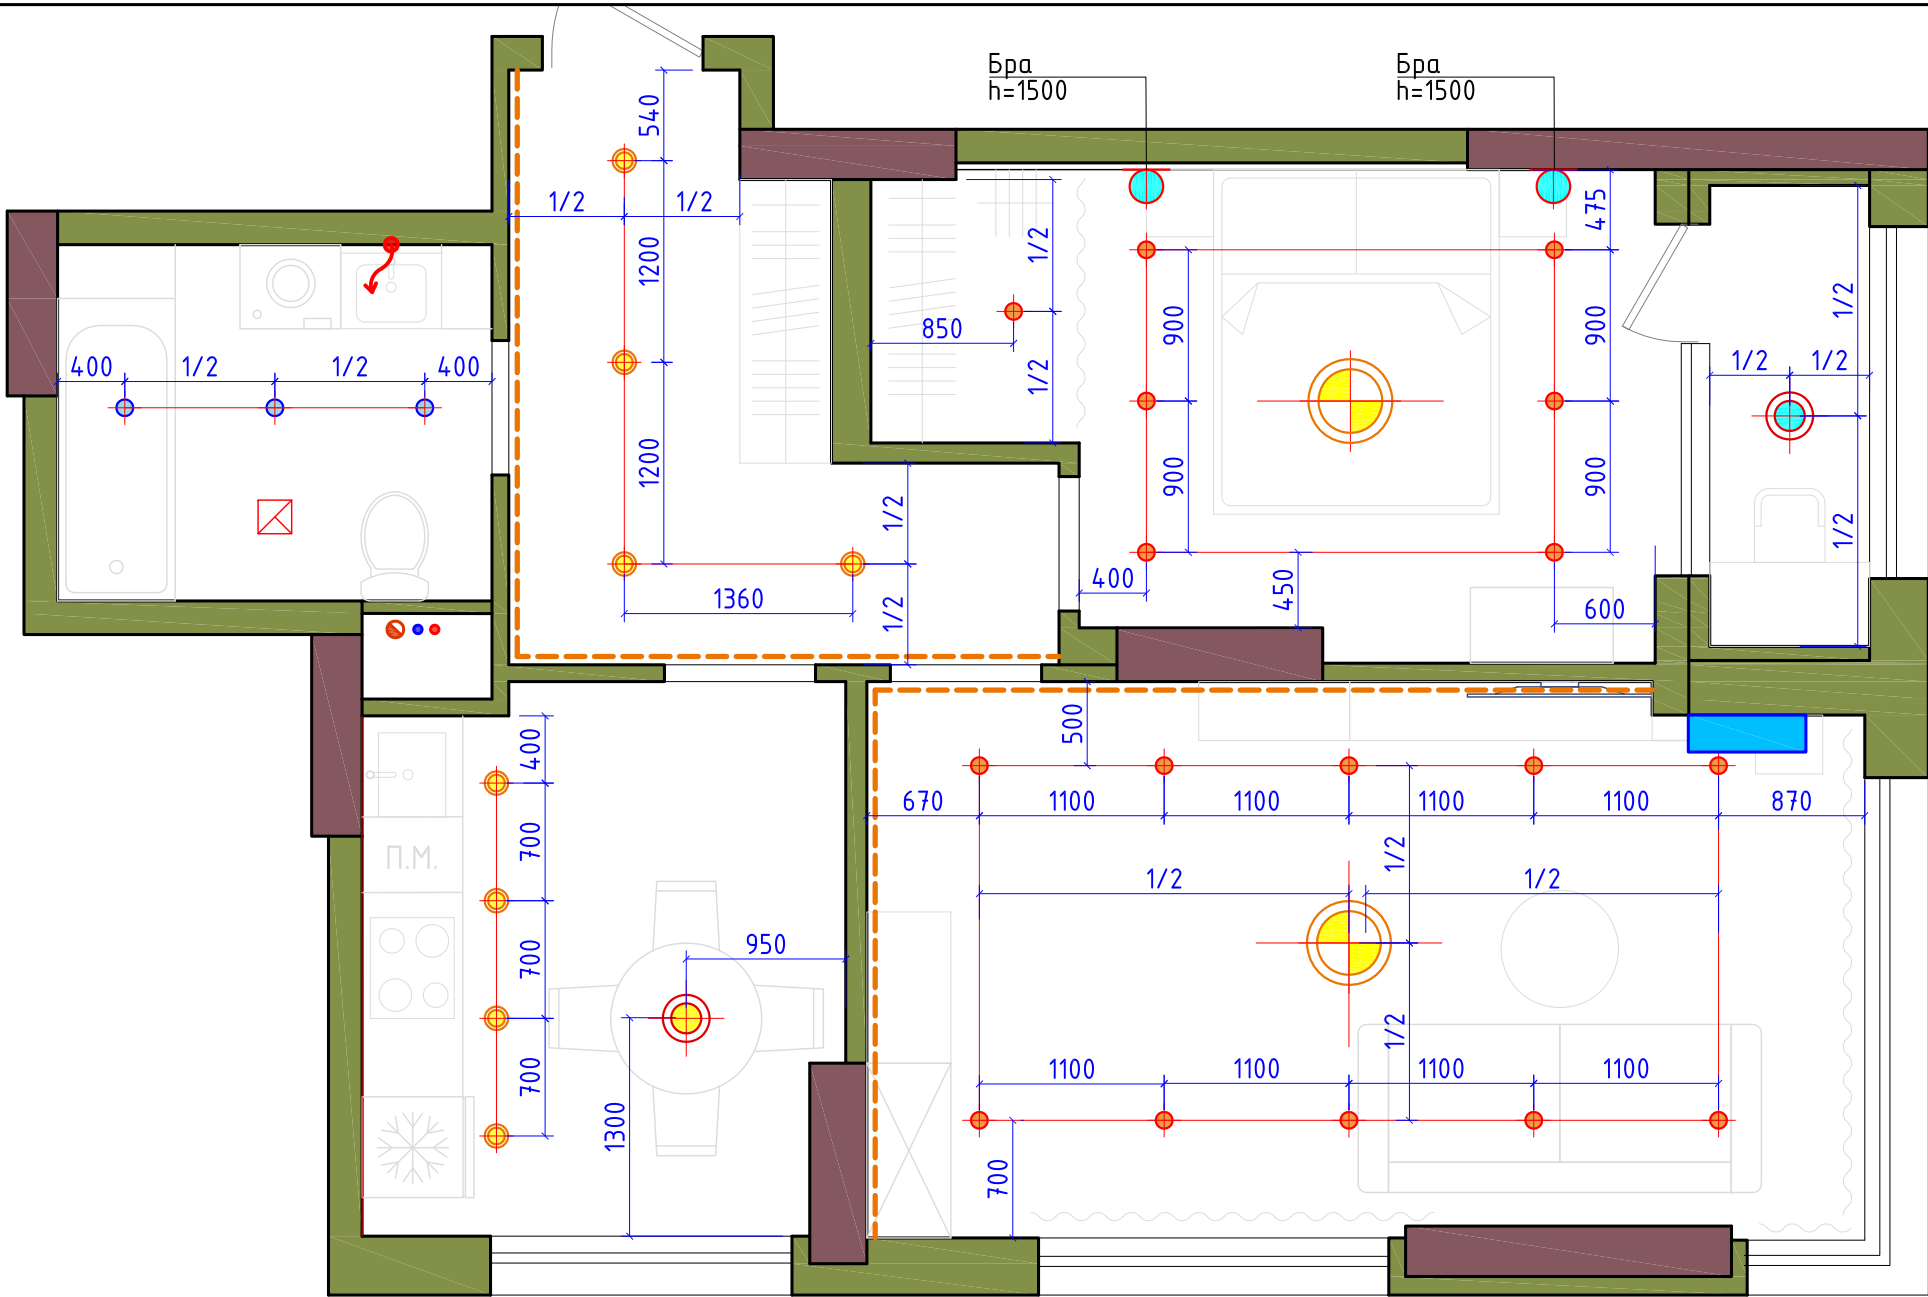


ПРИМЕЧАНИЕ:

- Смотреть совместно с листами развёрток и планом освещения
- Высоту потолка определить по месту, отметка уровня потолка может измениться в зависимости от конструкций существующего потолка и пола
- Конструктив потолка согласовать со строителями по месту
- Предусмотреть закладные или усиленный каркас в местах крепления светильников
- При монтаже конструкций потолка учесть расположение светильников
- Любые расхождения с проектом согласовать с дизайнером
- Все размеры указаны в миллиметрах и являются проектными. По факту могут отличаться в большую или меньшую сторону

Спецификация

Усл. обозн.	Наименование	Кол-во
	Точечный светильник тип 1	16
	Точечный светильник тип 2 (влагостойкий)	3
	Точечный светильник тип 3 (накладной)	8
	Бра	2
	Подвесной светильник	1
	Плафон круглый	1
	Люстра	1
	Светодиодная лента в теневом профиле	14,7 п.м.
	Вытяжной вентилятор	1
	Внутренний блок кондиционера	1

					Стадия	Лист	Листов
					РП		
Дизайнер	Джамбулатов А.			План привязки осветительных приборов			

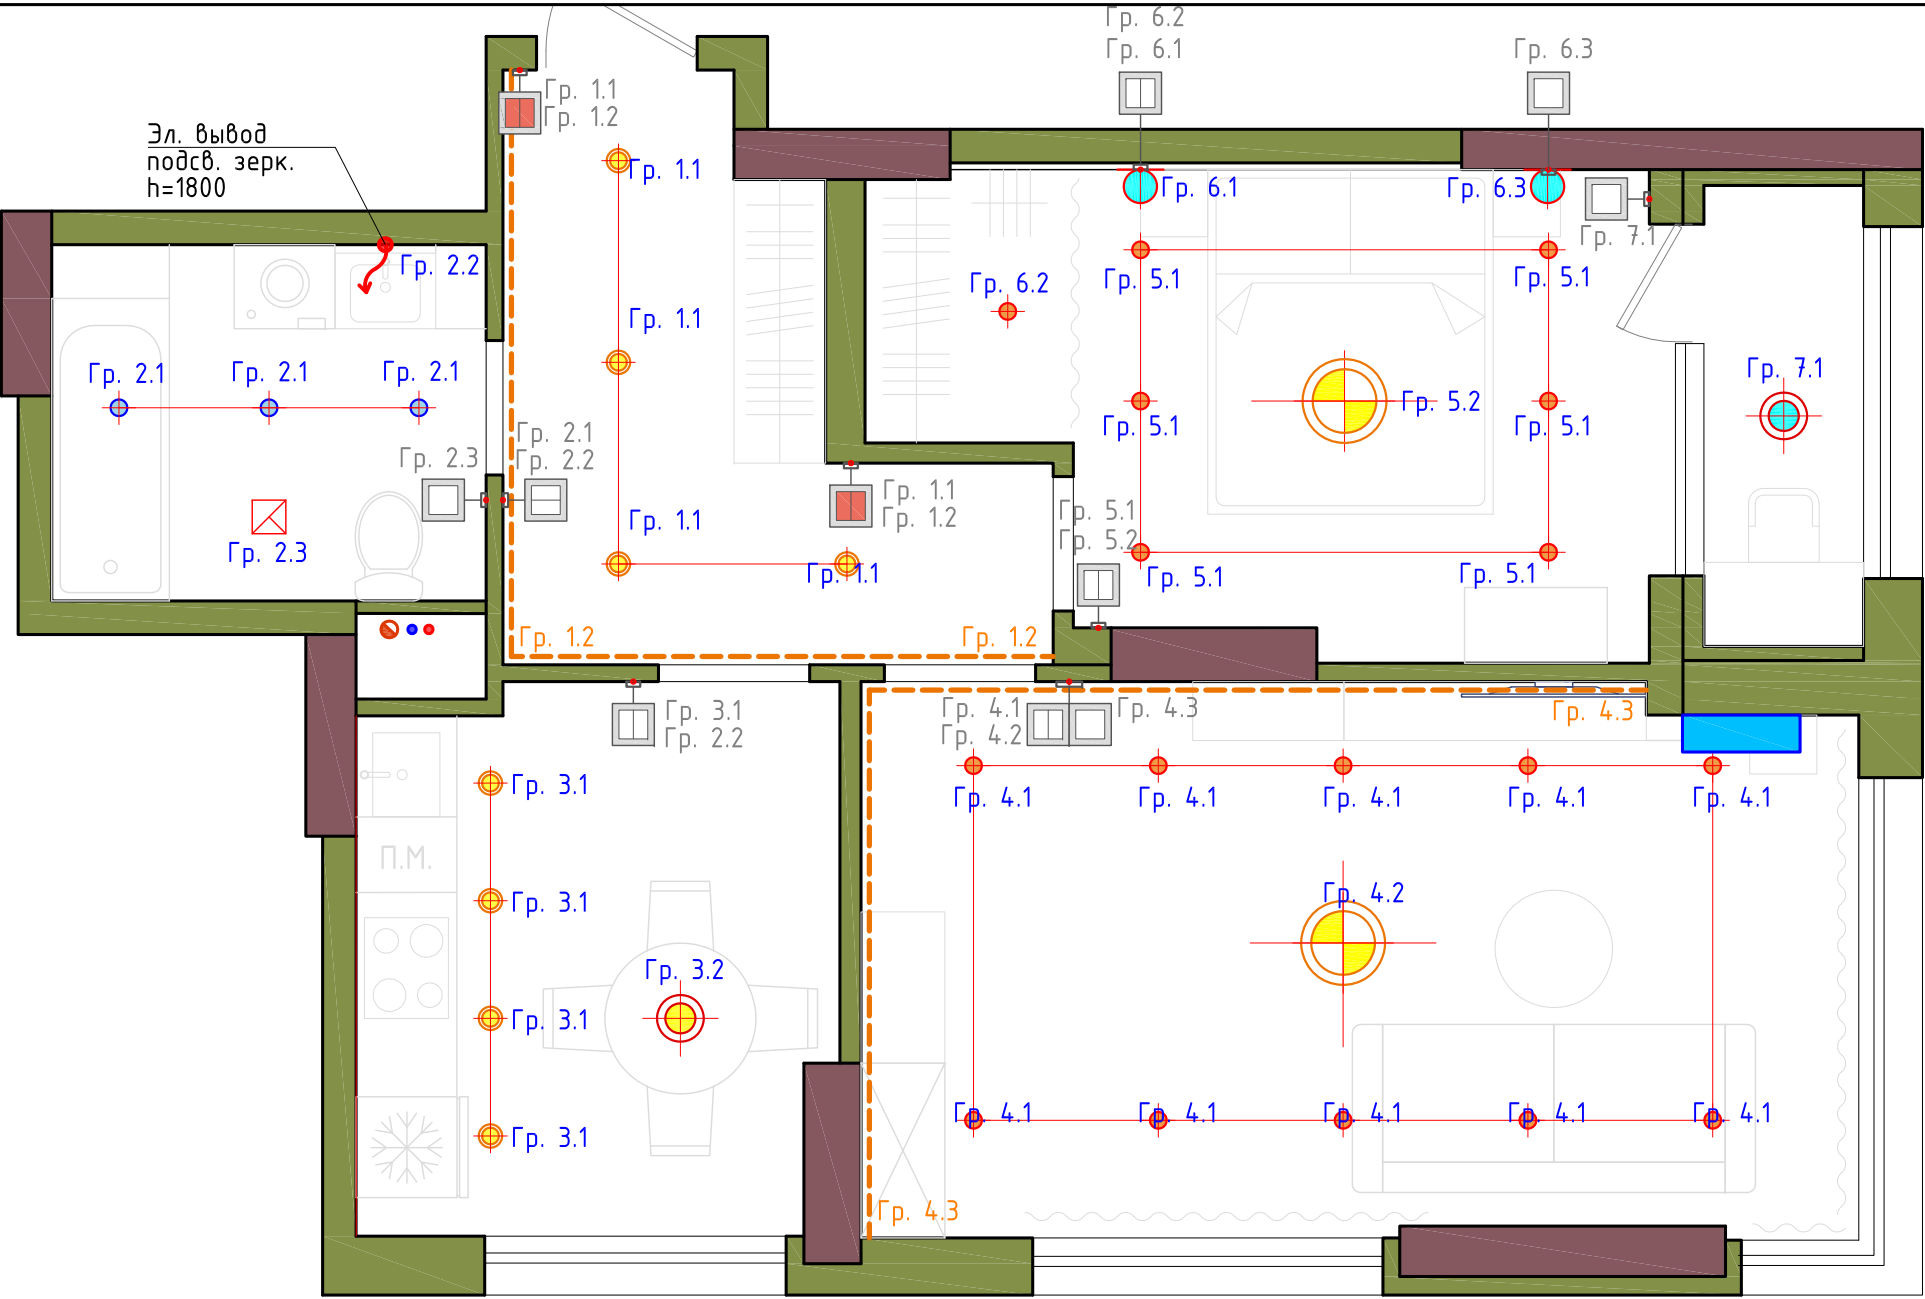


Усл. обозн.	Наименование
	Выключатель одноклавишный (IP 20)
	Выключатель двухклавишный (IP 20)
	Выключатель проходной двухклавишный (IP 20)
	Выключатель перекрестный одноклавишный (IP 20)

ПРИМЕЧАНИЕ:

- Смотреть совместно с развертками и планом потолка
- Предусмотреть закладные для светильников
- При замене светильников может измениться их расположение и количество
- Размещение трансформаторов для светодиодной ленты уточнить по месту.
- Уточнить количество светильников у поставщика перед покупкой
- Расстановка электрических выводов, выключателей и розеток в зоне кухонной мебели является предварительной и будет уточнена фабрикой изготовителем после утверждения Заказчиком модели кухни.
- Все электрические выводы (в том числе для люстр,подвесов и бра) сделать с запасом не менее 500 мм
- Любые расхождения с проектом согласовать с дизайнером
- Все размеры указаны в миллиметрах и являются проектными. По факту могут отличаться в большую или меньшую сторону

					Стадия	Лист	Листов
					РП		
Дизайнер	Джамбулатов А.			План управления освещением			

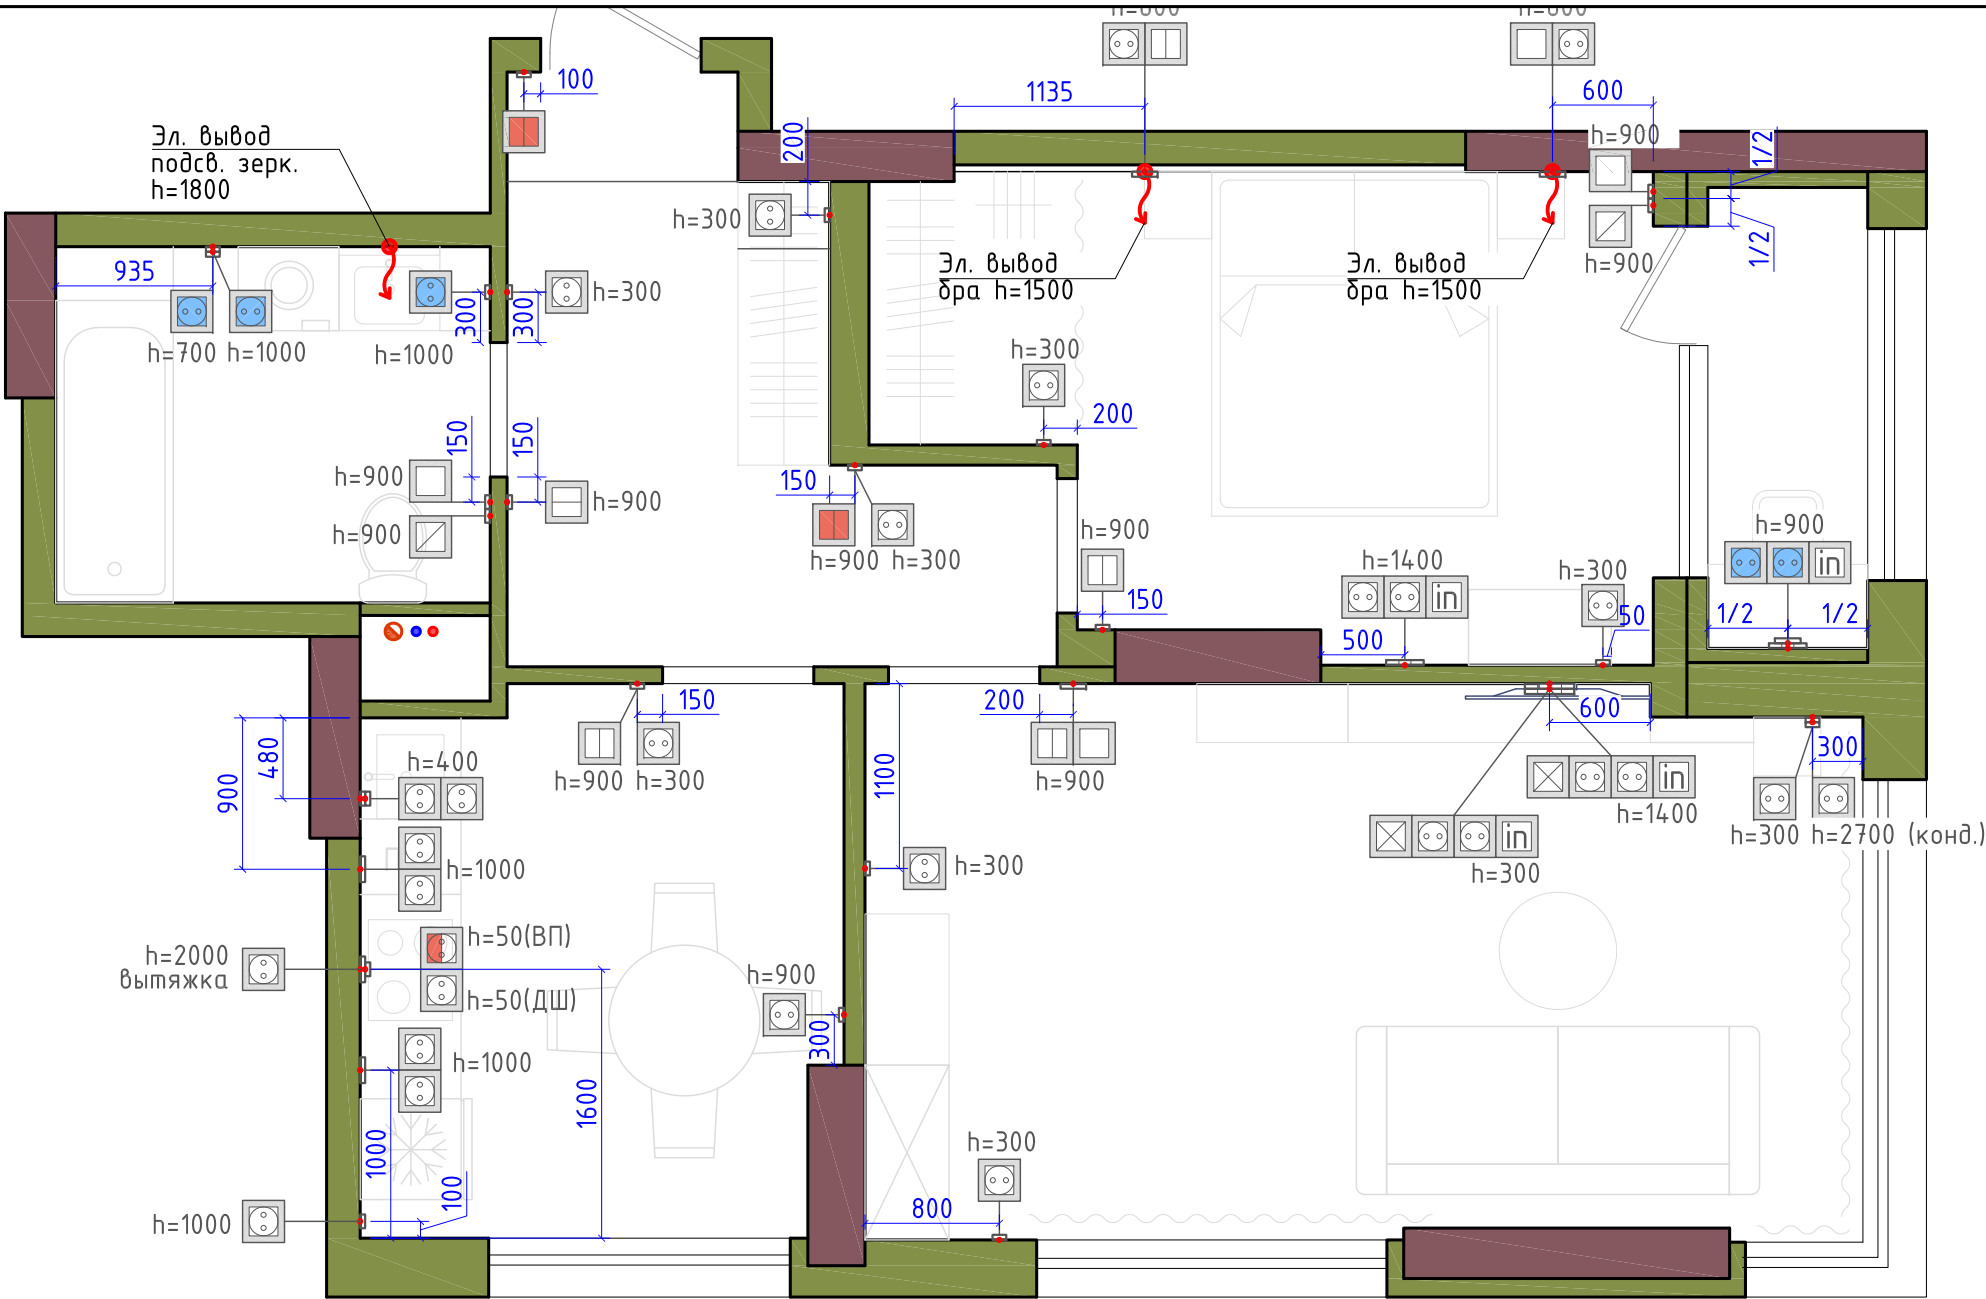


Спецификация электроприборов

Усл. обозн.	Наименование	Кол-во
	Выключатель одноклавишный (IP 20)	5
	Выключатель двухклавишный (IP 20)	4
	Выключатель проходной двухклавишный (IP 20)	2
	Выключатель проходной одноклавишный (IP 20)	-
	Розетка 220 В (IP 20)	29
	Розетка влагозащищенная 220 В (IP 44)	5
	Розетка силовая (IP 20)	1
	Фальшрозетка (кабельканал)	2
	Сетевая розетка (интернет)	4
	Терморегулятор	2
	Вывод кабеля с электропитанием	3
	Мастер выключатель	-

ПРИМЕЧАНИЕ:

- Высоту расположения эл.розетки уточнить после подбора модели вытяжки.
- Смотреть совместно с развертками
- Расположение розеток на кухне уточнить с поставщиком кухни
- Все электрические выводы (в том числе для люстр,подвесов и бра сделать с запасом не менее 500 мм
- Расположение трансформаторов подсветок уточнить с прорабом на авторском надзоре
- Расстановка электрических выводов, выключателей и розеток в зоне кухонной мебели является предварительной и будет уточнена фабрикой изготовителем после утверждения Заказчиком модели кухни.
- Любые расхождения с проектом согласовать с дизайнером
- Все размеры указаны в миллиметрах и являются проектными. По факту могут отличаться в большую или меньшую сторону

					Стадия	Лист	Листов
					РП		
Дизайнер	Джамбулатов А.			План электрооборудования			

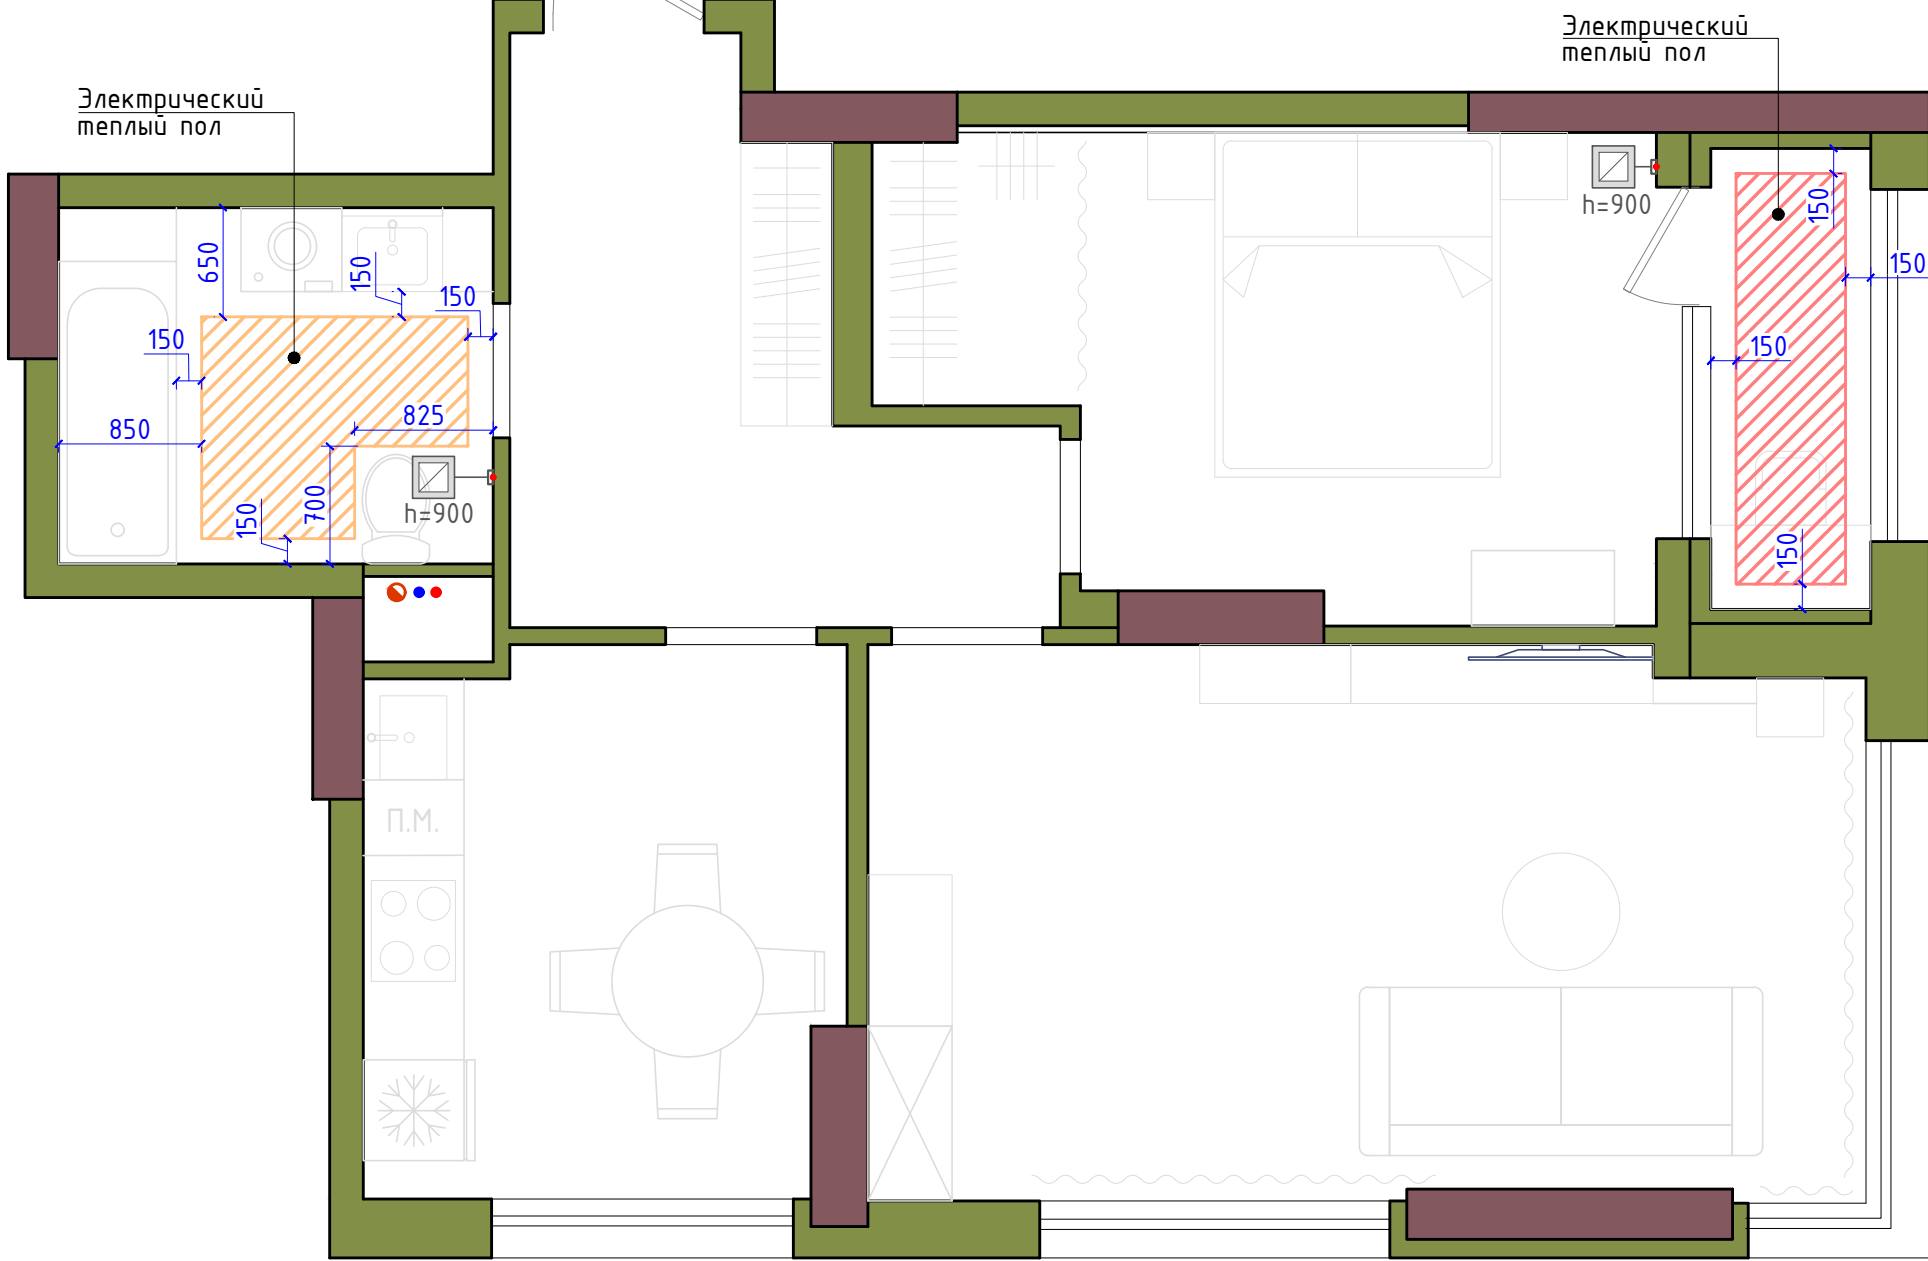

Спецификация терморегуляторов

Усл. обозн.	Наименование	Кол-во
	Терморегулятор (теплый пол)	2


Спецификация теплых полов

Усл. обозн.	Наименование	Площадь, м2
	Теплый пол (санузел)	1,7
	Теплый пол (лоджия)	1,6

ПРИМЕЧАНИЕ:

- Размеры даны от уровня чистового пола
- Любые расхождения с проектом согласовать с дизайнером
- Все размеры указаны в миллиметрах и являются проектными. По факту могут отличаться в большую или меньшую сторону
- Подключение всех приборов с ссылками на тех.карты поставщика уточнить дополнительно перед монтажом коммуникаций

					Стадия	Лист	Листов
					РП	15	
Дизайнер	Джамбулатов А.			План теплого пола			

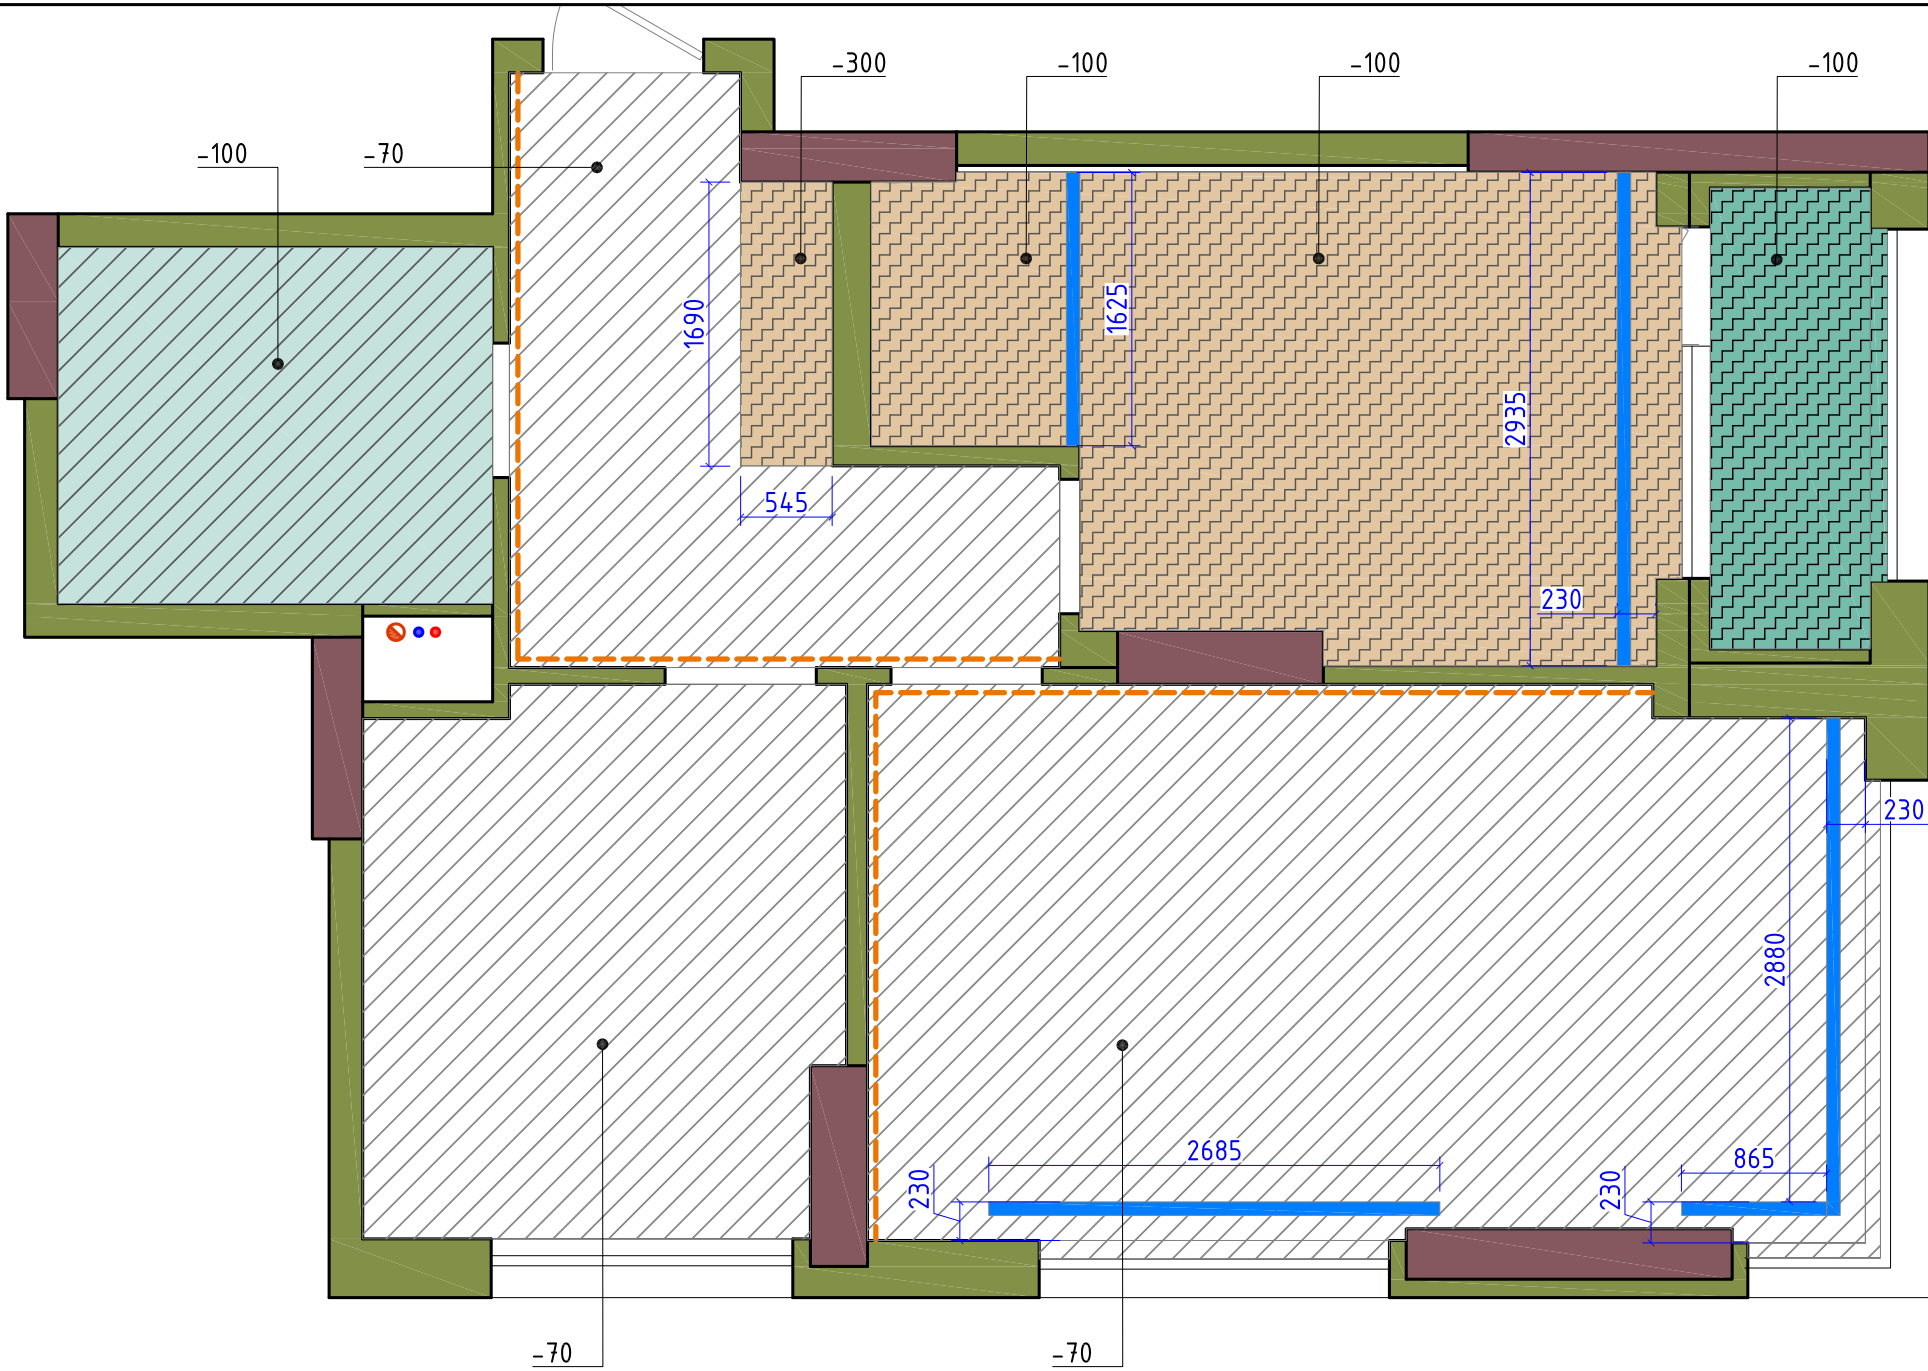

Спецификация отделки потолков

Усл. обозн.	Тип	Площадь, м2	Опуск
	- Натяжной потолок	36,0	-70
	- ГКЛ 12,5 мм	13,0	-100, -300
	- ГКЛВ 12,5 мм	2,8	-100
	- Натяжной потолок	5,5	-100

Спецификация потолочных элементов

Усл. обозн.	Тип	п. м.
	- Встроенный профиль для штор	10,1
	- Теневой зазор с LED подсветкой	13,5
	- Теневой профиль	-

ПРИМЕЧАНИЕ:

- Смотреть совместно с листами развёрток и планом освещения
- Высоту потолка определить по месту, отметка уровня потолка может измениться в зависимости от конструкций существующего потолка и пола
- Конструктив потолка согласовать со строителями по месту
- Предусмотреть закладные или усиленный каркас в местах крепления светильников
- При монтаже конструкций потолка учесть расположение светильников
- Любые расхождения с проектом согласовать с дизайнером
- Все размеры указаны в миллиметрах и являются проектными. По факту могут отличаться в большую или меньшую сторону

					Стадия	Лист	Листов
					РП	8	
Дизайнер	Джамбулатов А.			План отделки потолка			