

Рабочий проект

Заказчик _____ Тапалов Аян

Дизайнер _____ Ермаганбетова Жадыра

_____ 8700481-70-97

2026

	* Ведомость рабочих чертежей основного комплекта		
	Лист	Наименование	Примечание
	1	Лист общих данных	
	2	Обмерный план	
	3	План демонтажа	
	4	План монтажа	
	5	Кладочный план после перепланировки	
	6	План сантехнического оборудования	
	7	Планировочное решение	
	8	План полов	
	8-1	План Теплых полов	
	9	План открывание дверей	
	10	План освещения-Схема освещения	
	11	План электрики	
YERMAGANBETOVA_ZH РАБОЧИЙ ПРОЕКТ		Лист 1	

Обмерный план


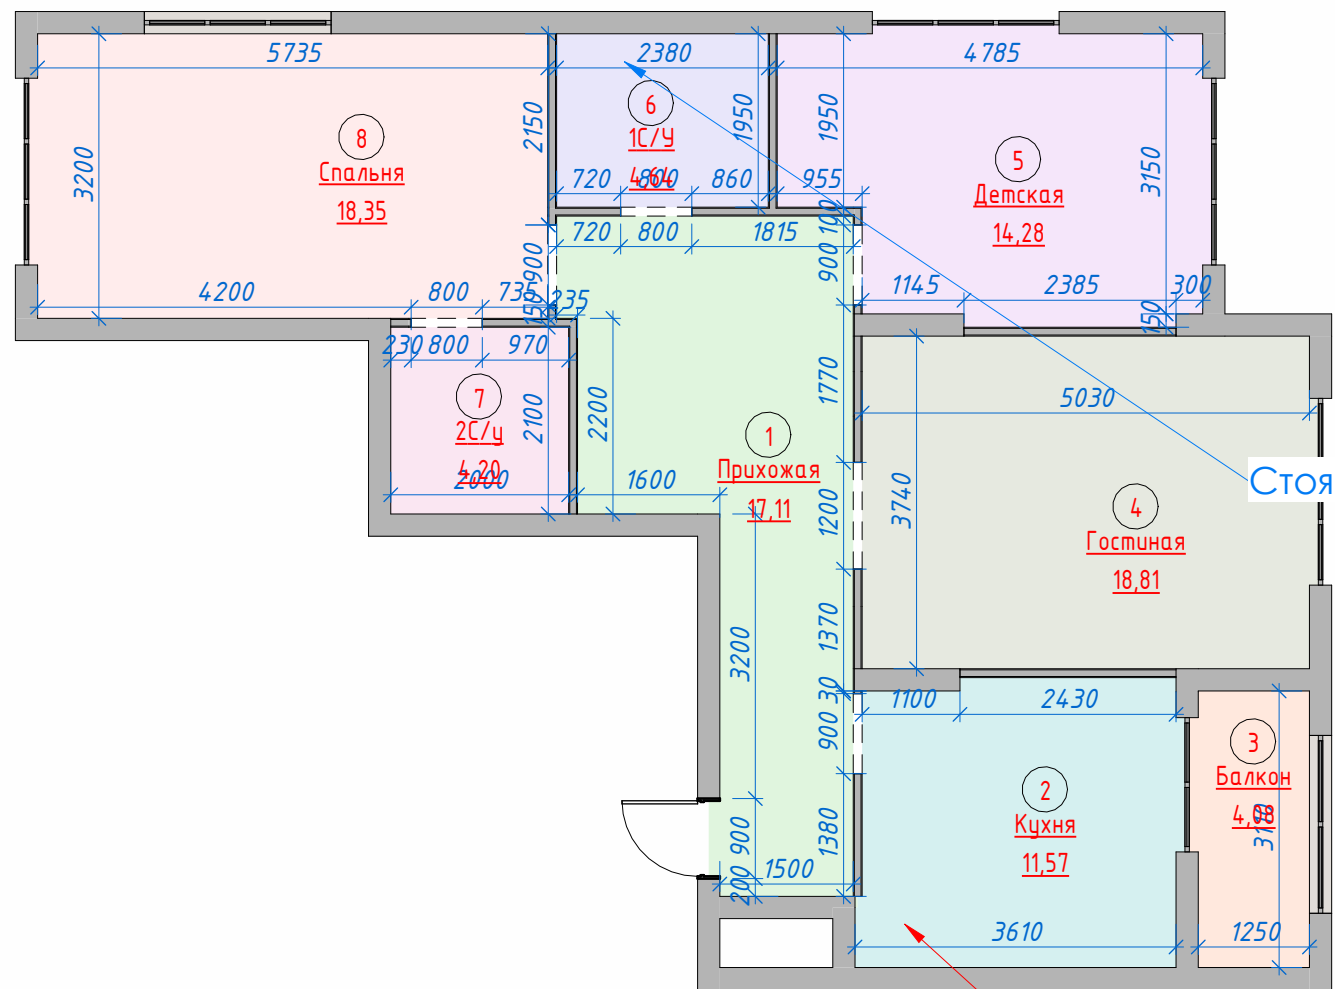


Схема 3 Д -Обмер

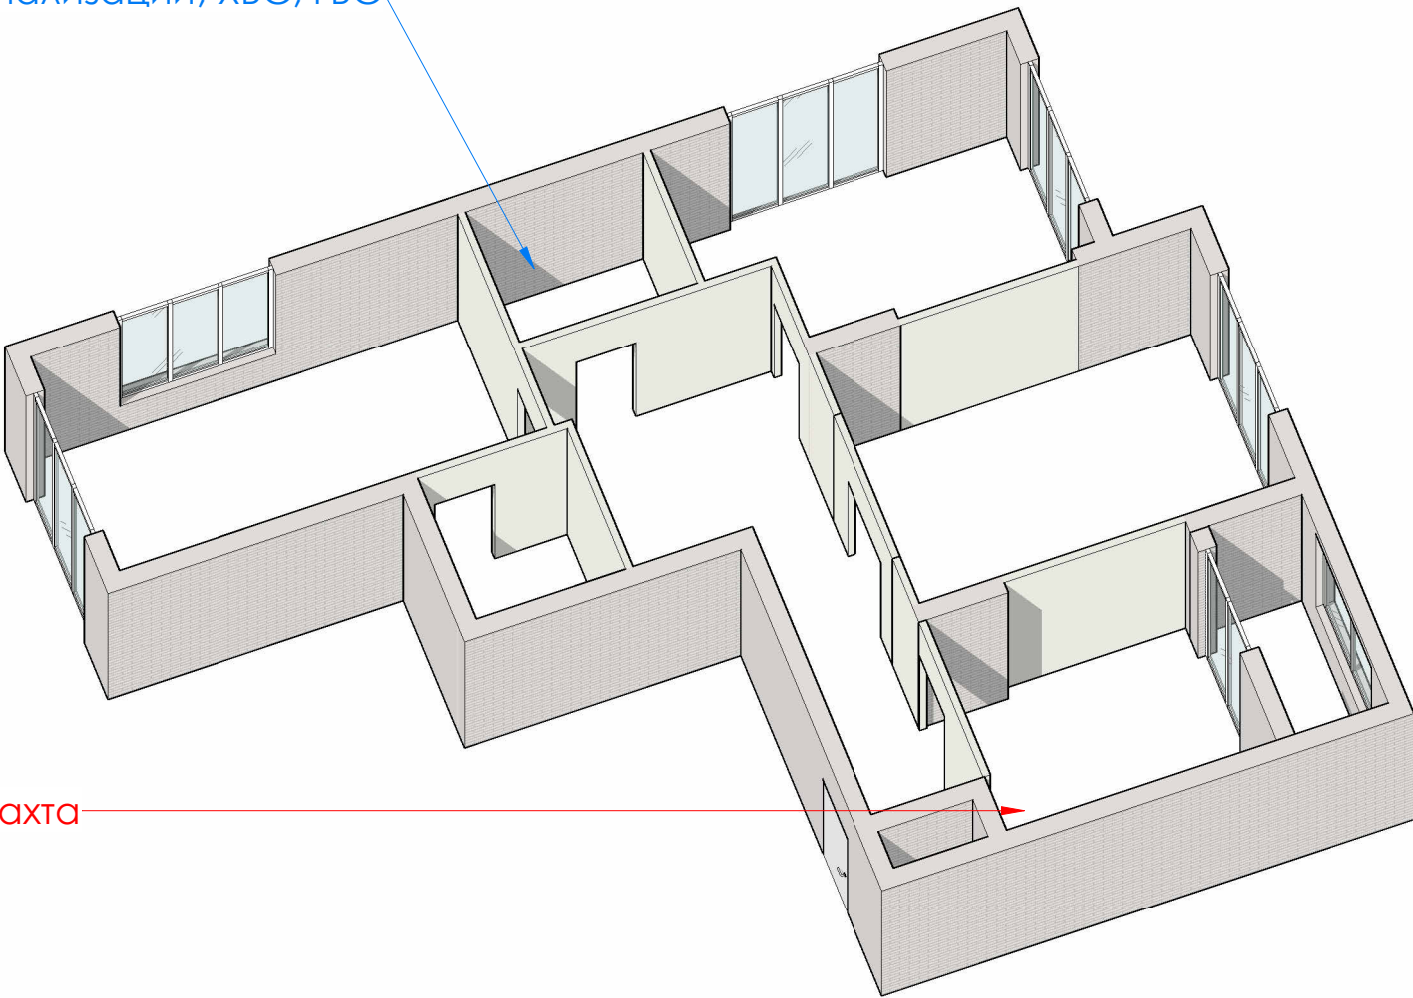

* Экспликация помещений (Обмерный план)			
№ пом	Наименование	Площадь, м²	Кат. помещения
1	Прихожая	17,11 м²	
2	Кухня	11,57 м²	
3	Балкон	4,08 м²	
4	Гостиная	18,81 м²	
5	Детская	14,28 м²	
6	1С/У	4,64 м²	
7	2С/У	4,20 м²	
8	Спальня	18,35 м²	

Общий итог: 8 93,04 м²

Вентшахта

Примечание:
1. Комплект рабочих чертежей разработан на основе обмеров. Все размеры даны без учёта выравнивания стен, пола, потолка
2. Все размеры указаны в миллиметрах
3. Перед началом работ все размеры проверить по месту
4. Высота Потолка Н = 3000 мм.
5. Высота Проёма двери Н = 2200 мм.


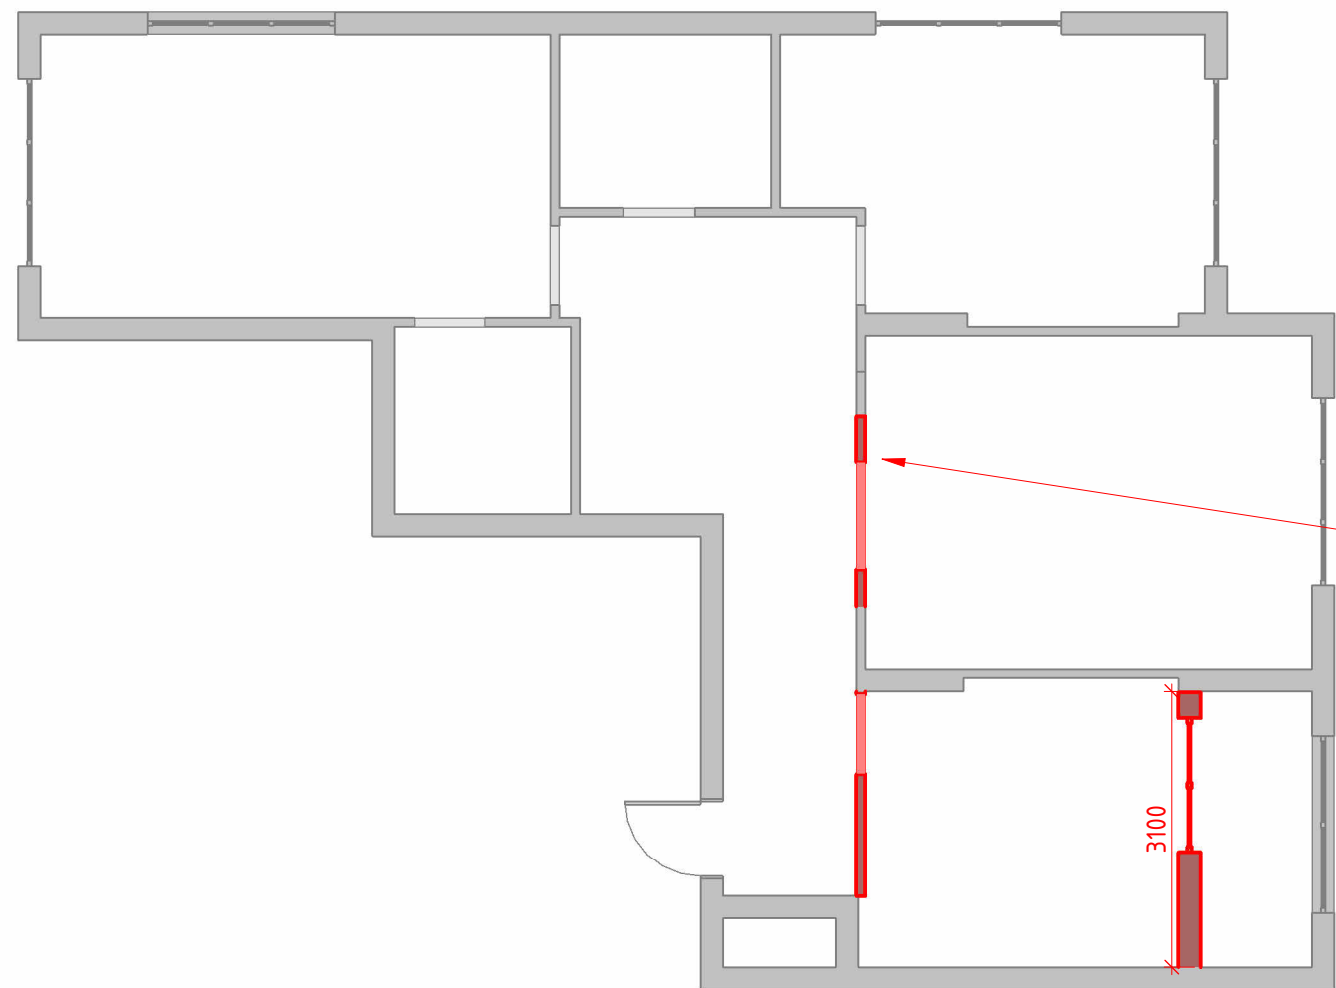


Схема 3 Д - Демонтаж

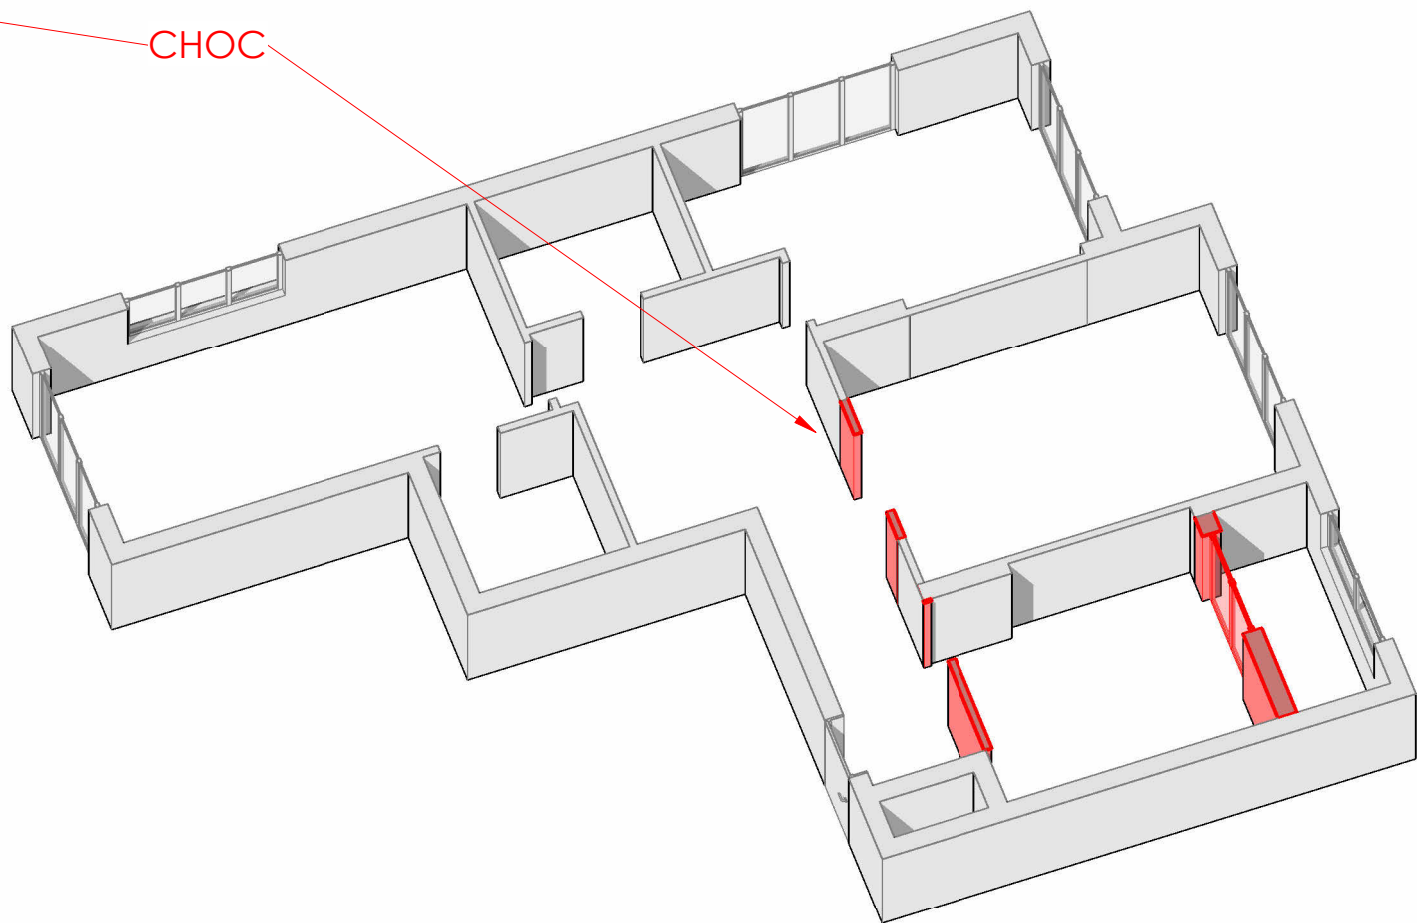

Примечание:
1. Комплект рабочих чертежей разработан на основе обмеров.
2. Все размеры указаны в миллиметрах
3. Перед началом работ все размеры проверить по месту
4. Высота Потолка Н = 3000 мм.
5. Высота Проема двери Н = 2200 мм.

План монтажа



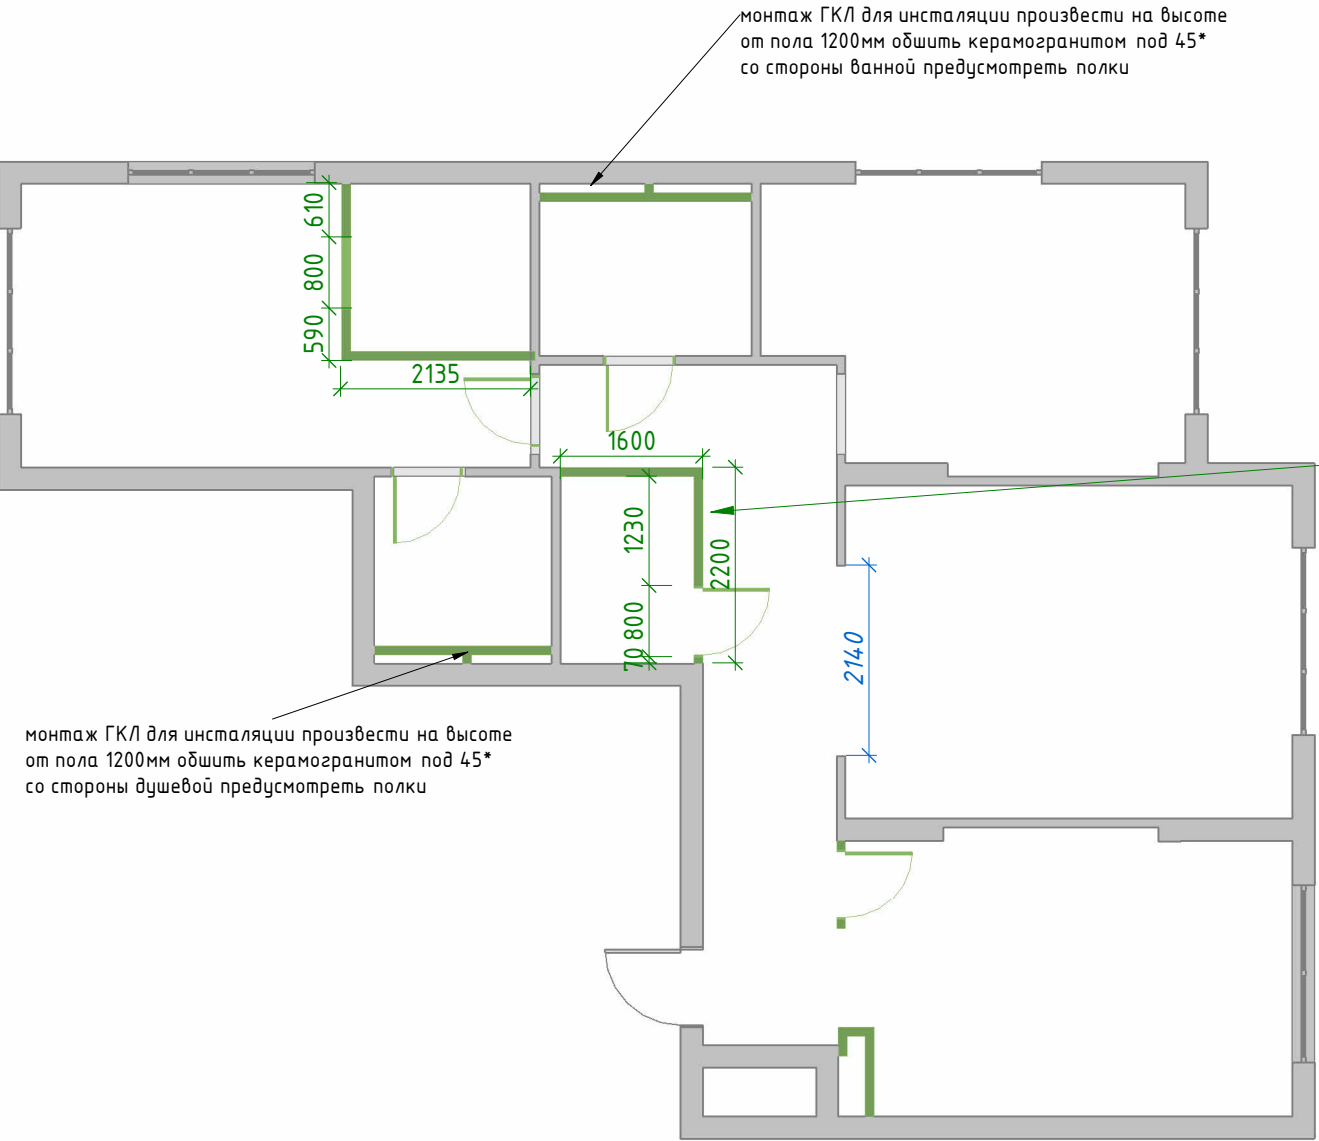


Схема 3 Д -Монтаж

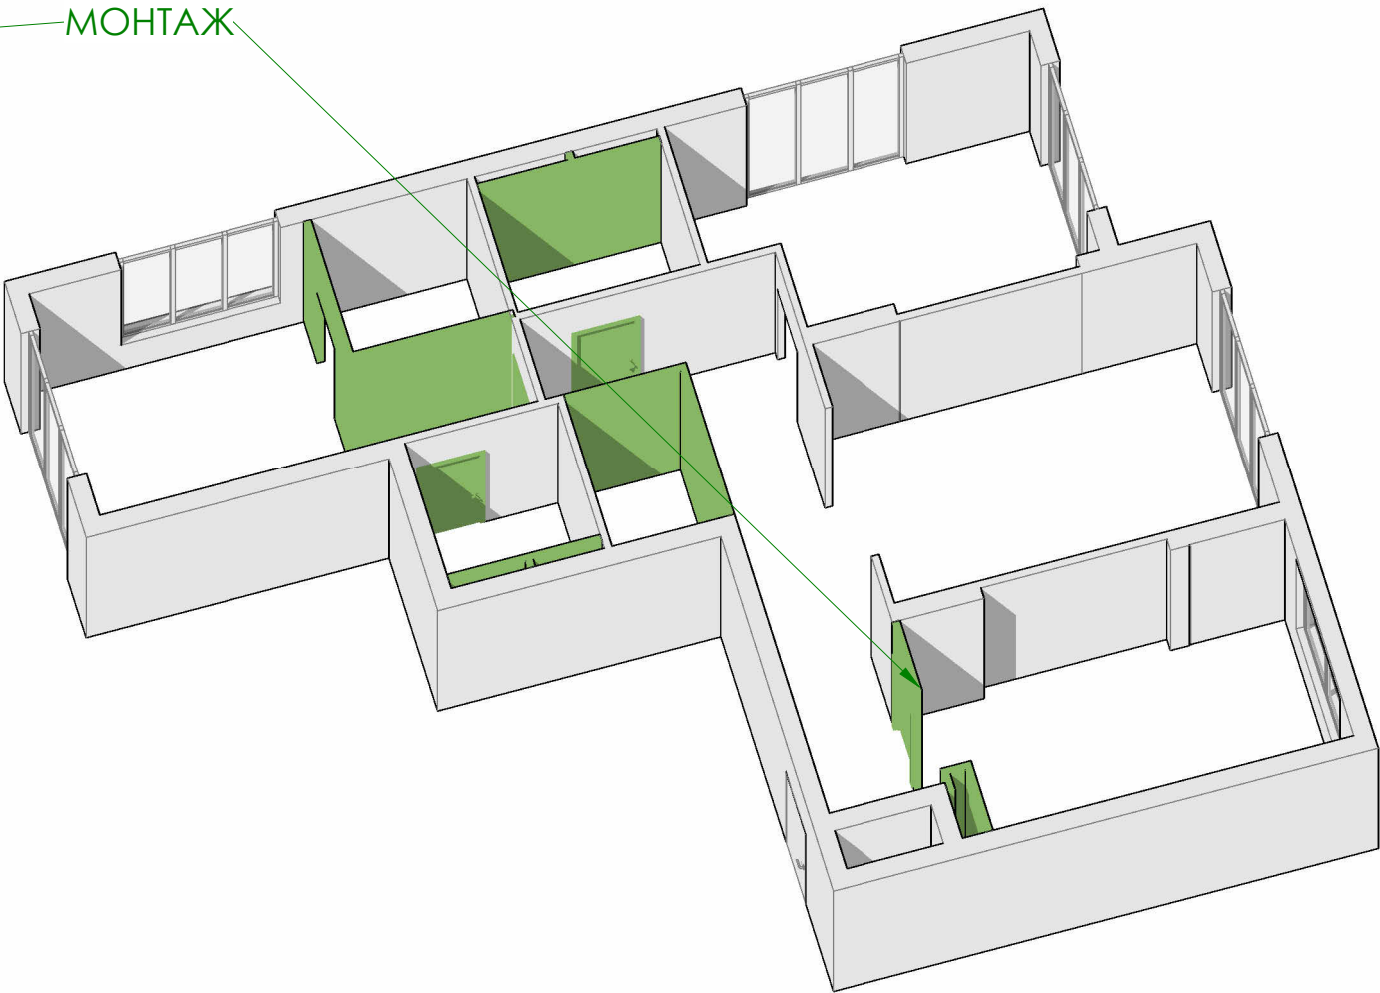


- Примечание:
- 1. Комплект рабочих чертежей разработан на основе обмеров.
 - 2. Все размеры указаны в миллиметрах
 - 3. Перед началом работ все размеры проверить по месту
 - 4. Высота Потолка H = 3000 мм.
 - 5. Высота Проема двери H = 2200 мм.

Кладочный план после перепланировки

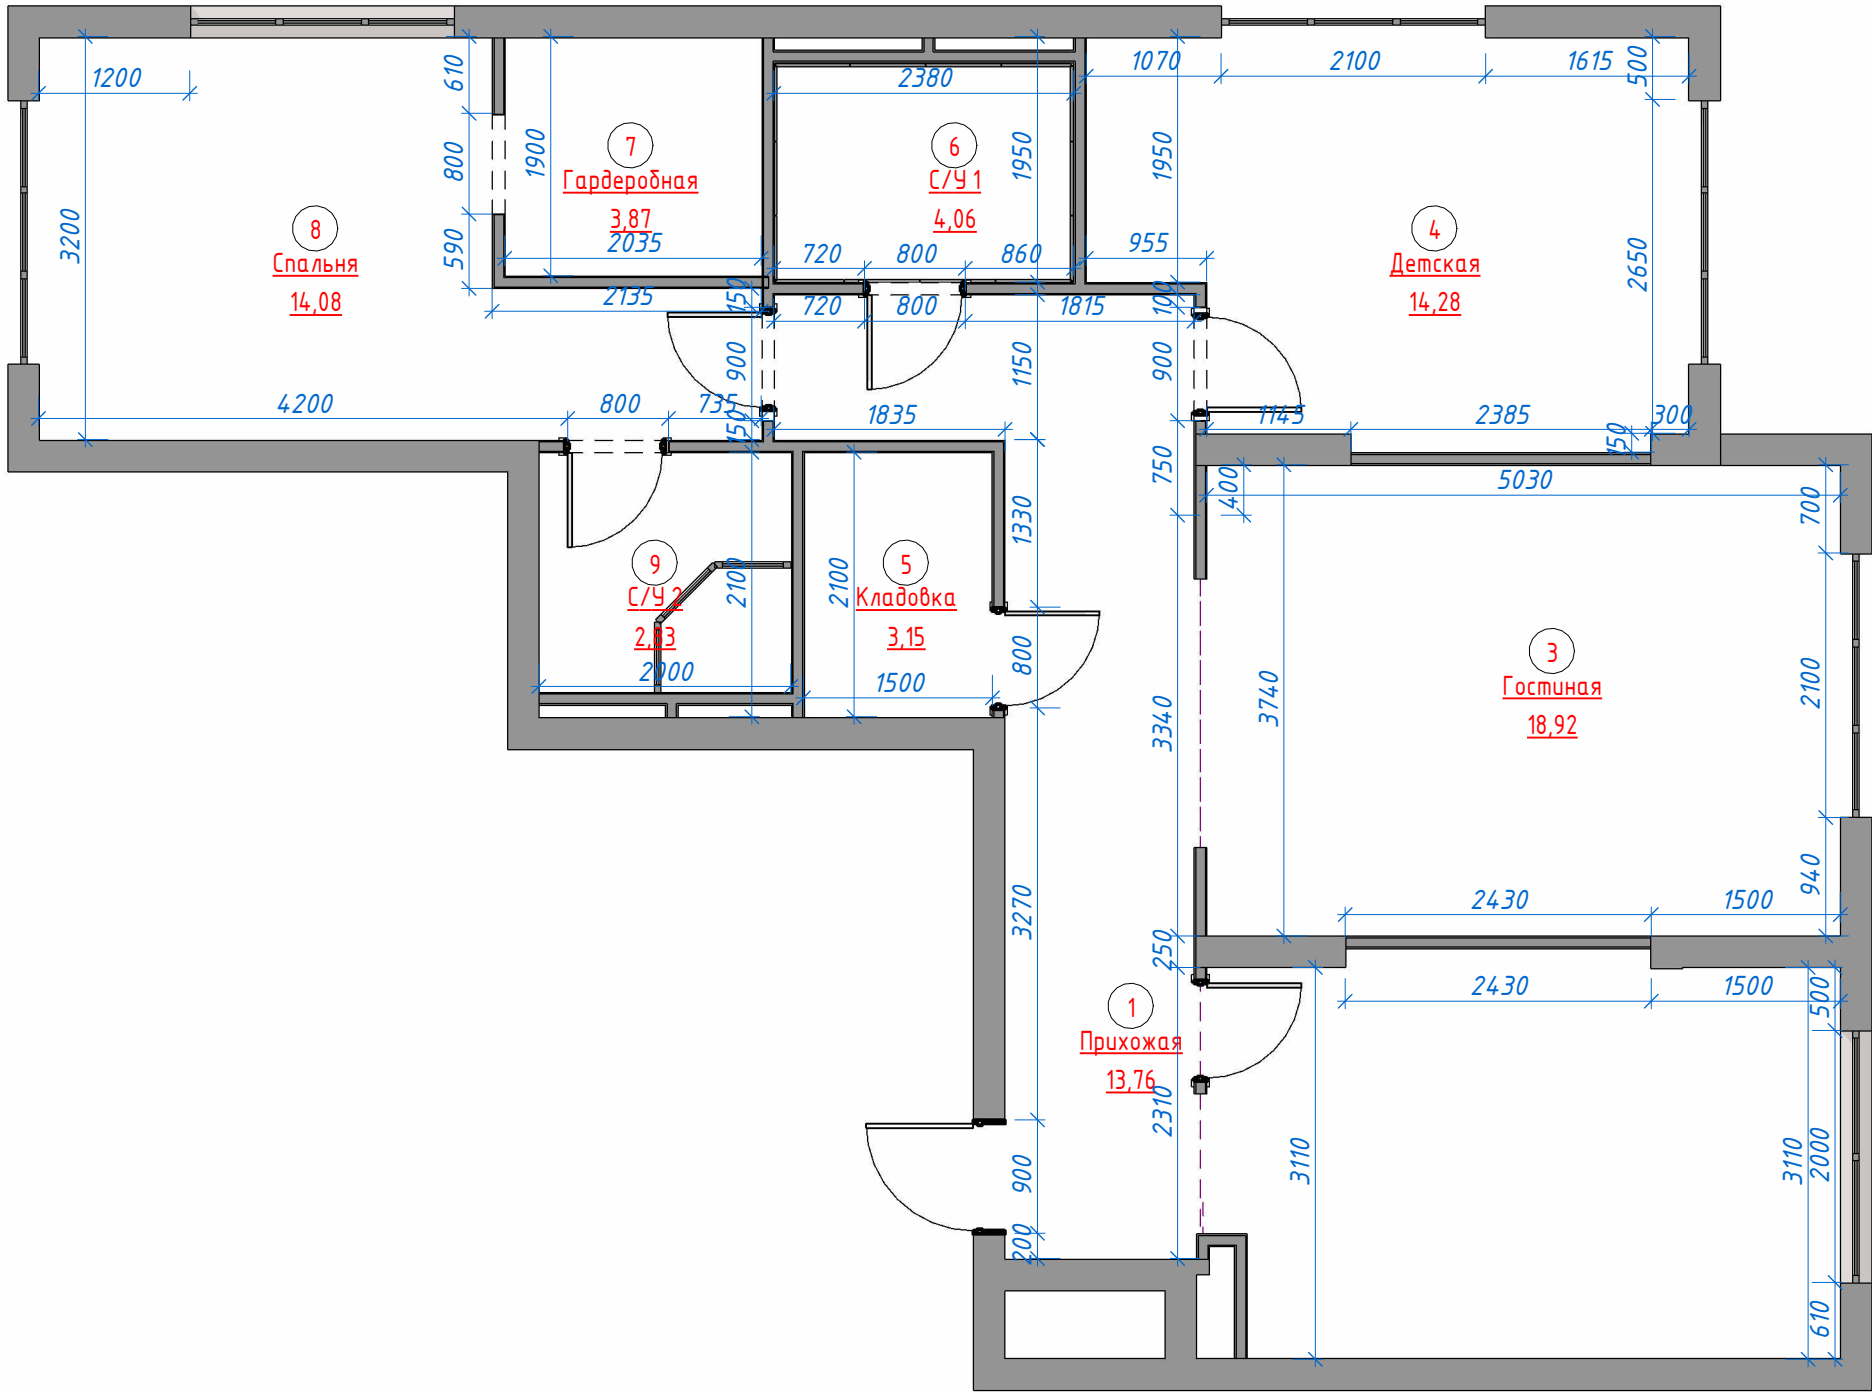


* Экспликация помещений...		
№ пом	Наименование	Площадь, м²
1	Прихожая	13,76 м²
3	Гостиная	18,92 м²
4	Детская	14,28 м²
5	Кладовка	3,15 м²
6	С/У 1	4,06 м²
7	Гардеробная	3,87 м²
8	Спальня	14,08 м²
9	С/У 2	2,83 м²
Общий итог: 8		74,94 м²

План сантехнических приборов
1 : 50

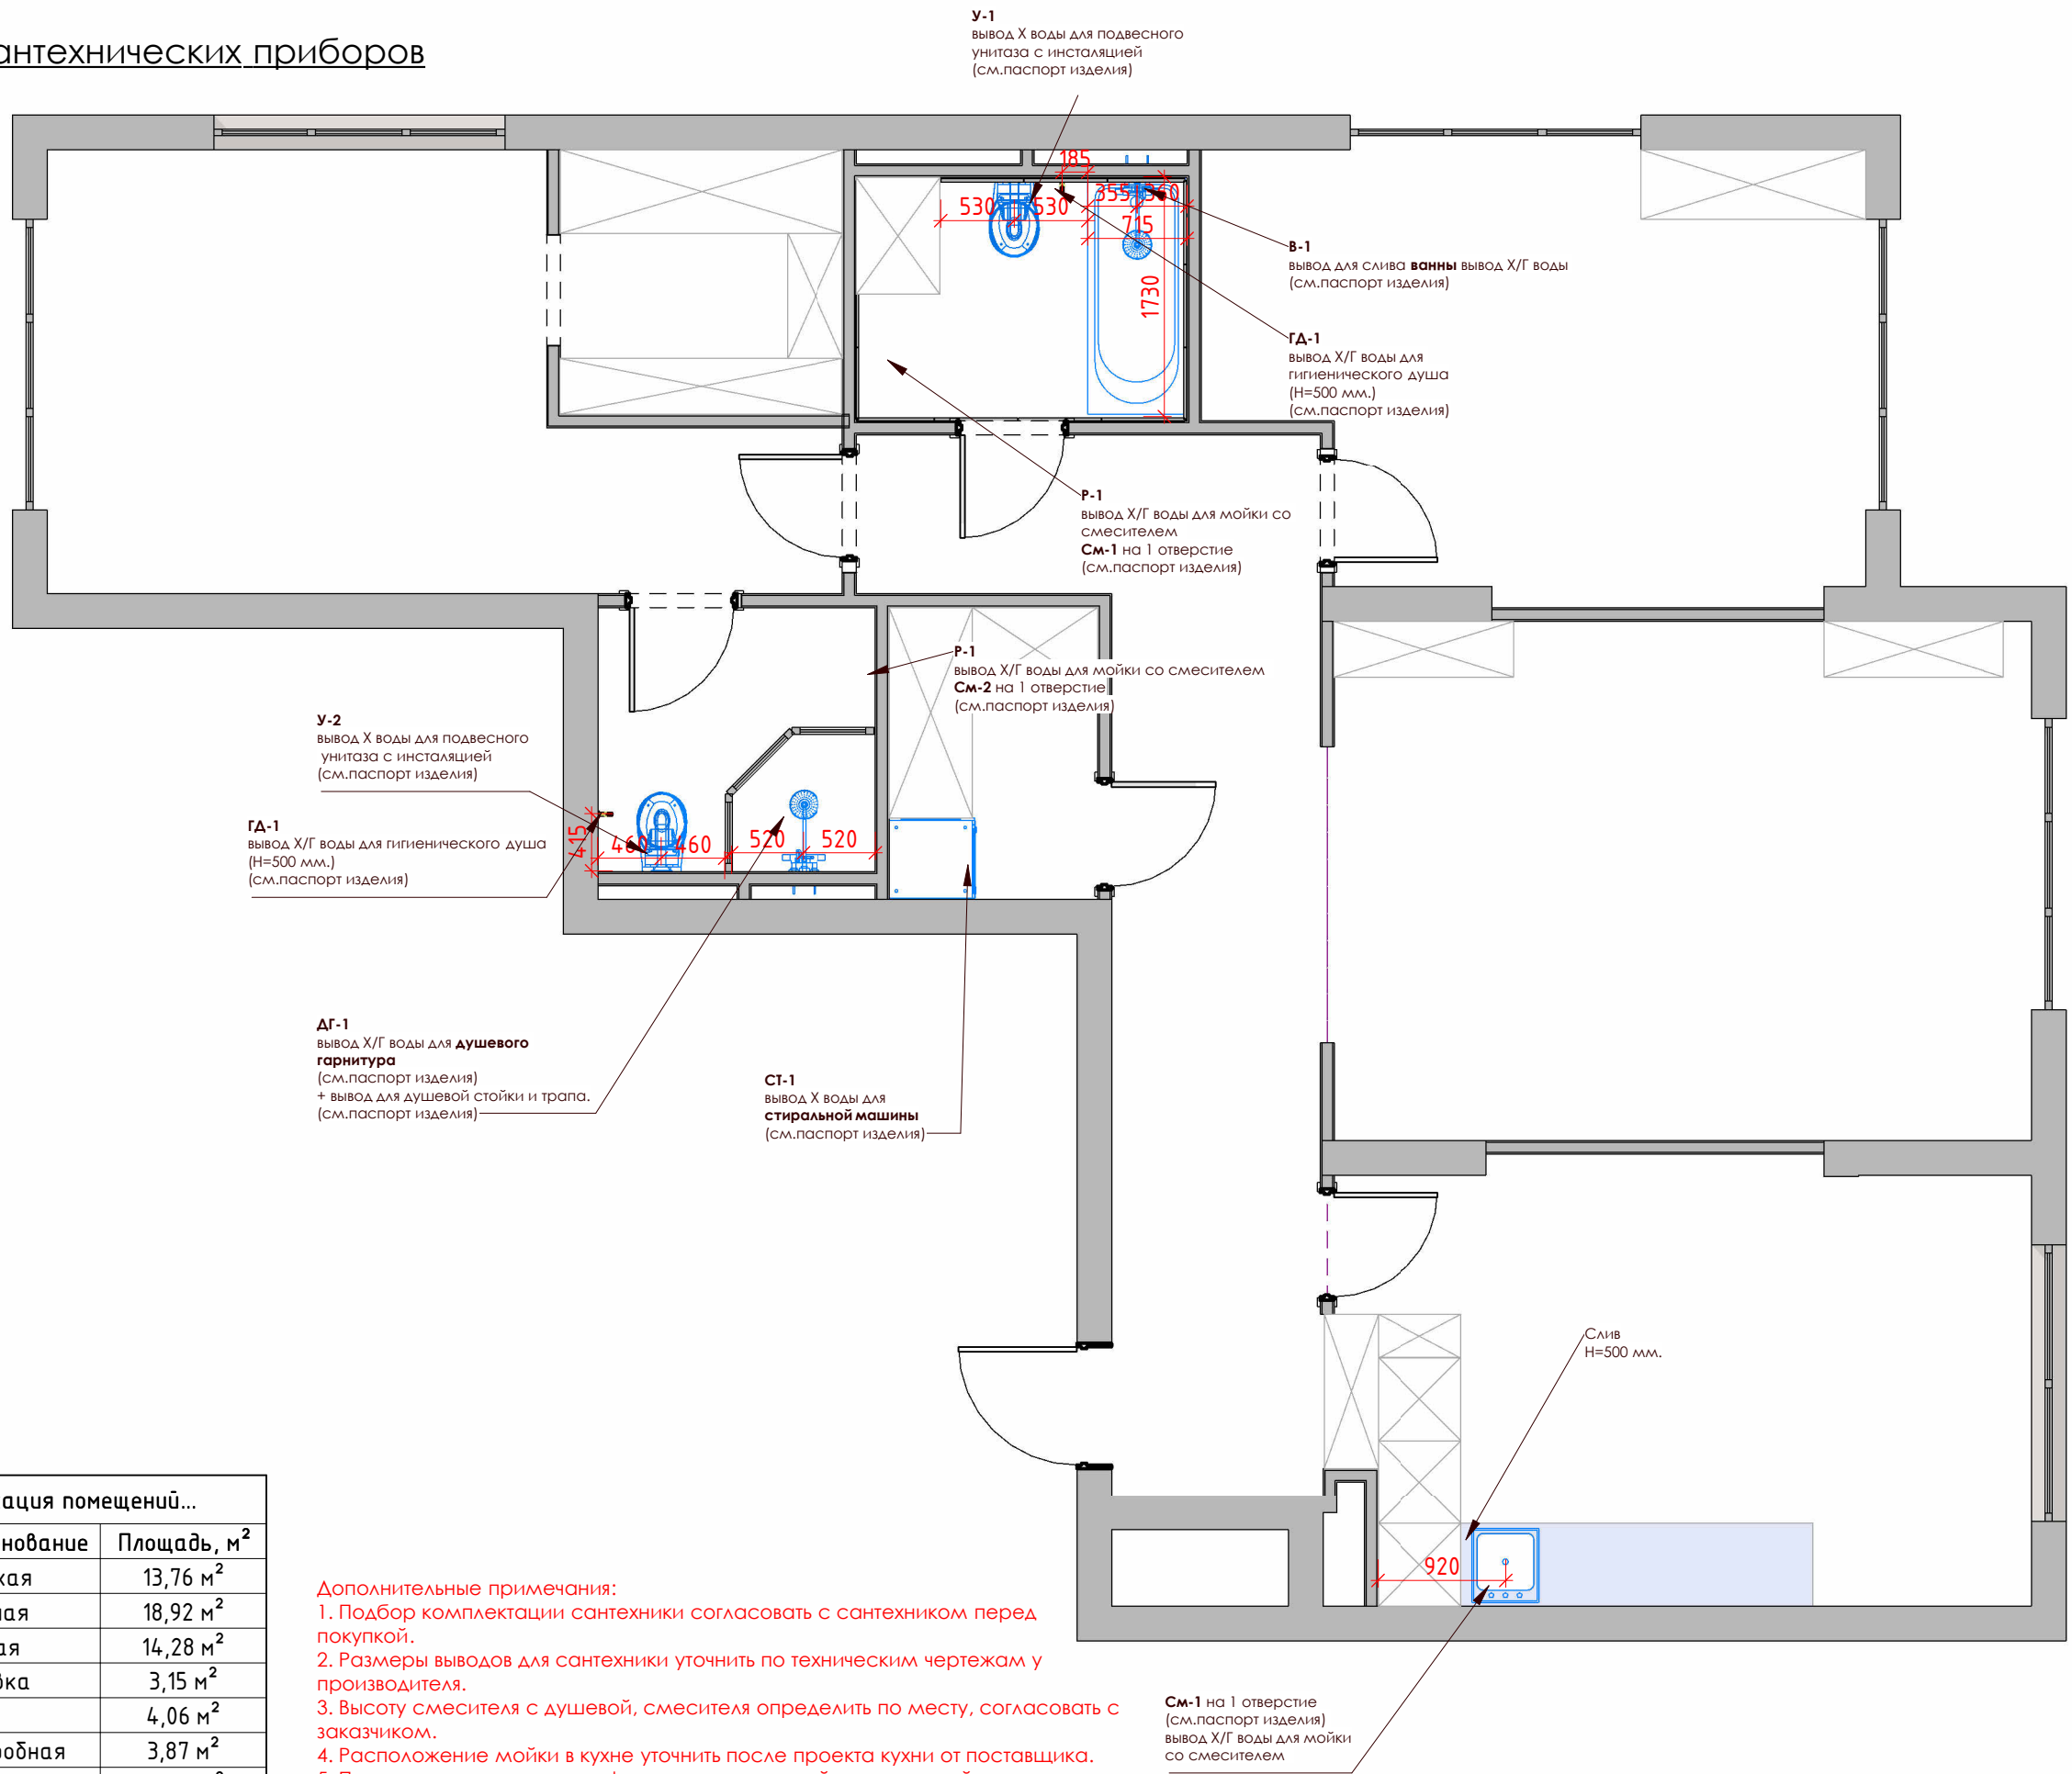

* Экспликация помещений...		
№ пом	Наименование	Площадь, м ²
1	Прихожая	13,76 м ²
3	Гостиная	18,92 м ²
4	Детская	14,28 м ²
5	Кладовка	3,15 м ²
6	С/У 1	4,06 м ²
7	Гардеробная	3,87 м ²
8	Спальня	14,08 м ²
9	С/У 2	2,83 м ²
Общий итог: 8		74,94 м ²

- Дополнительные примечания:
- Подбор комплектации сантехники согласовать с сантехником перед покупкой.
 - Размеры выводов для сантехники уточнить по техническим чертежам у производителя.
 - Высоту смесителя с душевой, смесителя определить по месту, согласовать с заказчиком.
 - Расположение мойки в кухне уточнить после проекта кухни от поставщика.
 - Предусмотреть установку фильтров для питьевой воды и тонкой очистки воды.
1. Комплект рабочих чертежей разработан на основе обмеров.
2. Все размеры указаны в миллиметрах
3. Перед началом работ все размеры проверить по месту
4. Высота Потолка Н = 3000 мм.
5. Высота Проема двери Н = 2100 мм.

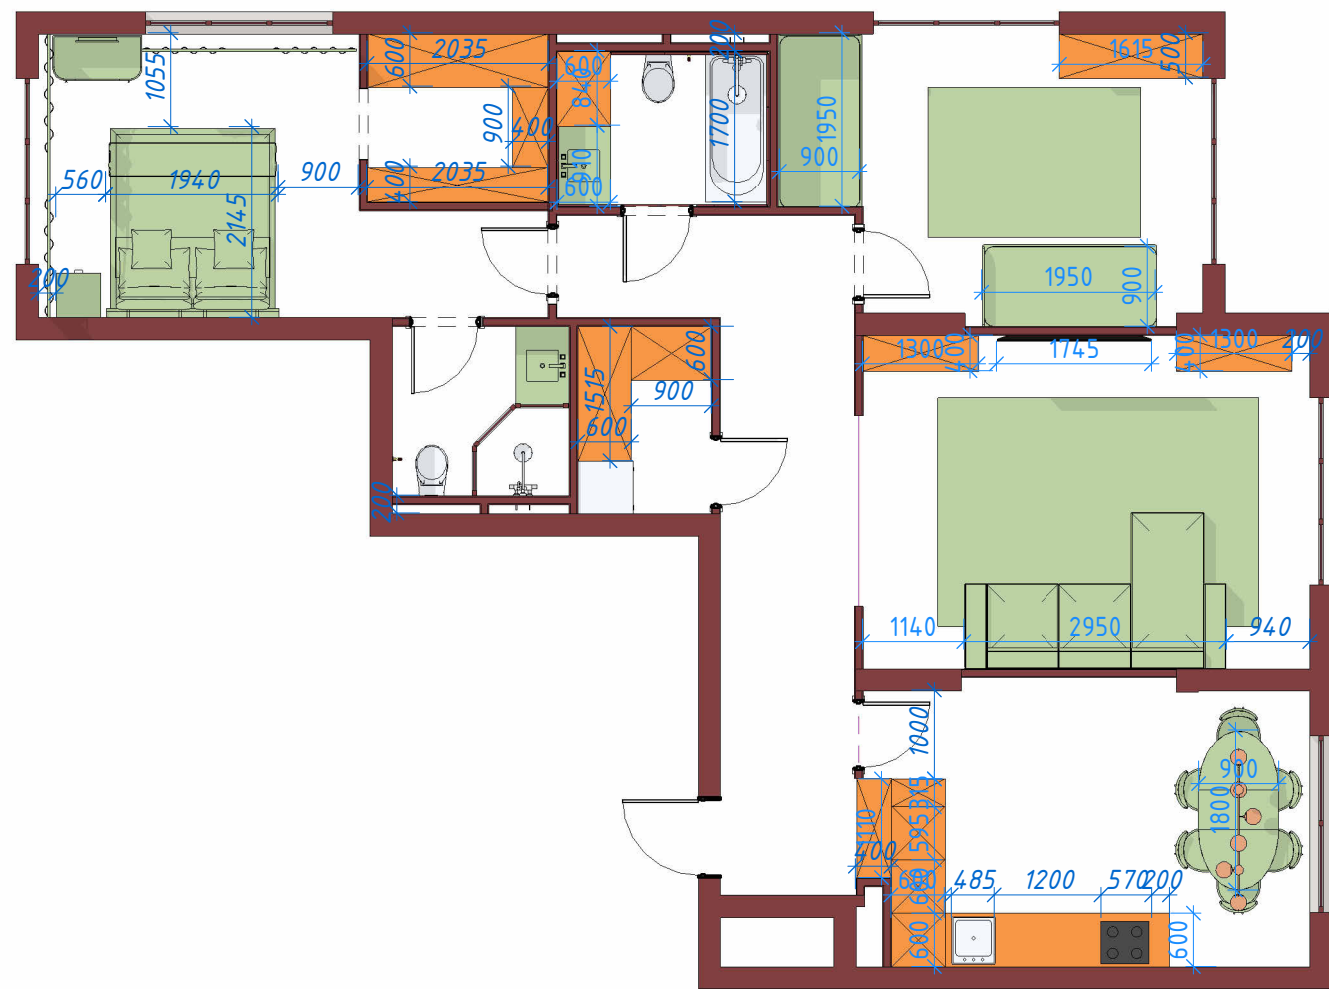


* Экспликация помещений...		
№ пом	Наименование	Площадь, м²
1	Прихожая	13,76 м²
3	Гостиная	18,92 м²
4	Детская	14,28 м²
5	Кладовка	3,15 м²
6	С/У 1	4,06 м²
7	Гардеробная	3,87 м²
8	Спальня	14,08 м²
9	С/У 2	2,83 м²
Общий итог: 8		74,94 м²

Дополнительные примечания:
1. Эскиз встроенной мебели, корпусной мебели и кухни производится после замера и проекта от производителя.
2. Согласовать наполнения гардеробных и шкафов при заказе с поставщиком/производителем.

Примечание:
1. Комплект рабочих чертежей разработан на основе обмеров.
2. Все размеры указаны в миллиметрах
3. Перед началом работ все размеры проверить по месту
4. Высота Потолка Н = 3000 мм.
5. Высота Проема двери Н = 2200 мм.

План полов

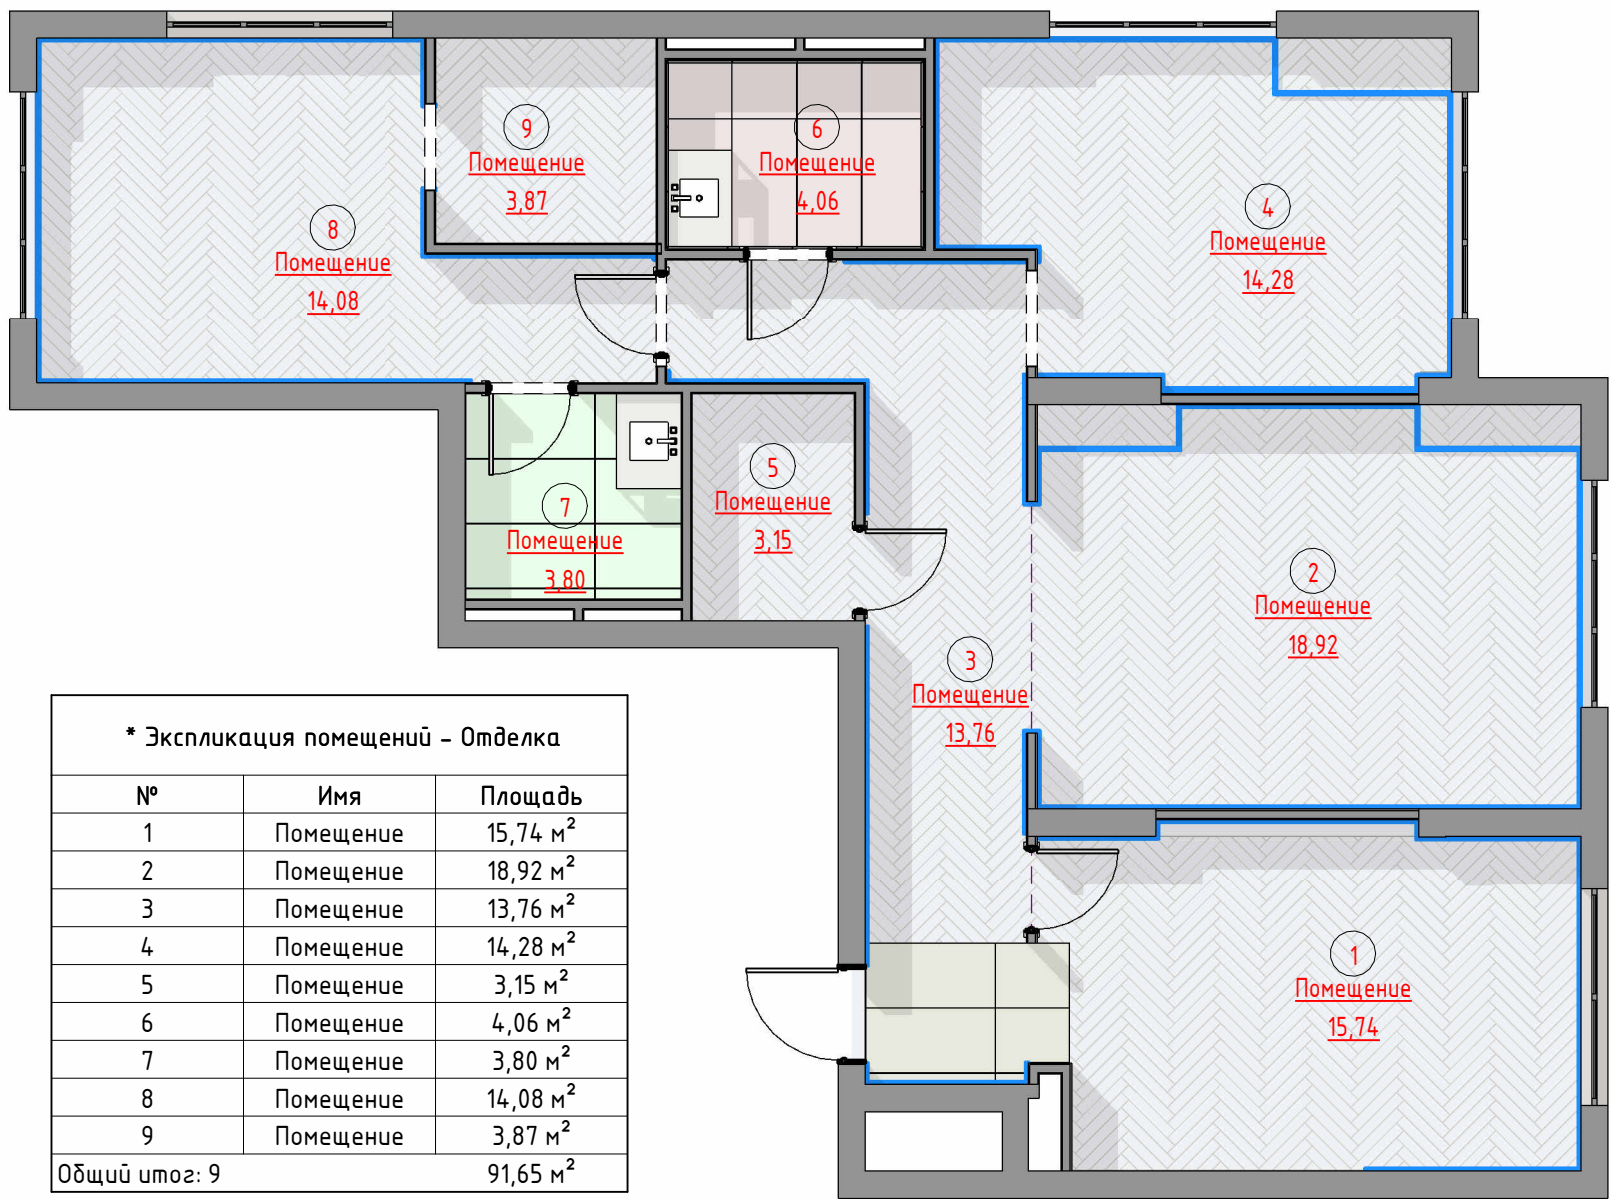

Условные обозначения

— - плинтус h =100 мм

Ведомость отделки пола				
Марка	Изо	Тип	Площадь	Описание
л-1		ламинат елка	84,72 м ²	доска елочка
Общий итог: 2			84,72 м ²	

Спецификация элементов пола				
Марка	Изо	Тип	Длина	Ком-ий
П		Плинтус	80,76 м	дюрполимерные 100мм
Общий итог: 14			80,76 м	


Ведомость отделки ПОЛА керамогранитной плиткой				
Изо	Тип	Число	Ком-ий	Площадь
	Керамогранит (тип 1)	6	ПРИХОЖАЯ	2 м ²
	Керамогранит (тип 2)	8	ВАННА	4 м ²
	Керамогранит (тип 3)	8	ДУШ	4 м ²
	Стеклопакет 20 мм	27		45 м ²
	Стеклопакет 25 мм	42		24 м ²

Дополнительные примечания:


- 1. В душевой кабине предусмотреть стяжку с уклоном 2%
- 2. Цвет затирки выбрать под цвет плитки
- 3. В качестве компенсатора использовать плоский Т-профиль
- 4. Плитку пересчитать при заказе с менеджером салона
- 5. Материалы посчитаны без запаса

Примечание:

- 1. Комплект рабочих чертежей разработан на основе обмеров.
- 2. Все размеры указаны в миллиметрах
- 3. Перед началом работ все размеры проверить по месту
- 4. Высота Потолка Н = 3000 мм.
- 5. Высота Проема двери Н = 2100 мм.

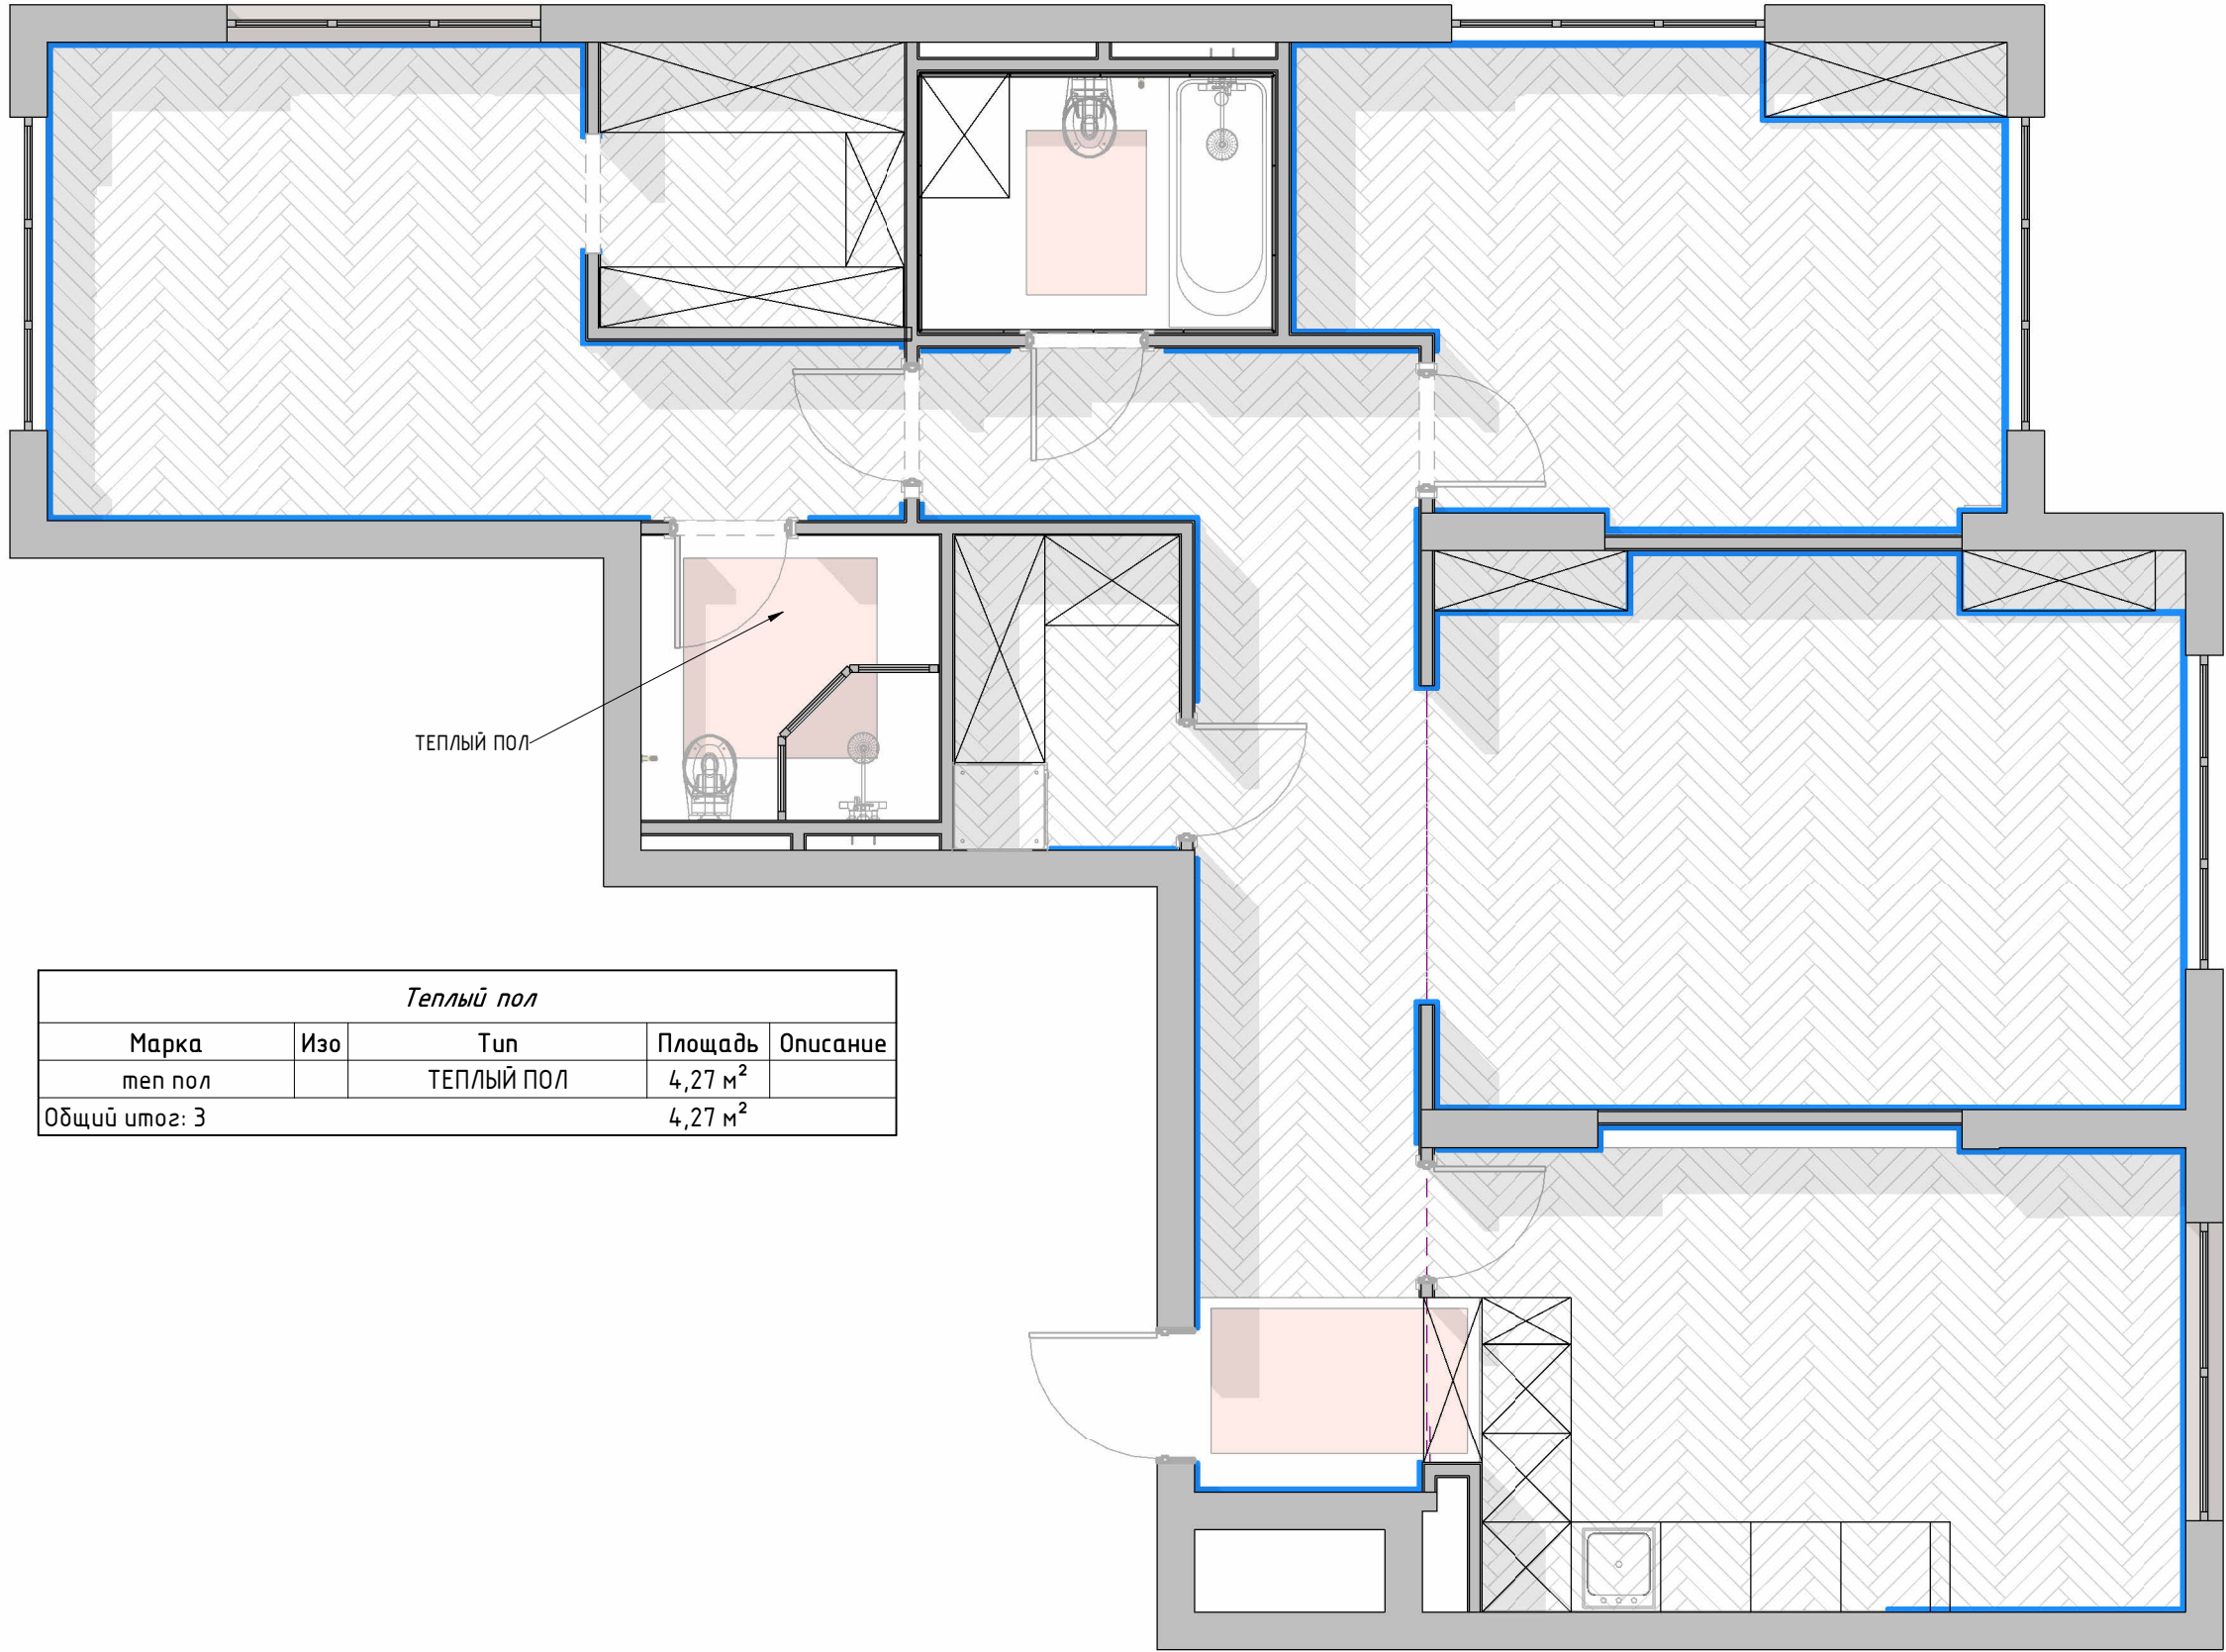

План открывания дверей

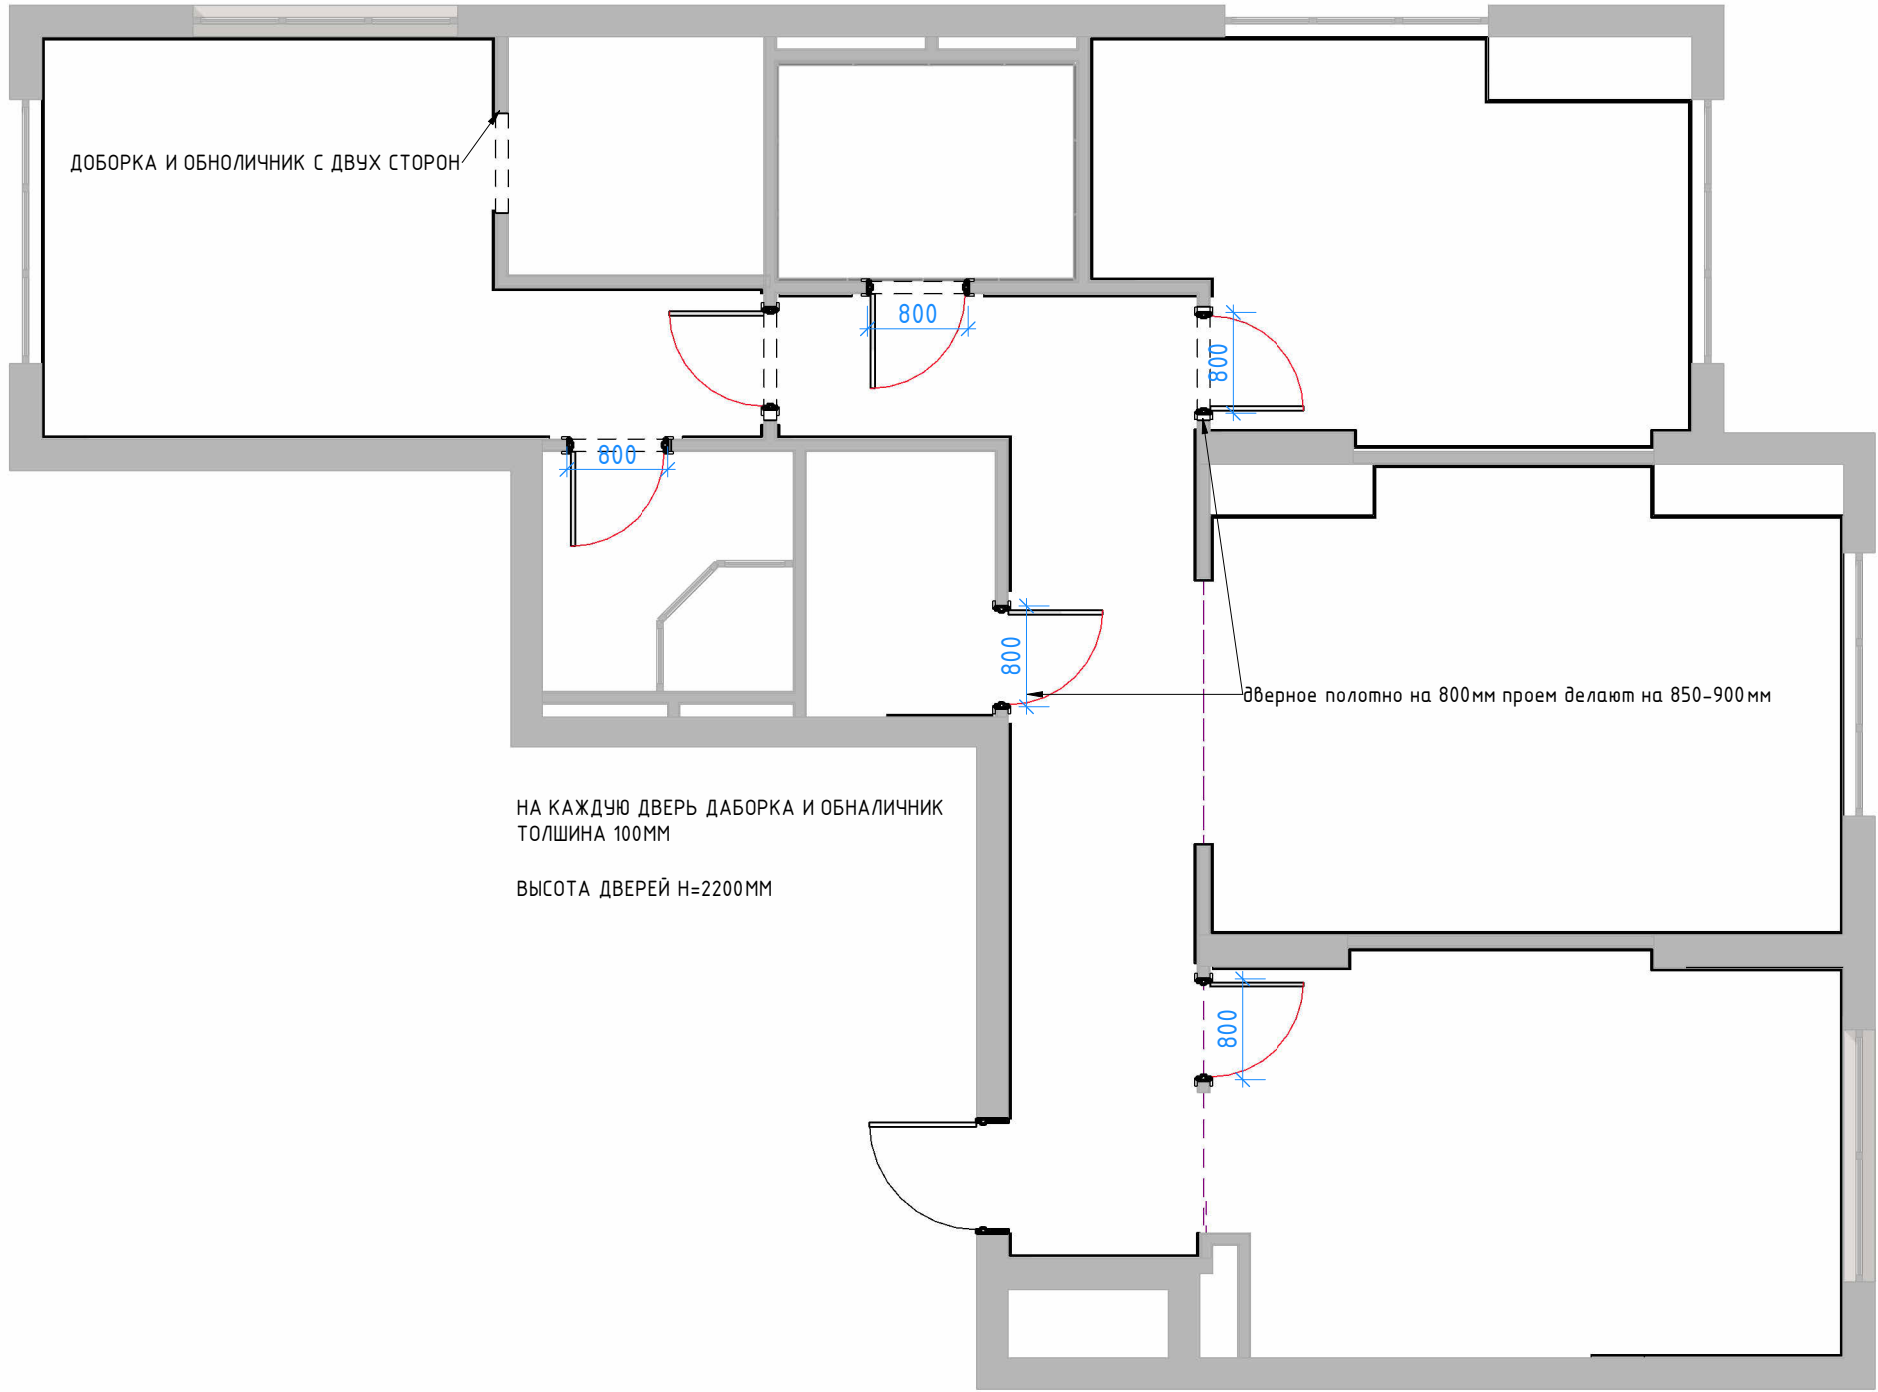

- Примечание:
- 1. Комплект рабочих чертежей разработан на основе обмеров.
 - 2. Все размеры указаны в миллиметрах
 - 3. Перед началом работ все размеры проверить по месту
 - 4. Высота Потолка Н = 3000 мм.
 - 5. Высота Проема двери Н = 2100 мм.

План осветительного оборудования


Схема управления освещением



Дополнительные примечания:
1. Разметить места расположения точечных светильников и согласовать с заказчиком.

Примечание:
1. Комплект рабочих чертежей разработан на основе обмеров.
2. Все размеры указаны в миллиметрах
3. Перед началом работ все размеры проверить по месту

План сводный электроприборов

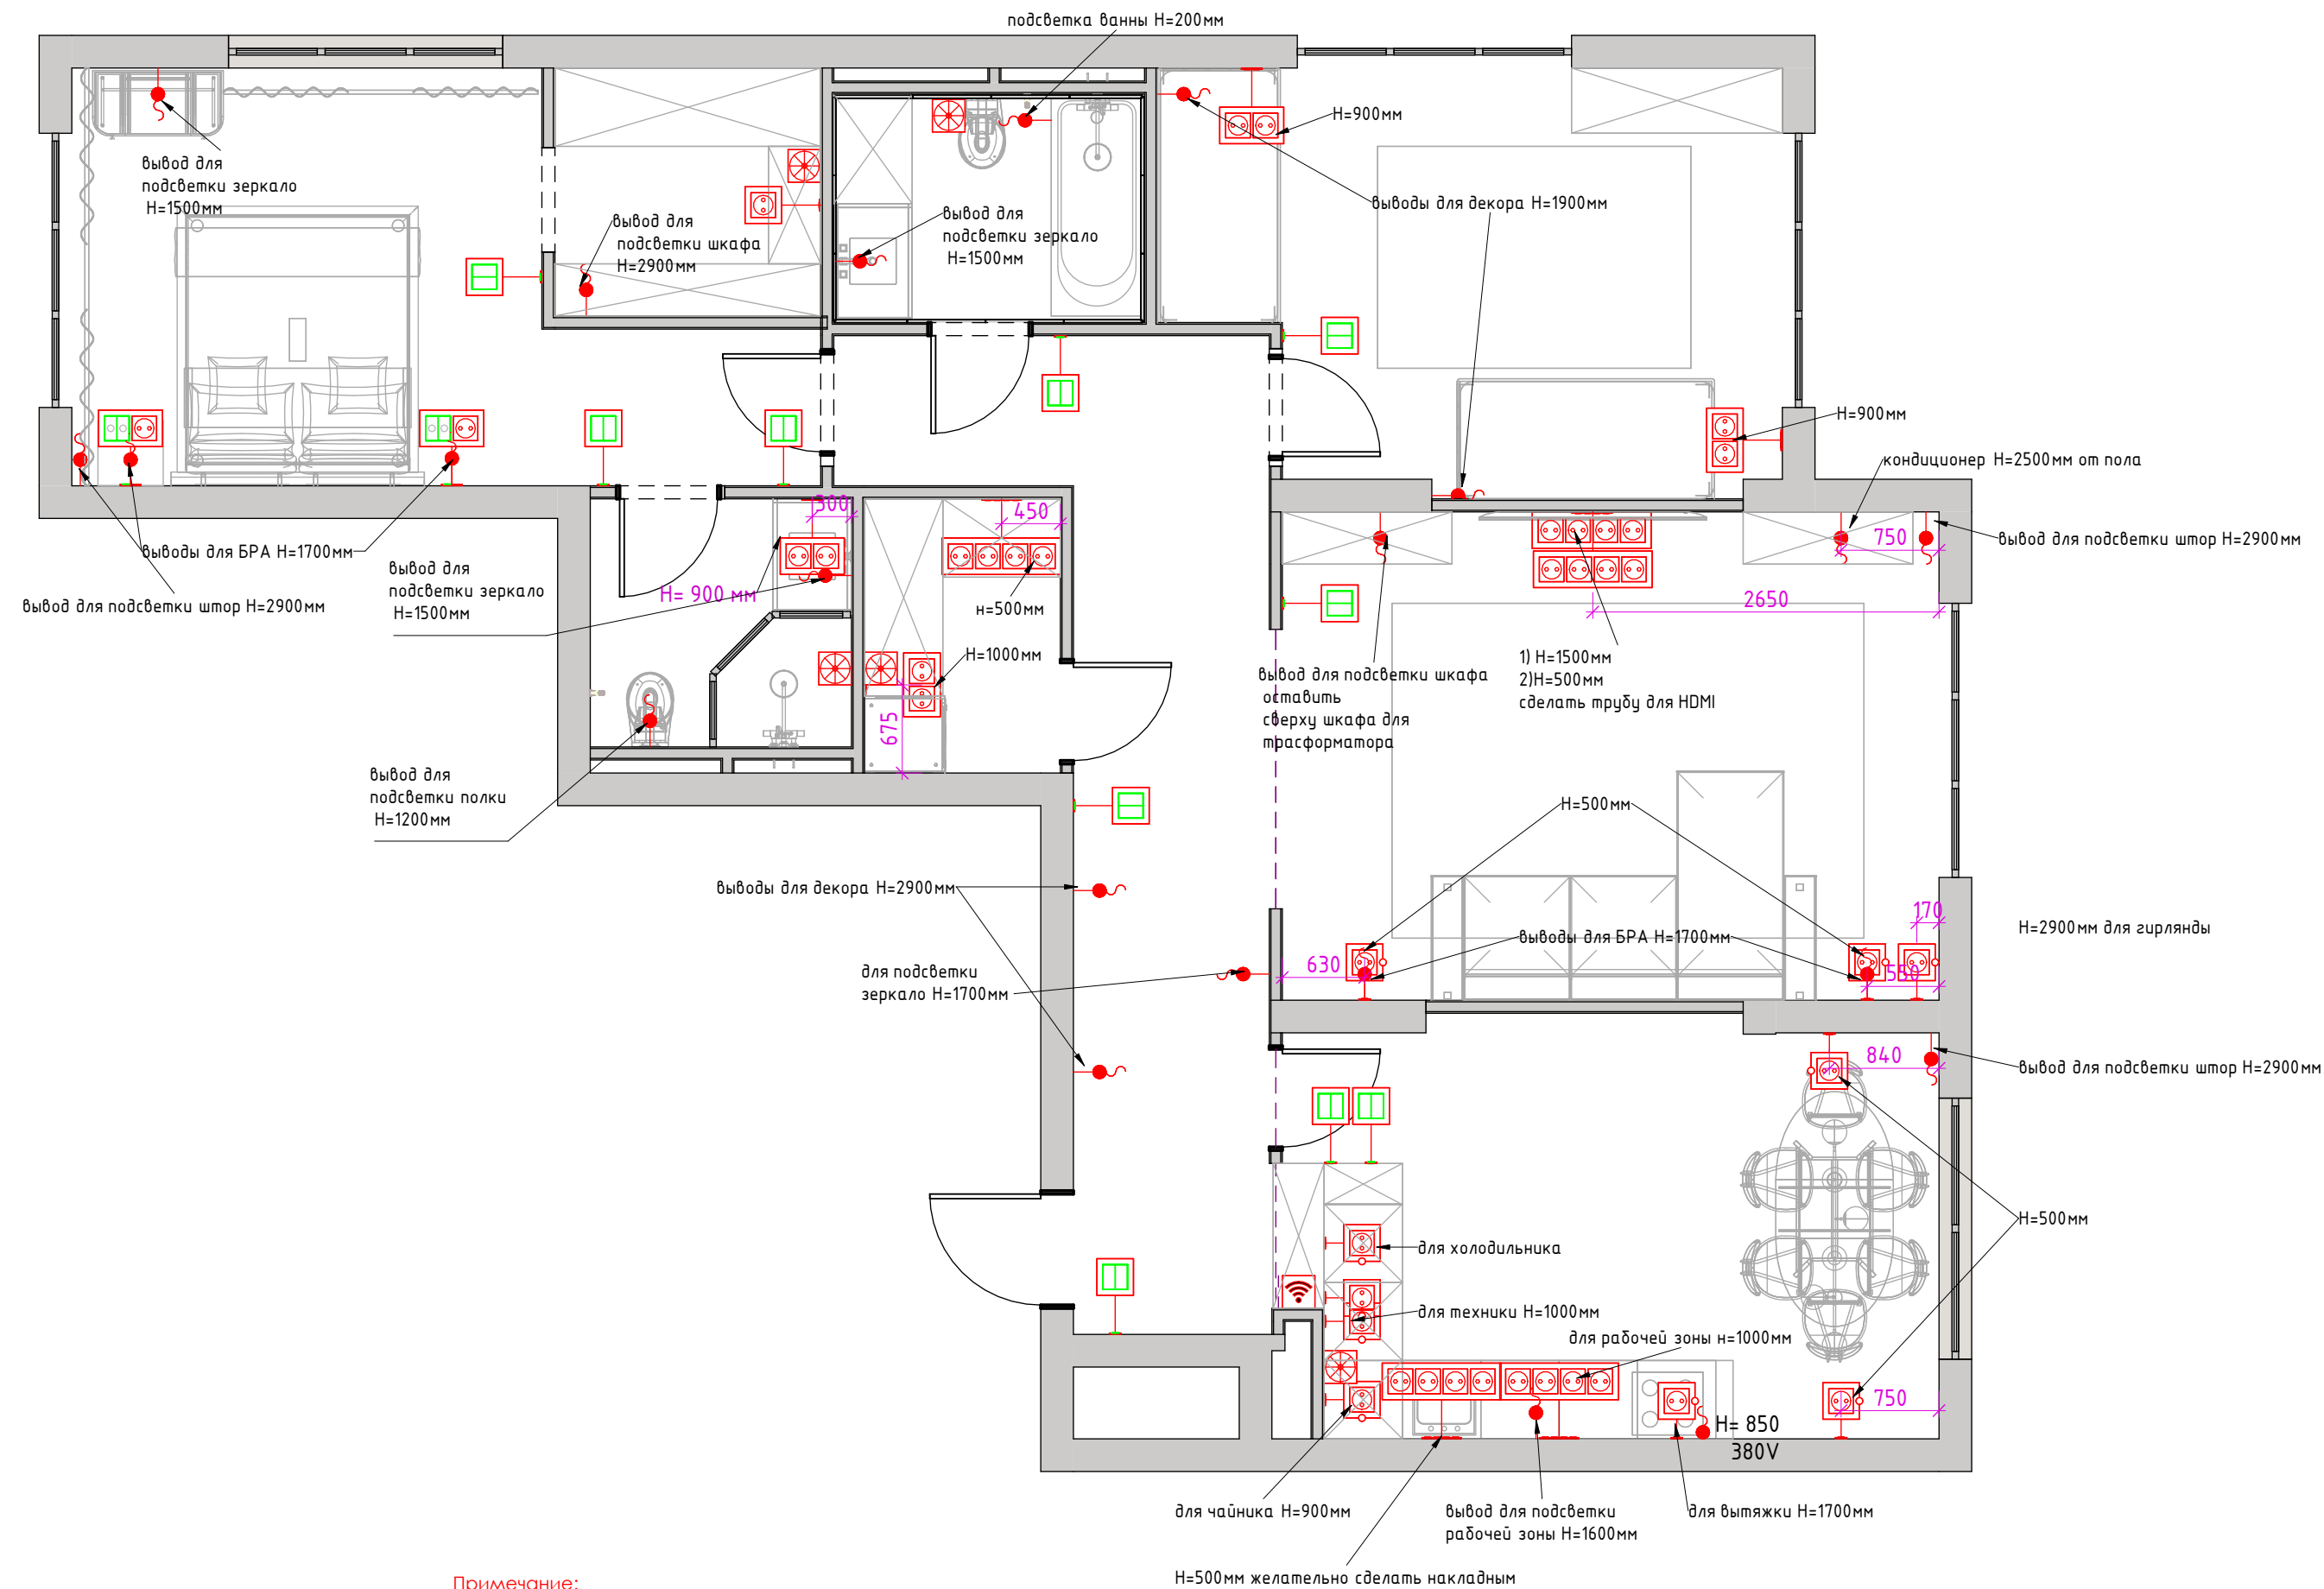

Примечание:
1. Комплект рабочих чертежей разработан на основе обмеров.
2. Все размеры указаны в миллиметрах
3. Перед началом работ все размеры проверить по месту
4. Высота Потолка H = 3000 мм.
5. Высота Проема двери H = 2200 мм.

YERMAGANBETOVA_ZH
РАБОЧИЙ ПРОЕКТ

План электрики

Лист
11