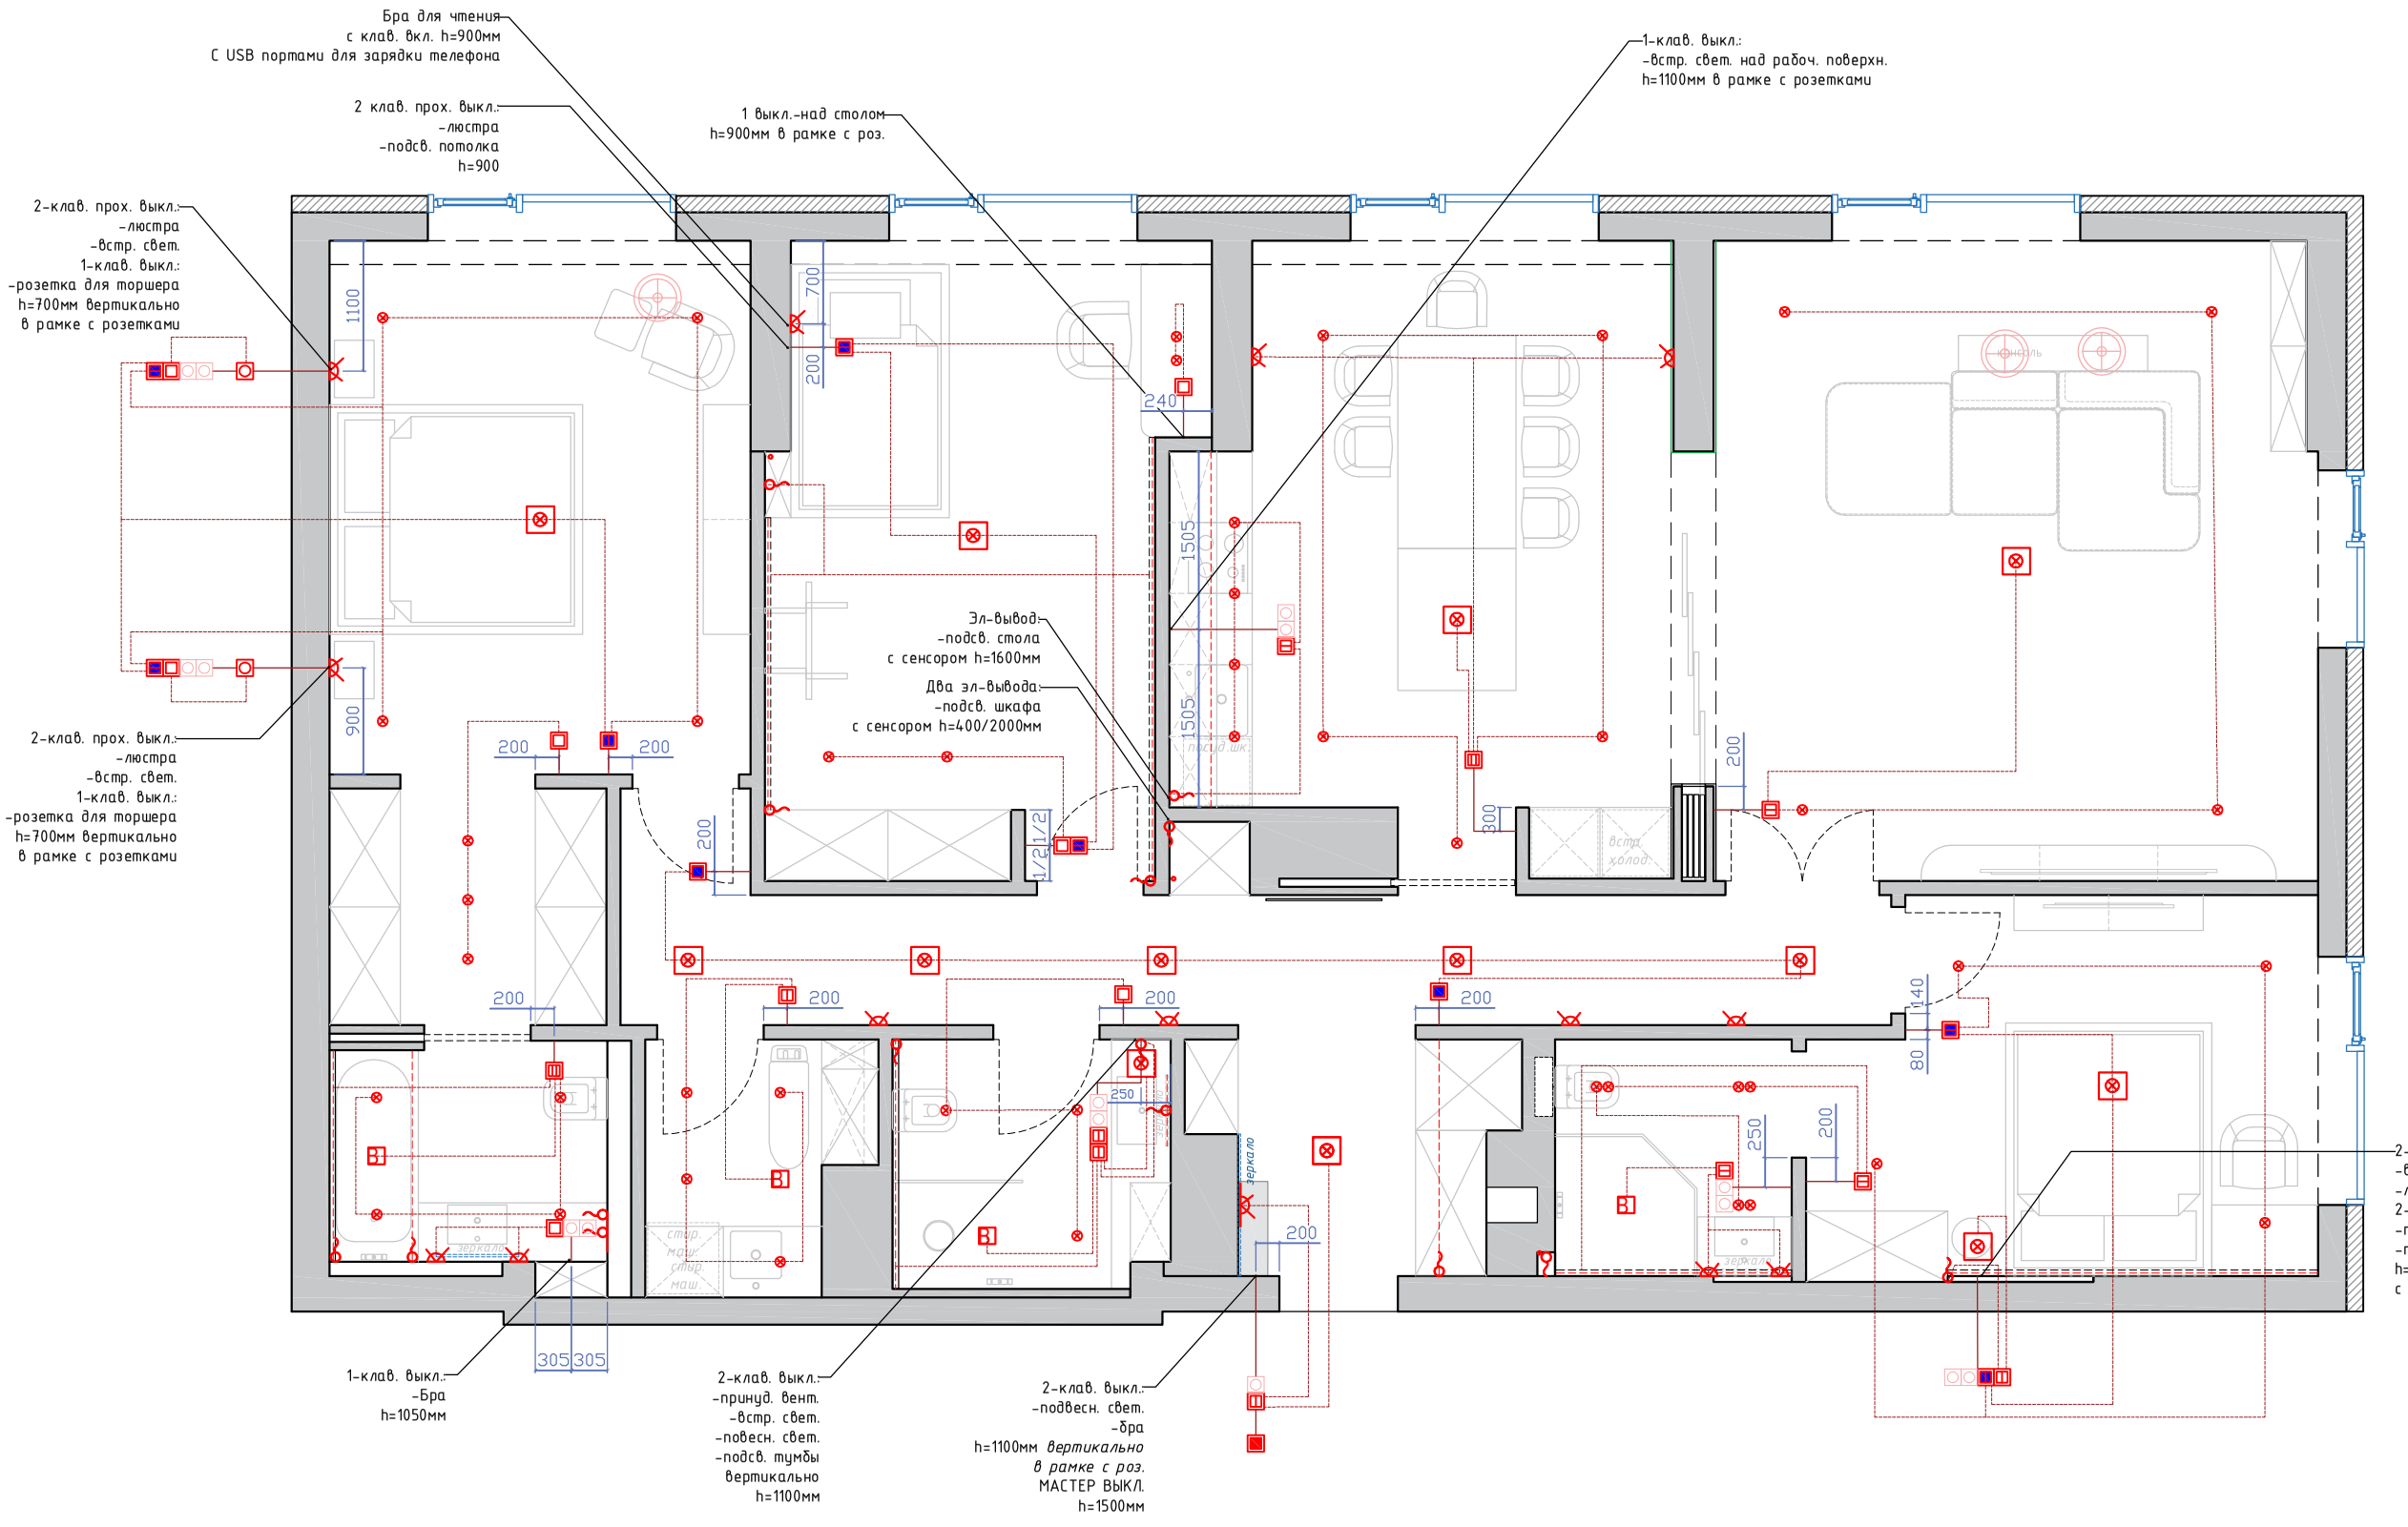


ПРИМЕЧАНИЯ:

1. *Дизайн проект разработан на базе проектных размеров. Связи с этим необходимо учитывать возможную не стыковку проектных и реальных размеров. Все возникающие в процессе работы вопросы решаются совместно с прорабом.*
2. *Единицы измерения указаны в миллиметрах.*
3. *Все высоты указаны от уровня чистого пола.*
4. *Высота выключателей - 900мм (если не указано иное)*
5. *Привязка от центра выключателя до угла/откоса 200мм (если не указано иное)*
6. *Привязки указаны по центру выключателя/общей рамки с розетками и выключателями.*
7. *Все электро-выводы выполнить с запасом, ввиду внесения возможных изменений в проект.*
8. *Предварительные разметки по электричеству согласовать с заказчиком.*

розетка, h=300 (где высоты не указаны)	Мастер-выкл., откл. групп. электроприбор.	светильник подвесной
выкл.,h=900(где высоты не указаны)	расст. от выкл/роз до откоса 200	бра на стене
выкл., двухклавишный	светильник накладной	А антена
выкл., проходной	светильник встроенный	И интернет
выкл., двухкл. проходн.	электрический вывод 220V	принудительная вентиляция

ИСПОЛНИТЕЛЬ	ИСАБЕКОВА Ж.К.
ЗАКАЗЧИК	
НАЗВАНИЕ ПРОЕКТА	Г.АСТАНА
НАИМЕНОВАНИЕ ПЛАНА	ОБМЕРНЫЙ ПЛАН
ДАТА	17.03.2026
ЛИСТ/ЛИСТОВ	3/21
СОГЛАСОВАНО	

(ЗАПОЛНЯЕТСЯ ЛИЧНО ЗАКАЗЧИКОМ)

КОНТАКТЫ ДЛЯ СВЯЗИ
С ИСПОЛНИТЕЛЕМ ТЕЛ.: 8 701 522 20 35 ПОЧТА: