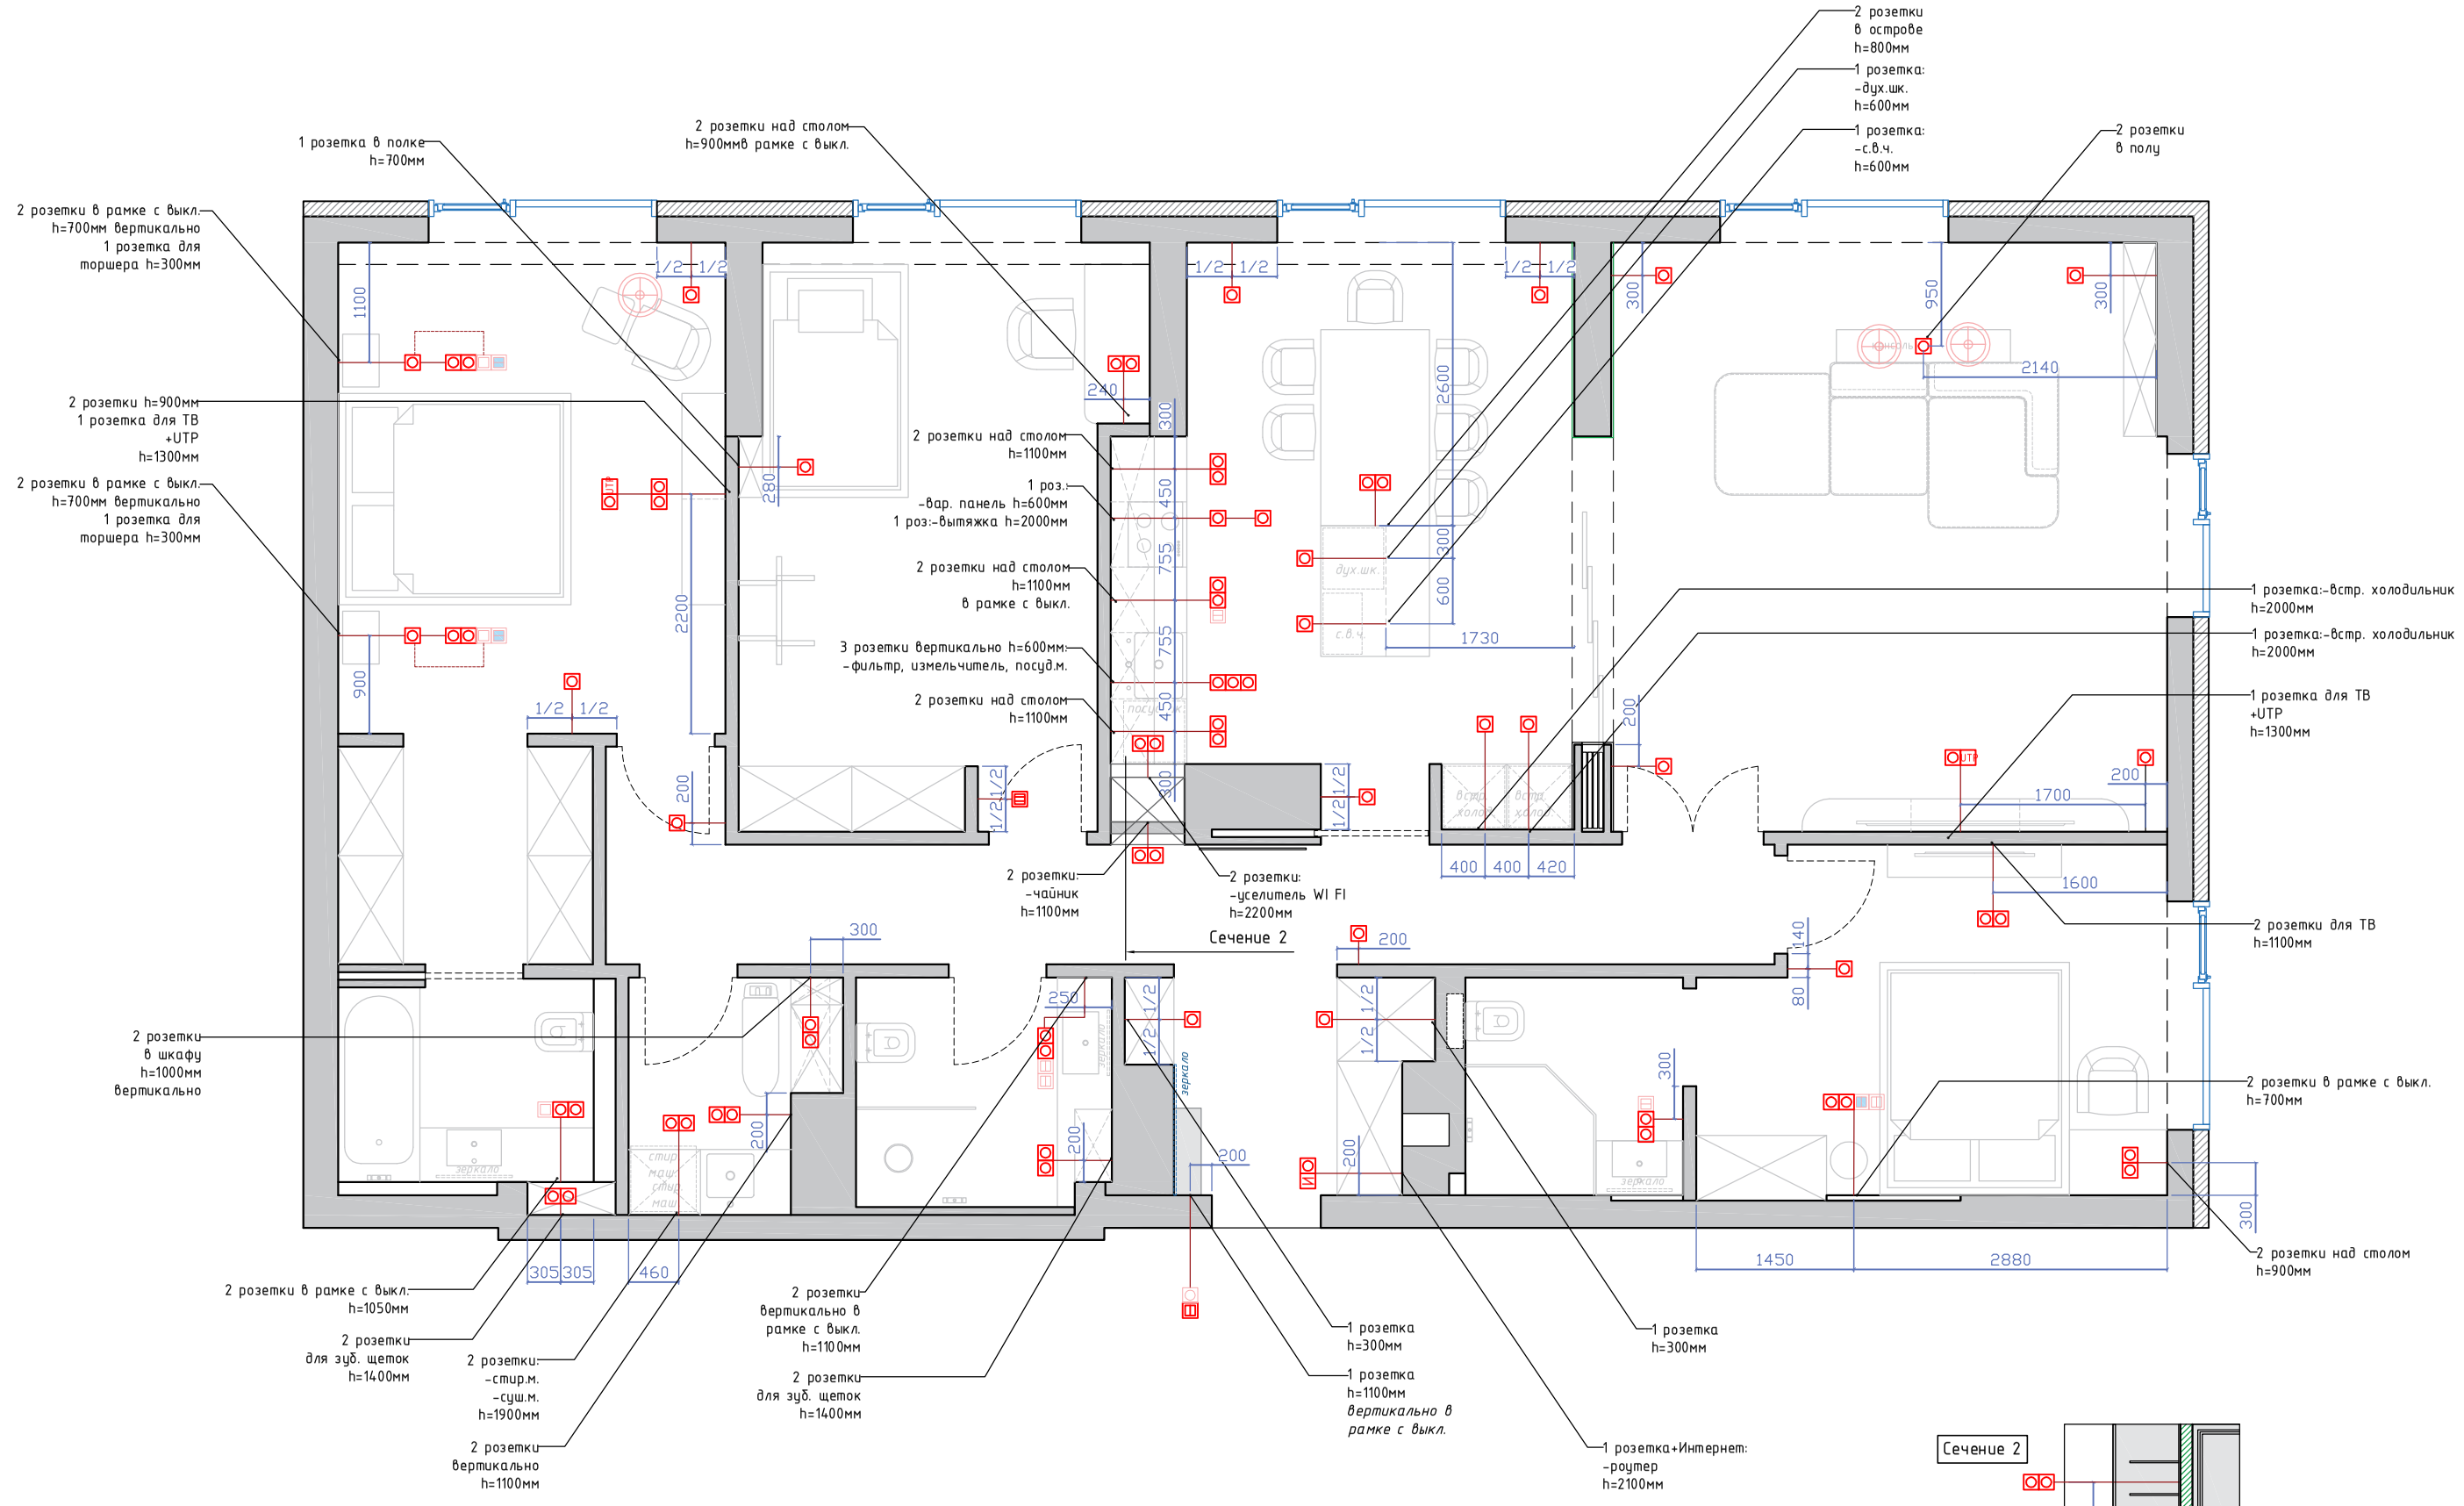


ПРИМЕЧАНИЯ:

1. *Дизайн проект разработан на базе проектных размеров. Связи с этим необходимо учитывать возможную не стыковку проектных и реальных размеров. Все возникающие в процессе работы вопросы решаются совместно с прорабом.*
2. *Единицы измерения указаны в миллиметрах.*
3. *Все высоты указаны от уровня чистого пола.*
4. *Высота розеток - 300мм (если не указано иное)*
5. *Привязка от центра розетки до угла/откоса 200мм (если не указано иное)*
6. *Привязки указаны по центру розетки/общей рамки с розетками и выключателями.*
7. *Все электро-выводы выполнить с запасом, ввиду внесения возможных изменений в проект.*

розетка, h=300 (где высоты не указаны)	Мастер-выкл., откл. групп. электроприбор.	светильник подвесной
выкл.,h=900(где высоты не указаны)	расст. от выкл/роз до откоса 200	бра на стене
выкл., двухклавишный	светильник накладной	антена
выкл., проходной	светильник встроенный	интернет
выкл., двухкл. проходн.	электрический вывод 220V	принудительная вентиляция

ИСПОЛНИТЕЛЬ	ИСАБЕКОВА Ж.К.
ЗАКАЗЧИК	
НАЗВАНИЕ ПРОЕКТА	Г.АСТАНА
ЛИСТ/ЛИСТОВ	3/21
НАИМЕНОВАНИЕ ПЛАНА	ОБМЕРНЫЙ ПЛАН
ДАТА	17.03.2026
СОГЛАСОВАНО	

(ЗАПОЛНЯЕТСЯ ЛИЧНО ЗАКАЗЧИКОМ)

КОНТАКТЫ ДЛЯ СВЯЗИ С ИСПОЛНИТЕЛЕМ ТЕЛ.: 8 701 522 20 35 ПОЧТА: