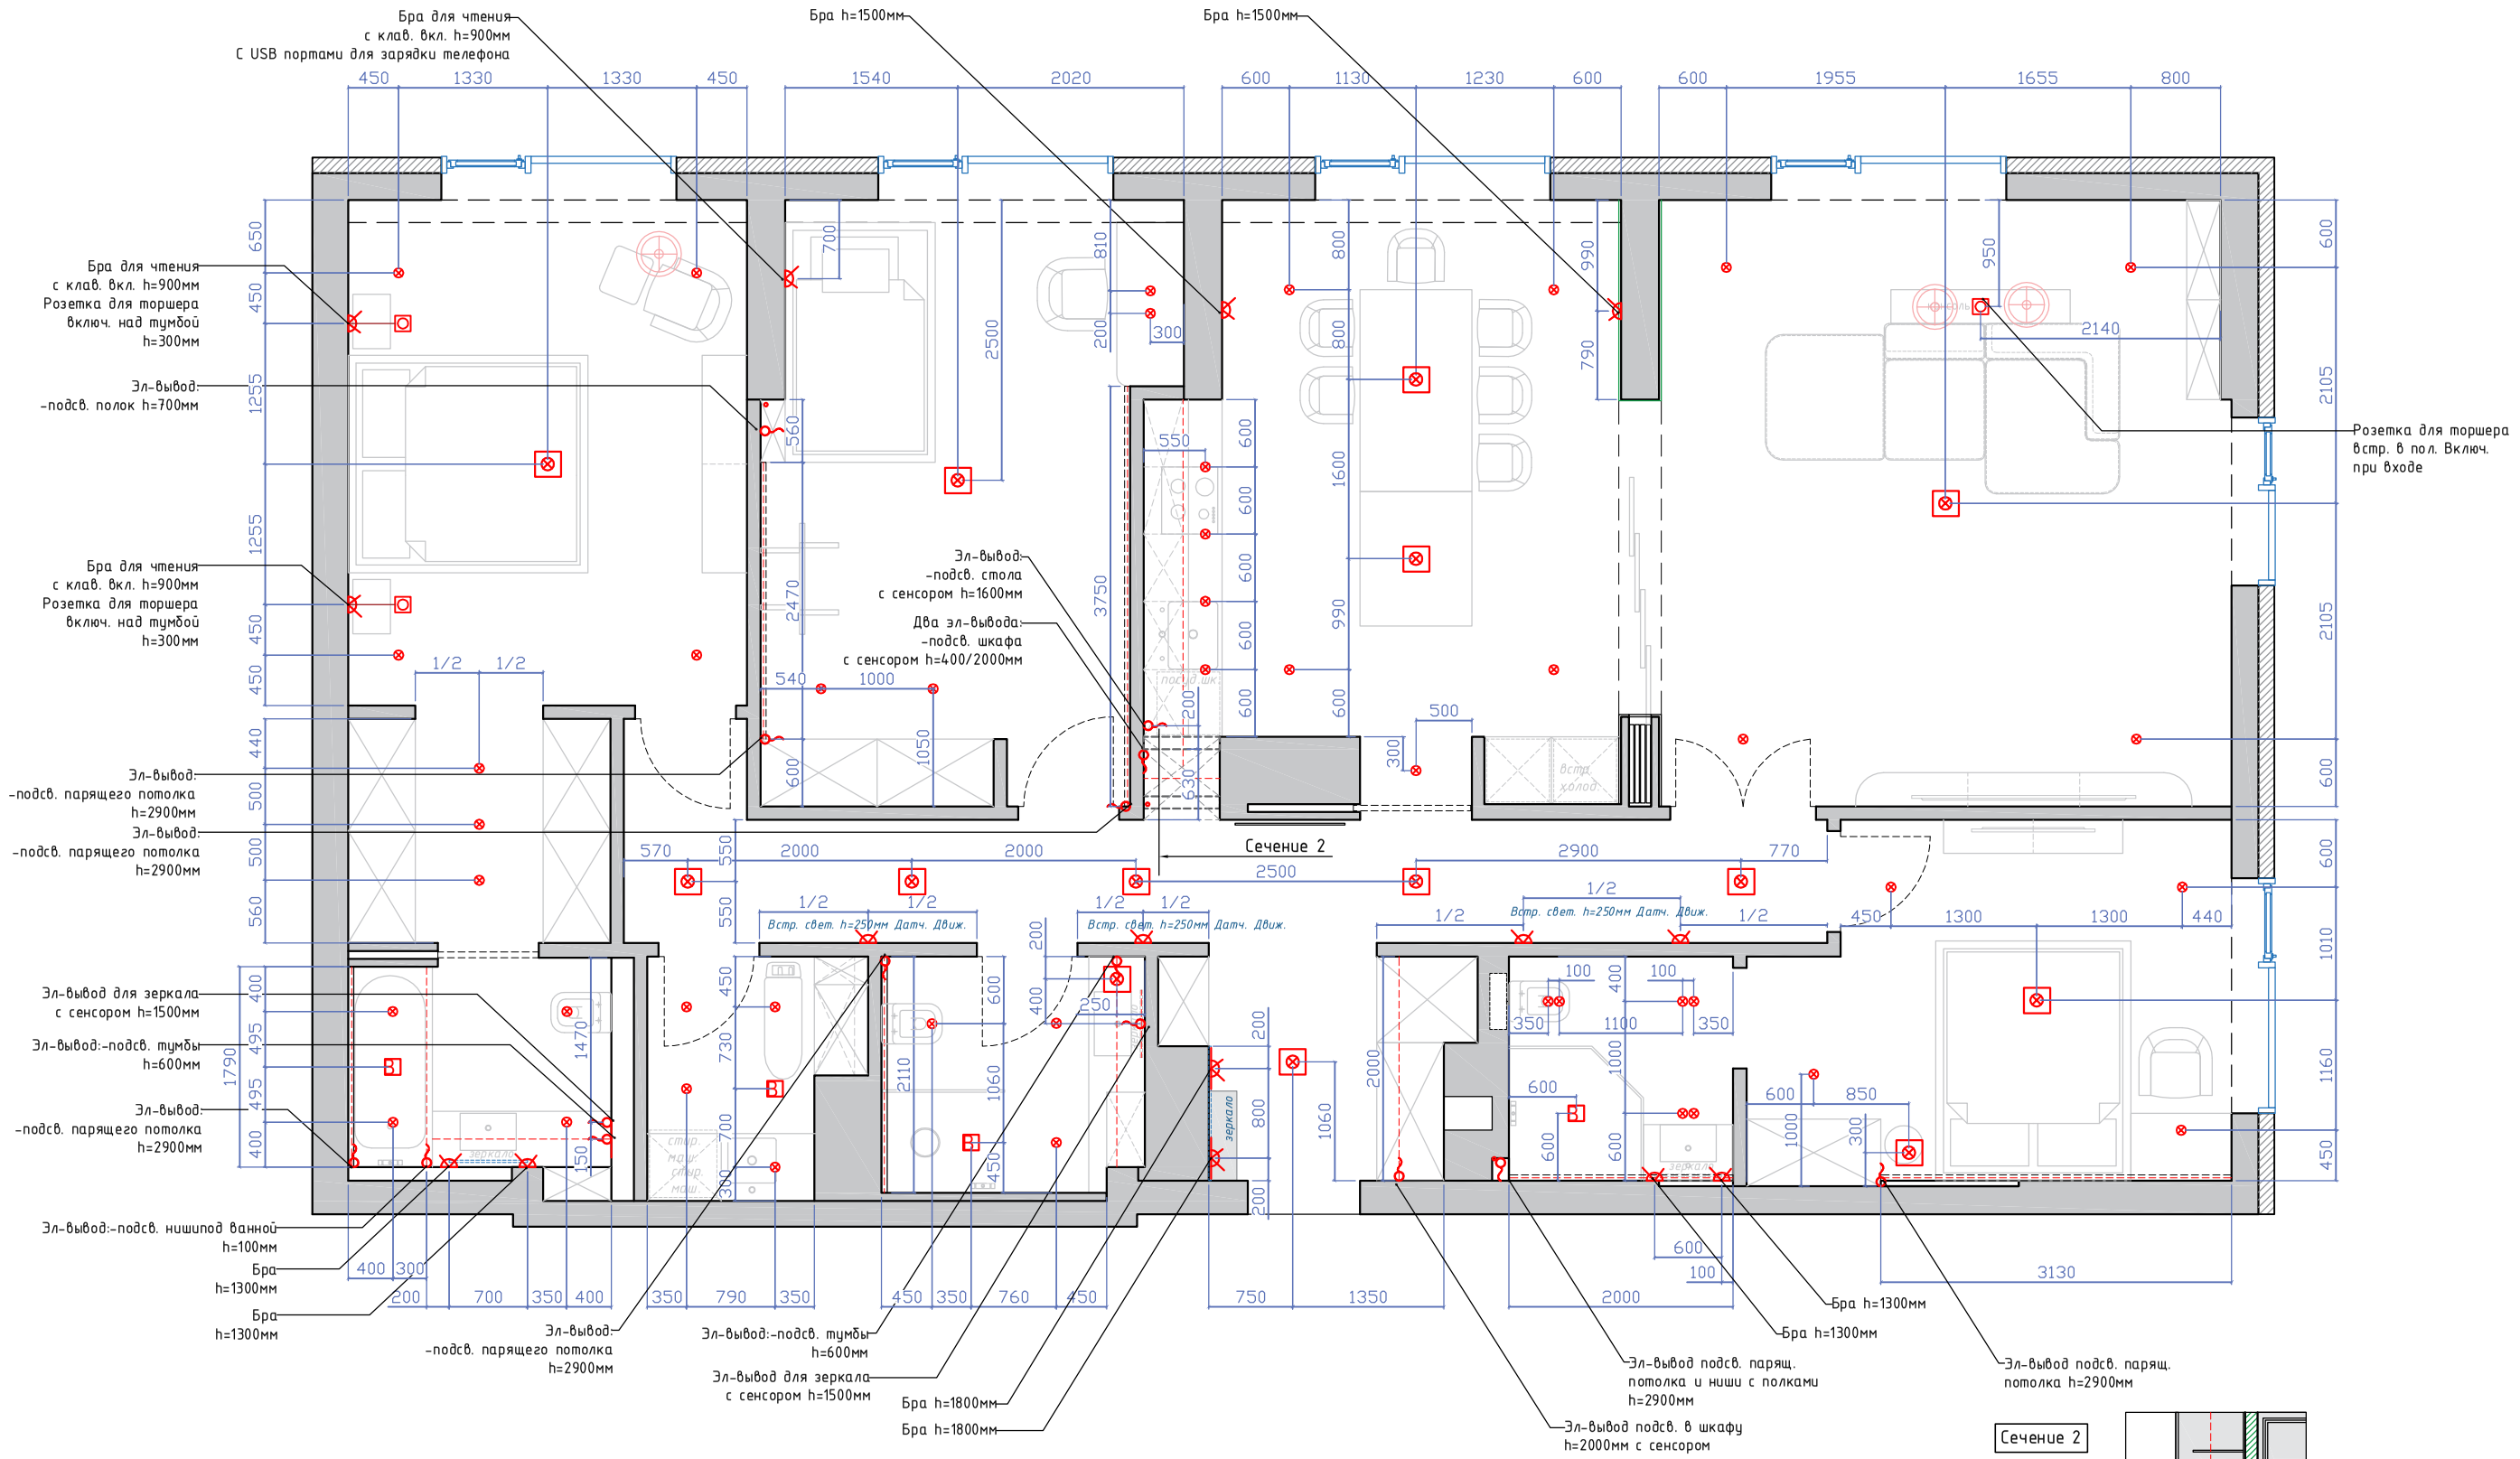


ПРИМЕЧАНИЯ:

1. *Дизайн проект разработан на базе проектных размеров. Связи с этим необходимо учитывать возможную не стыковку проектных и реальных размеров. Все возникающие в процессе работы вопросы решаются совместно с прорабом.*
2. *Единицы измерения указаны в миллиметрах.*
3. *Все привязки указаны от центра электровывода*
4. *Все высоты указаны от уровня чистого пола.*
5. *Все электровыводы выполнить с запасом, ввиду внесения возможных изменений в проект.*
6. *Предварительные разметки по электричеству согласовать с заказчиком.*
7. *Трансформаторы для встроенной подсветки мебели расположить в закрытых секциях шкафов.*
8. *Трансформаторы для стеновых и потолочных подсветок разместить в отдельной щитовой.*

розетка, h=300 (где высоты не указаны)	Мастер-выкл., откл. групп. электроприбор.	светильник подвесной
выкл.,h=900(где высоты не указаны)	расст. от выкл/роз до откоса 200	бра на стене
выкл., двухклавишный	светильник накладной	А антена
выкл., проходной	светильник встроенный	И интернет
выкл., двухкл. проходн.	электрический вывод 220V	принудительная вентиляция

ИСПОЛНИТЕЛЬ	ИСАБЕКОВА Ж.К.	КОНТАКТЫ ДЛЯ СВЯЗИ С ИСПОЛНИТЕЛЕМ ТЕЛ.: 8 701 522 20 35 ПОЧТА:	
ЗАКАЗЧИК		НАЗВАНИЕ ПРОЕКТА	Г.АСТАНА
НАИМЕНОВАНИЕ ПЛАНА	ОБМЕРНЫЙ ПЛАН	ЛИСТ/ЛИСТОВ	3/21
ДАТА	17.03.2026	СОГЛАСОВАНО	

(ЗАПОЛНЯЕТСЯ ЛИЧНО ЗАКАЗЧИКОМ)